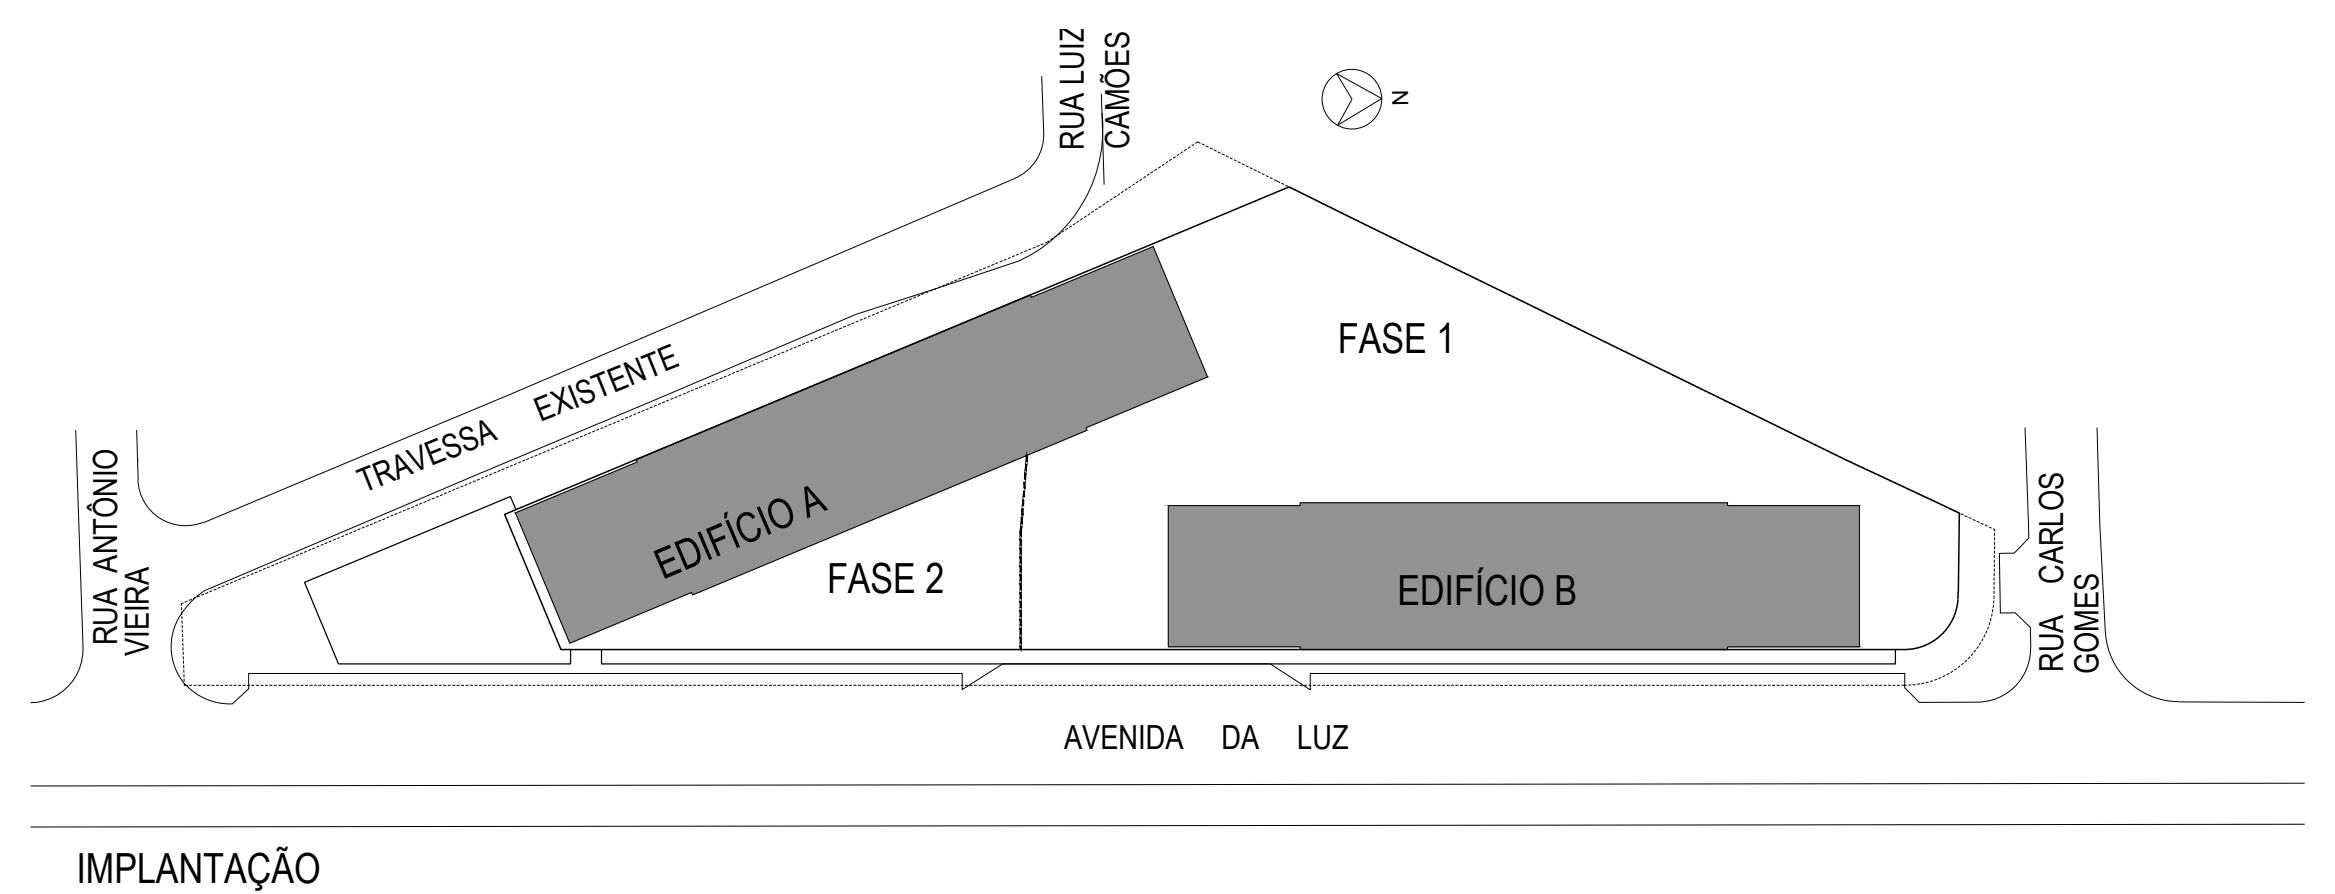

IMPLANTAÇÃO
esc.: 1:500

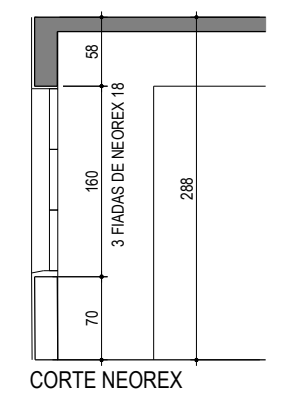

CORTE NEOREX
esc. 1:50

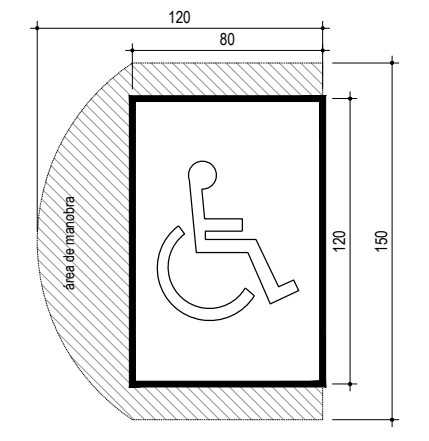

SINALIZAÇÃO
ÁREA DE RESGATE NAS ESCADAS

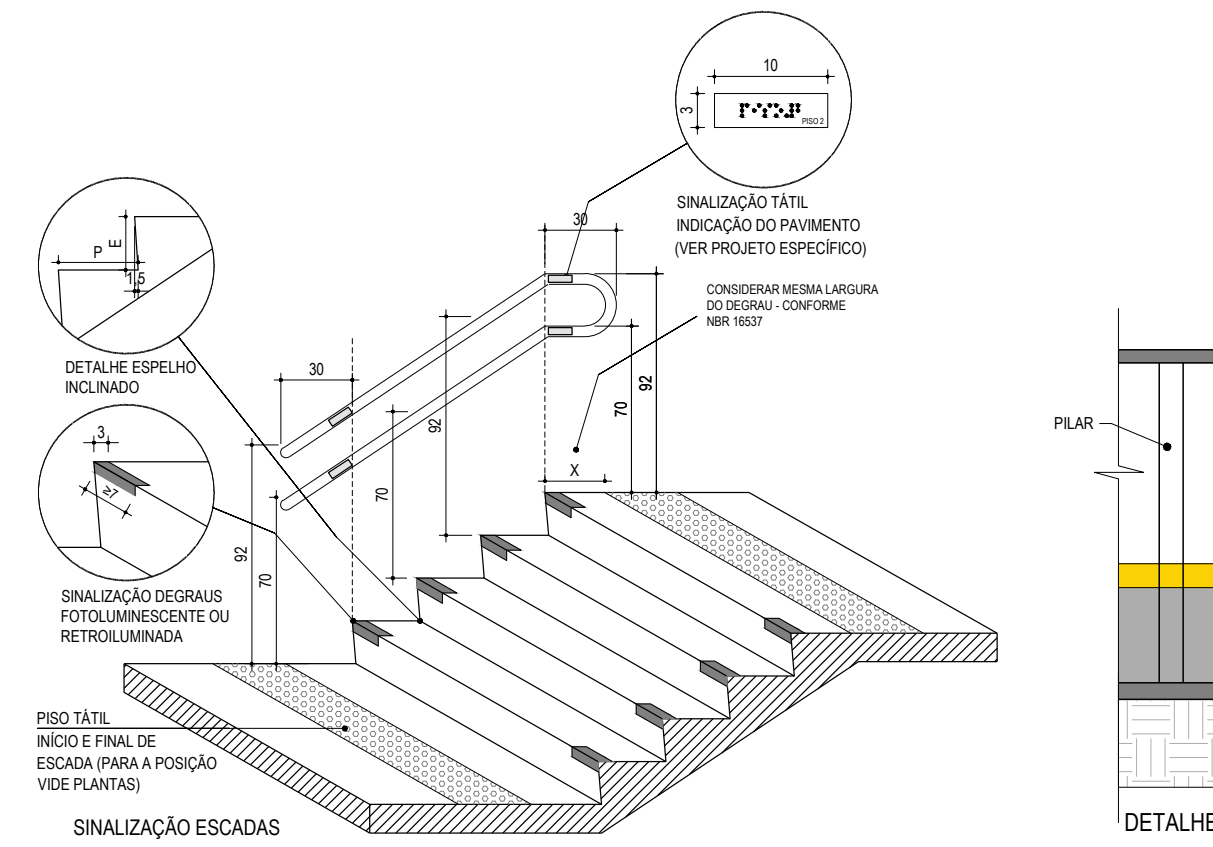
10
3
SINALIZAÇÃO TÁTIL INDICAÇÃO DO PAVIMENTO (VER PROJETO ESPECÍFICO)
CONSIDERAR MESMA LARGURA DO DEGRAU - CONFORME NBR 16537
DETALHE ESPELHO INCLINADO
SINALIZAÇÃO DEGRAUS FOTOLUMINESCENTE OU RETROILUMINADA
PISO TÁTIL INÍCIO E FINAL DE ESCADA (PARA A POSIÇÃO VIDE PLANTAS)
30
92
70
X

SINALIZAÇÃO ESCADAS
SEM ESCALA

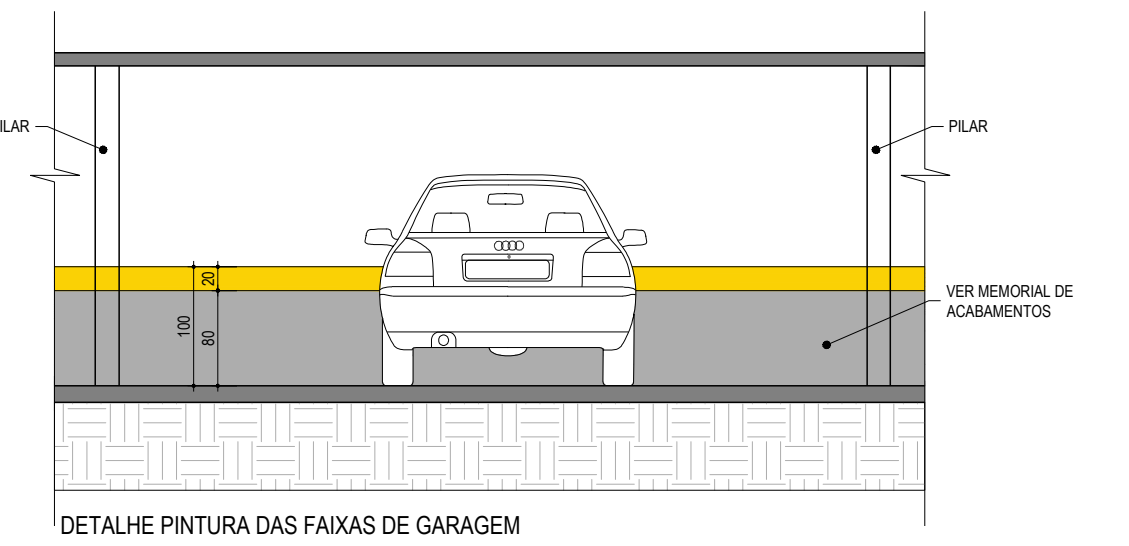

DETALHE PINTURA DAS FAIXAS DE GARAGEM
ESC. 1:50

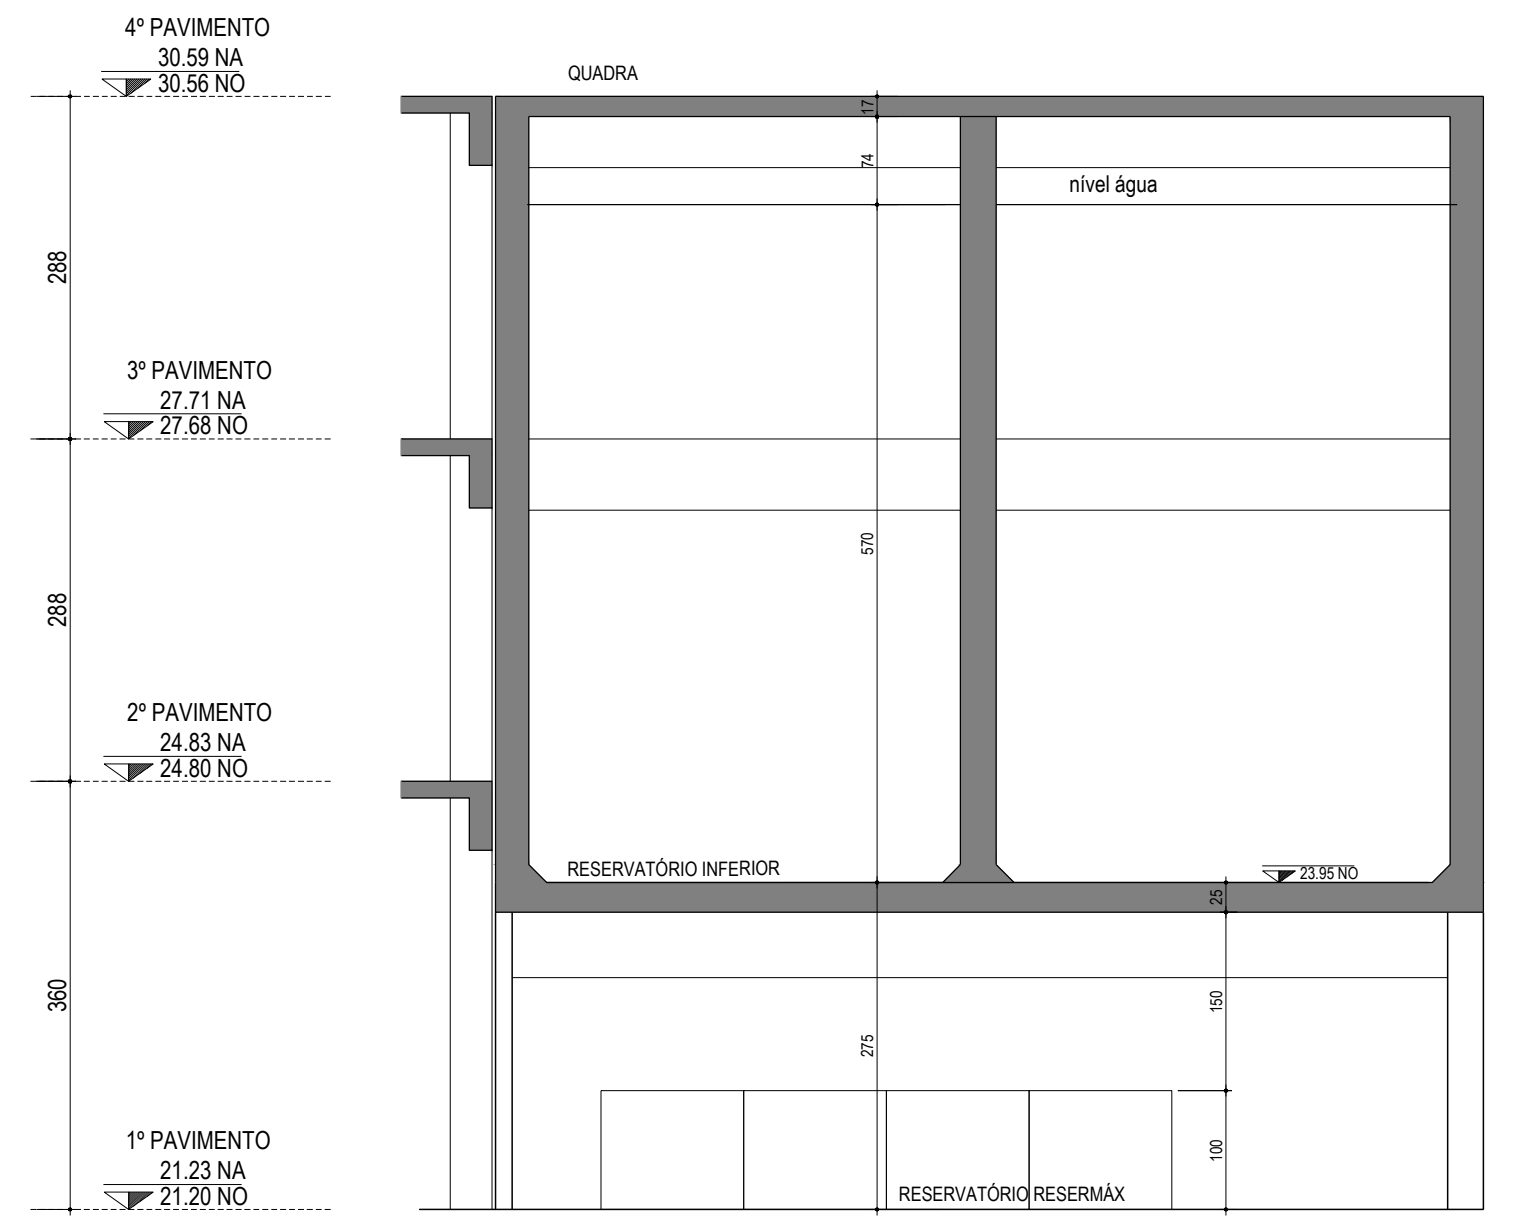

CORTE 1-1 RESERVATÓRIO
esc. 1:50

OBRA: ATENTAR COM AS DIMENSÕES DOS ENCHIMENTOS PARA NÃO INTERFERIREM NAS MEDIDAS DAS VAGAS E MANOBRAS

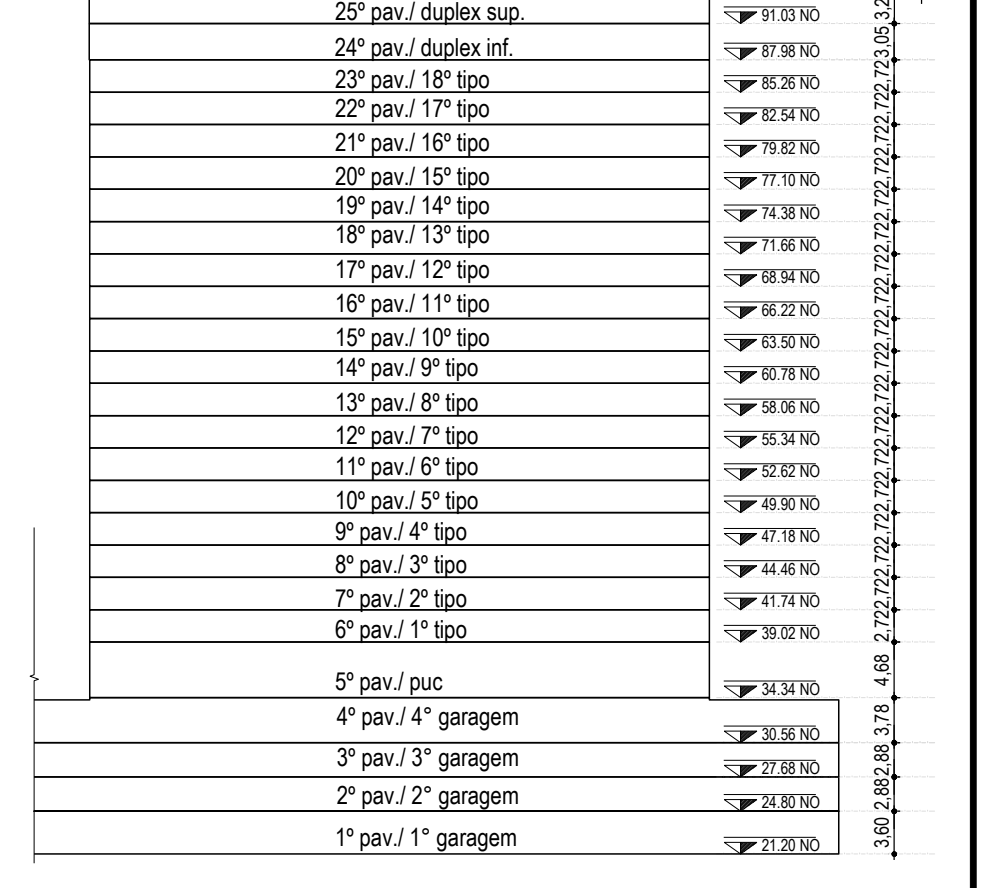

CORTE ESQUEMÁTICO
esc.: 1:500

LEIS

NBR 15575:2013 - DESEMPENHO DE EDIFICAÇÕES HABITACIONAIS;
NBR 9050:2020 - ACESSIBILIDADE A EDIFICAÇÕES, MOBILIÁRIO, ESPAÇO E EQUIPAMENTOS URBANOS;
NBR 14718:2019 - GUARDA-CORPOS PARA EDIFICAÇÕES;
NBR 13103:2020 - INSTALAÇÃO DE APARELHOS A GÁS PARA USO RESIDENCIAL - REQUISITOS DOS AMBIENTES;
NBR 9077:2001 - SAÍDAS DE EMERGÊNCIA EM EDIFÍCIOS;
NBR NM 313 - ELEVADORES DE PASSAGEIROS;

VIDA ÚTIL DO PROJETO (VUP)

Conforme mínimo especificado na NBR 15575:2013- Desempenho de edificações habitacionais

- ESTRUTURA: >/ 50 anos;
- PISOS INTERNOS: >/ 13 anos;
- VEDAÇÃO VERTICAL EXTERNA: >/ 40 anos;
- VEDAÇÃO VERTICAL INTERNA: >/ 20 anos;
- COBERTURA: >/ 20 anos;
- HIDROSSANITÁRIO: >/ 20 anos;

TRRF DAS PAREDES

a. ESCADA DE EMERGÊNCIA, SALA DE PRESSURIZAÇÃO E CASA DE BOMBAS DE INCÊNDIO DEVEM TER TRRF DE 120 min;
b. ESTRUTURAS DA EDIFICAÇÃO DEVEM TER TRRF DE 120min;
c. ABERTURAS ENTRE LAJES (SHAFTS) DEVEM TER VEDAÇÃO COM MATERIAIS DE TRRF DE 120min;
d. AS PAREDES ENTRE AS UNIDADES E ENTRE AS UNIDADES E A ÁREA DE CIRCULAÇÃO DEVEM TER TRRF DE 60min;
e. COMPARTIMENTAÇÃO VERTICAL EXTERNA DE FACHADA COM VERGA-PEITORIL DE 1,20m COM TRRF DE 120 min;

LEGENDA DETALHE DE MADEIRA

PEM - PORTA ENTRADA DE MADEIRA
PIM - PORTA INTERNA DE MADEIRA
RU - RESISTENTE À UMIDADE
PIA - PORTA INSOLANTE ACÚSTICA

NOTAS

1 - TODAS AS MEDIDAS ESTÃO EM CENTÍMETROS.
2 - VER MEMORIAL DESCRITIVO DE ACABAMENTOS.
3 - VER CADERNOS DE DETALHES.
4 - ÁREAS EXTERNAS - VER PROJETO DE PAISAGISMO.
5 - ÁREAS SOCIAIS INTERNAS - VER PROJETO DE INTERIORES.
6 - CONSIDERAR AS MEDIDAS PARA AS VAGAS:
. VAGA = 250 x 500 cm
. VAGA P.C.D. = 370 x 500 cm

TABELA DE ACABAMENTOS

VER ESPECIFICAÇÃO COMPLETA DE MATERIAIS NOS CADERNOS DE DETALHES E NO MEMORIAL DE ACABAMENTOS DO CLIENTE. PARA O USO DE MATERIAIS SIMILARES CONSULTAR O COORDENADOR DE PROJETOS.

INDICAÇÃO DE NÍVEIS

00.00(NA) → NÍVEL ACABADO
00.00(NO) → NÍVEL OSSO

▨ - SINALIZAÇÃO TÁTIL

LEGENDA:

REPRESENTAÇÃO GRÁFICA

▭	ALVENARIA
▨	ENCHIMENTO
▒	FORRO / SANCA
🟦	AR CONDICIONADO PREVISÃO

PLANTAS DE REFERÊNCIA PARA BASE DE PROJETO

REVISÃO	DATA	DESCRIÇÃO	RESP.
00	15/02/2023	EMISSÃO INICIAL	

INCORPORAÇÃO
JERONIMO DA VEIGA
Empreendimentos e Participações Ltda.

CONSTRUÇÃO

PROJETISTA
ADESA ARQUITETURA
RUA PADRE GARCIA VELHO, 73 - CJ. 41
CEP: 05421- 030
FONE: 3032 4355 / 3032 4362

DISCIPLINA
ARQUITETURA

CÓDIGO/OBRA
DUO

FASE
LIBERADO OBRA

EMPREENDIMENTO
DUO
AV_LUZ

ASSUNTO
PLANTA
2º_PAVIMENTO

FOLHA N.º
ARQ
102

RESPONSÁVEL
ADELINO SANTOS

SUPERVISOR
ADELINO SANTOS

COORDENADOR
ALISSA LOPES

REVISÃO
R00

PROJETISTA

ARQUIVO
DUO-ARQ-LO-102-PLA-2PV-R00.dwg

ESCALA
1:75

DATA
15/02/2023

DIREITOS AUTORAIS RESERVADO A REPRODUÇÃO TOTAL OU PARCIAL SEM PRÉVIA AUTORIZAÇÃO, CONFORME RESOLUÇÃO N° 67, DE 5 DE DEZEMBRO DE 2013