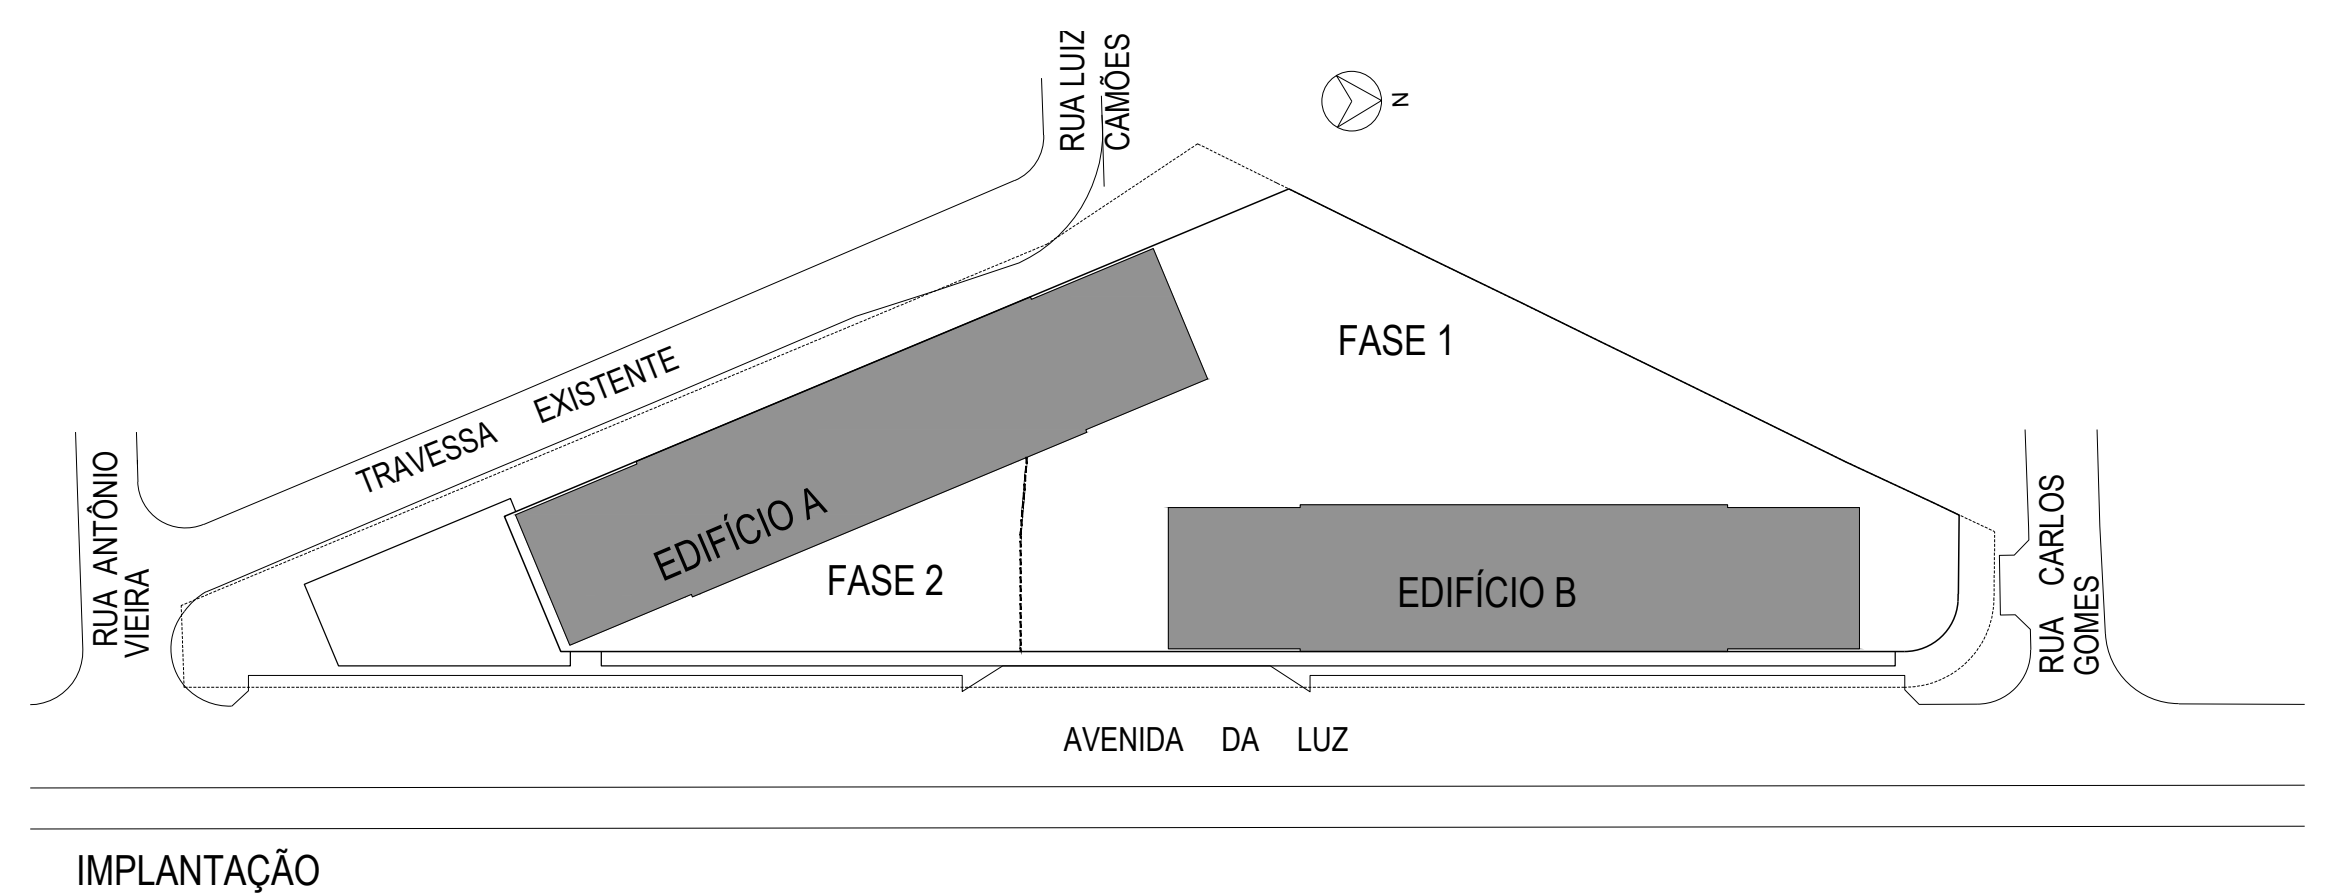
RUA LUIZ CAMÕES
TRAVESSA EXISTENTE
RUA ANTÔNIO VIEIRA
FASE 1
EDIFÍCIO A
FASE 2
EDIFÍCIO B
RUA CARLOS GOMES
AVENIDA DA LUZ
N

IMPLANTAÇÃO
esc.: 1:500

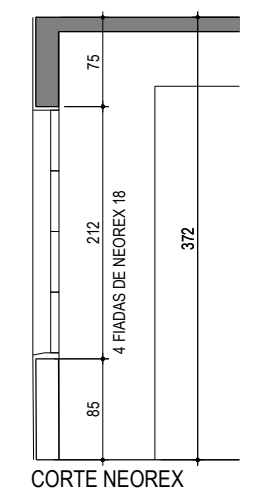
75
212
4 FIADAS DE NEOREX 18
372
85

CORTE NEOREX
esc. 1:50

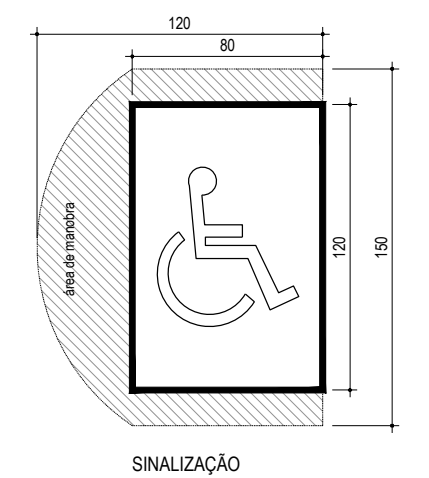
120
80
área de manobra
120
150

SINALIZAÇÃO
ÁREA DE RESGATE NAS ESCADAS

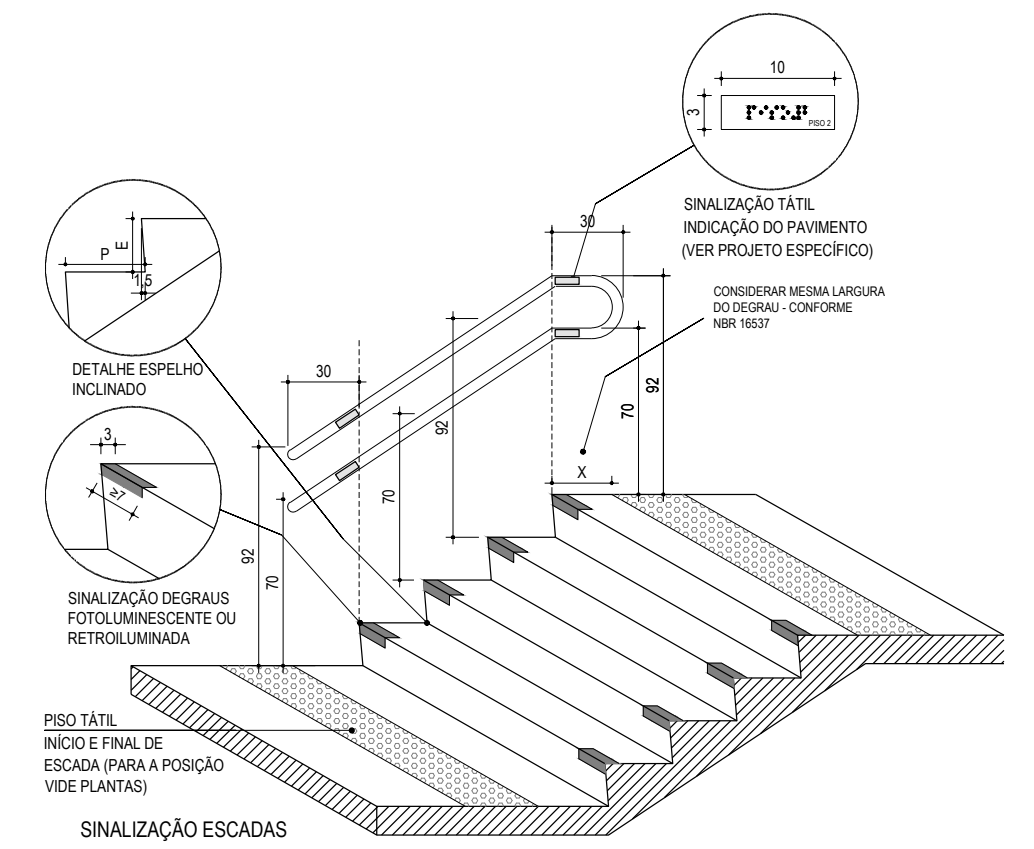
10
3
SINALIZAÇÃO TÁTIL INDICAÇÃO DO PAVIMENTO (VER PROJETO ESPECÍFICO)
CONSIDERAR MESMA LARGURA DO DEGRAU - CONFORME NBR 16537
DETALHE ESPELHO INCLINADO
SINALIZAÇÃO DEGRAUS FOTOLUMINESCENTE OU RETROILUMINADA
PISO TÁTIL INÍCIO E FINAL DE ESCADA (PARA A POSIÇÃO VIDE PLANTAS)
30
92
70
X

SINALIZAÇÃO ESCADAS
SEM ESCALA

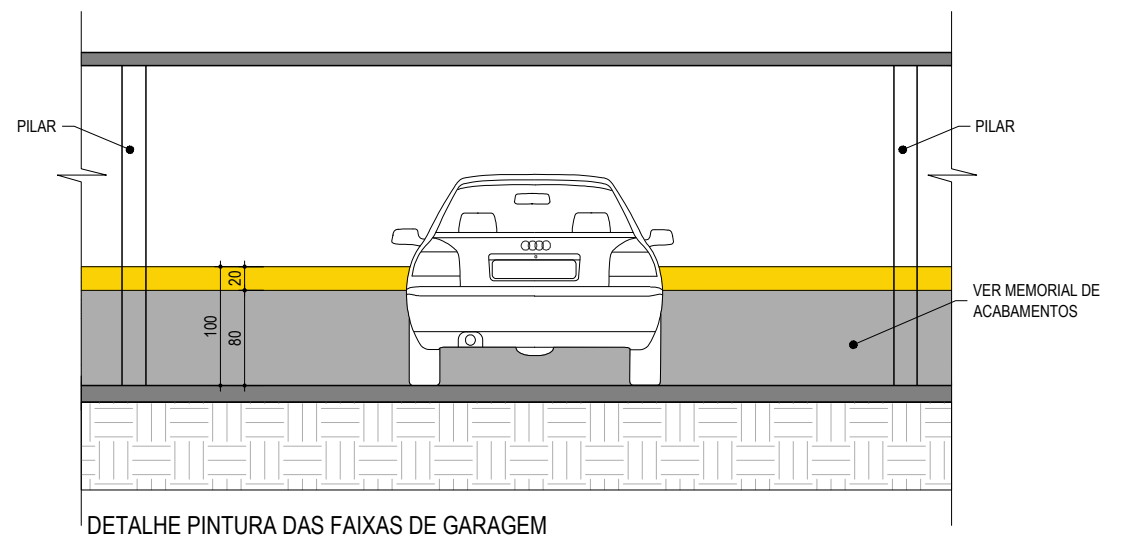
PILAR
PILAR
VER MEMORIAL DE ACABAMENTOS
20
100
80

DETALHE PINTURA DAS FAIXAS DE GARAGEM
ESC. 1:50

TRAVESSA EXISTENTE (Boulevard)
LUIZ DE CAMÕES
RUA ANTÔNIO VIEIRA
RUA CARLOS GOMES
AVENIDA DA LUZ
N
OBRA: ATENTAR PARA NAS DIMENSÕES DOS ENCHIMENTOS PARA NÃO INTERFERIREM NAS MEDIDAS DAS VAGAS E MANOBRAS
30,56 NO
21,35
X1
X2
Y1
Y2
B

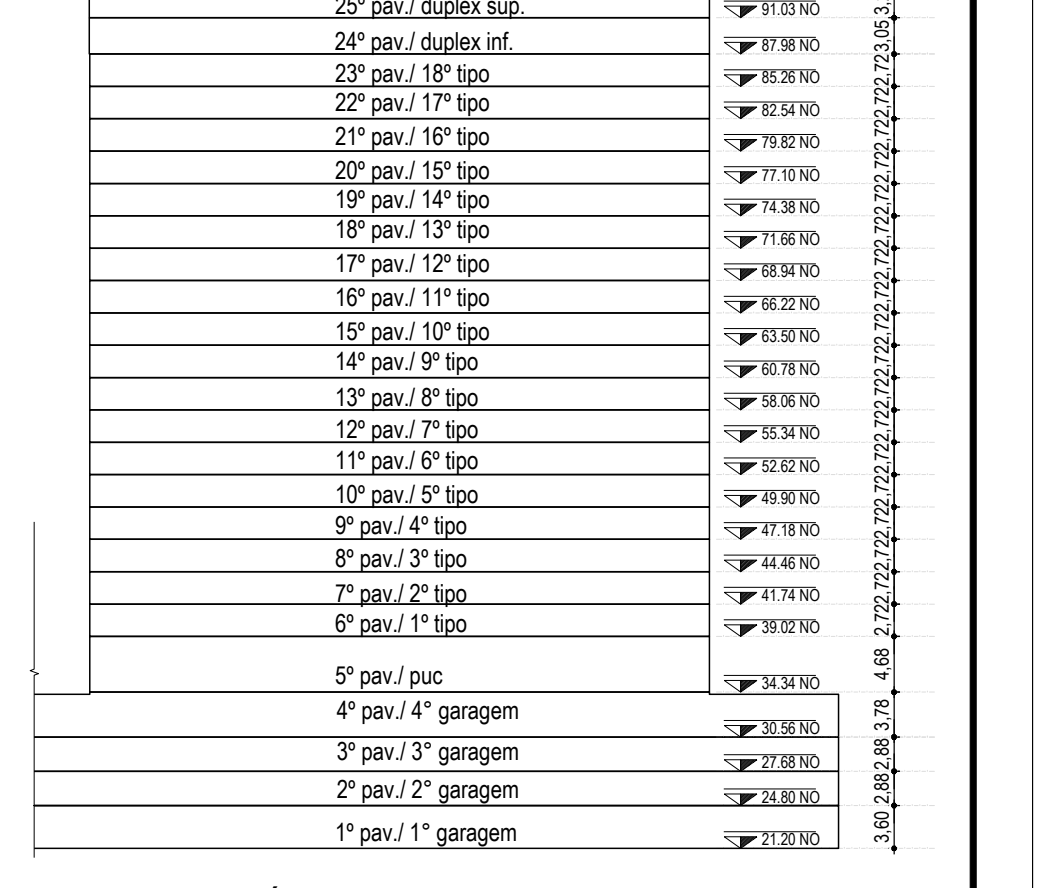
cobertura
reservatório superior
barrilete
25º pav./ duplex sup.
24º pav./ duplex inf.
23º pav./ 18º tipo
22º pav./ 17º tipo
21º pav./ 16º tipo
20º pav./ 15º tipo
19º pav./ 14º tipo
18º pav./ 13º tipo
17º pav./ 12º tipo
16º pav./ 11º tipo
15º pav./ 10º tipo
14º pav./ 9º tipo
13º pav./ 8º tipo
12º pav./ 7º tipo
11º pav./ 6º tipo
10º pav./ 5º tipo
9º pav./ 4º tipo
8º pav./ 3º tipo
7º pav./ 2º tipo
6º pav./ 1º tipo
5º pav./ puc
4º pav./ 4° garagem
3º pav./ 3° garagem
2º pav./ 2° garagem
1º pav./ 1° garagem
101.15 NO
96.65 NO
94.23 NO
91.03 NO
87.98 NO
85.26 NO
82.54 NO
79.82 NO
77.10 NO
74.38 NO
71.66 NO
68.94 NO
66.22 NO
63.50 NO
60.78 NO
58.06 NO
55.34 NO
52.62 NO
49.90 NO
47.18 NO
44.46 NO
41.74 NO
39.02 NO
34.34 NO
30.56 NO
27.68 NO
24.80 NO
21.20 NO
4,50
2,42
3,20
3,05
2,72
4,68
3,78
2,88
2,88
3,60

CORTE ESQUEMÁTICO
esc.: 1:500

LEIS

NBR 15575:2013 - DESEMPENHO DE EDIFICAÇÕES HABITACIONAIS;
NBR 9050:2020 - ACESSIBILIDADE A EDIFICAÇÕES, MOBILIÁRIO, ESPAÇO E EQUIPAMENTOS URBANOS;
NBR 14718:2019 - GUARDA-CORPOS PARA EDIFICAÇÕES;
NBR 13103:2020 - INSTALAÇÃO DE APARELHOS A GÁS PARA USO RESIDENCIAL - REQUISITOS DOS AMBIENTES;
NBR 9077:2001 - SAÍDAS DE EMERGÊNCIA EM EDIFÍCIOS;
NBR NM 313 - ELEVADORES DE PASSAGEIROS;

VIDA ÚTIL DO PROJETO (VUP)
Conforme mínimo especificado na NBR 15575:2013- Desempenho de edificações habitacionais

- ESTRUTURA: >/ 50 anos;
- PISOS INTERNOS: >/ 13 anos;
- VEDAÇÃO VERTICAL EXTERNA: >/ 40 anos;
- VEDAÇÃO VERTICAL INTERNA: >/ 20 anos;
- COBERTURA: >/ 20 anos;
- HIDROSSANITÁRIO: >/ 20 anos;

TRRF DAS PAREDES
a. ESCADA DE EMERGÊNCIA, SALA DE PRESSURIZAÇÃO E CASA DE BOMBAS DE INCÊNDIO DEVEM TER TRRF DE 120 min;
b. ESTRUTURAS DA EDIFICAÇÃO DEVEM TER TRRF DE 120min;
c. ABERTURAS ENTRE LAJES (SHAFTS) DEVEM TER VEDAÇÃO COM MATERIAIS DE TRRF DE 120min;
d. AS PAREDES ENTRE AS UNIDADES E ENTRE AS UNIDADES E A ÁREA DE CIRCULAÇÃO DEVEM TER TRRF DE 60min;
e. COMPARTIMENTAÇÃO VERTICAL EXTERNA DE FACHADA COM VERGA-PEITORIL DE 1,20m COM TRRF DE 120 min;

LEGENDA DETALHE DE MADEIRA
PEM - PORTA ENTRADA DE MADEIRA
PIM - PORTA INTERNA DE MADEIRA
RU - RESISTENTE À UMIDADE
PIA - PORTA INSOLANTE ACÚSTICA

NOTAS
1 - TODAS AS MEDIDAS ESTÃO EM CENTÍMETROS.
2 - VER MEMORIAL DESCRITIVO DE ACABAMENTOS.
3 - VER CADERNOS DE DETALHES.
4 - ÁREAS EXTERNAS - VER PROJETO DE PAISAGISMO.
5 - ÁREAS SOCIAIS INTERNAS - VER PROJETO DE INTERIORES.
6 - CONSIDERAR AS MEDIDAS PARA AS VAGAS:
. VAGA = 250 x 500 cm
. VAGA P.C.D. = 370 x 500 cm

TABELA DE ACABAMENTOS
VER ESPECIFICAÇÃO COMPLETA DE MATERIAIS NOS CADERNOS DE DETALHES E NO MEMORIAL DE ACABAMENTOS DO CLIENTE. PARA O USO DE MATERIAIS SIMILARES CONSULTAR O COORDENADOR DE PROJETOS.

INDICAÇÃO DE NÍVEIS
00.00(NA) → NÍVEL ACABADO
00.00(NO) → NÍVEL OSSO

⬡ - SINALIZAÇÃO TÁTIL

LEGENDA:

REPRESENTAÇÃO GRÁFICA

☐	ALVENARIA
▨	ENCHIMENTO
▒	FORRO / SANCA
🟦	AR CONDICIONADO PREVISÃO

PLANTAS DE REFERÊNCIA PARA BASE DE PROJETO

REVISÃO	DATA	DESCRIÇÃO	RESP.
00	15/02/2023	EMISSÃO INICIAL	

INCORPORAÇÃO
JERONIMO DA VEIGA
Empreendimentos e Participações Ltda.

CONSTRUÇÃO

PROJETISTA
ADESA ARQUITETURA
RUA PADRE GARCIA VELHO, 73 - CJ. 41
CEP: 05421- 030
FONE: 3032 4355 / 3032 4362

DISCIPLINA
ARQUITETURA

CÓDIGO/OBRA
DUO

FASE
LIBERADO OBRA

EMPREENDIMENTO
DUO
AV_LUZ

ASSUNTO
PLANTA
4º_PAVIMENTO

FOLHA N.º
ARQ
104

RESPONSÁVEL
ADELINO SANTOS

SUPERVISOR
ADELINO SANTOS

COORDENADOR
ALISSA LOPES

REVISÃO
R00

PROJETISTA

ARQUIVO
DUO-ARQ-LO-104-PLA-4PV-R00.dwg

ESCALA
1:75

DATA
15/02/2023

DIREITOS AUTORAIS RESERVADO A REPRODUÇÃO TOTAL OU PARCIAL SEM PRÉVIA AUTORIZAÇÃO, CONFORME RESOLUÇÃO N° 67, DE 5 DE DEZEMBRO DE 2013