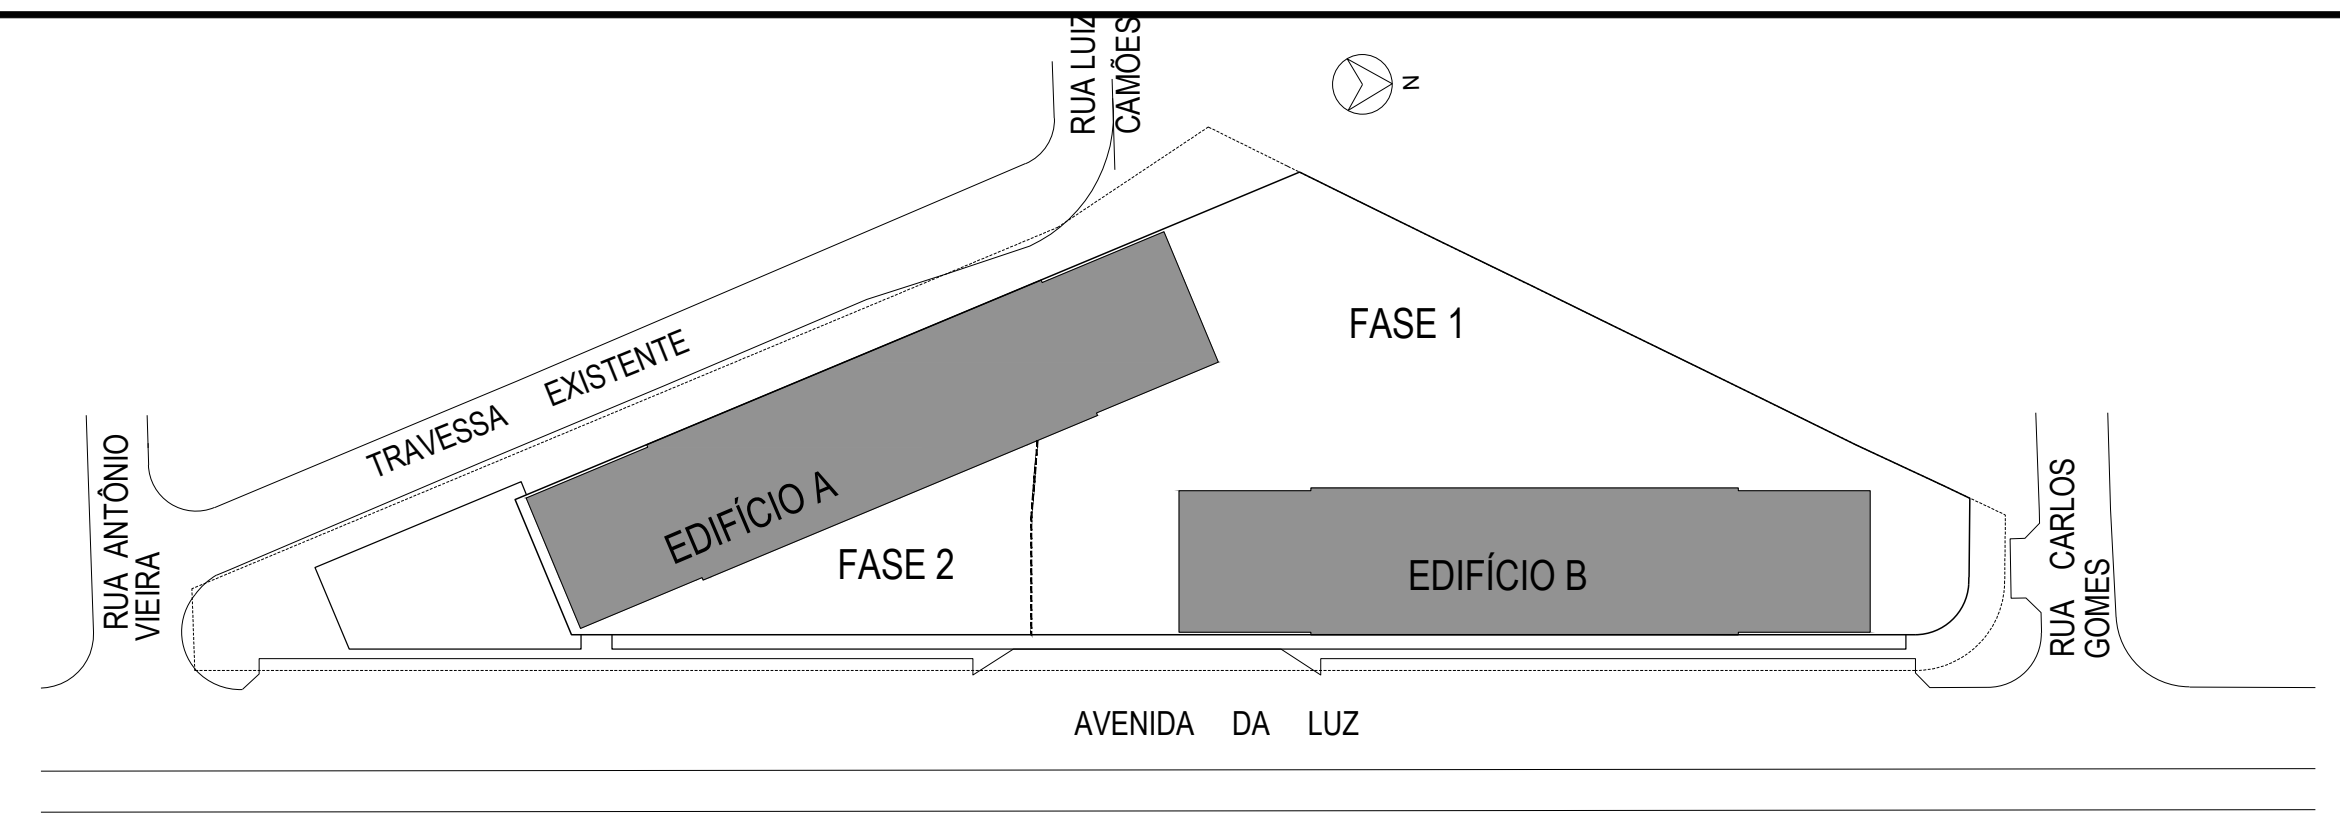
RUA LUIZ CAMÕES
TRAVESSA EXISTENTE
FASE 1
FASE 2
EDIFÍCIO A
EDIFÍCIO B
RUA ANTÔNIO VIEIRA
RUA CARLOS GOMES
AVENIDA DA LUZ

IMPLANTAÇÃO
esc.: 1:500

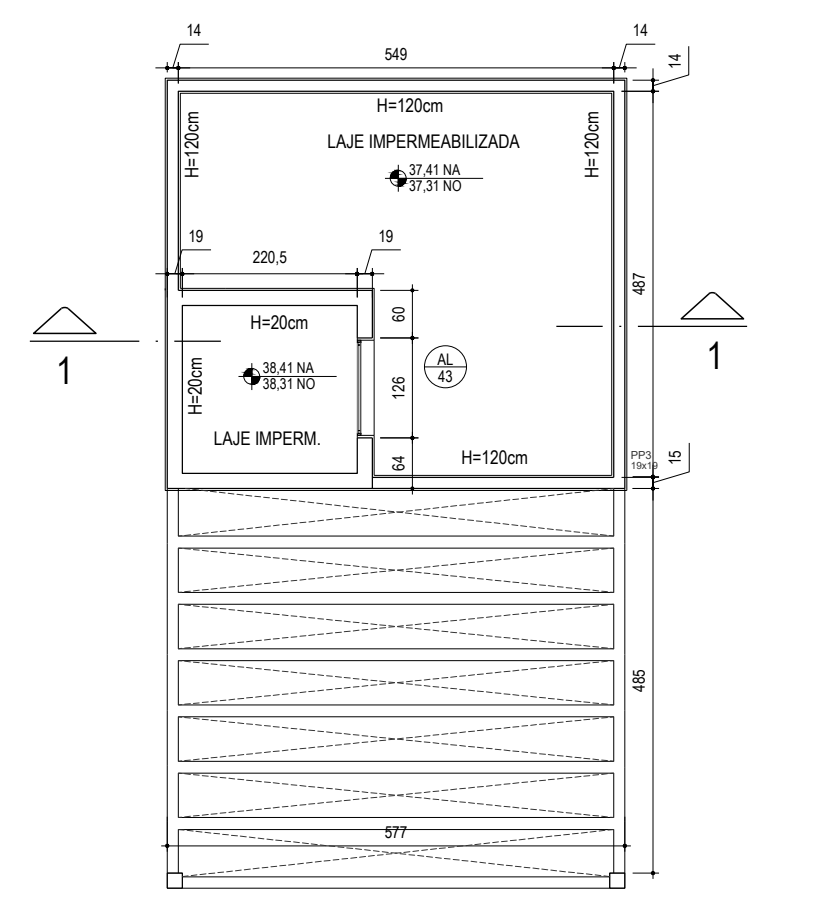
549
H=120cm
LAJE IMPERMEABILIZADA
37,41 NA
37,31 NO
220,5
H=20cm
38,41 NA
38,31 NO
LAJE IMPERM.
AL 43
H=120cm
1
1
485
577

PLANTA COBERTURA ACESSO
esc. 1:75

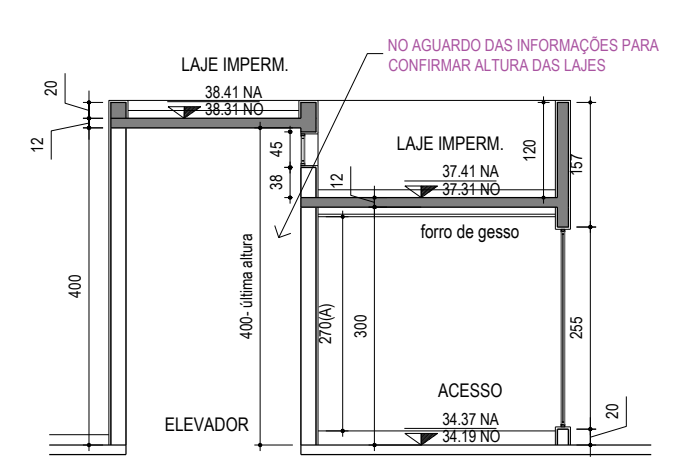
LAJE IMPERM.
38,41 NA
38,31 NO
NO AGUARDO DAS INFORMAÇÕES PARA CONFIRMAR ALTURA DAS LAJES
LAJE IMPERM.
37,41 NA
37,31 NO
forro de gesso
400- última altura
ELEVADOR
ACESSO
34,37 NA
34,19 NO

CORTE 1-1
esc. 1:75

RUA LUIZ DE CAMÕES
TRAVESSA EXISTENTE (Bosque)
RUA ANTÔNIO VIEIRA
AVENIDA DA LUZ
RUA CARLOS GOMES
N
21.48
21,35
VER FOLHA 106
VER FOLHA 110
COWORKING
ELEVADOR
ESPAÇO FITNESS
CIRCULAÇÃO
W.C. P.C.D.
W.C. MASC.
W.C. FEM.
HALL
SPA
BRINQUEDOTECA
ESPAÇO DE CONVIVÊNCIA
ACESSO
QUADRA STREET BALL
JUNTA
proj. cobertura
proj. pergolado descoberto
DECK MOLHADO
NA 34.70
NF 34.60
NL 34.50
PISCINA ADULTOS
NA 34.70
NF 33.50
NL 33.40
PISCINA INFANTIL
NA 34.22
NF 33.92
NL 33.82
C=9.6m i=4.9%
NP 34.33
NL 34.19
NP 34.80
NL 34.70
NT 35.00
NL 34.50
NT 34.69
NL 34.19
NM 34.80
NM 35.00
34,37 NA
34,34 NO
34,38 NA
34,34 NO
A
B
Y
1
20,63
20,85
20,41

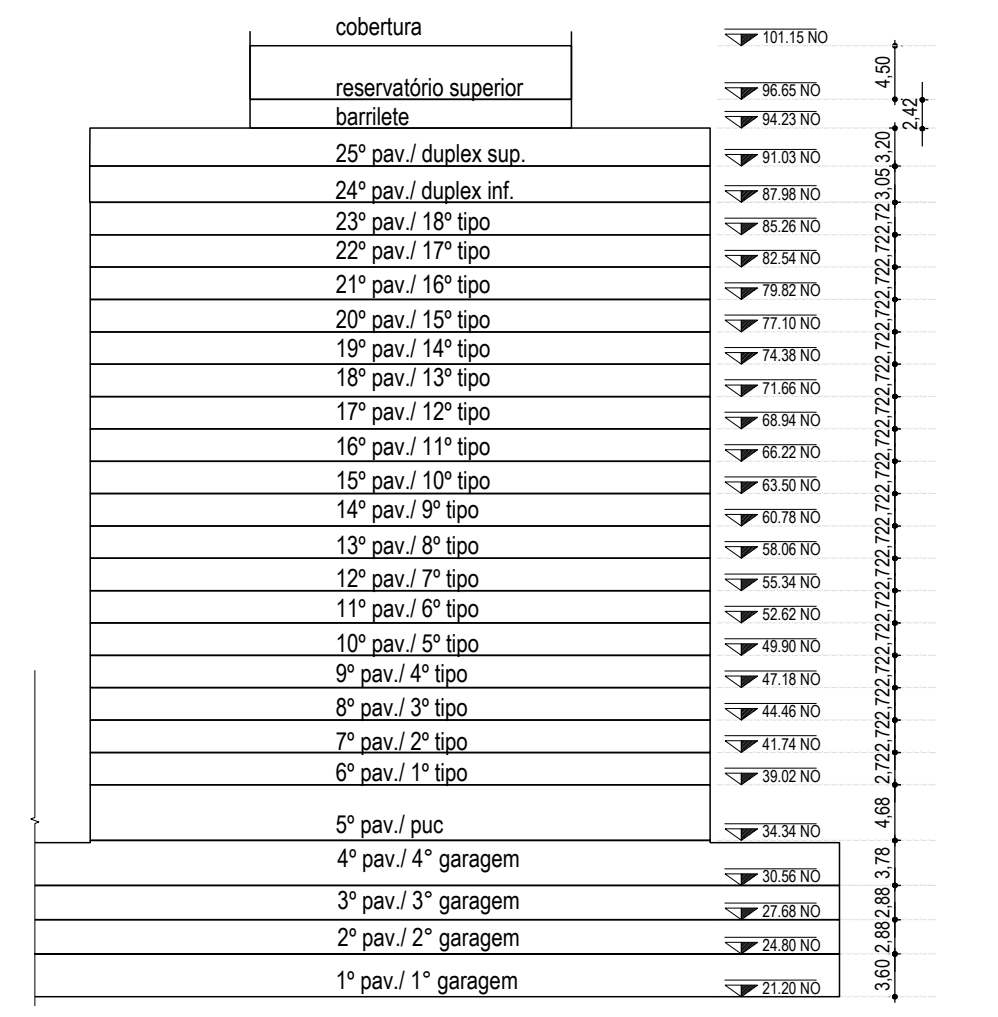
cobertura
reservatório superior
barrilete
25º pav./ duplex sup.
24º pav./ duplex inf.
23º pav./ 18º tipo
22º pav./ 17º tipo
21º pav./ 16º tipo
20º pav./ 15º tipo
19º pav./ 14º tipo
18º pav./ 13º tipo
17º pav./ 12º tipo
16º pav./ 11º tipo
15º pav./ 10º tipo
14º pav./ 9º tipo
13º pav./ 8º tipo
12º pav./ 7º tipo
11º pav./ 6º tipo
10º pav./ 5º tipo
9º pav./ 4º tipo
8º pav./ 3º tipo
7º pav./ 2º tipo
6º pav./ 1º tipo
5º pav./ puc
4º pav./ 4° garagem
3º pav./ 3° garagem
2º pav./ 2° garagem
1º pav./ 1° garagem
101.15 NO
96.65 NO
94.23 NO
91.03 NO
87.98 NO
85.26 NO
82.54 NO
79.82 NO
77.10 NO
74.38 NO
71.66 NO
68.94 NO
66.22 NO
63.50 NO
60.78 NO
58.06 NO
55.34 NO
52.62 NO
49.90 NO
47.18 NO
44.46 NO
41.74 NO
39.02 NO
34.34 NO
30.56 NO
27.68 NO
24.80 NO
21.20 NO
4,50
2,42
3,20
3,05
2,72
4,68
3,78
2,88
3,60

CORTE ESQUEMÁTICO
esc.: 1:500

LEIS

NBR 15575:2013 - DESEMPENHO DE EDIFICAÇÕES HABITACIONAIS;
NBR 9050:2020 - ACESSIBILIDADE A EDIFICAÇÕES, MOBILIÁRIO, ESPAÇO E EQUIPAMENTOS URBANOS;
NBR 14718:2019 - GUARDA-CORPOS PARA EDIFICAÇÕES;
NBR 13103:2020 - INSTALAÇÃO DE APARELHOS A GÁS PARA USO RESIDENCIAL - REQUISITOS DOS AMBIENTES;
NBR 9077:2001 - SAÍDAS DE EMERGÊNCIA EM EDIFÍCIOS;
NBR NM 313 - ELEVADORES DE PASSAGEIROS;

VIDA ÚTIL DO PROJETO (VUP)
Conforme mínimo especificado na NBR 15575:2013- Desempenho de edificações habitacionais

- ESTRUTURA: >/ 50 anos;
- PISOS INTERNOS: >/ 13 anos;
- VEDAÇÃO VERTICAL EXTERNA: >/ 40 anos;
- VEDAÇÃO VERTICAL INTERNA: >/ 20 anos;
- COBERTURA: >/ 20 anos;
- HIDROSSANITÁRIO: >/ 20 anos;

TRRF DAS PAREDES

a. ESCADA DE EMERGÊNCIA, SALA DE PRESSURIZAÇÃO E CASA DE BOMBAS DE INCÊNDIO DEVEM TER TRRF DE 120 min;
b. ESTRUTURAS DA EDIFICAÇÃO DEVEM TER TRRF DE 120min;
c. ABERTURAS ENTRE LAJES (SHAFTS) DEVEM TER VEDAÇÃO COM MATERIAIS DE TRRF DE 120min;
d. AS PAREDES ENTRE AS UNIDADES E ENTRE AS UNIDADES E A ÁREA DE CIRCULAÇÃO DEVEM TER TRRF DE 60min;
e. COMPARTIMENTAÇÃO VERTICAL EXTERNA DE FACHADA COM VERGA-PEITORIL DE 1,20m COM TRRF DE 120 min;

LEGENDA DETALHE DE MADEIRA
PEM - PORTA ENTRADA DE MADEIRA
PIM - PORTA INTERNA DE MADEIRA
RU - RESISTENTE À UMIDADE
PIA - PORTA INSOLANTE ACÚSTICA

NOTAS

1 - TODAS AS MEDIDAS ESTÃO EM CENTÍMETROS.
2 - VER MEMORIAL DESCRITIVO DE ACABAMENTOS.
3 - VER CADERNOS DE DETALHES.
4 - ÁREAS EXTERNAS - VER PROJETO DE PAISAGISMO.
5 - ÁREAS SOCIAIS INTERNAS - VER PROJETO DE INTERIORES.
6 - CONSIDERAR AS MEDIDAS PARA AS VAGAS:
. VAGA = 250 x 500 cm
. VAGA P.C.D. = 370 x 500 cm

TABELA DE ACABAMENTOS

VER ESPECIFICAÇÃO COMPLETA DE MATERIAIS NOS CADERNOS DE DETALHES E NO MEMORIAL DE ACABAMENTOS DO CLIENTE. PARA O USO DE MATERIAIS SIMILARES CONSULTAR O COORDENADOR DE PROJETOS.

INDICAÇÃO DE NÍVEIS

00.00(NA) → NÍVEL ACABADO
00.00(NO) → NÍVEL OSSO

⬡ - SINALIZAÇÃO TÁTIL

LEGENDA:

REPRESENTAÇÃO GRÁFICA

- ▭ ALVENARIA
- ▨ ENCHIMENTO
- ▭ FORRO / SANCA
- 🟦 AR CONDICIONADO PREVISÃO

PLANTAS DE REFERÊNCIA PARA BASE DE PROJETO

REVISÃO	DATA	DESCRIÇÃO	RESP.
00	24/02/2023	EMISSÃO INICIAL	

INCORPORAÇÃO
JERONIMO DA VEIGA
Empreendimentos e Participações Ltda.

CONSTRUÇÃO

PROJETISTA
ADESA ARQUITETURA
RUA PADRE GARCIA VELHO, 73 - CJ. 41
CEP: 05421- 030
FONE: 3032 4355 / 3032 4362

DISCIPLINA
ARQUITETURA

CÓDIGO/OBRA
DUO

FASE
LIBERADO OBRA

EMPREENDIMENTO
DUO
AV_LUZ

ASSUNTO
PLANTA
PUC

FOLHA N.º
ARQ
105

RESPONSÁVEL
ADELINO SANTOS

SUPERVISOR
ADELINO SANTOS

COORDENADOR
ALISSA LOPES

REVISÃO
R00

PROJETISTA

ARQUIVO
DUO-ARQ-LO-105-PLA-PUC-R00.dwg

ESCALA
1:75

DATA
24/02/2023

DIREITOS AUTORAIS RESERVADO A REPRODUÇÃO TOTAL OU PARCIAL SEM PRÉVIA AUTORIZAÇÃO, CONFORME RESOLUÇÃO N° 67, DE 5 DE DEZEMBRO DE 2013