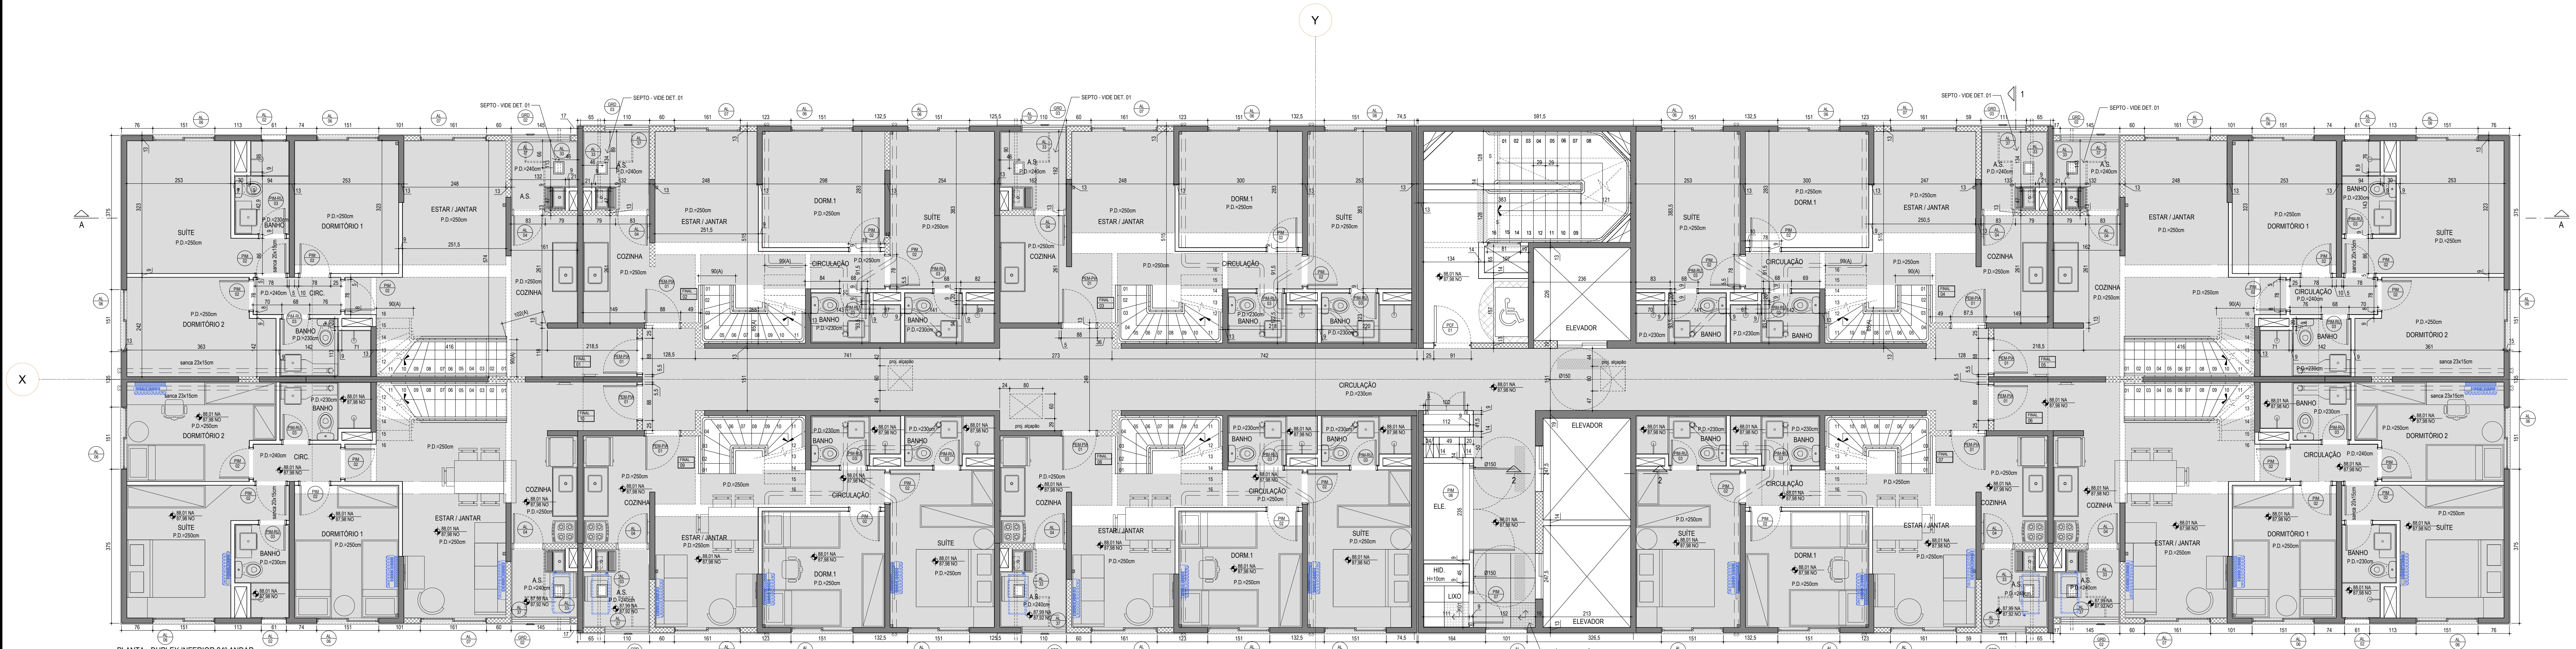
Y
X
A
SEPTO - VIDE DET. 01
SUÍTE
DORMITÓRIO 1
DORMITÓRIO 2
ESTAR / JANTAR
COZINHA
BANHO
CIRC.
A.S.
DORM 1
CIRCULAÇÃO
ELEVADOR
ELE
HID.
LIXO
INÍCIO PAGINAÇÃO

PLANTA - DUPLEX INFERIOR 24º ANDAR

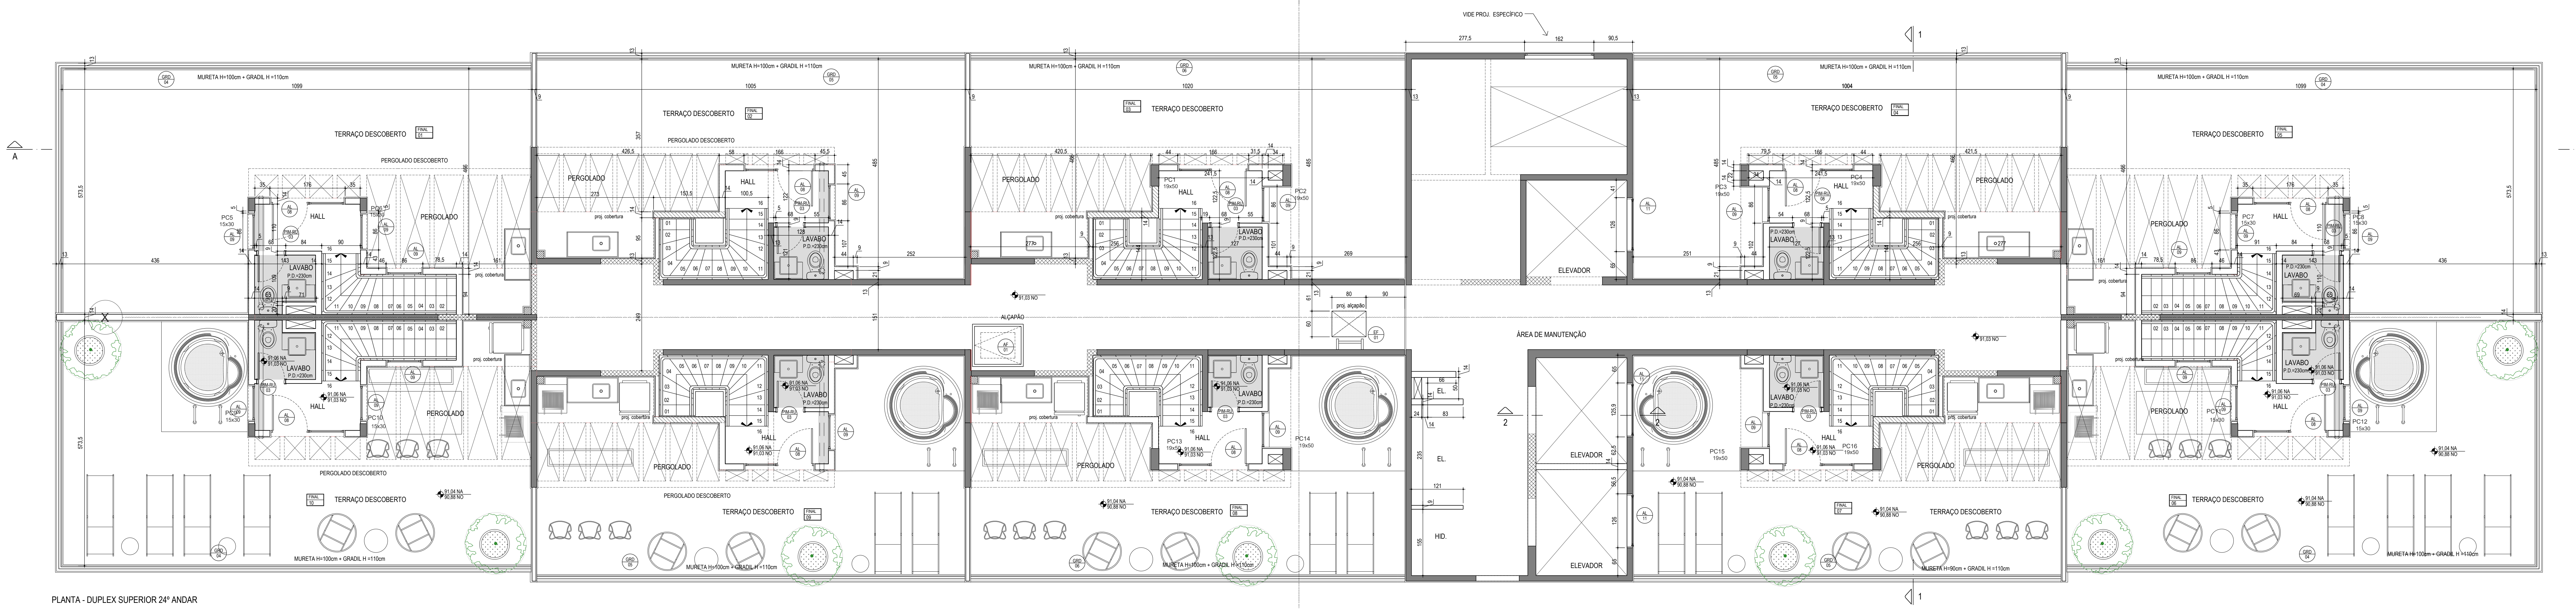
VIDE PROJ. ESPECÍFICO
MURETA H=100cm + GRADIL H =110cm
TERRAÇO DESCOBERTO
PERGOLADO DESCOBERTO
PERGOLADO
HALL
LAVABO
ALÇAPÃO
ÁREA DE MANUTENÇÃO
ELEVADOR
EL.
HID

PLANTA - DUPLEX SUPERIOR 24º ANDAR

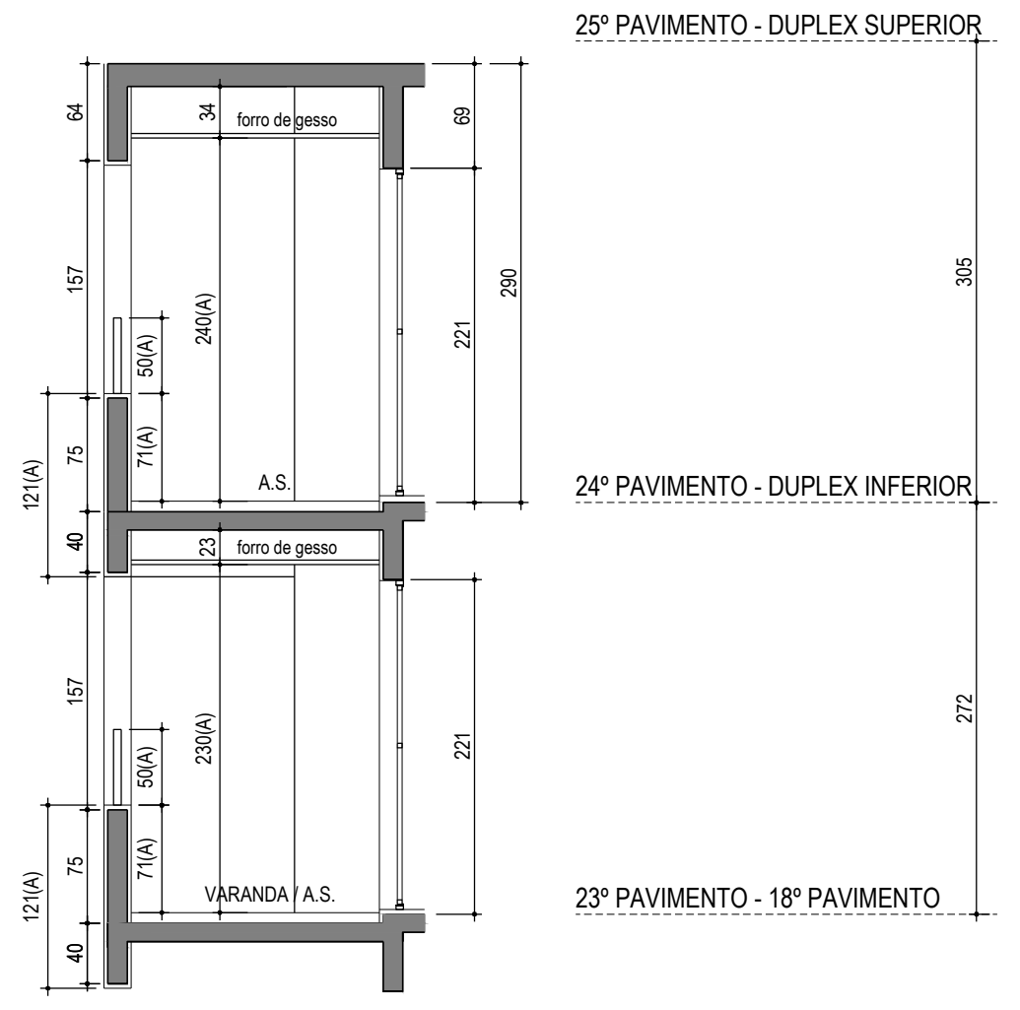
25º PAVIMENTO - DUPLEX SUPERIOR
24º PAVIMENTO - DUPLEX INFERIOR
23º PAVIMENTO - 18º PAVIMENTO
forro de gesso
A.S.
VARANDA / A.S.
64
34
69
157
290
240(A)
221
305
50(A)
71(A)
75
121(A)
40
23
230(A)
272

CORTE 1-1 VENTILAÇÃO A.S.
ESC. 1:50

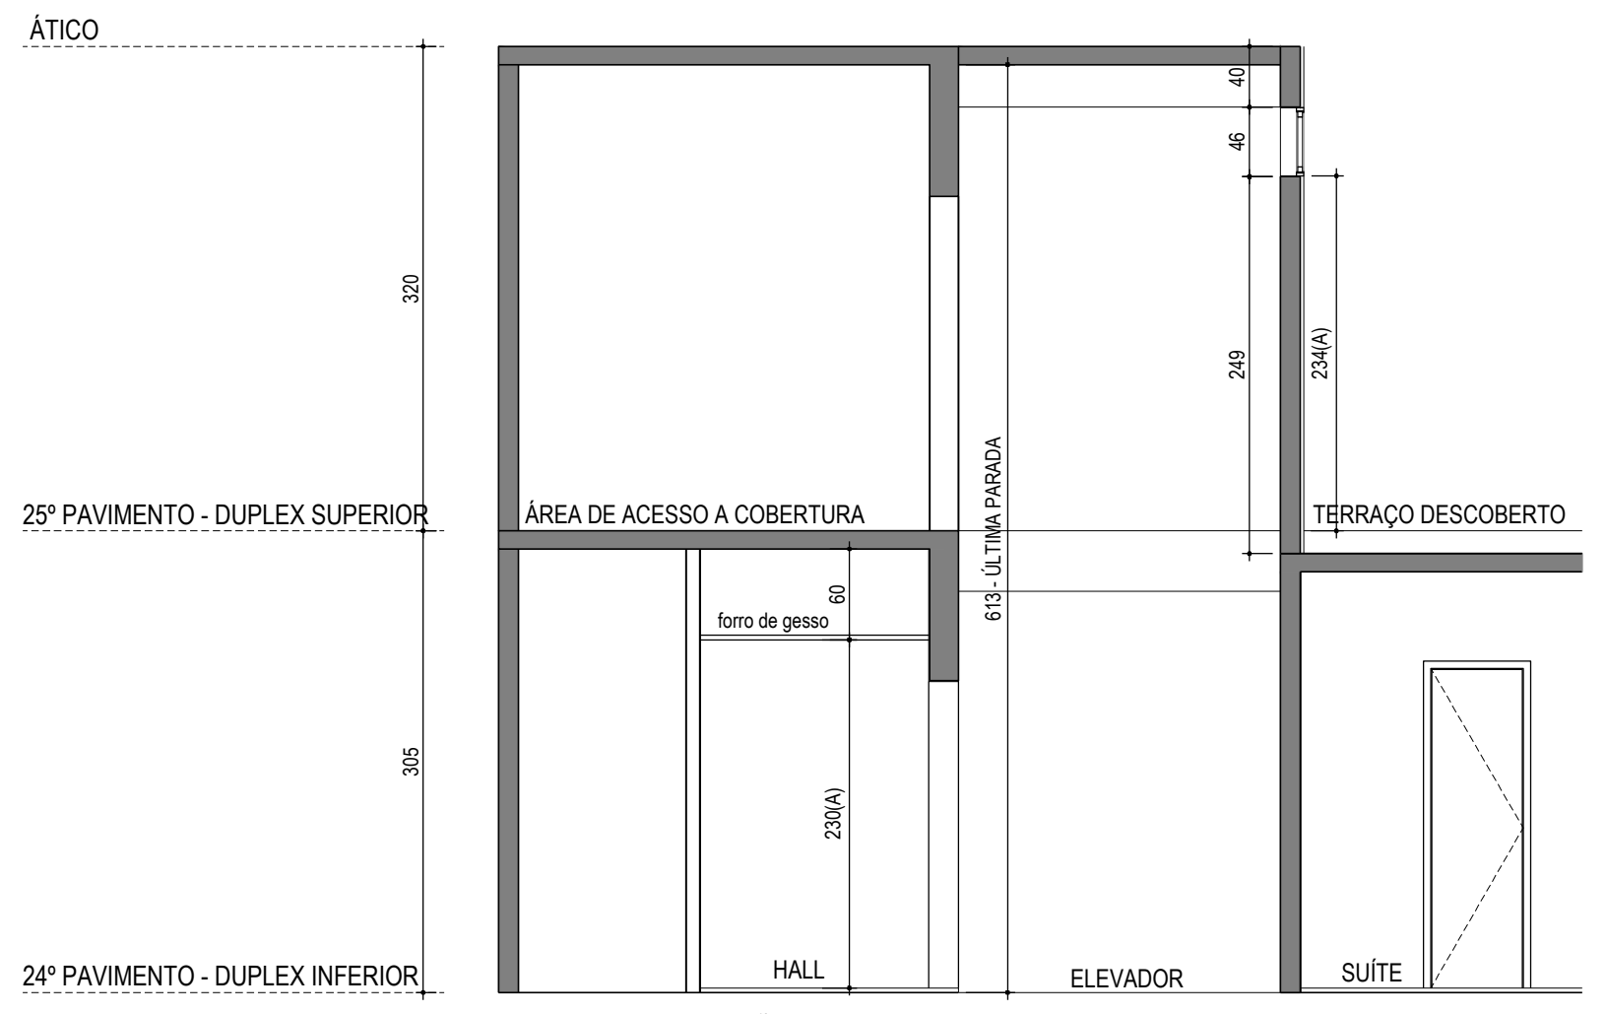
ÁTICO
25º PAVIMENTO - DUPLEX SUPERIOR
24º PAVIMENTO - DUPLEX INFERIOR
ÁREA DE ACESSO A COBERTURA
TERRAÇO DESCOBERTO
forro de gesso
613 - ÚLTIMA PARADA
HALL
ELEVADOR
SUÍTE
320
305
40
46
249
234(A)
60
230(A)

CORTE 2-2 VENTILAÇÃO ELEVADOR
ESC. 1:50

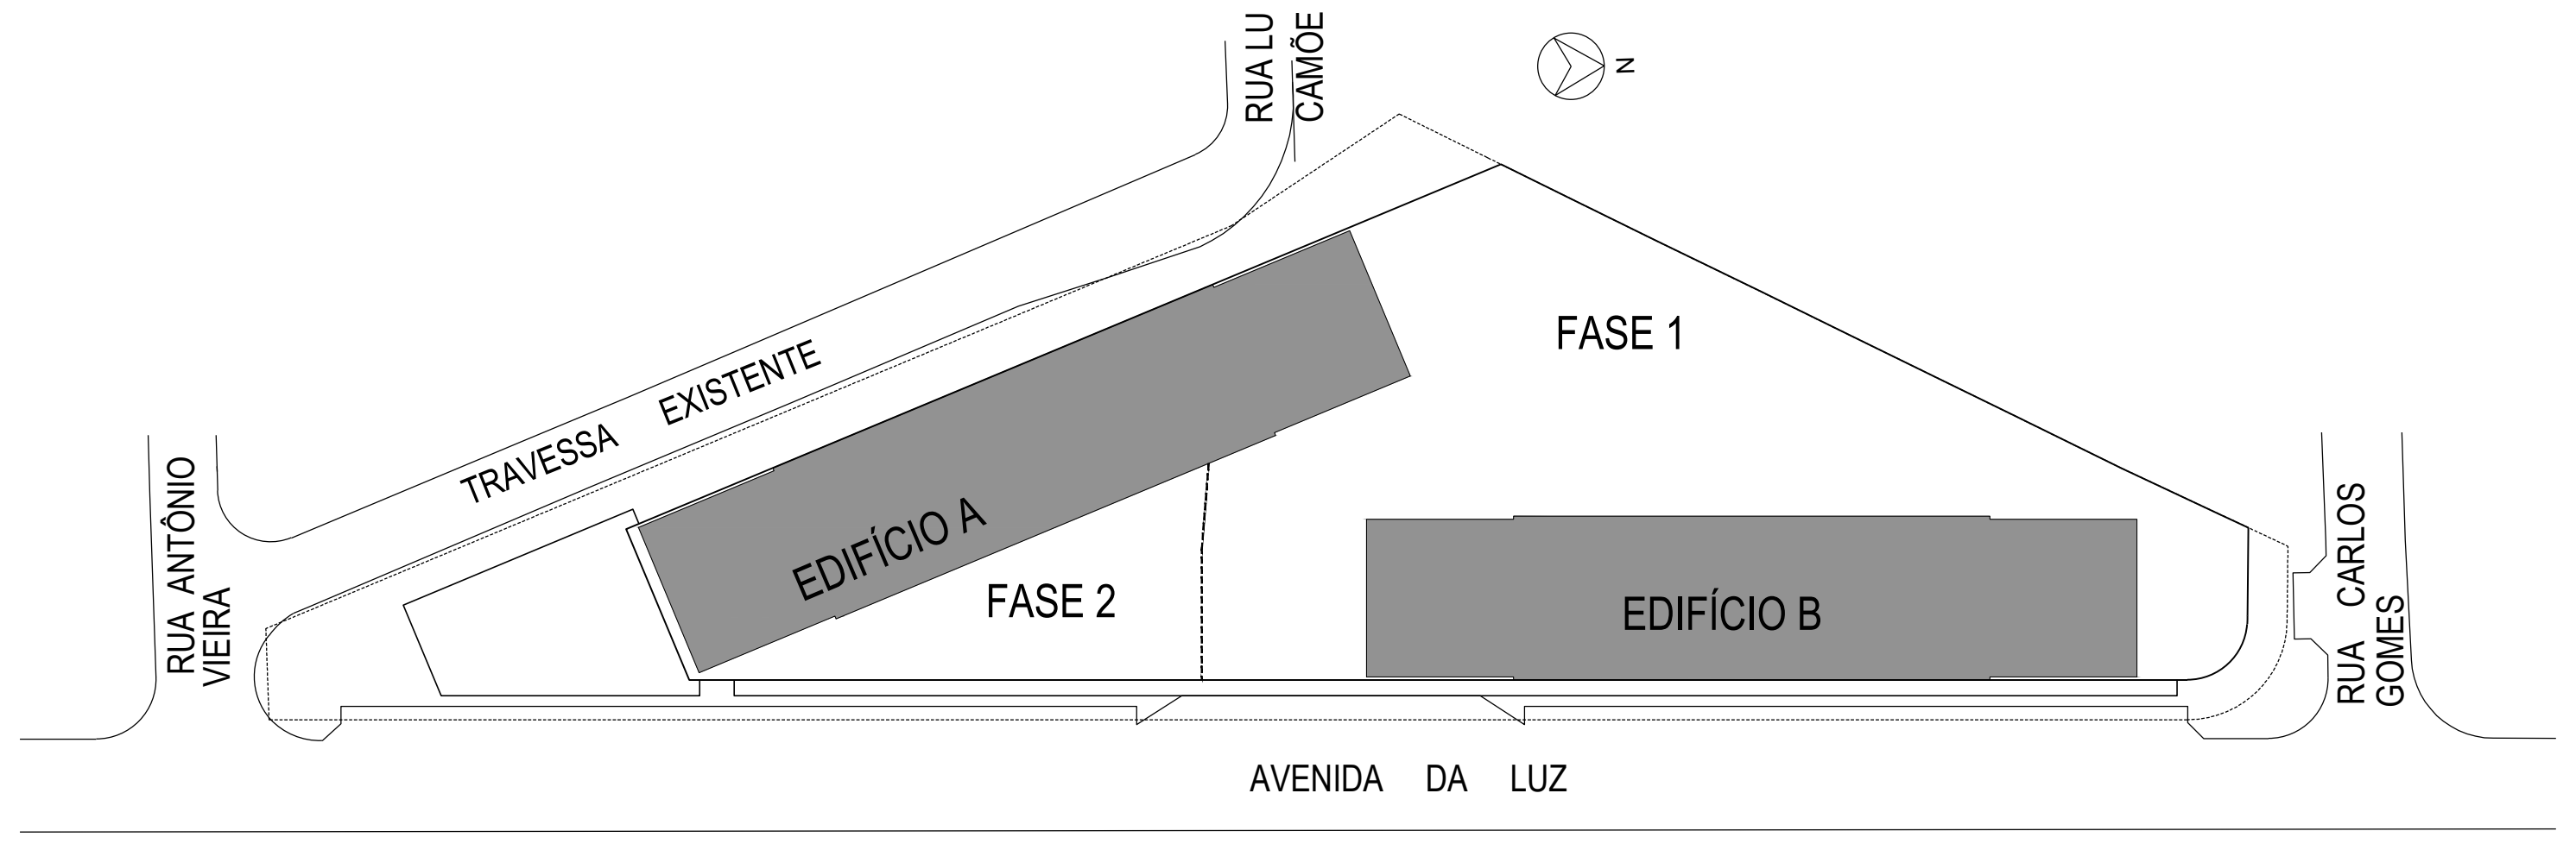
RUA LU CAMÕE
N
TRAVESSA EXISTENTE
FASE 1
FASE 2
EDIFÍCIO A
EDIFÍCIO B
RUA ANTÔNIO VIEIRA
RUA CARLOS GOMES
AVENIDA DA LUZ

IMPLANTAÇÃO
esc.: 1:500

cobertura

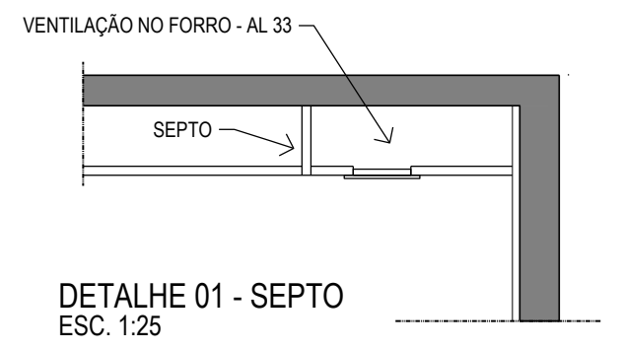
VENTILAÇÃO NO FORRO - AL 33
SEPTO

DETALHE 01 - SEPTO
ESC. 1:25

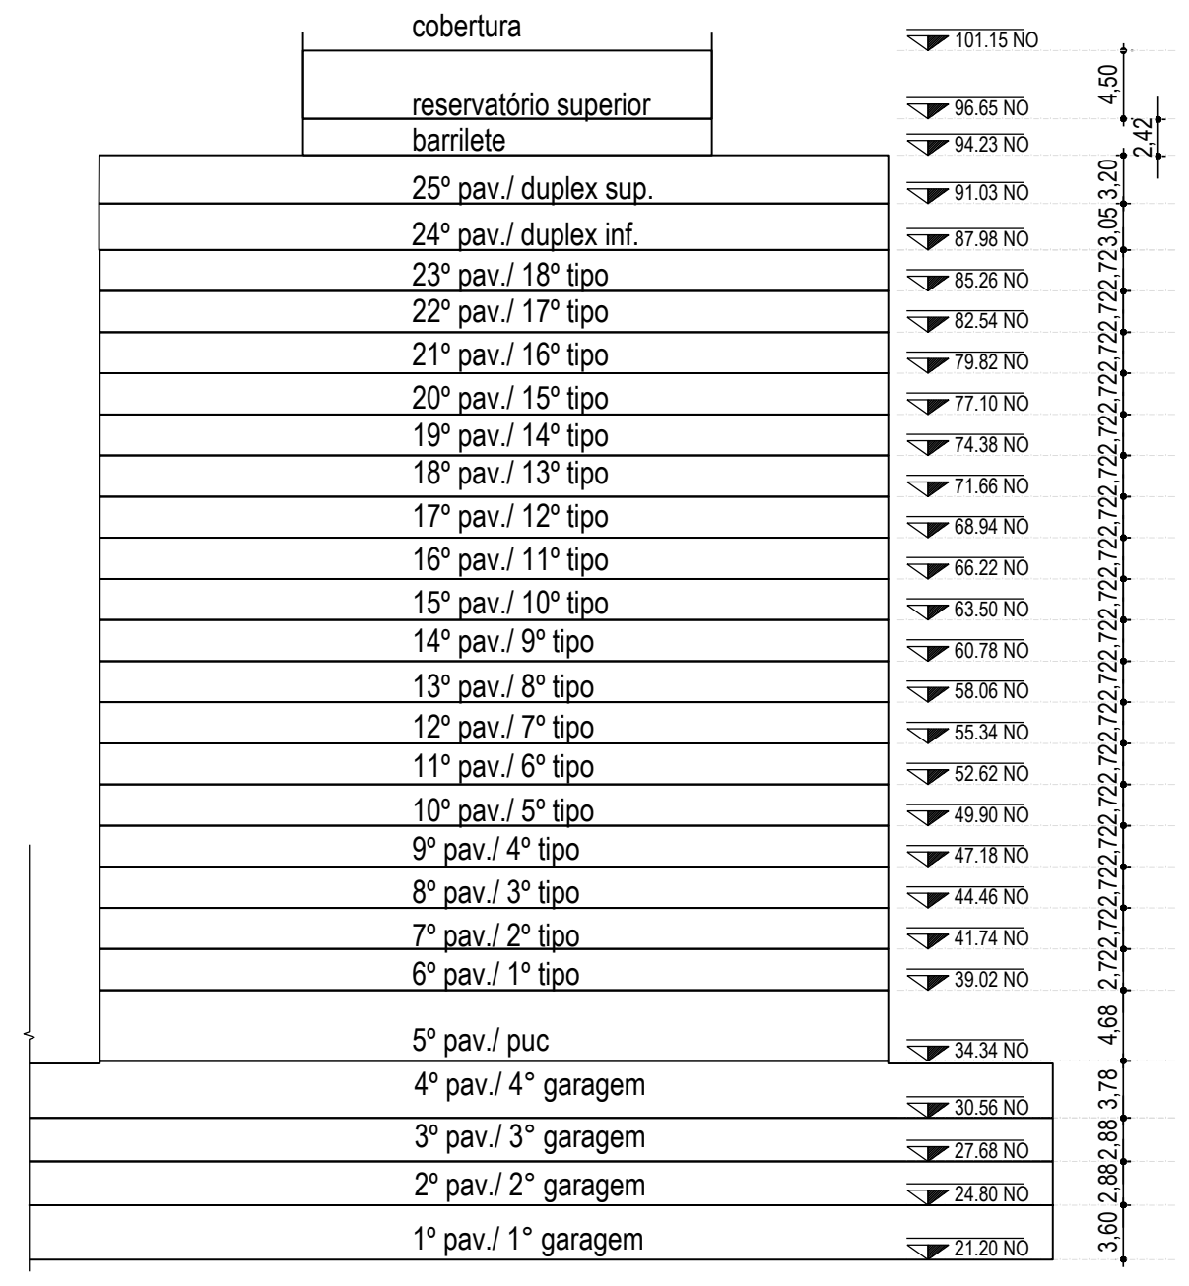
cobertura
reservatório superior
barrilete
25º pav./ duplex sup.
24º pav./ duplex inf.
23º pav./ 18º tipo
22º pav./ 17º tipo
21º pav./ 16º tipo
20º pav./ 15º tipo
19º pav./ 14º tipo
18º pav./ 13º tipo
17º pav./ 12º tipo
16º pav./ 11º tipo
15º pav./ 10º tipo
14º pav./ 9º tipo
13º pav./ 8º tipo
12º pav./ 7º tipo
11º pav./ 6º tipo
10º pav./ 5º tipo
9º pav./ 4º tipo
8º pav./ 3º tipo
7º pav./ 2º tipo
6º pav./ 1º tipo
5º pav./ puc
4º pav./ 4° garagem
3º pav./ 3° garagem
2º pav./ 2° garagem
1º pav./ 1° garagem
101.15 NO
96.65 NO
94.23 NO
91.03 NO
87.98 NO
85.26 NO
82.54 NO
79.82 NO
77.10 NO
74.38 NO
71.66 NO
68.94 NO
66.22 NO
63.50 NO
60.78 NO
58.06 NO
55.34 NO
52.62 NO
49.90 NO
47.18 NO
44.46 NO
41.74 NO
39.02 NO
34.34 NO
30.56 NO
27.68 NO
24.80 NO
21.20 NO
4,50
2,42
3,20
3,05
2,72
4,68
3,78
2,88
3,60

CORTE ESQUEMÁTICO
esc.: 1:500

TABELA DE ESTUDO PARA ELEVADORES			
DATA DA SOLICITAÇÃO : 2022			
FORNECEDORES	ATLAS	OTIS	PROJETO
DIMENSÕES DA CAIXA	240 x 210cm	243x213cm / 236x225cm	251x213cm / 236x230cm
ALTURA ÚLTIMA PARADA	450cm	495cm / 470cm	613cm
ALTURA DO POÇO DE ELEVADOR	180cm	140cm / 170cm	180cm

LEIS

NBR 15575:2013 - DESEMPENHO DE EDIFICAÇÕES HABITACIONAIS;
NBR 9050:2020 - ACESSIBILIDADE A EDIFICAÇÕES, MOBILIÁRIO, ESPAÇO E EQUIPAMENTOS URBANOS;
NBR 14718:2019 - GUARDA-CORPOS PARA EDIFICAÇÕES;
NBR 13103:2020 - INSTALAÇÃO DE APARELHOS A GÁS PARA USO RESIDENCIAL - REQUISITOS DOS AMBIENTES;
NBR 9077:2001 - SAÍDAS DE EMERGÊNCIA EM EDIFÍCIOS;
NBR NM 313 - ELEVADORES DE PASSAGEIROS;

VIDA ÚTIL DO PROJETO (VUP)

Conforme mínimo especificado na NBR 15575:2013- Desempenho de edificações habitacionais

- ESTRUTURA: >/ 50 anos;
- PISOS INTERNOS: >/ 13 anos;
- VEDAÇÃO VERTICAL EXTERNA: >/ 40 anos;
- VEDAÇÃO VERTICAL INTERNA: >/ 20 anos;
- COBERTURA: >/ 20 anos;
- HIDROSSANITÁRIO: >/ 20 anos;

TRRF DAS PAREDES

a. ESCADA DE EMERGÊNCIA, SALA DE PRESSURIZAÇÃO E CASA DE BOMBAS DE INCÊNDIO DEVEM TER TRRF DE 120 min;
b. ESTRUTURAS DA EDIFICAÇÃO DEVEM TER TRRF DE 120min;
c. ABERTURAS ENTRE LAJES (SHAFTS) DEVEM TER VEDAÇÃO COM MATERIAIS DE TRRF DE 120min;
d. AS PAREDES ENTRE AS UNIDADES E ENTRE AS UNIDADES E A ÁREA DE CIRCULAÇÃO DEVEM TER TRRF DE 60min;
e. COMPARTIMENTAÇÃO VERTICAL EXTERNA DE FACHADA COM VERGA-PEITORIL DE 1,20m COM TRRF DE 120 min;

LEGENDA DETALHE DE MADEIRA

PEM - PORTA ENTRADA DE MADEIRA
PIM - PORTA INTERNA DE MADEIRA
RU - RESISTENTE À UMIDADE
PIA - PORTA INSOLANTE ACÚSTICA

NOTAS

1 - TODAS AS MEDIDAS ESTÃO EM CENTÍMETROS.
2 - VER MEMORIAL DESCRITIVO DE ACABAMENTOS.
3 - VER CADERNOS DE DETALHES.
4 - ÁREAS EXTERNAS - VER PROJETO DE PAISAGISMO.
5 - ÁREAS SOCIAIS INTERNAS - VER PROJETO DE INTERIORES.
6 - CONSIDERAR AS MEDIDAS PARA AS VAGAS:
. VAGA = 250 x 500 cm
. VAGA P.C.D. = 370 x 500 cm

TABELA DE ACABAMENTOS

VER ESPECIFICAÇÃO COMPLETA DE MATERIAIS NOS CADERNOS DE DETALHES E NO MEMORIAL DE ACABAMENTOS DO CLIENTE. PARA O USO DE MATERIAIS SIMILARES CONSULTAR O COORDENADOR DE PROJETOS.

INDICAÇÃO DE NÍVEIS

00.00(NA) → NÍVEL ACABADO
00.00(NO) → NÍVEL OSSO

▨ - SINALIZAÇÃO TÁTIL

LEGENDA:

REPRESENTAÇÃO GRÁFICA

▭	ALVENARIA
▨	ENCHIMENTO
▒	FORRO / SANCA
🟦	AR CONDICIONADO PREVISÃO

PLANTAS DE REFERÊNCIA PARA BASE DE PROJETO

REVISÃO	DATA	DESCRIÇÃO	RESP.
00	24/02/2023	EMISSÃO INICIAL	

INCORPORAÇÃO
JERONIMO DA VEIGA
Empreendimentos e Participações Ltda.

CONSTRUÇÃO

PROJETISTA
ADESA ARQUITETURA
RUA PADRE GARCIA VELHO, 73 - CJ. 41
CEP: 05421- 030
FONE: 3032 4355 / 3032 4362

DISCIPLINA
ARQUITETURA
CÓDIGO/OBRA
DUO
FASE
LIBERADO OBRA

EMPREENDIMENTO
DUO
AV_LUZ
ASSUNTO
PLANTAS
DUPLEX_TORRE_A

FOLHA N.º
ARQ
108

RESPONSÁVEL: ADELINO SANTOS
SUPERVISOR: ADELINO SANTOS
COORDENADOR: ALISSA LOPES
REVISÃO: R00
PROJETISTA
ARQUIVO: DUO-ARQ-LO-108-PLA-DPA-R00.dwg
ESCALA: 1:50
DATA: 24/02/2023

DIREITOS AUTORAIS RESERVADO A REPRODUÇÃO TOTAL OU PARCIAL SEM PRÉVIA AUTORIZAÇÃO, CONFORME RESOLUÇÃO N° 67, DE 5 DE DEZEMBRO DE 2013