
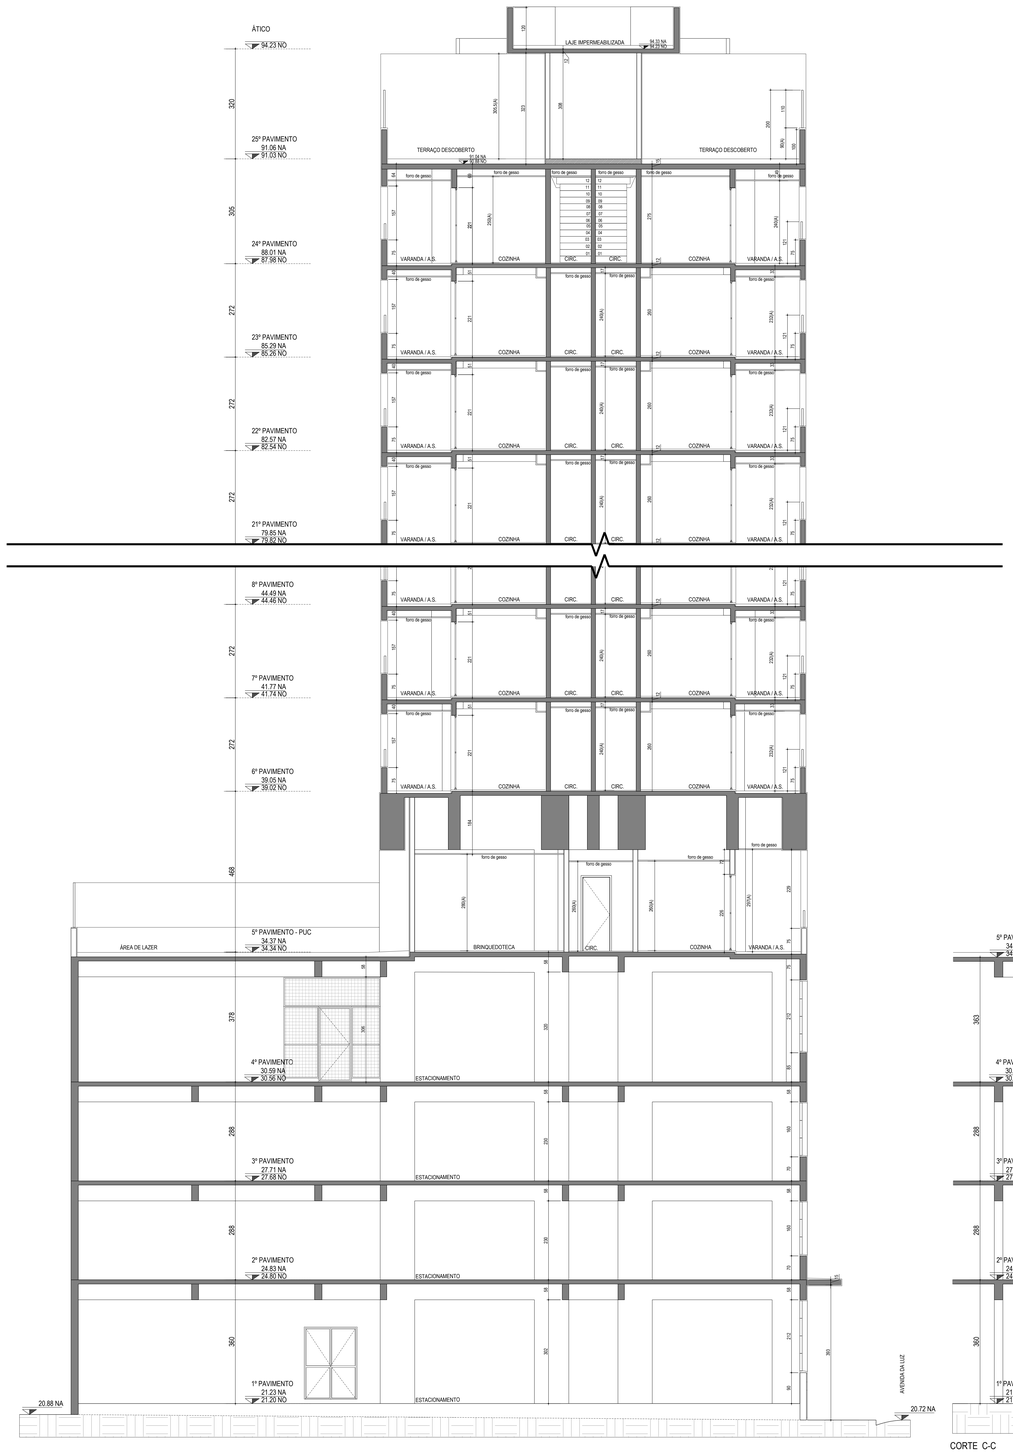


CORTE C-C

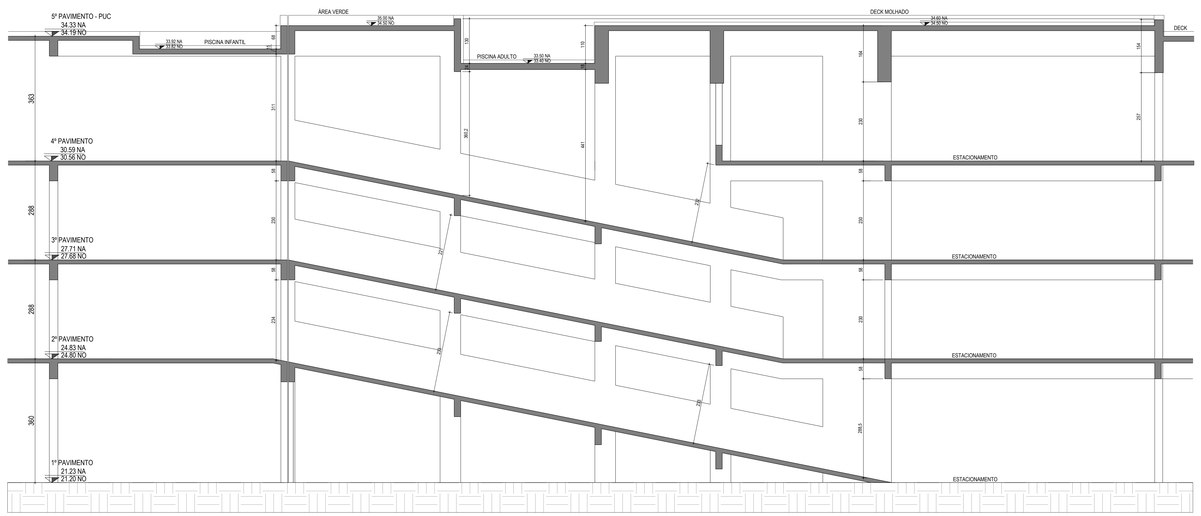

LEIS

NBR 15575:2013 - DESEMPENHO DE EDIFICAÇÕES HABITACIONAIS;
NBR 9050:2020 - ACESSIBILIDADE A EDIFICAÇÕES, MOBILIÁRIO, ESPAÇO E EQUIPAMENTOS URBANOS;
NBR 14718:2019 - GUARDA-CORPOS PARA EDIFICAÇÕES;
NBR 13103:2020 - INSTALAÇÃO DE APARELHOS A GÁS PARA USO RESIDENCIAL - REQUISITOS DOS AMBIENTES;
NBR 9077:2001 - SAÍDAS DE EMERGÊNCIA EM EDIFÍCIOS;
NBR NM 313 - ELEVADORES DE PASSAGEIROS;

VIDA ÚTIL DO PROJETO (VUP)

Conforme mínimo especificado na NBR 15575:2013 - Desempenho de edificações habitacionais

- ESTRUTURA: >= 50 anos;
- PISOS INTERNOS: >=13 anos;
- VEDAÇÃO VERTICAL EXTERNA: >= 40 anos;
- VEDAÇÃO VERTICAL INTERNA: >= 20 anos;
- COBERTURA: >=20 anos;
- HIDROSSANITÁRIO: >= 20 anos;

TRRF DAS PAREDES

a. ESCADA DE EMERGÊNCIA, SALA DE PRESSURIZAÇÃO E CASA DE BOMBAS DE INCÊNDIO DEVEM TER TRRF DE 120 min;
b. ESTRUTURAS DA EDIFICAÇÃO DEVEM TER TRRF DE 120min;
c. PAREDES ENTRE UNIDADES AUTÔNOMAS DEVEM SER COM MATERIAIS DE TRRF DE 120min;
d. AS PAREDES ENTRE AS UNIDADES E ENTRE AS UNIDADES E A ÁREA DE CIRCULAÇÃO DEVEM TER TRRF DE 60min;
e. COMPARTIMENTAÇÃO VERTICAL EXTERNA DE FACHADA COM VERGA PEITORIL DE 1,20m COM TRRF DE 120 min;

LEGENDA DETALHE DE MADEIRA

PEM - PORTA ENTRADA DE MADEIRA
PIM - PORTA INTERNA DE MADEIRA
RU - REVESTIMENTO EMBORRACHADO
PIA - PORTA INSOLANTE ACÚSTICA

NOTAS

1 - TODAS AS MEDIDAS ESTÃO EM CENTÍMETROS;
2 - VER MEMORIAL DESCRITIVO DE ACABAMENTOS;
3 - VER CADERNOS DE DETALHES;
4 - VER PAISAGISMO - VER PROJETO DE PAISAGISMO;
5 - ÁREAS SOCIAIS INTERNAS - VER PROJETO DE INTERIORES;
6 - CONSIDERAR AS MEDIDAS PARA AS VAGAS:
VAGA = 250 x 500 cm
VAGA P.C.D. = 370 x 500 cm

TABELA DE ACABAMENTOS

VER ESPECIFICAÇÃO COMPLETA DE MATERIAIS NOS CADERNOS DE DETALHES E NO MEMORIAL DE ACABAMENTOS DO CLIENTE. PARA O USO DE MATERIAIS ALTERNATIVOS, CONSULTAR COORDENADOR DE PROJETOS;

INDICAÇÃO DE NÍVEIS

+.00.00(NA) = NÍVEL ACABADO
+.00.00(NO) = NÍVEL OSSO

SINALIZAÇÃO TÁTIL

LEGENDA:

REPRESENTAÇÃO GRÁFICA

ALVENARIA
ENCHIMENTO
FORRO / SANCA
AR CONDICIONADO PREVISÃO

PLANTAS DE REFERÊNCIA PARA BASE DE PROJETO

REVISÃO	DATA	DESCRIÇÃO	RESP.
00	24/02/2023	EMISSÃO INICIAL	

INCORPORAÇÃO — CONSTRUÇÃO

JERONIMO DA VEIGA
Empreendimentos e Participações Ltda

PROJETISTA
ADESA ARQUITETURA
RUA PADRE GARCIA VELHO, 73 - C.J. 41
CEP: 05421- 030
FONE: 3032 4358 / 3032 4362

DISCIPLINA: ARQUITETURA
CÓDIGO/OBRA: DUO
FASE: LIBERADO OBRA

EMPREENDIMENTO
DUO
AV_LUZ

ASSUNTO
CORTES
B-B_E_C-C

FOLHA N.º
ARQ
115

RESPONSÁVEL	SUPERVISOR	COORDENADOR	REVISÃO
ADELINO SANTOS	ADELINO SANTOS	ALISSA LOPES	R00

PROJETISTA	ARQUIVO	ESCALA	DATA
	DUO-ARQ-LO-115-CTE-CTB-R00.dwg	1:75	24/02/2023

DIREITOS AUTORAIS RESERVADO A REPRODUÇÃO TOTAL OU PARCIAL SEM PRÉVIA AUTORIZAÇÃO, CONFORME RESOLUÇÃO Nº 67, DE 5 DE DEZEMBRO DE 2013