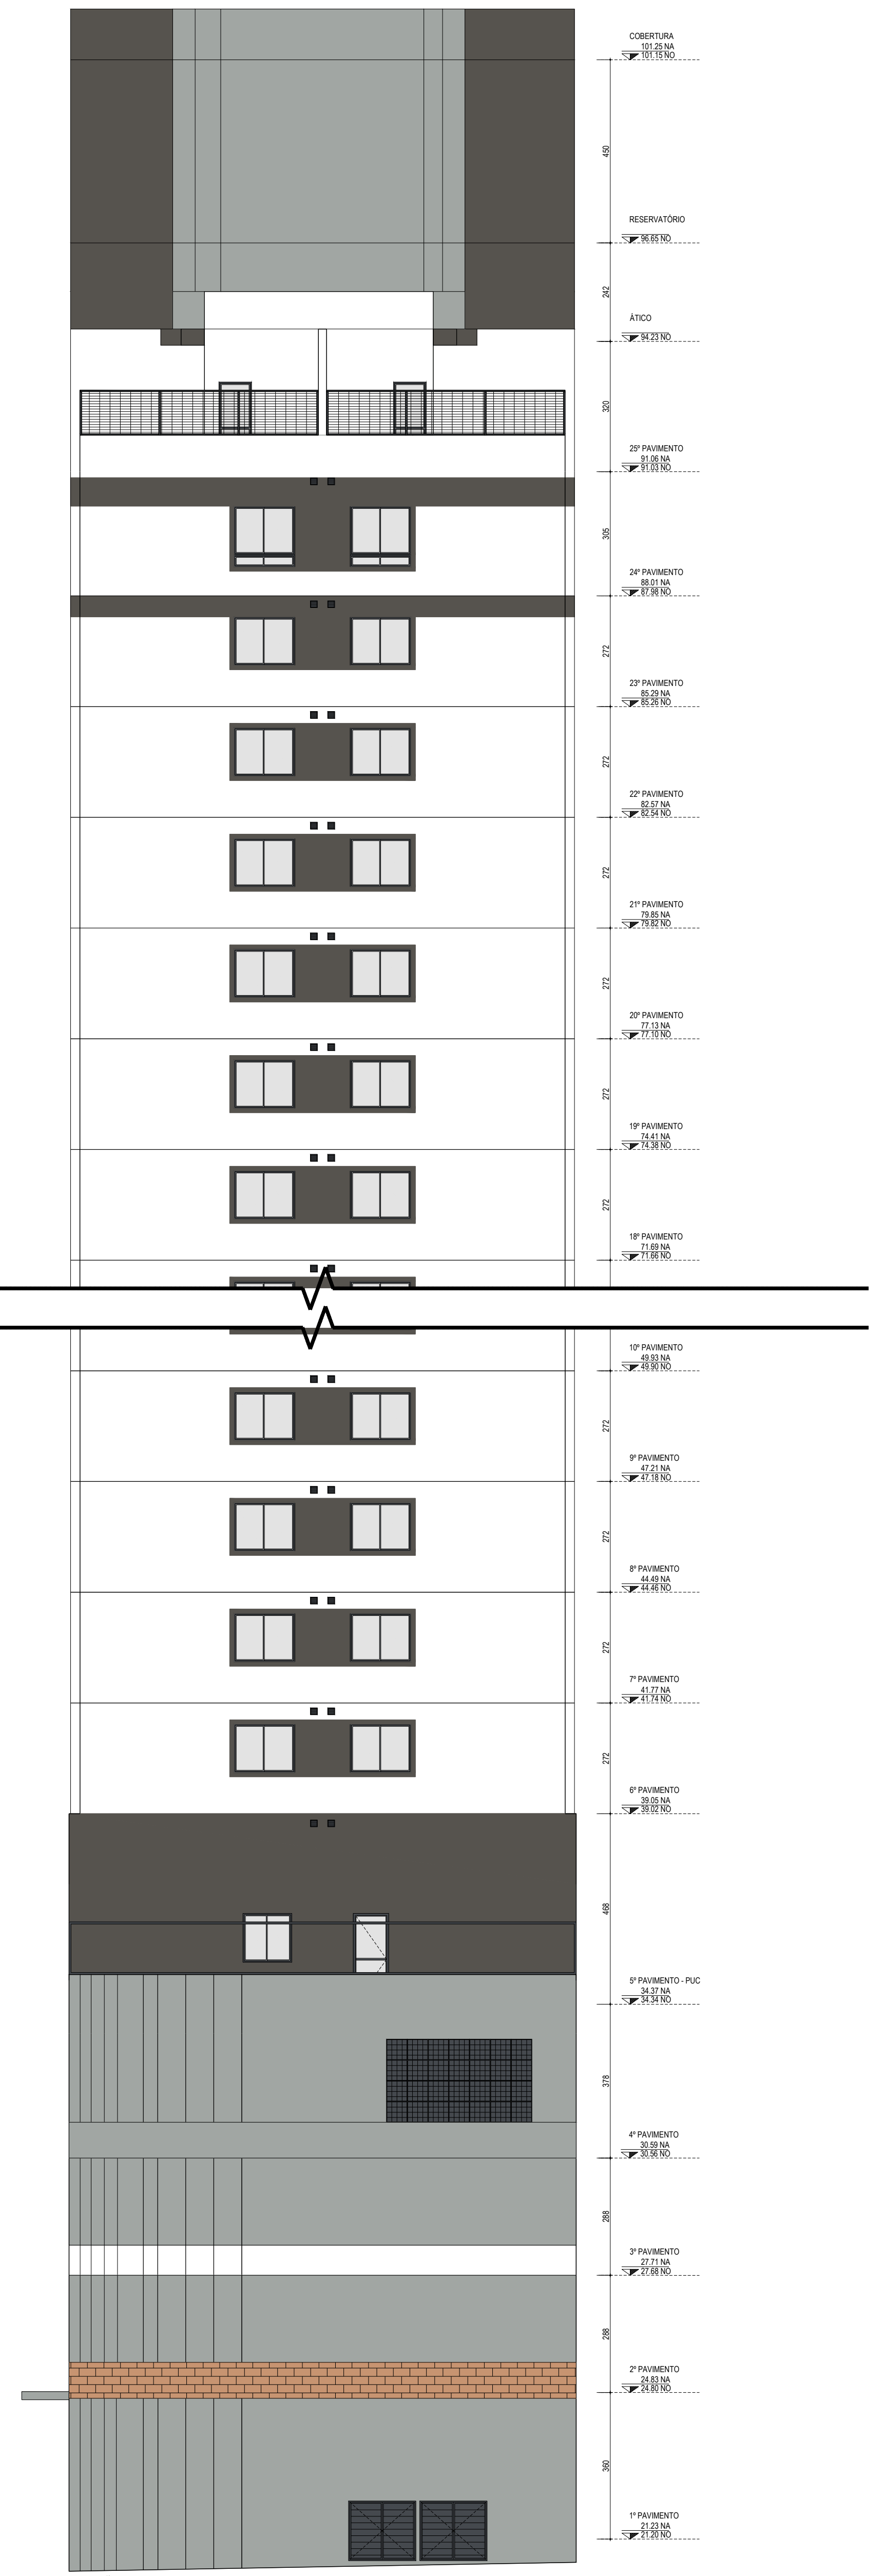
COBERTURA
101.25 NA
101.15 NO
450
RESERVATÓRIO
96.65 NO
242
ÁTICO
94.23 NO
320
25º PAVIMENTO
91.06 NA
91.03 NO
305
24º PAVIMENTO
88.01 NA
87.98 NO
272
23º PAVIMENTO
85.29 NA
85.26 NO
272
22º PAVIMENTO
82.57 NA
82.54 NO
272
21º PAVIMENTO
79.85 NA
79.82 NO
272
20º PAVIMENTO
77.13 NA
77.10 NO
272
19º PAVIMENTO
74.41 NA
74.38 NO
272
18º PAVIMENTO
71.69 NA
71.66 NO
10º PAVIMENTO
49.93 NA
49.90 NO
272
9º PAVIMENTO
47.21 NA
47.18 NO
272
8º PAVIMENTO
44.49 NA
44.46 NO
272
7º PAVIMENTO
41.77 NA
41.74 NO
272
6º PAVIMENTO
39.05 NA
39.02 NO
468
5º PAVIMENTO - PUC
34.37 NA
34.34 NO
378
4º PAVIMENTO
30.59 NA
30.56 NO
288
3º PAVIMENTO
27.71 NA
27.68 NO
288
2º PAVIMENTO
24.83 NA
24.80 NO
360
1º PAVIMENTO
21.23 NA
21.20 NO

ELEVAÇÃO 2

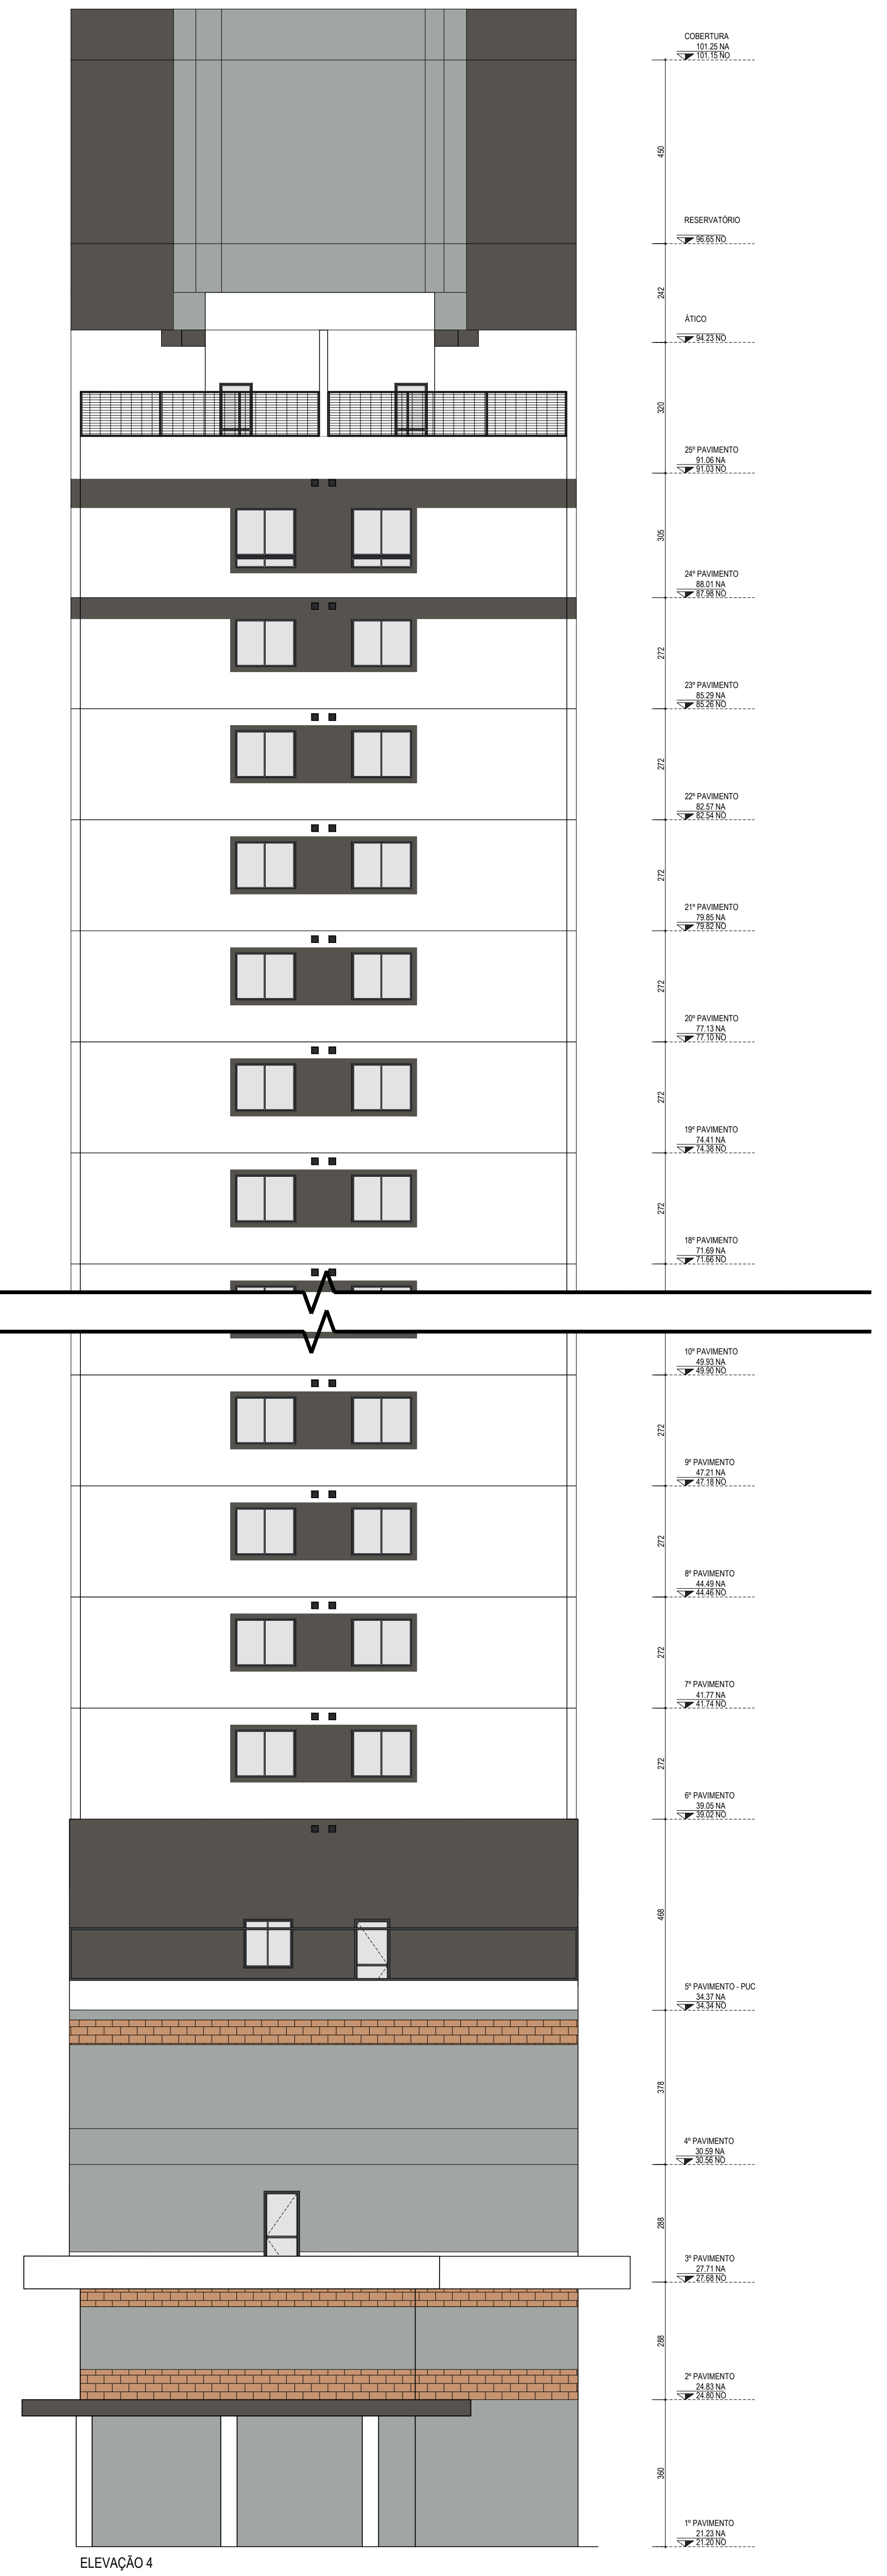
COBERTURA
101.25 NA
101.15 NO
450
RESERVATÓRIO
96.65 NO
242
ÁTICO
94.23 NO
320
25º PAVIMENTO
91.06 NA
91.03 NO
305
24º PAVIMENTO
88.01 NA
87.98 NO
272
23º PAVIMENTO
85.29 NA
85.26 NO
272
22º PAVIMENTO
82.57 NA
82.54 NO
272
21º PAVIMENTO
79.85 NA
79.82 NO
272
20º PAVIMENTO
77.13 NA
77.10 NO
272
19º PAVIMENTO
74.41 NA
74.38 NO
272
18º PAVIMENTO
71.69 NA
71.66 NO
10º PAVIMENTO
49.93 NA
49.90 NO
272
9º PAVIMENTO
47.21 NA
47.18 NO
272
8º PAVIMENTO
44.49 NA
44.46 NO
272
7º PAVIMENTO
41.77 NA
41.74 NO
272
6º PAVIMENTO
39.05 NA
39.02 NO
468
5º PAVIMENTO - PUC
34.37 NA
34.34 NO
378
4º PAVIMENTO
30.59 NA
30.56 NO
288
3º PAVIMENTO
27.71 NA
27.68 NO
288
2º PAVIMENTO
24.83 NA
24.80 NO
360
1º PAVIMENTO
21.23 NA
21.20 NO

ELEVAÇÃO 4

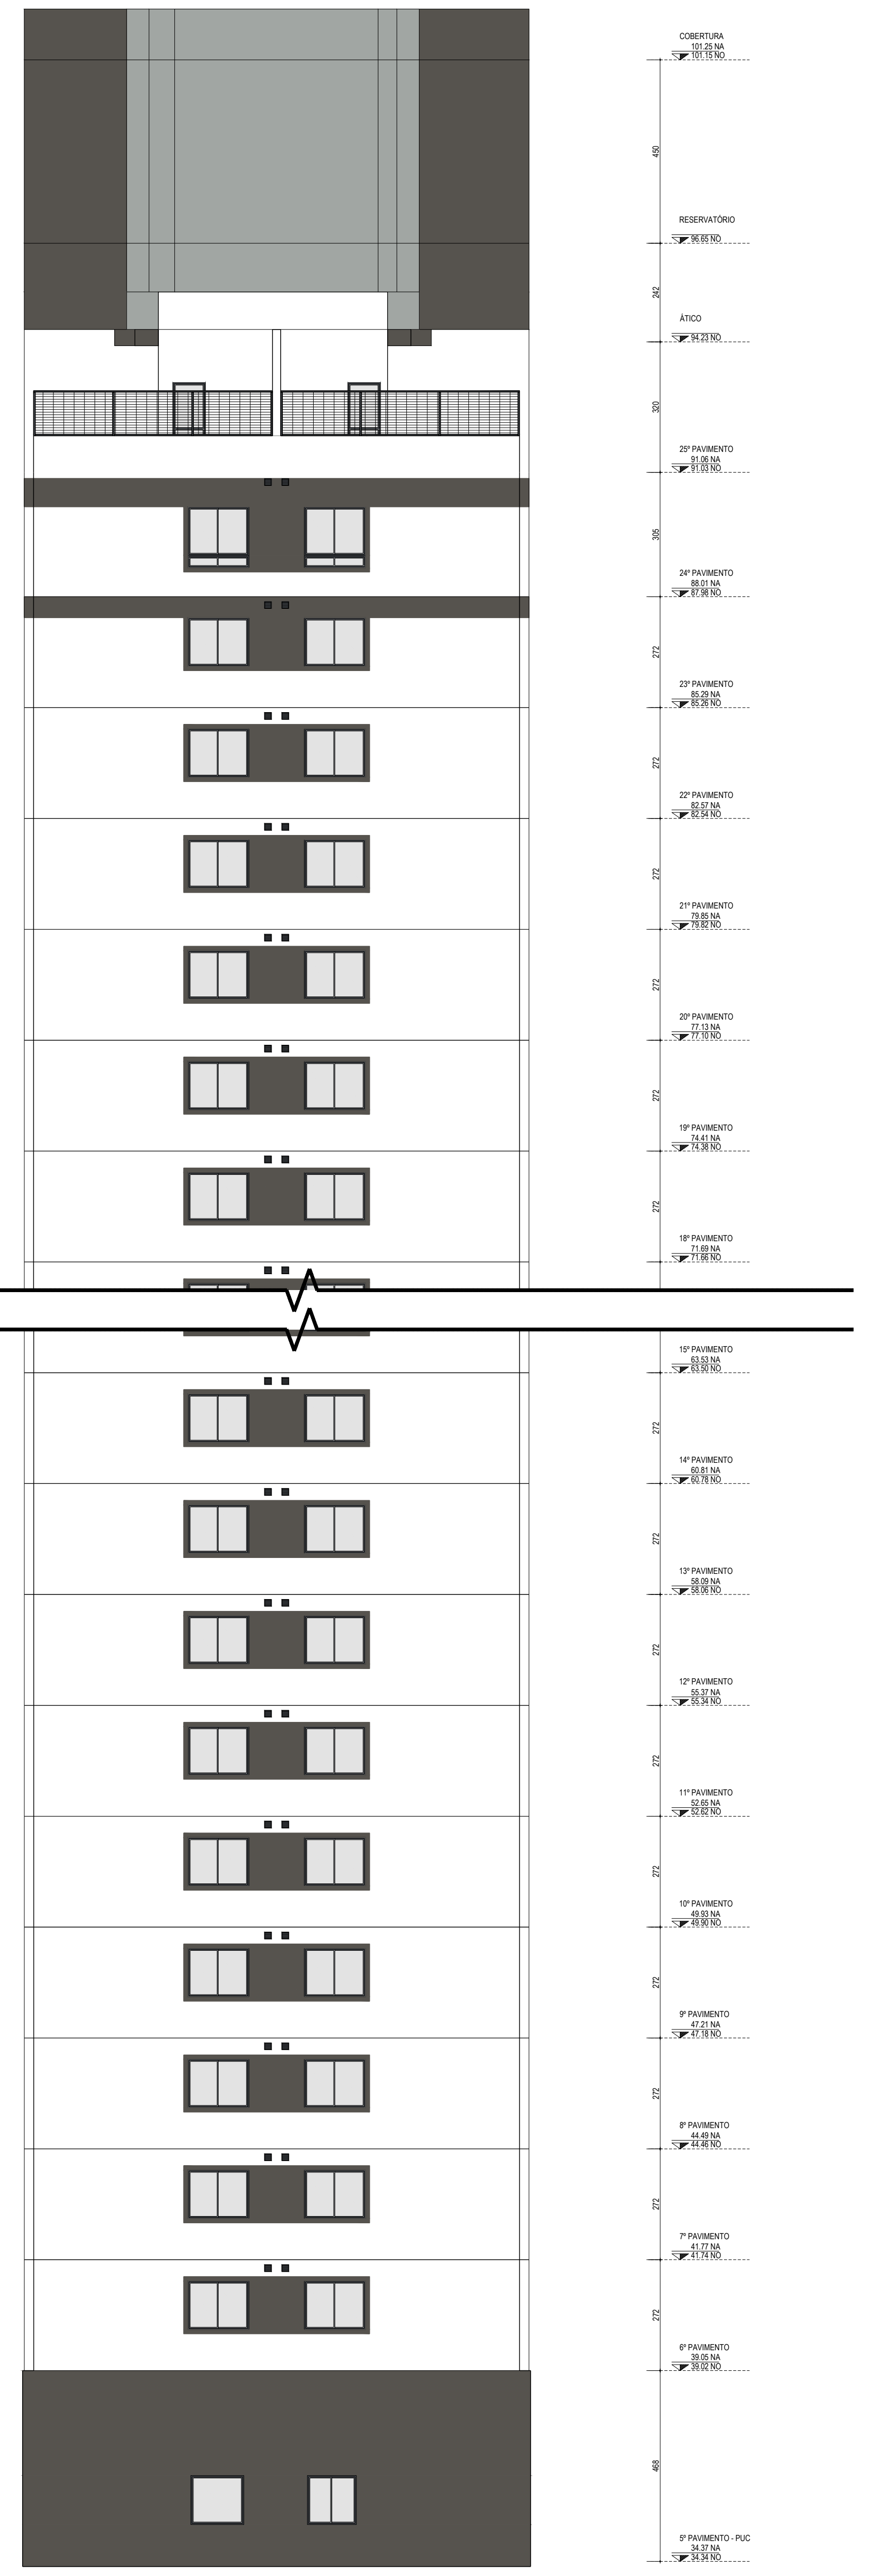
COBERTURA
101.25 NA
101.15 NO
450
RESERVATÓRIO
96.65 NO
242
ÁTICO
94.23 NO
320
25º PAVIMENTO
91.06 NA
91.03 NO
305
24º PAVIMENTO
88.01 NA
87.98 NO
272
23º PAVIMENTO
85.29 NA
85.26 NO
272
22º PAVIMENTO
82.57 NA
82.54 NO
272
21º PAVIMENTO
79.85 NA
79.82 NO
272
20º PAVIMENTO
77.13 NA
77.10 NO
272
19º PAVIMENTO
74.41 NA
74.38 NO
272
18º PAVIMENTO
71.69 NA
71.66 NO
15º PAVIMENTO
63.53 NA
63.50 NO
272
14º PAVIMENTO
60.81 NA
60.78 NO
272
13º PAVIMENTO
58.09 NA
58.06 NO
272
12º PAVIMENTO
55.37 NA
55.34 NO
272
11º PAVIMENTO
52.65 NA
52.62 NO
272
10º PAVIMENTO
49.93 NA
49.90 NO
272
9º PAVIMENTO
47.21 NA
47.18 NO
272
8º PAVIMENTO
44.49 NA
44.46 NO
272
7º PAVIMENTO
41.77 NA
41.74 NO
272
6º PAVIMENTO
39.05 NA
39.02 NO
468
5º PAVIMENTO - PUC
34.37 NA
34.34 NO

ELEVAÇÃO 5

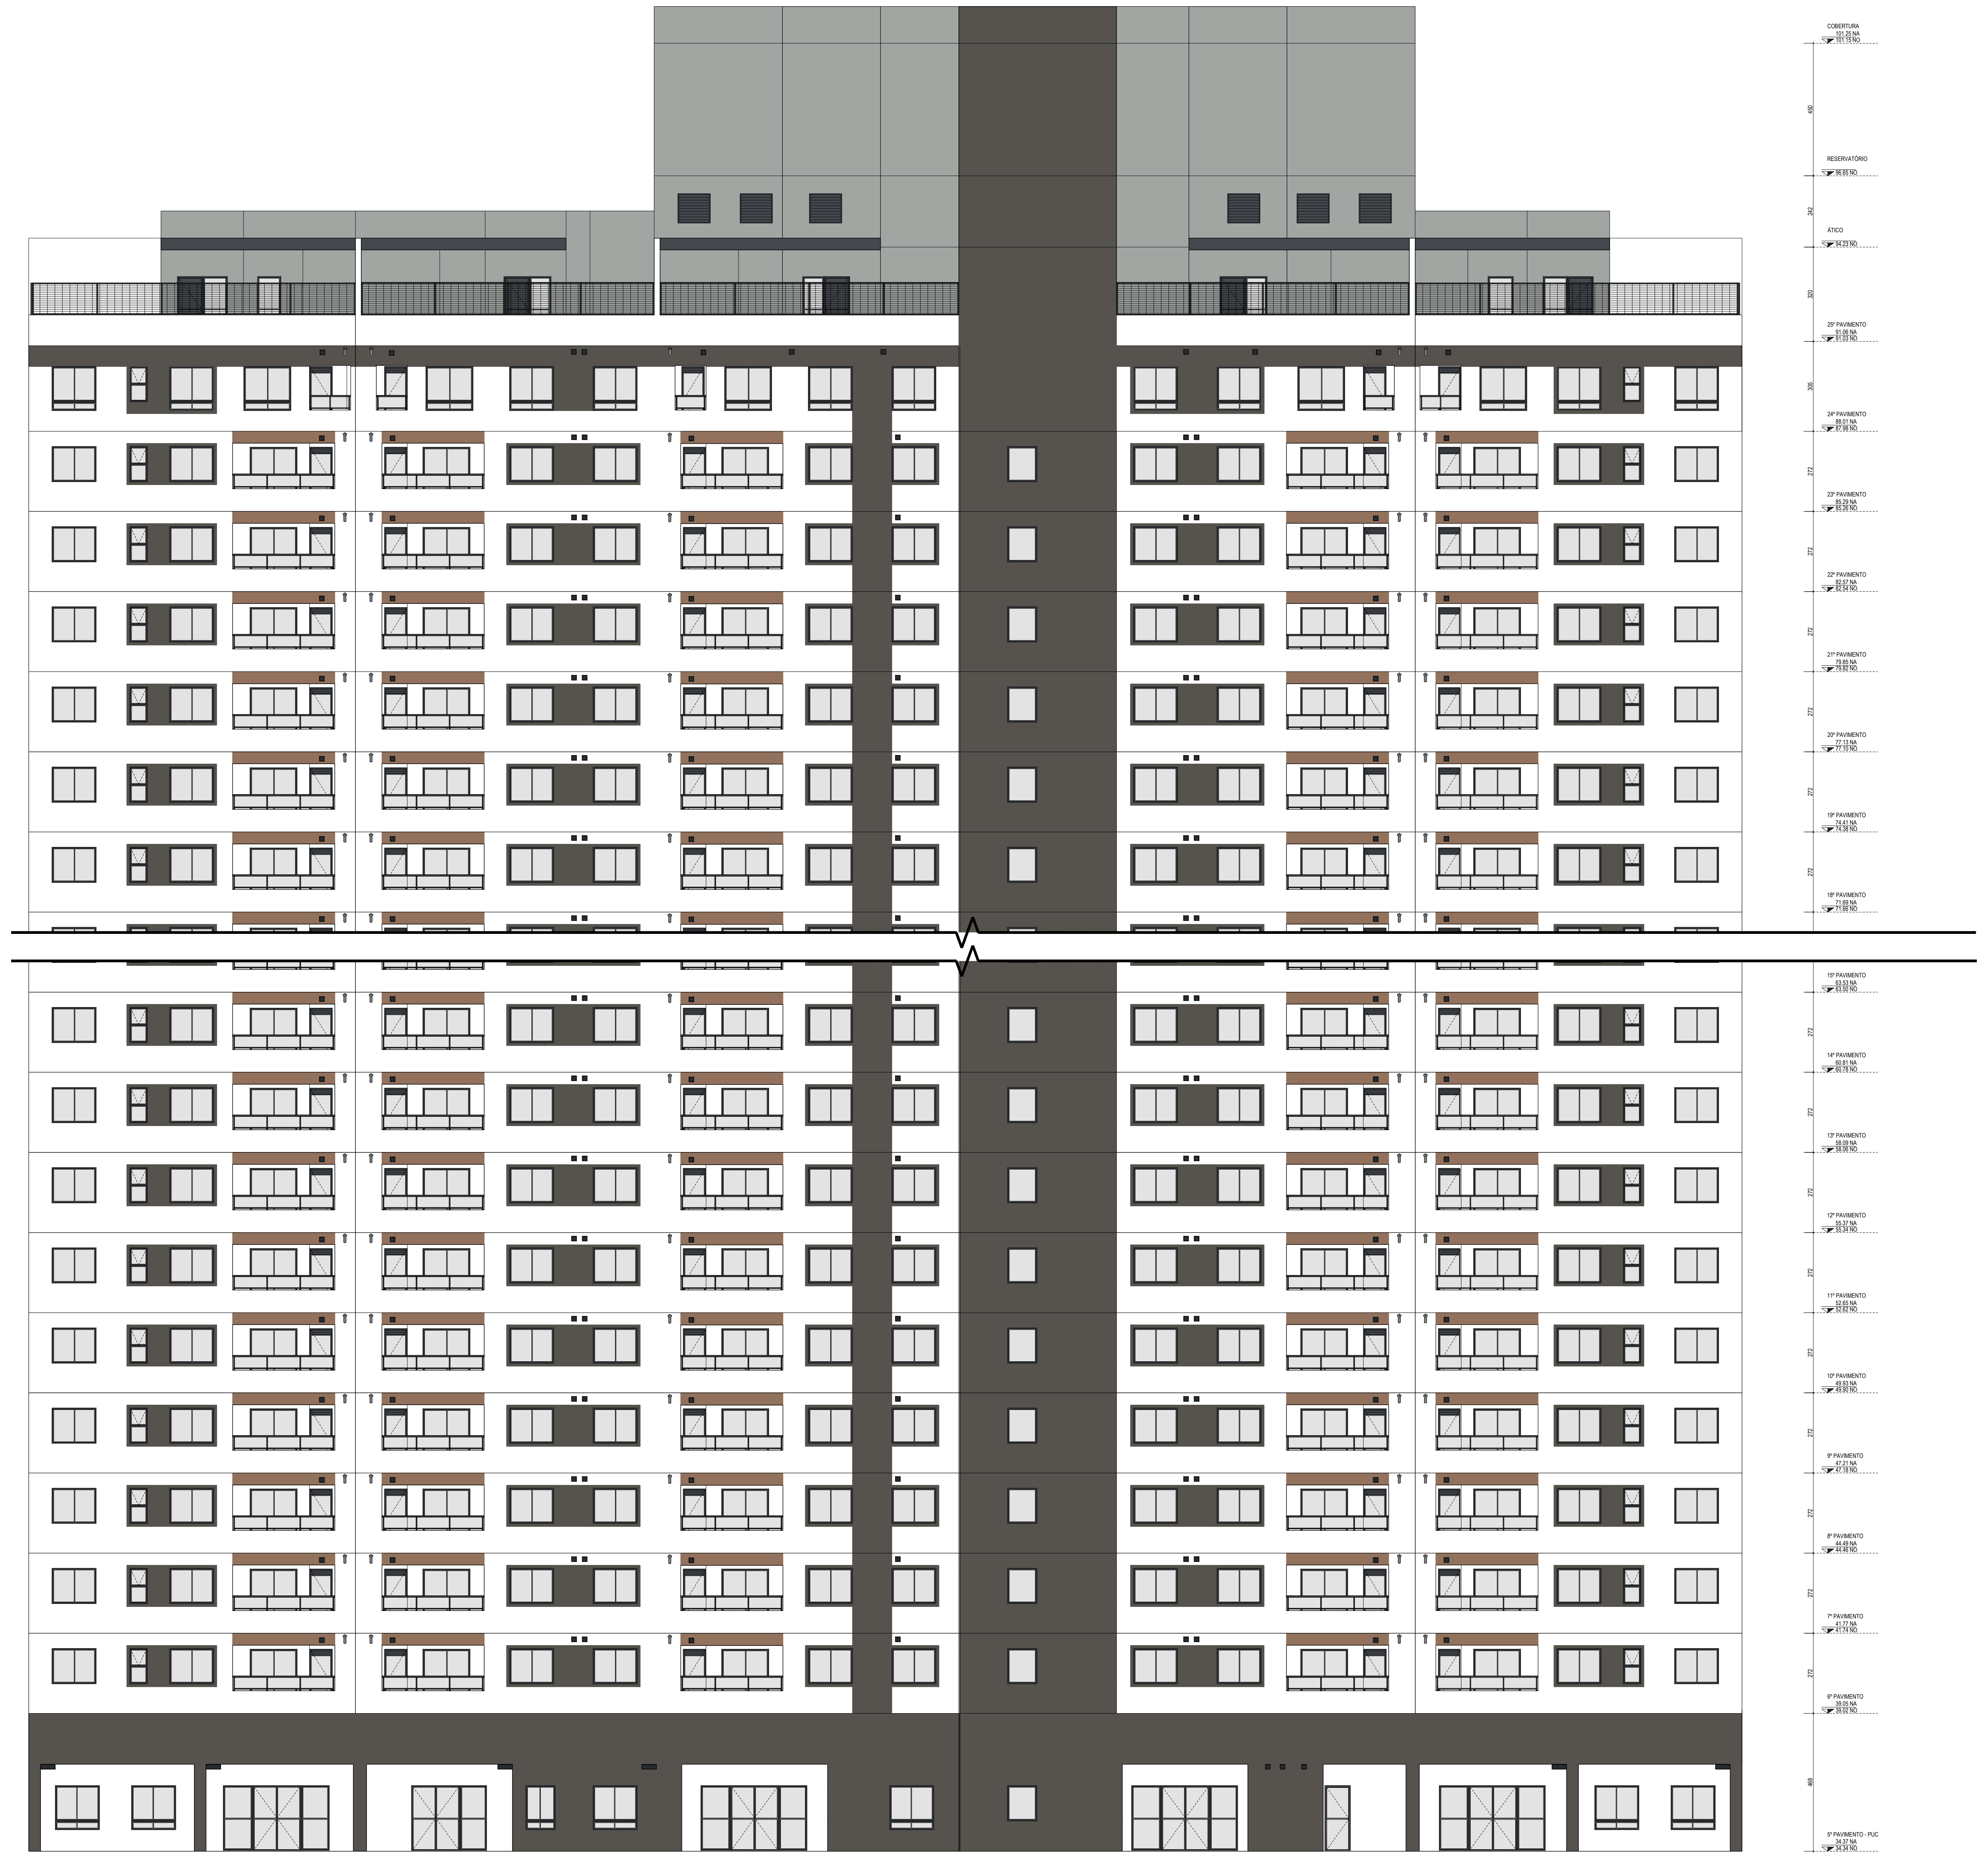
COBERTURA
101.25 NA
101.15 NO
450
RESERVATÓRIO
96.65 NO
242
ÁTICO
94.23 NO
320
25º PAVIMENTO
91.06 NA
91.03 NO
305
24º PAVIMENTO
88.01 NA
87.98 NO
272
23º PAVIMENTO
85.29 NA
85.26 NO
272
22º PAVIMENTO
82.57 NA
82.54 NO
272
21º PAVIMENTO
79.85 NA
79.82 NO
272
20º PAVIMENTO
77.13 NA
77.10 NO
272
19º PAVIMENTO
74.41 NA
74.38 NO
272
18º PAVIMENTO
71.69 NA
71.66 NO
15º PAVIMENTO
63.53 NA
63.50 NO
272
14º PAVIMENTO
60.81 NA
60.78 NO
272
13º PAVIMENTO
58.09 NA
58.06 NO
272
12º PAVIMENTO
55.37 NA
55.34 NO
272
11º PAVIMENTO
52.65 NA
52.62 NO
272
10º PAVIMENTO
49.93 NA
49.90 NO
272
9º PAVIMENTO
47.21 NA
47.18 NO
272
8º PAVIMENTO
44.49 NA
44.46 NO
272
7º PAVIMENTO
41.77 NA
41.74 NO
272
6º PAVIMENTO
39.05 NA
39.02 NO
468
5º PAVIMENTO - PUC
34.37 NA
34.34 NO

ELEVAÇÃO 6

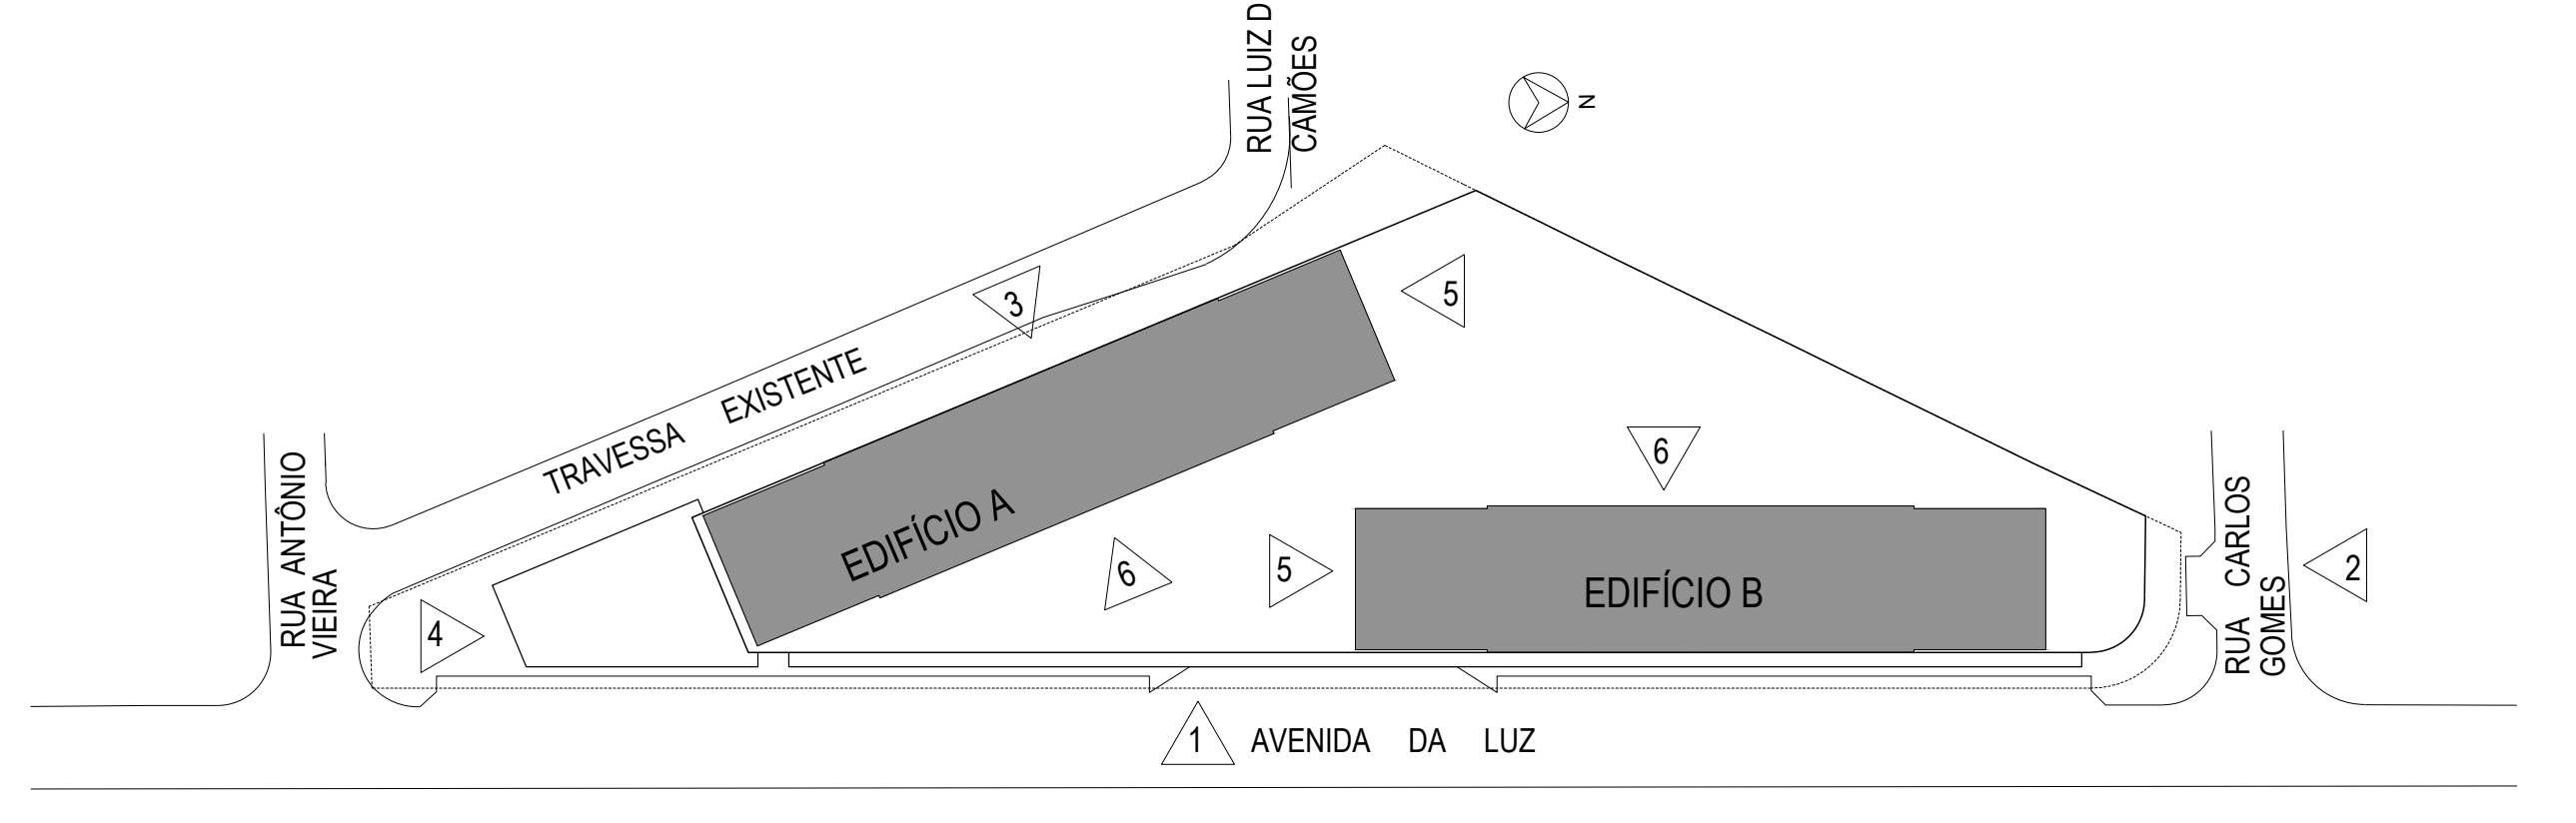
RUA LUIZ DE CAMÕES
N
TRAVESSA EXISTENTE
3
5
EDIFÍCIO A
6
5
6
EDIFÍCIO B
RUA ANTÔNIO VIEIRA
4
RUA CARLOS GOMES
2
1
AVENIDA DA LUZ

IMPLANTAÇÃO
esc.: 1:500

LEGENDA

- ■ Cinza fechado (Ref. P750) - SUVINIL
- ■ Platina (Ref. RM039) - SUVINIL
- ■ Castanha do Pará (Ref. E172) - SUVINIL
- □ Petúnia Branca (Ref. A207) - SUVINIL
- ▦ A SER DEFINIDO

LEIS

NBR 15575:2013 - DESEMPENHO DE EDIFICAÇÕES HABITACIONAIS;
NBR 9050:2020 - ACESSIBILIDADE A EDIFICAÇÕES, MOBILIÁRIO, ESPAÇO E EQUIPAMENTOS URBANOS;
NBR 14718:2019 - GUARDA-CORPOS PARA EDIFICAÇÕES;
NBR 13103:2020 - INSTALAÇÃO DE APARELHOS A GÁS PARA USO RESIDENCIAL - REQUISITOS DOS AMBIENTES;
NBR 9077:2001 - SAÍDAS DE EMERGÊNCIA EM EDIFÍCIOS;
NBR NM 313 - ELEVADORES DE PASSAGEIROS;

VIDA ÚTIL DO PROJETO (VUP)

Conforme mínimo especificado na NBR 15575:2013- Desempenho de edificações habitacionais

- ESTRUTURA: >/ 50 anos;
- PISOS INTERNOS: >/ 13 anos;
- VEDAÇÃO VERTICAL EXTERNA: >/ 40 anos;
- VEDAÇÃO VERTICAL INTERNA: >/ 20 anos;
- COBERTURA: >/ 20 anos;
- HIDROSSANITÁRIO: >/ 20 anos;

TRRF DAS PAREDES

a. ESCADA DE EMERGÊNCIA, SALA DE PRESSURIZAÇÃO E CASA DE BOMBAS DE INCÊNDIO DEVEM TER TRRF DE 120 min;
b. ESTRUTURAS DA EDIFICAÇÃO DEVEM TER TRRF DE 120min;
c. ABERTURAS ENTRE LAJES (SHAFTS) DEVEM TER VEDAÇÃO COM MATERIAIS DE TRRF DE 120min;
d. AS PAREDES ENTRE AS UNIDADES E ENTRE AS UNIDADES E A ÁREA DE CIRCULAÇÃO DEVEM TER TRRF DE 60min;
e. COMPARTIMENTAÇÃO VERTICAL EXTERNA DE FACHADA COM VERGA-PEITORIL DE 1,20m COM TRRF DE 120 min;

LEGENDA DETALHE DE MADEIRA

PEM - PORTA ENTRADA DE MADEIRA
PIM - PORTA INTERNA DE MADEIRA
RU - RESISTENTE À UMIDADE
PIA - PORTA INSOLANTE ACÚSTICA

NOTAS

1 - TODAS AS MEDIDAS ESTÃO EM CENTÍMETROS.
2 - VER MEMORIAL DESCRITIVO DE ACABAMENTOS.
3 - VER CADERNOS DE DETALHES.
4 - ÁREAS EXTERNAS - VER PROJETO DE PAISAGISMO.
5 - ÁREAS SOCIAIS INTERNAS - VER PROJETO DE INTERIORES.
6 - CONSIDERAR AS MEDIDAS PARA AS VAGAS:
. VAGA = 250 x 500 cm
. VAGA P.C.D. = 370 x 500 cm

TABELA DE ACABAMENTOS

VER ESPECIFICAÇÃO COMPLETA DE MATERIAIS NOS CADERNOS DE DETALHES E NO MEMORIAL DE ACABAMENTOS DO CLIENTE. PARA O USO DE MATERIAIS SIMILARES CONSULTAR O COORDENADOR DE PROJETOS.

INDICAÇÃO DE NÍVEIS

00.00(NA) → NÍVEL ACABADO
00.00(NO) → NÍVEL OSSO

▨ - SINALIZAÇÃO TÁTIL

LEGENDA:

REPRESENTAÇÃO GRÁFICA

- □ ALVENARIA
- ▨ ENCHIMENTO
- ■ FORRO / SANCA
- 🟦 AR CONDICIONADO PREVISÃO

PLANTAS DE REFERÊNCIA PARA BASE DE PROJETO

REVISÃO	DATA	DESCRIÇÃO	RESP.
00	24/02/2023	EMISSÃO INICIAL	

INCORPORAÇÃO
JERONIMO DA VEIGA
Empreendimentos e Participações Ltda.

CONSTRUÇÃO

PROJETISTA
ADESA ARQUITETURA
RUA PADRE GARCIA VELHO, 73 - CJ. 41
CEP: 05421- 030
FONE: 3032 4355 / 3032 4362

DISCIPLINA
ARQUITETURA

CÓDIGO/OBRA
DUO

FASE
LIBERADO OBRA

EMPREENDIMENTO
DUO
AV_LUZ

ASSUNTO
ELEVAÇÕES
2_4_5_6

FOLHA N.º
ARQ
117

RESPONSÁVEL
ADELINO SANTOS

SUPERVISOR
ADELINO SANTOS

COORDENADOR
ALISSA LOPES

REVISÃO
R00

PROJETISTA

ARQUIVO
DUO-ARQ-LO-117-ELV-GER-R00.dwg

ESCALA
1:75

DATA
24/02/2023

DIREITOS AUTORAIS RESERVADO A REPRODUÇÃO TOTAL OU PARCIAL SEM PRÉVIA AUTORIZAÇÃO, CONFORME RESOLUÇÃO N° 67, DE 5 DE DEZEMBRO DE 2013