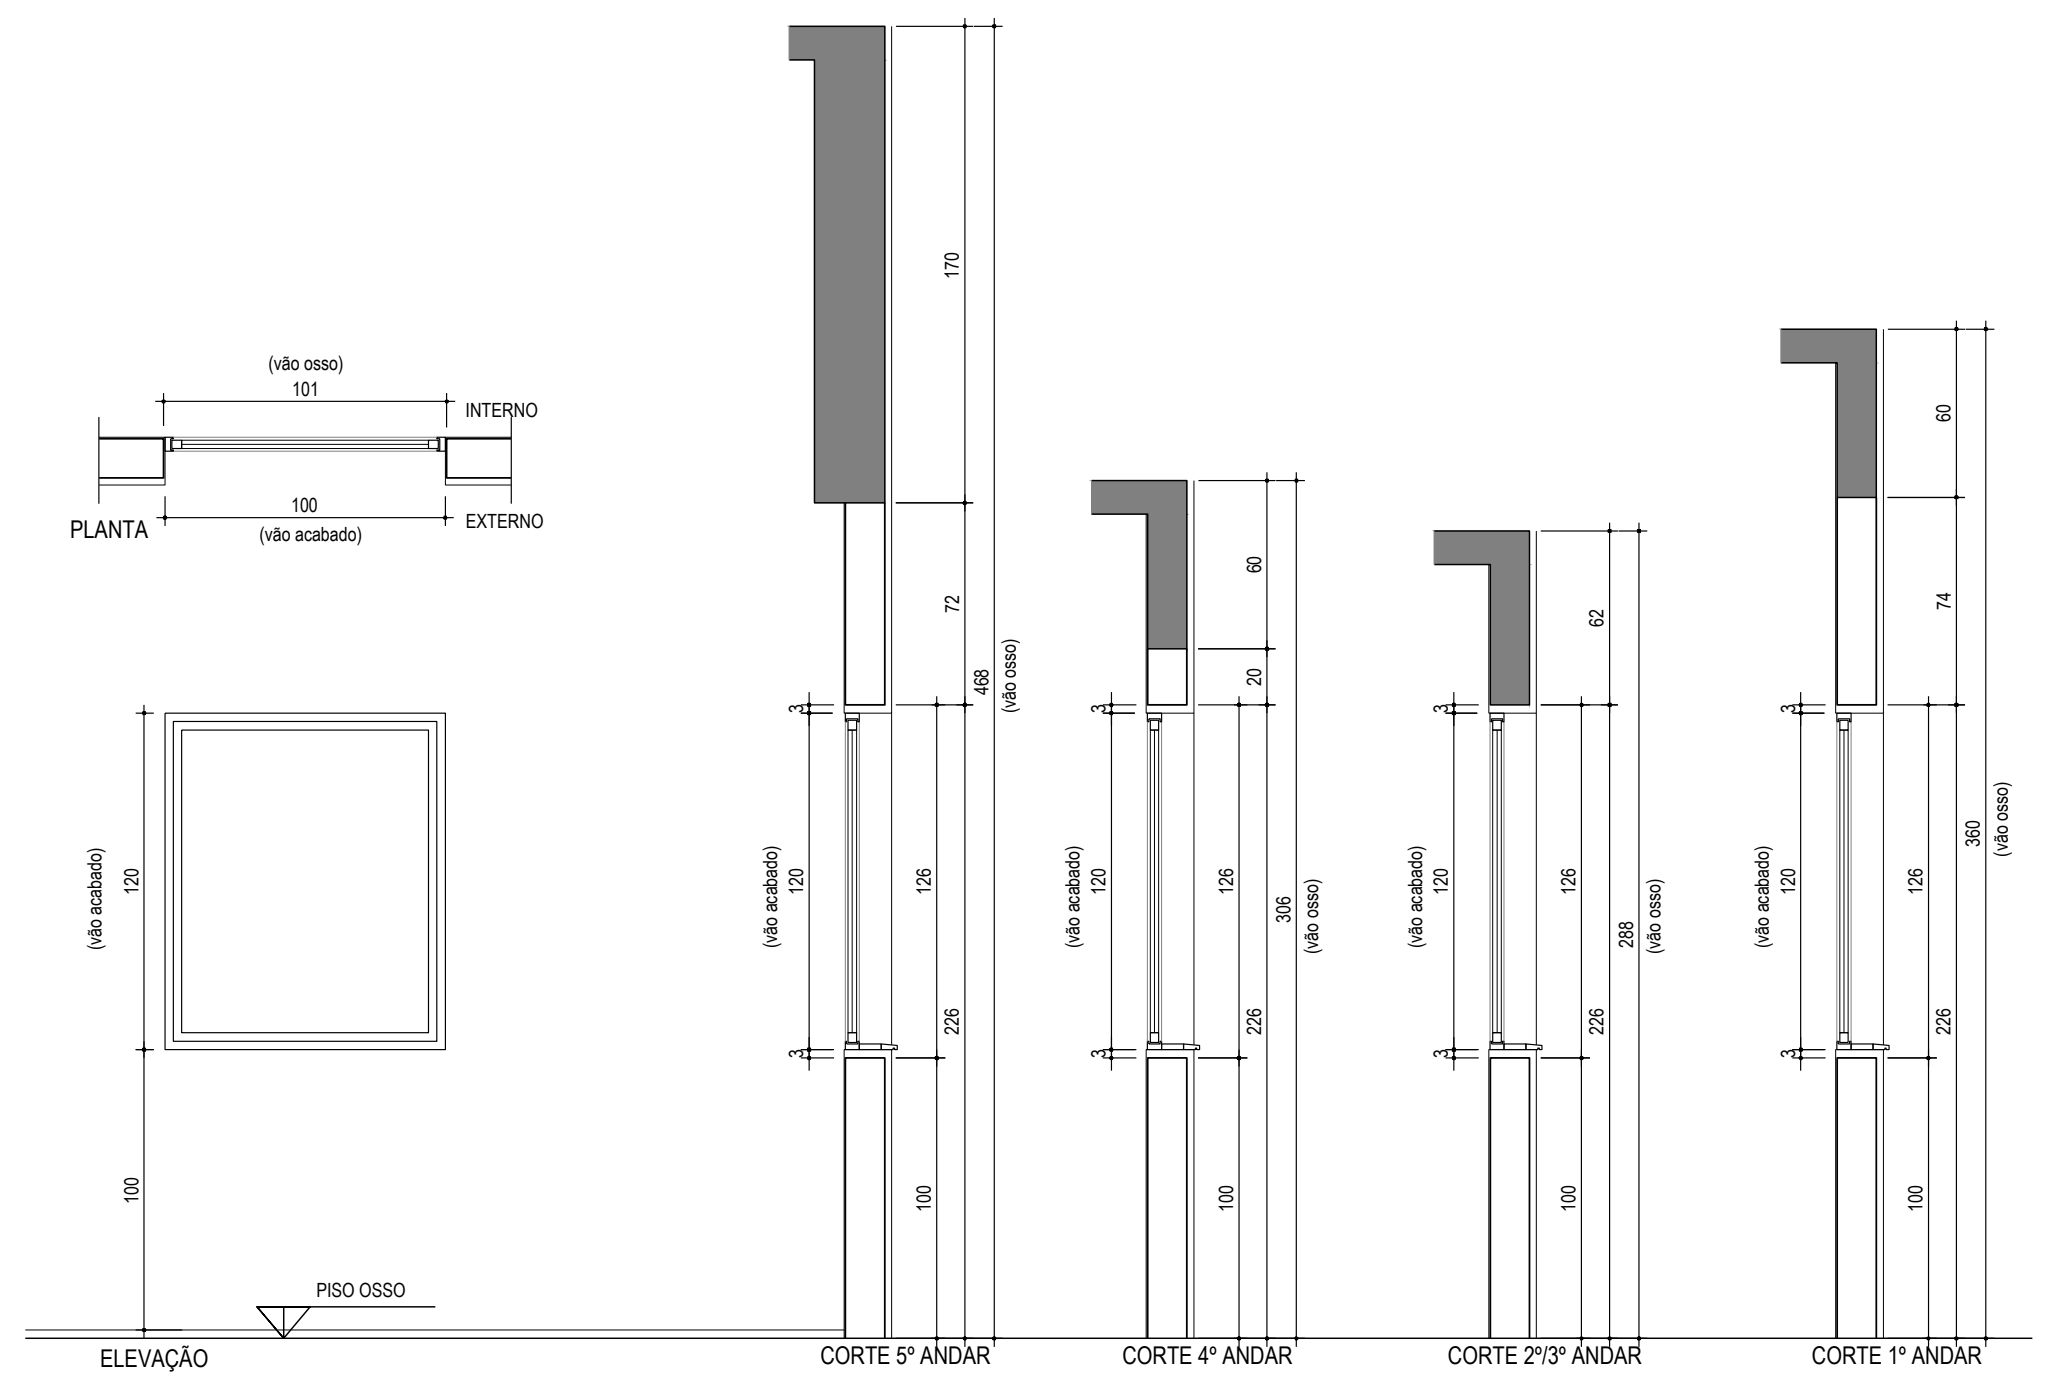
PLANTA
INTERNO
EXTERNO
ELEVAÇÃO
PISO OSSO
CORTE 5º ANDAR
CORTE 4º ANDAR
CORTE 2º/3º ANDAR
CORTE 1º ANDAR

AL 22		AMBIENTE	PAVIMENTO	QUANT.
TIPO:	CAIXILHO FIXO	ELEVADOR	5º ANDAR A / B	1 x 2 = 2
MATERIAL:	ALUMÍNIO	ELEVADOR	4º ANDAR	2
ACABAM.:	PINTURA ELETROSTÁTICA	ELEVADOR	3º ANDAR	2
COR:	GRAFITE - RAL 7024	ELEVADOR	2º ANDAR	2
VIDRO:	LISO E INCOLOR	ELEVADOR	1º ANDAR	2
OBSERVAÇÃO:	-		TOTAL	10

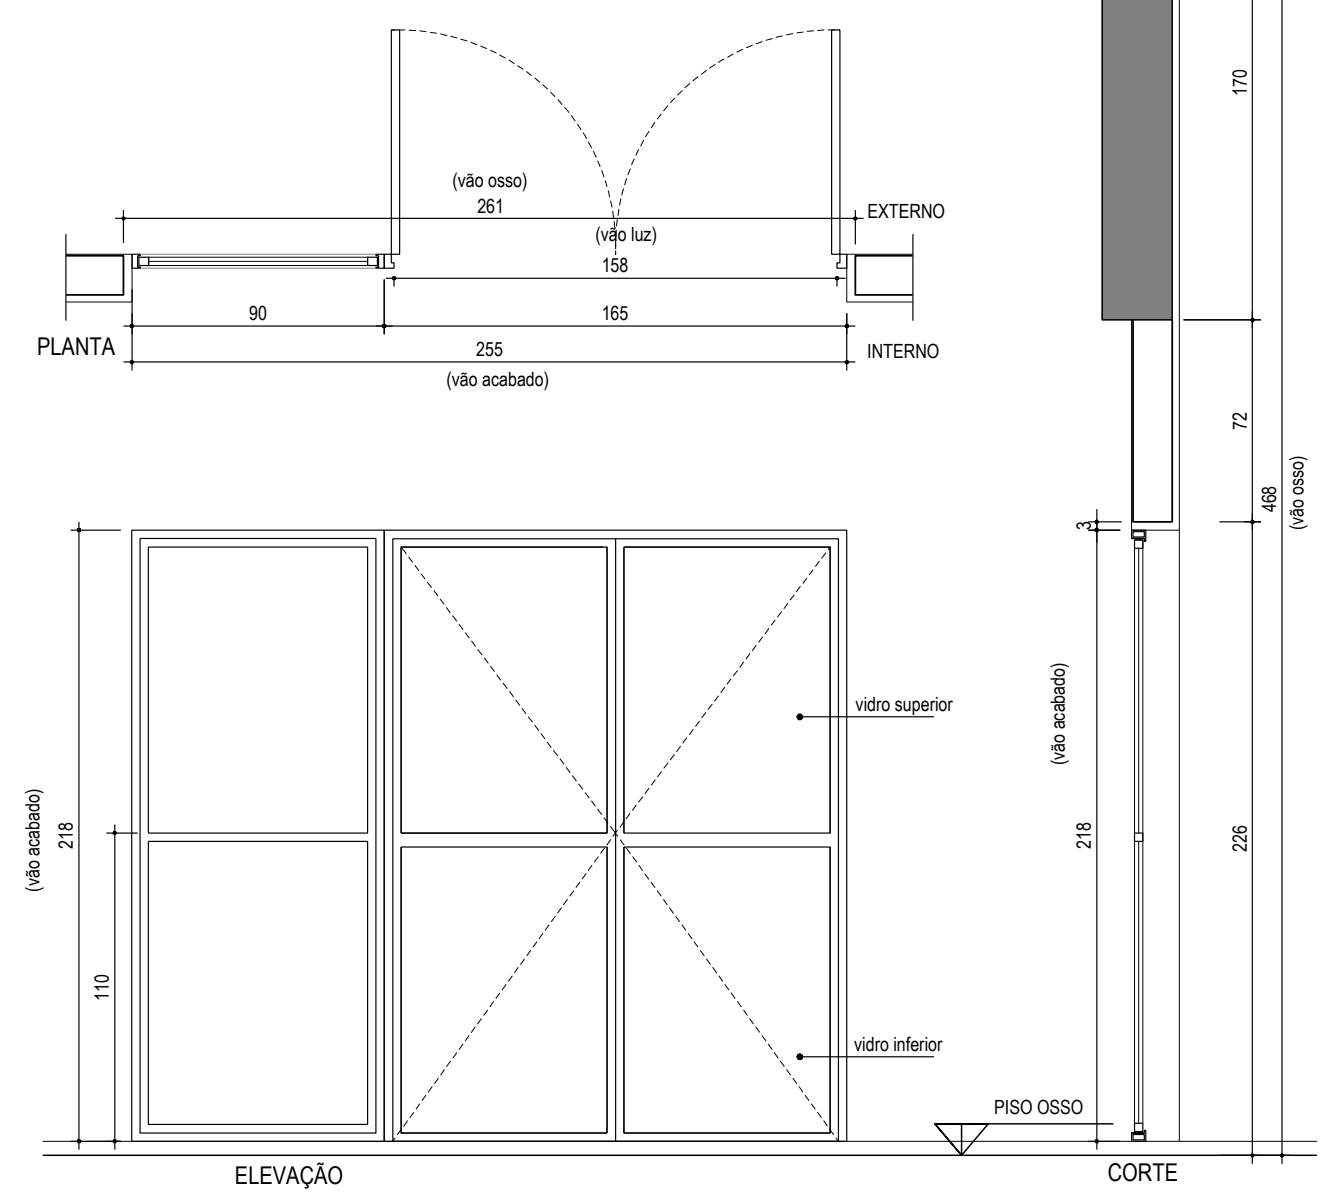
PLANTA
INTERNO
EXTERNO
vidro superior
vidro inferior
ELEVAÇÃO
PISO OSSO
CORTE

AL 23		AMBIENTE	PAVIMENTO	QUANT.
TIPO:	02 FOLHAS DE ABRIR + 01 FOLHA FIXA	LAZER	5º ANDAR A / B	1 x 2 = 2
MATERIAL:	ALUMÍNIO			
ACABAM.:	PINTURA ELETROSTÁTICA			
COR:	GRAFITE - RAL 7024			
VIDRO:	SUPERIOR - LISO E INCOLOR INFERIOR - INCOLOR LAMINADO OU TEMPERADO			
OBSERVAÇÃO:	-		TOTAL	2

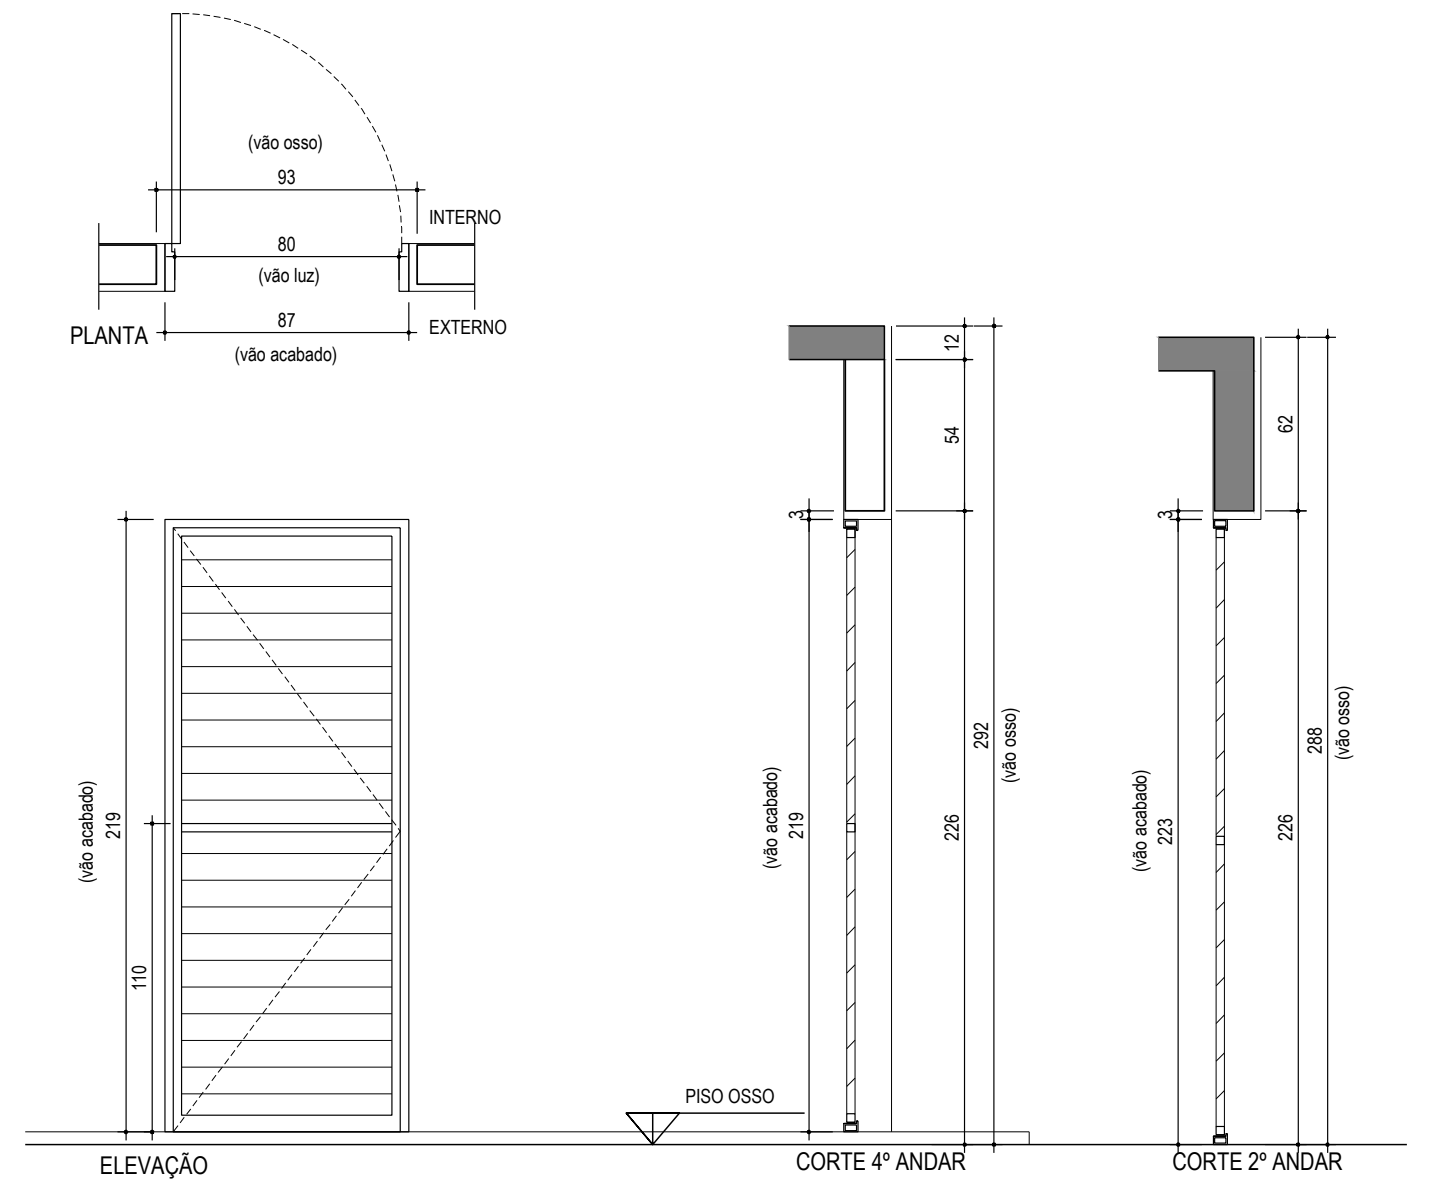
PLANTA
INTERNO
EXTERNO
ELEVAÇÃO
PISO OSSO
CORTE 4º ANDAR
CORTE 2º ANDAR

AL 24		AMBIENTE	PAVIMENTO	QUANT.
TIPO:	01 FOLHA DE ABRIR	DEPÓSITOS / COPA	4º ANDAR	3
MATERIAL:	ALUMÍNIO	DEPÓSITO/MEDID.	2º ANDAR	2
ACABAM.:	PINTURA ELETROSTÁTICA	LIXO / ACESSO	1º ANDAR	3
COR:	GRAFITE - RAL 7024	BARRILETE	ÁTICO A / B	1 x 2 = 2
VIDRO:	-			
OBSERVAÇÃO:	COM VENTILAÇÃO PERMANENTE		TOTAL	10

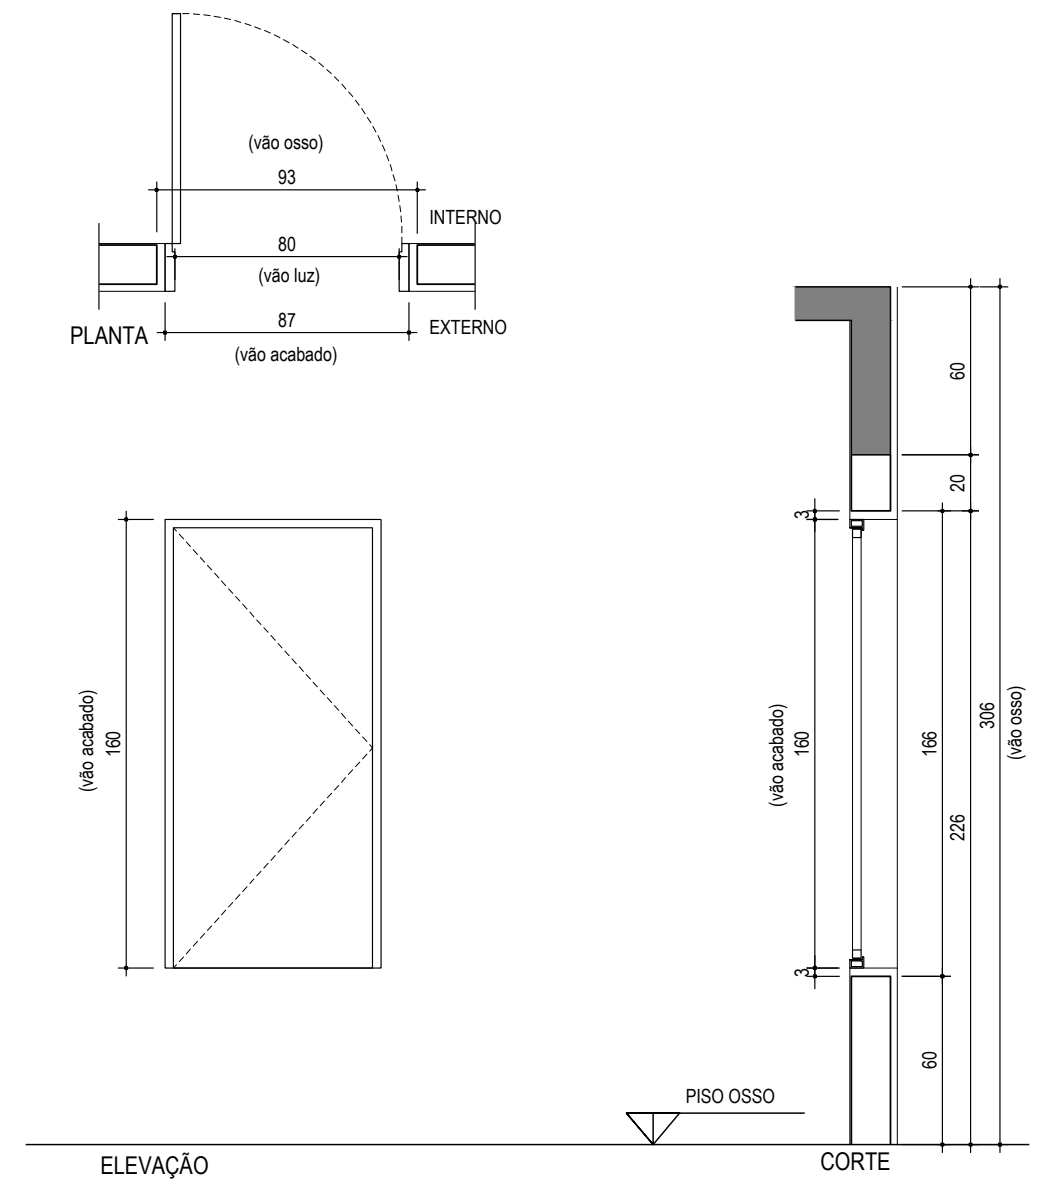
PLANTA
INTERNO
EXTERNO
ELEVAÇÃO
PISO OSSO
CORTE

AL 25		AMBIENTE	PAVIMENTO	QUANT.
TIPO:	01 FOLHA DE ABRIR	LAJE VERDE	4º ANDAR	1
MATERIAL:	ALUMÍNIO			
ACABAM.:	PINTURA ELETROSTÁTICA			
COR:	GRAFITE - RAL 7024			
VIDRO:	-			
OBSERVAÇÃO:	-		TOTAL	1

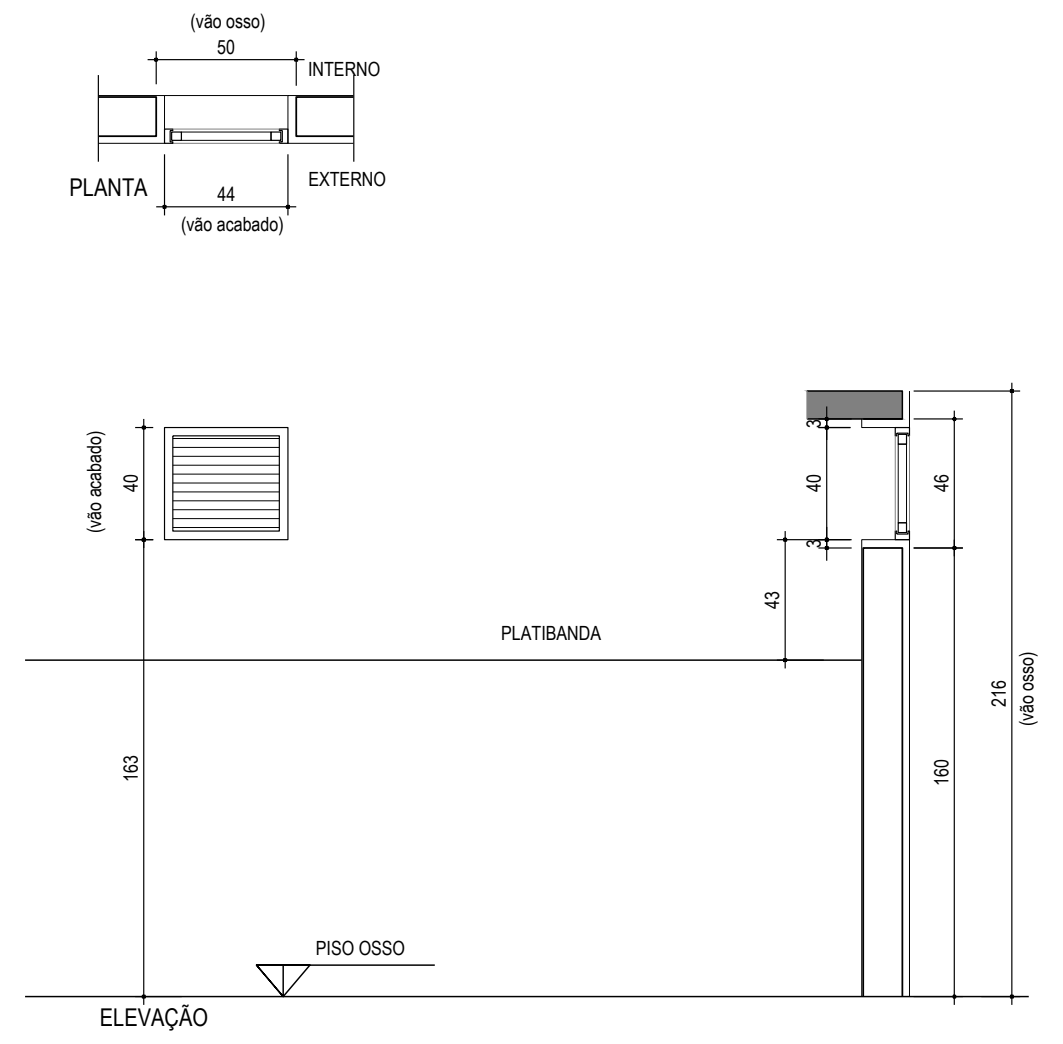
PLANTA
INTERNO
EXTERNO
PLATIBANDA
ELEVAÇÃO
PISO OSSO
163
160

AL 26		AMBIENTE	PAVIMENTO	QUANT.
TIPO:	CAIXILHO FIXO	VENTILAÇÃO GÁS	COBERTURA A / B	2 x 2 = 4
MATERIAL:	ALUMÍNIO			
ACABAM.:	PINTURA ELETROSTÁTICA			
COR:	GRAFITE - RAL 7024			
VIDRO:	LISO E INCOLOR			
OBSERVAÇÃO:	COM VENTILAÇÃO PERMANENTE		TOTAL	4

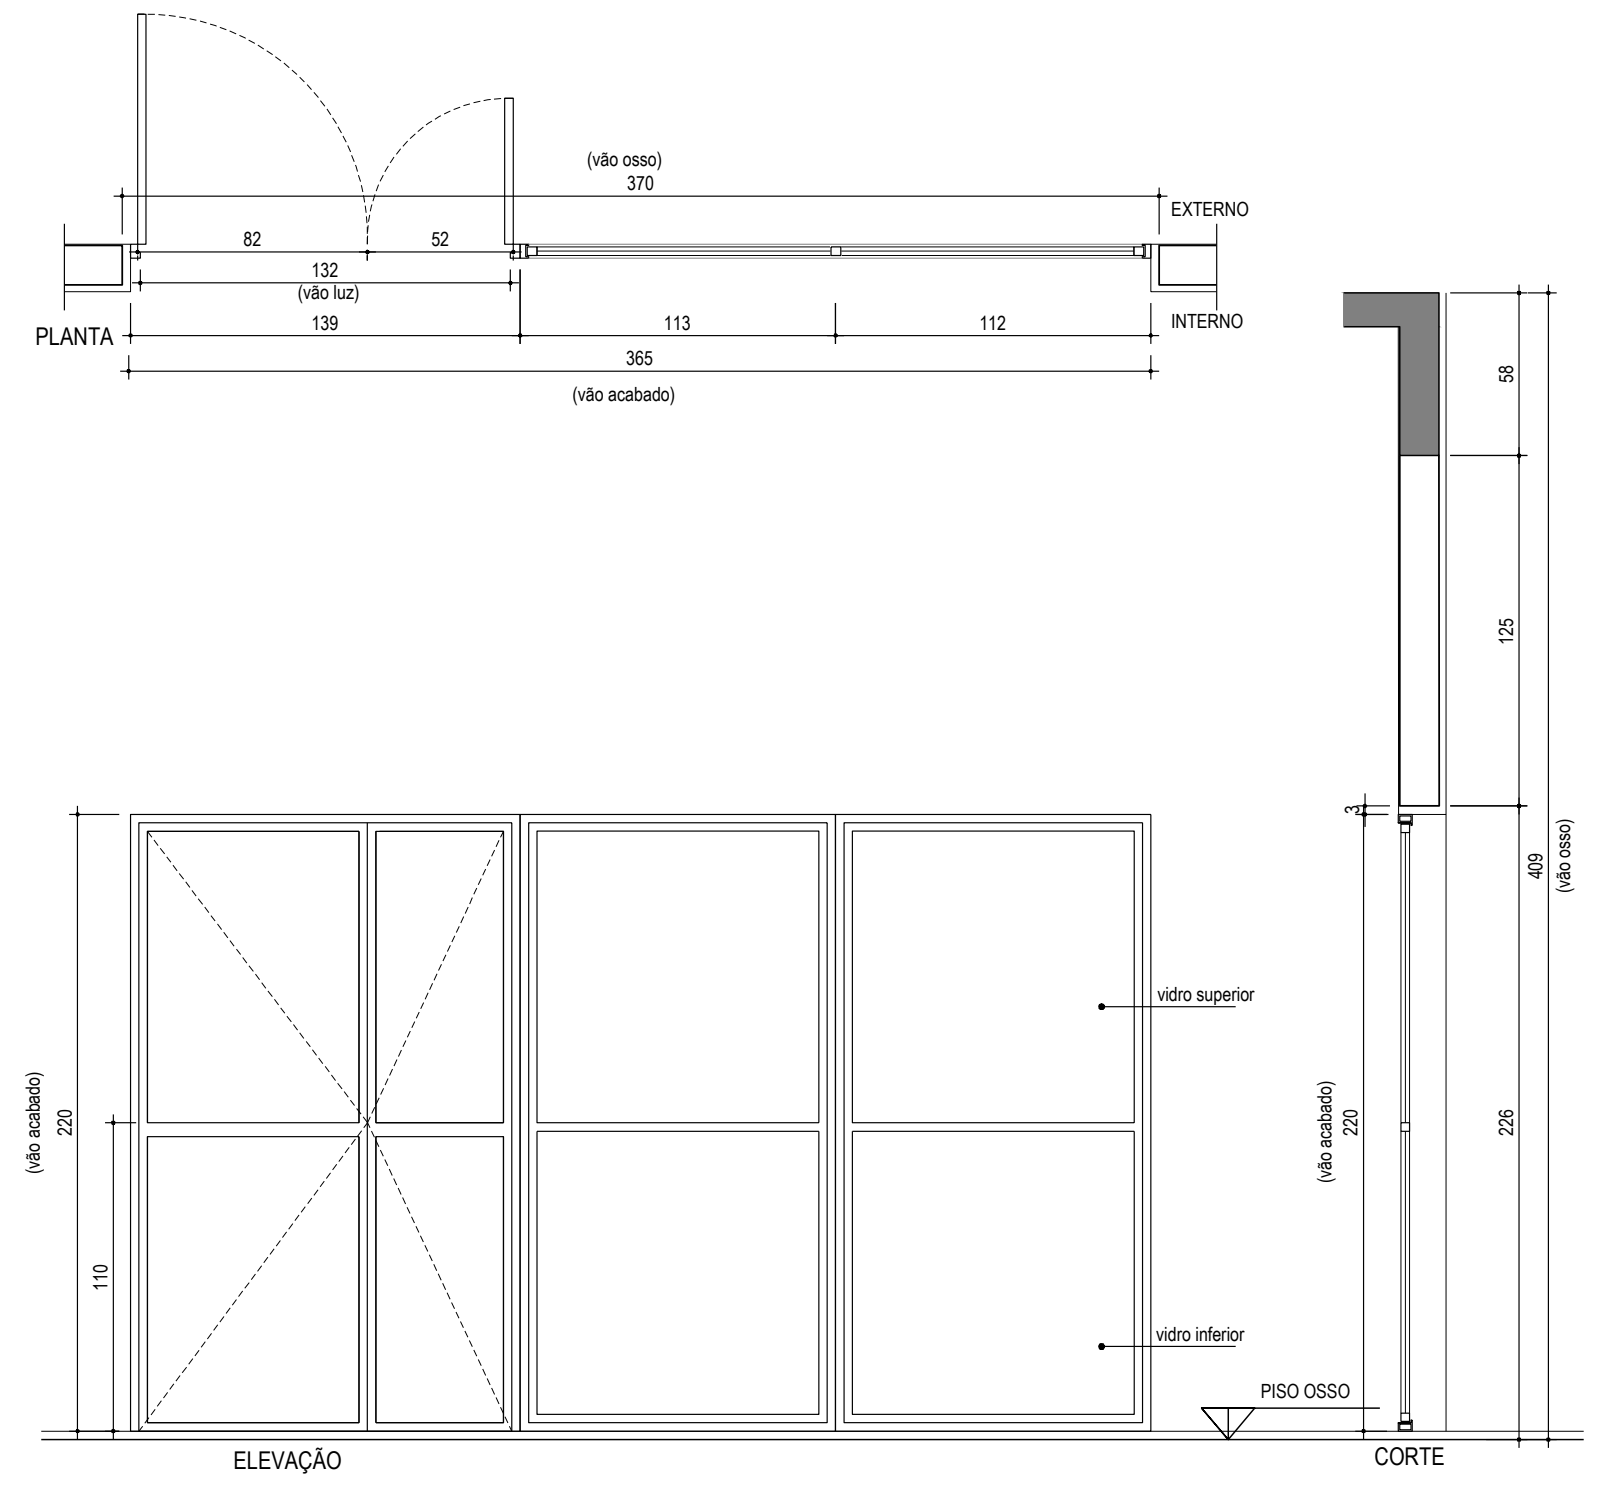
PLANTA
INTERNO
EXTERNO
vidro superior
vidro inferior
ELEVAÇÃO
PISO OSSO
CORTE

AL 27		AMBIENTE	PAVIMENTO	QUANT.
TIPO:	02 FOLHAS DE ABRIR + 02 FOLHAS FIXAS	ACESSO	1º ANDAR	1
MATERIAL:	ALUMÍNIO			
ACABAM.:	PINTURA ELETROSTÁTICA			
COR:	GRAFITE - RAL 7024			
VIDRO:	SUPERIOR - LISO E INCOLOR INFERIOR - INCOLOR LAMINADO OU TEMPERADO			
OBSERVAÇÃO:	-		TOTAL	1

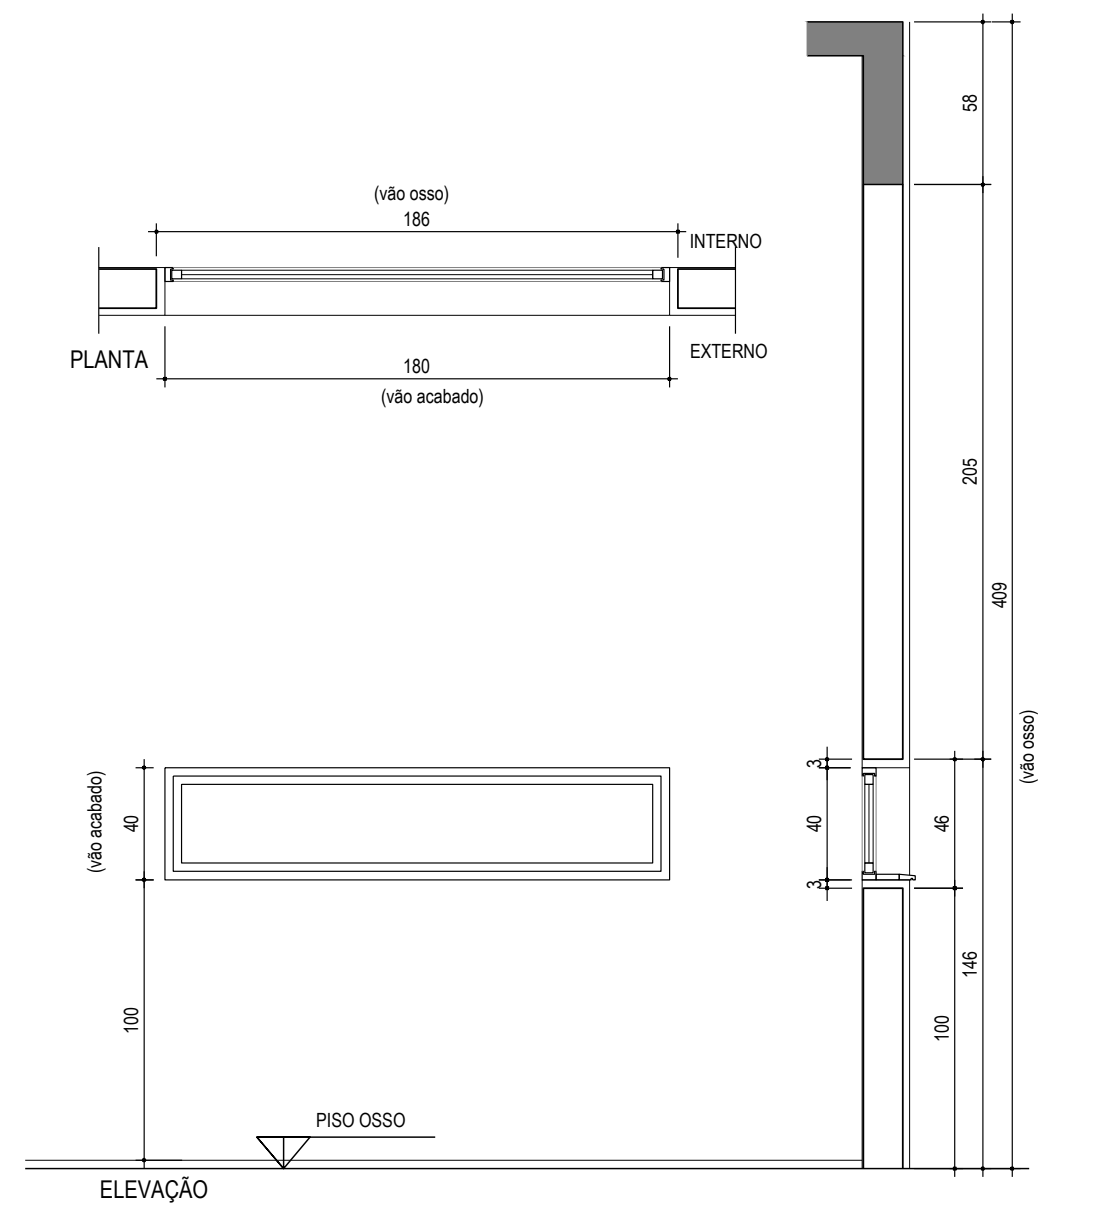
PLANTA
INTERNO
EXTERNO
ELEVAÇÃO
PISO OSSO
CORTE

AL 28		AMBIENTE	PAVIMENTO	QUANT.
TIPO:	CAIXILHO FIXO	PORTARIA	1º ANDAR	1
MATERIAL:	ALUMÍNIO			
ACABAM.:	PINTURA ELETROSTÁTICA			
COR:	GRAFITE - RAL 7024			
VIDRO:	LISO E INCOLOR			
OBSERVAÇÃO:	-		TOTAL	1

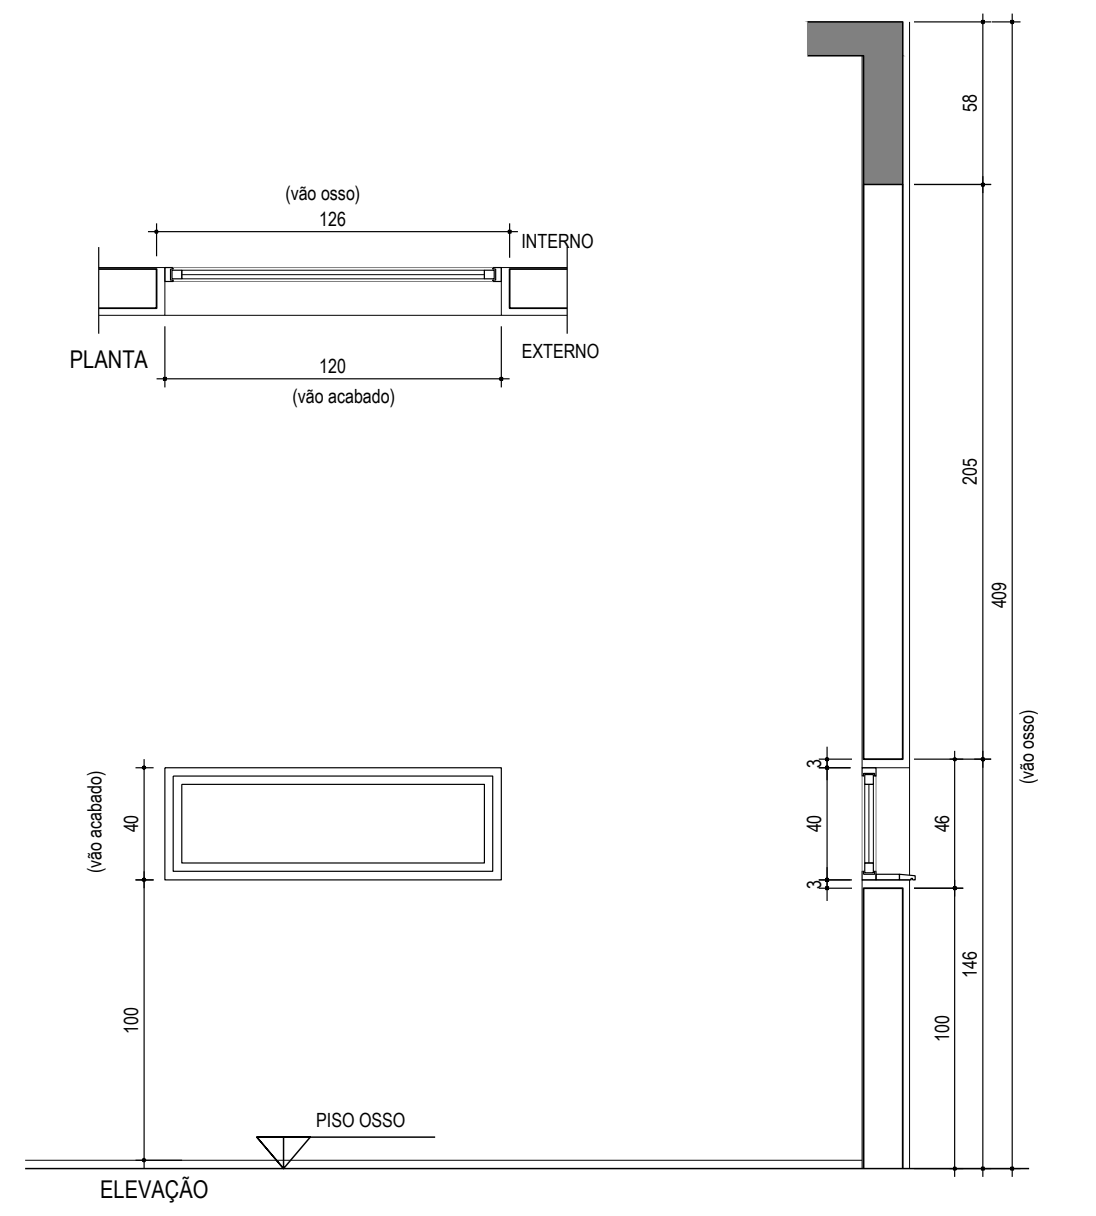
PLANTA
INTERNO
EXTERNO
ELEVAÇÃO
PISO OSSO
CORTE

AL 29		AMBIENTE	PAVIMENTO	QUANT.
TIPO:	CAIXILHO FIXO	PORTARIA	1º ANDAR	1
MATERIAL:	ALUMÍNIO			
ACABAM.:	PINTURA ELETROSTÁTICA			
COR:	GRAFITE - RAL 7024			
VIDRO:	LISO E INCOLOR			
OBSERVAÇÃO:	-		TOTAL	1

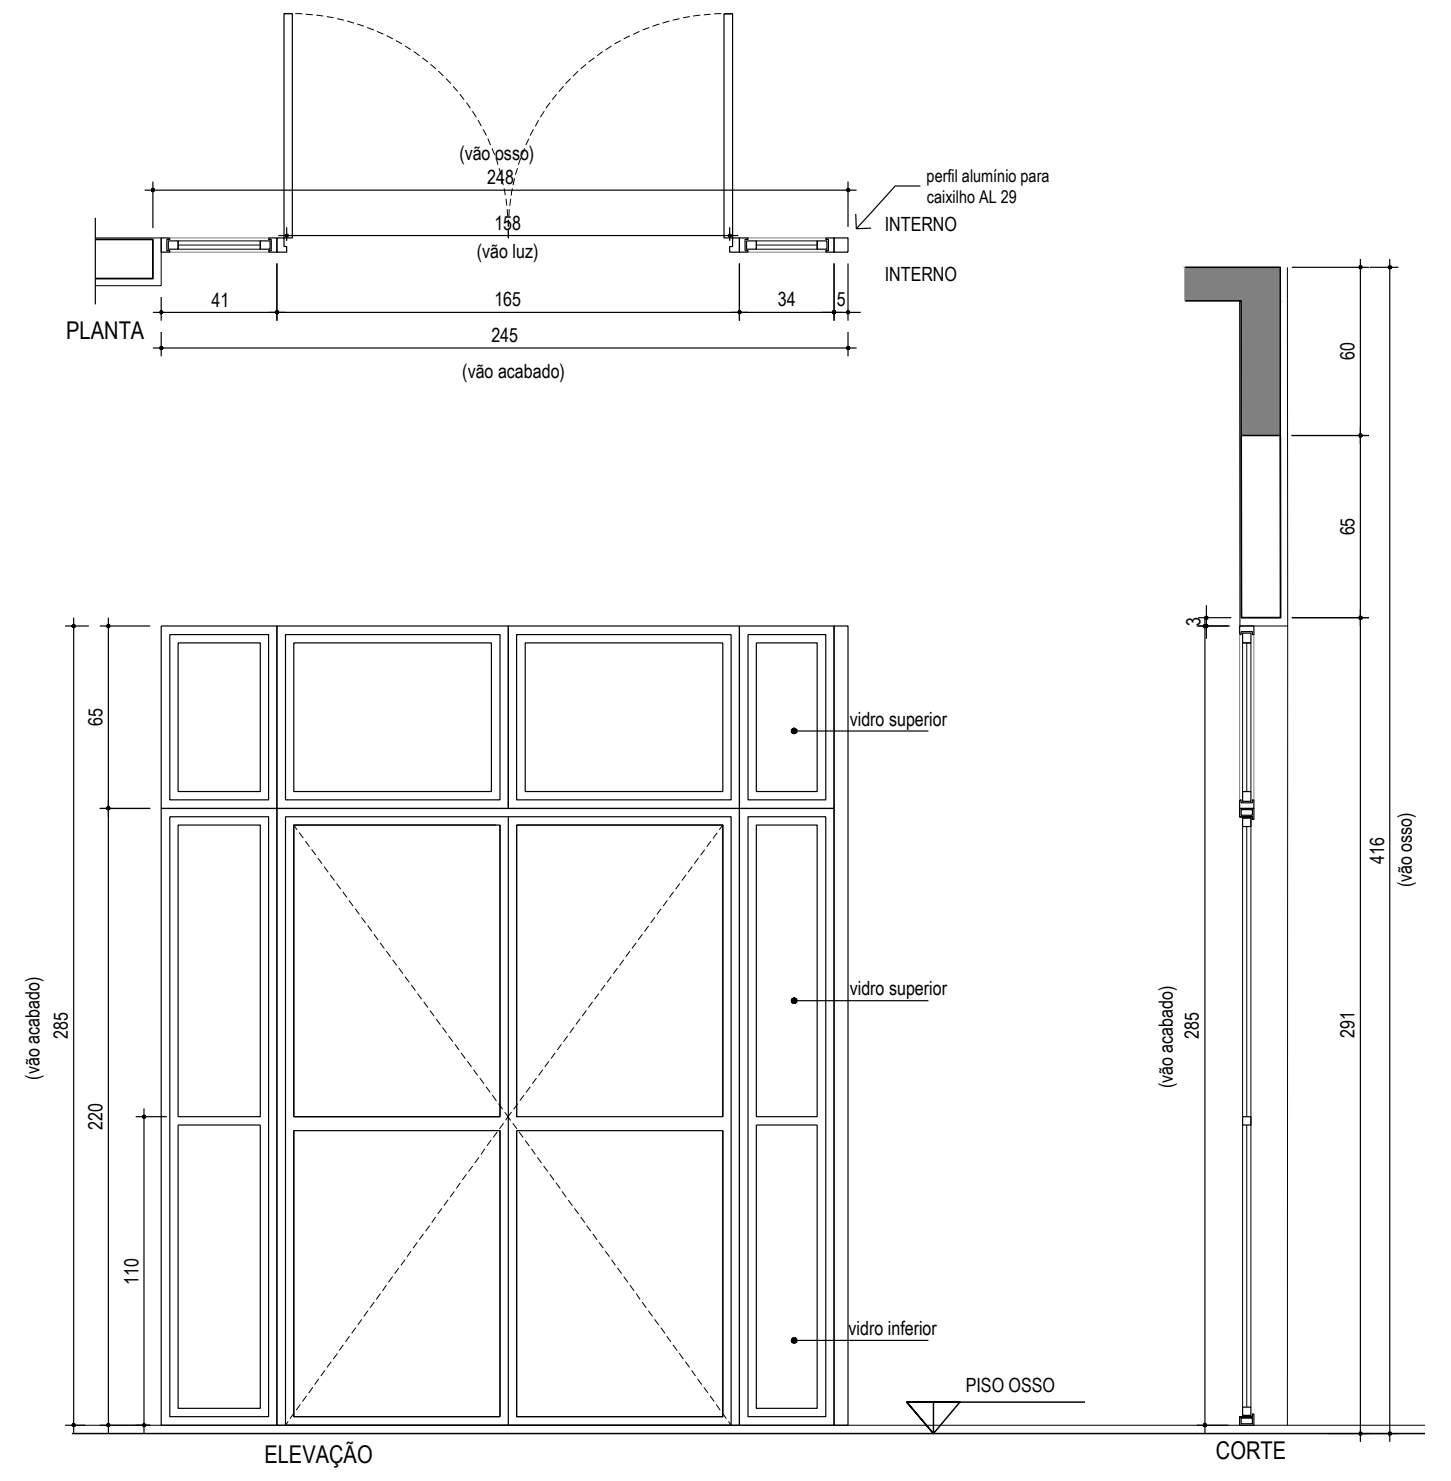
PLANTA
(vão osso)
248
perfil alumínio para
INTERNO
vidro superior
vidro inferior
ELEVAÇÃO
PISO OSSO
CORTE

AL 30		AMBIENTE	PAVIMENTO	QUANT.
TIPO:	02 FOLHAS DE ABRIR + 06 FOLHAS FIXAS	ACESSO	1º ANDAR	1
MATERIAL:	ALUMÍNIO			
ACABAM.:	PINTURA ELETROSTÁTICA			
COR:	GRAFITE - RAL 7024			
VIDRO:	SUPERIOR - LISO E INCOLOR INFERIOR - INCOLOR LAMINADO OU TEMPERADO			
OBSERVAÇÃO:	-		TOTAL	1

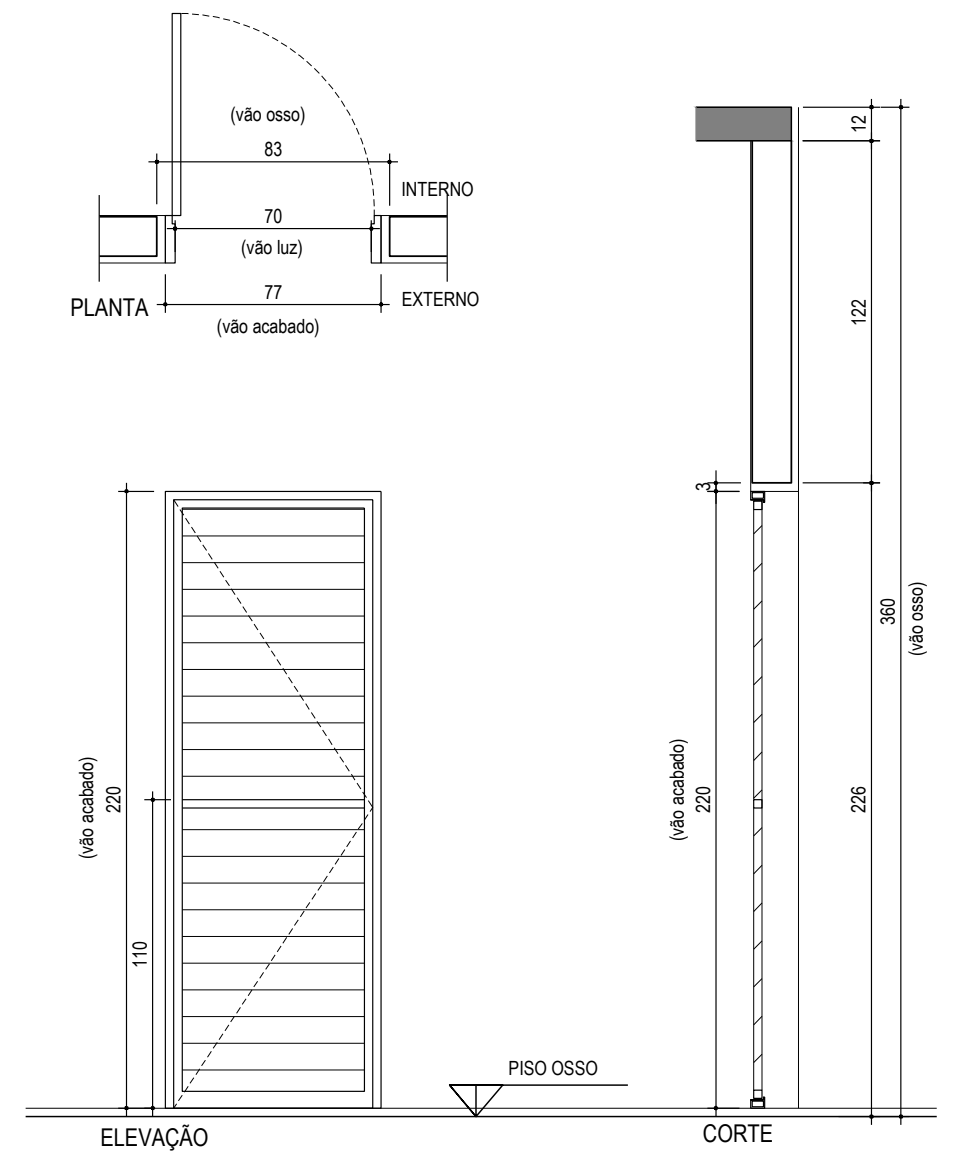
PLANTA
INTERNO
EXTERNO
ELEVAÇÃO
PISO OSSO
CORTE

AL 31		AMBIENTE	PAVIMENTO	QUANT.
TIPO:	01 FOLHA DE ABRIR	DG / ADM. / REUSO	1º ANDAR	3
MATERIAL:	ALUMÍNIO			
ACABAM.:	PINTURA ELETROSTÁTICA			
COR:	GRAFITE - RAL 7024			
VIDRO:	-			
OBSERVAÇÃO:	COM VENTILAÇÃO PERMANENTE		TOTAL	3

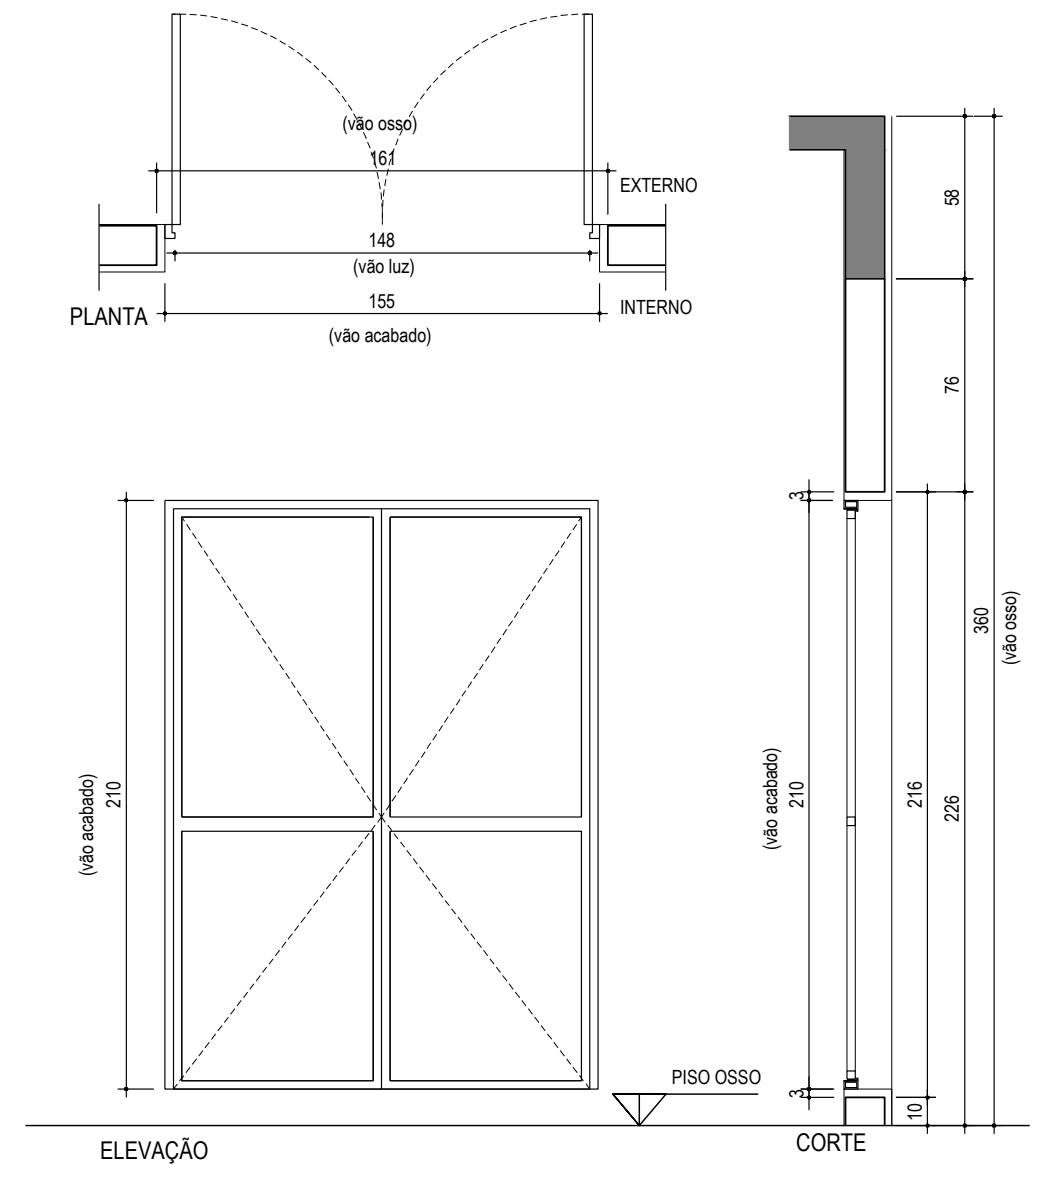
PLANTA
INTERNO
EXTERNO
ELEVAÇÃO
PISO OSSO
CORTE

AL 32		AMBIENTE	PAVIMENTO	QUANT.
TIPO:	01 FOLHA DE ABRIR	RESERVATÓRIO IN.	1º ANDAR	1
MATERIAL:	ALUMÍNIO			
ACABAM.:	PINTURA ELETROSTÁTICA			
COR:	GRAFITE - RAL 7024			
VIDRO:	-			
OBSERVAÇÃO:	-		TOTAL	1

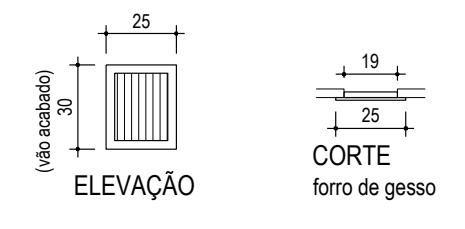
ELEVAÇÃO
CORTE
forro de gesso

AL 33		AMBIENTE	PAVIMENTO	QUANT.
TIPO:	01 FOLHA FIXA	TERRAÇO	TIPO TORRE A / B	10 x 18 x 2 = 360
MATERIAL:	ALUMÍNIO	TERRAÇO	DUPLEX INF. A / B	10 x 2 = 20
ACABAM.:	PINTURA ELETROSTÁTICA	TERRAÇO	5º ANDAR A / B	5 x 2 = 10
COR:	BRANCO (IDEM FORRO DE GESSO)			
VIDRO:	-			
OBSERVAÇÃO:	COM VENTILAÇÃO PERMANENTE		TOTAL	390

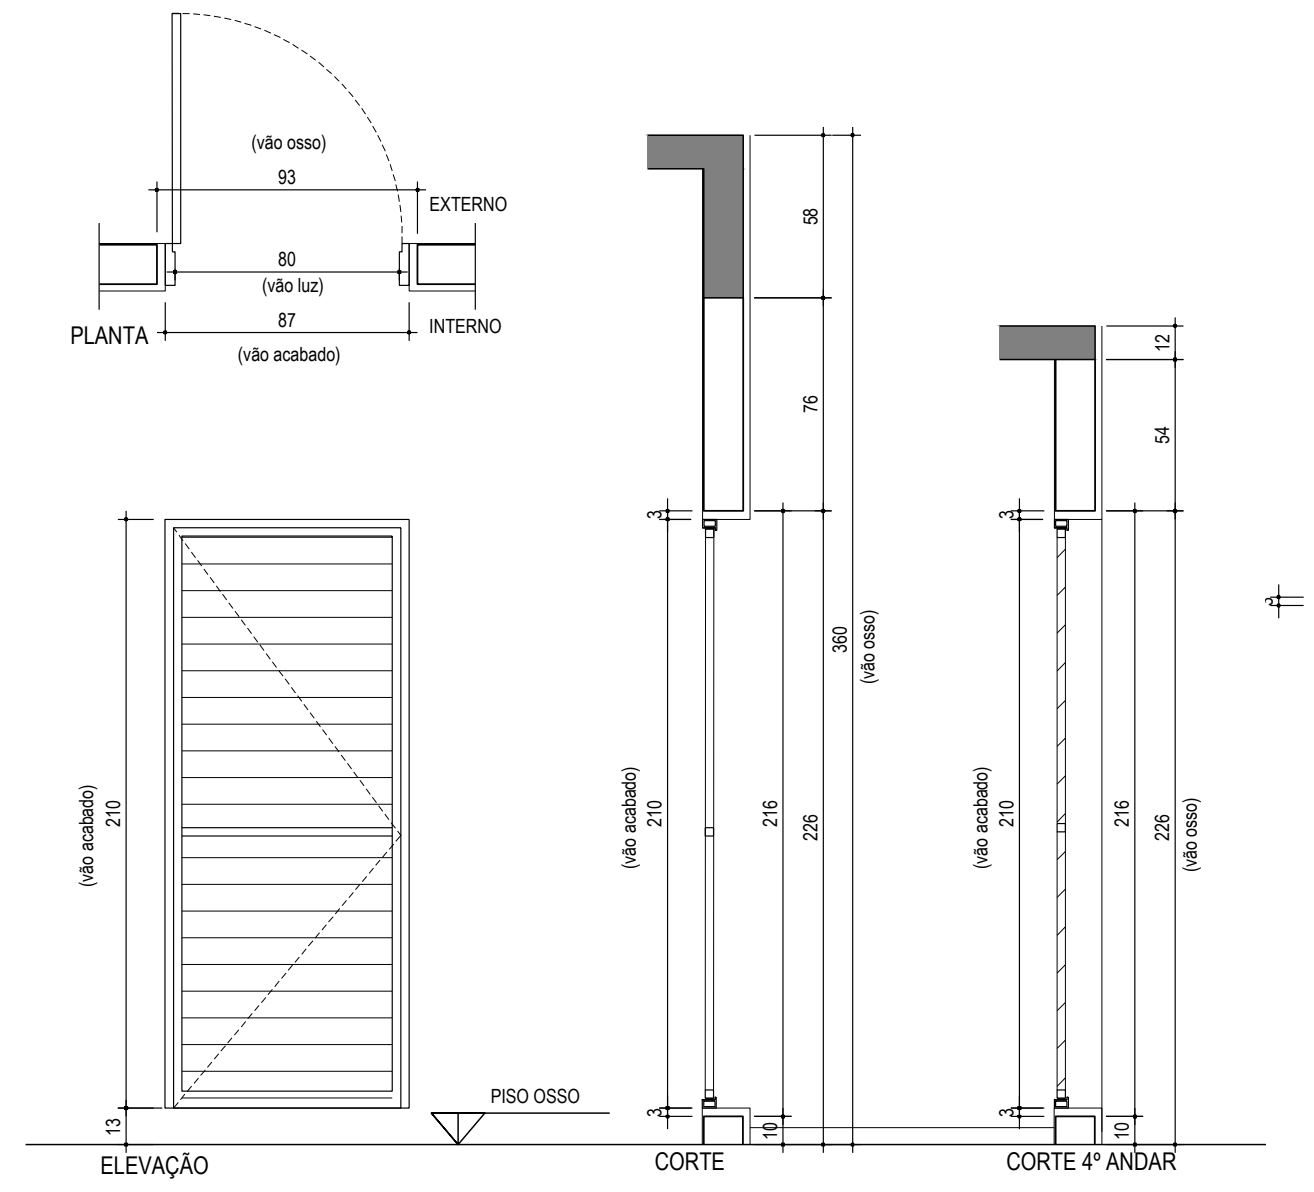
PLANTA
INTERNO
EXTERNO
ELEVAÇÃO
PISO OSSO
CORTE
CORTE 4º ANDAR

AL 34		AMBIENTE	PAVIMENTO	QUANT.
TIPO:	01 FOLHA DE ABRIR	LIXO	1º ANDAR	1
MATERIAL:	ALUMÍNIO	CASA DE BOMBAS	4º ANDAR	1
ACABAM.:	PINTURA ELETROSTÁTICA			
COR:	GRAFITE - RAL 7024			
VIDRO:	-			
OBSERVAÇÃO:	COM VENTILAÇÃO PERMANENTE		TOTAL	2

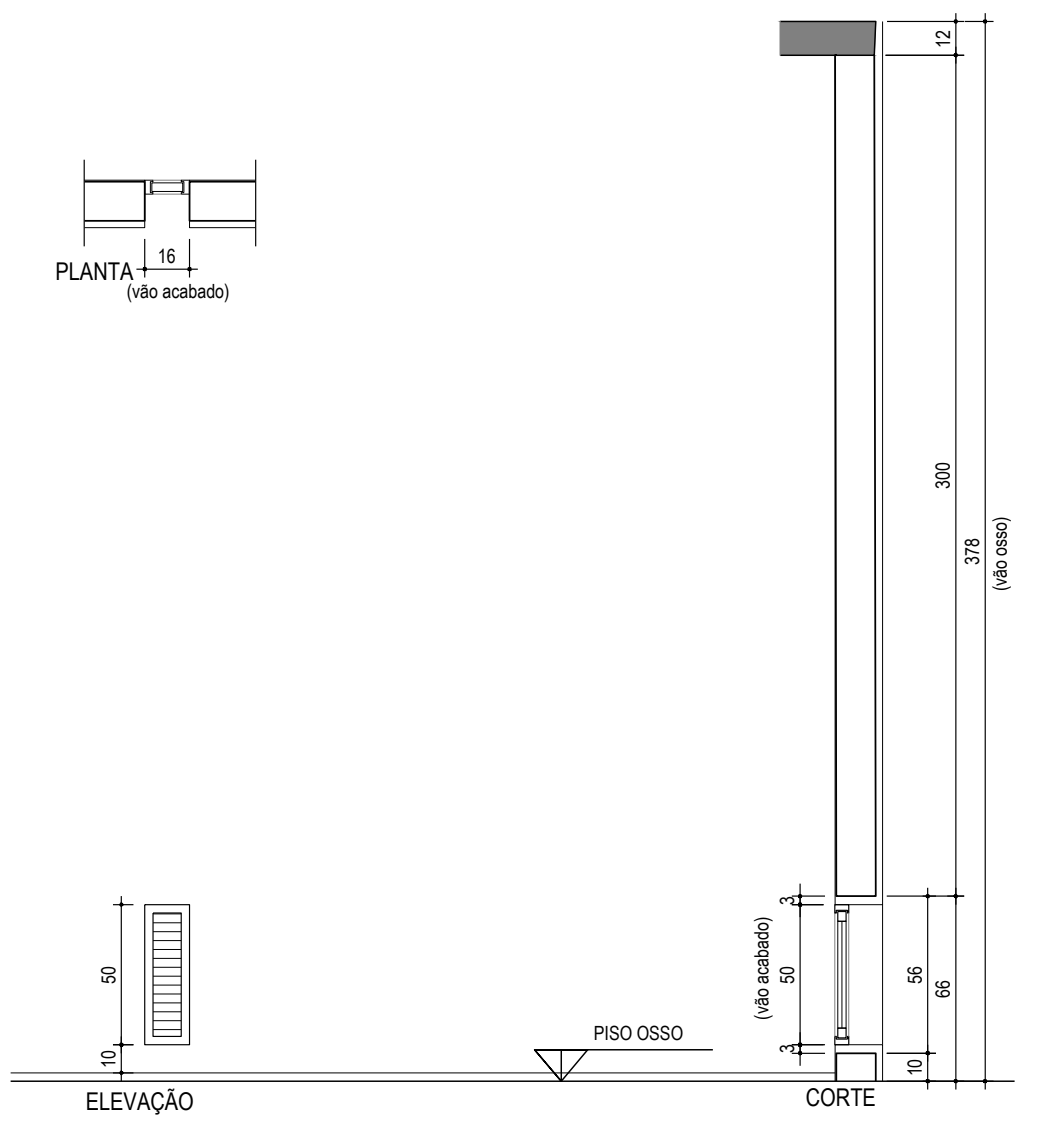
PLANTA
ELEVAÇÃO
PISO OSSO
CORTE
(vão acabado)
50
56
66
10

AL 35		AMBIENTE	PAVIMENTO	QUANT.
TIPO:	01 FOLHA FIXA	SHAFT GÁS	4º ANDAR	2
MATERIAL:	ALUMÍNIO			
ACABAM.:	PINTURA ELETROSTÁTICA			
COR:	GRAFITE - RAL 7024			
VIDRO:	-			
OBSERVAÇÃO:	COM VENTILAÇÃO PERMANENTE		TOTAL	2

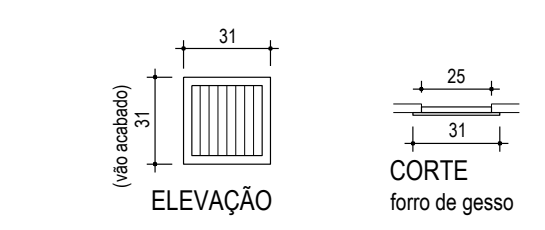
ELEVAÇÃO
CORTE
forro de gesso

AL 36		AMBIENTE	PAVIMENTO	QUANT.
TIPO:	01 FOLHA FIXA	HALL ELEV	4º pav.	9
MATERIAL:	ALUMÍNIO			
ACABAM.:	PINTURA ELETROSTÁTICA			
COR:	BRANCO (IDEM FORRO DE GESSO)			
VIDRO:	-			
OBSERVAÇÃO:	COM VENTILAÇÃO PERMANENTE		TOTAL	9

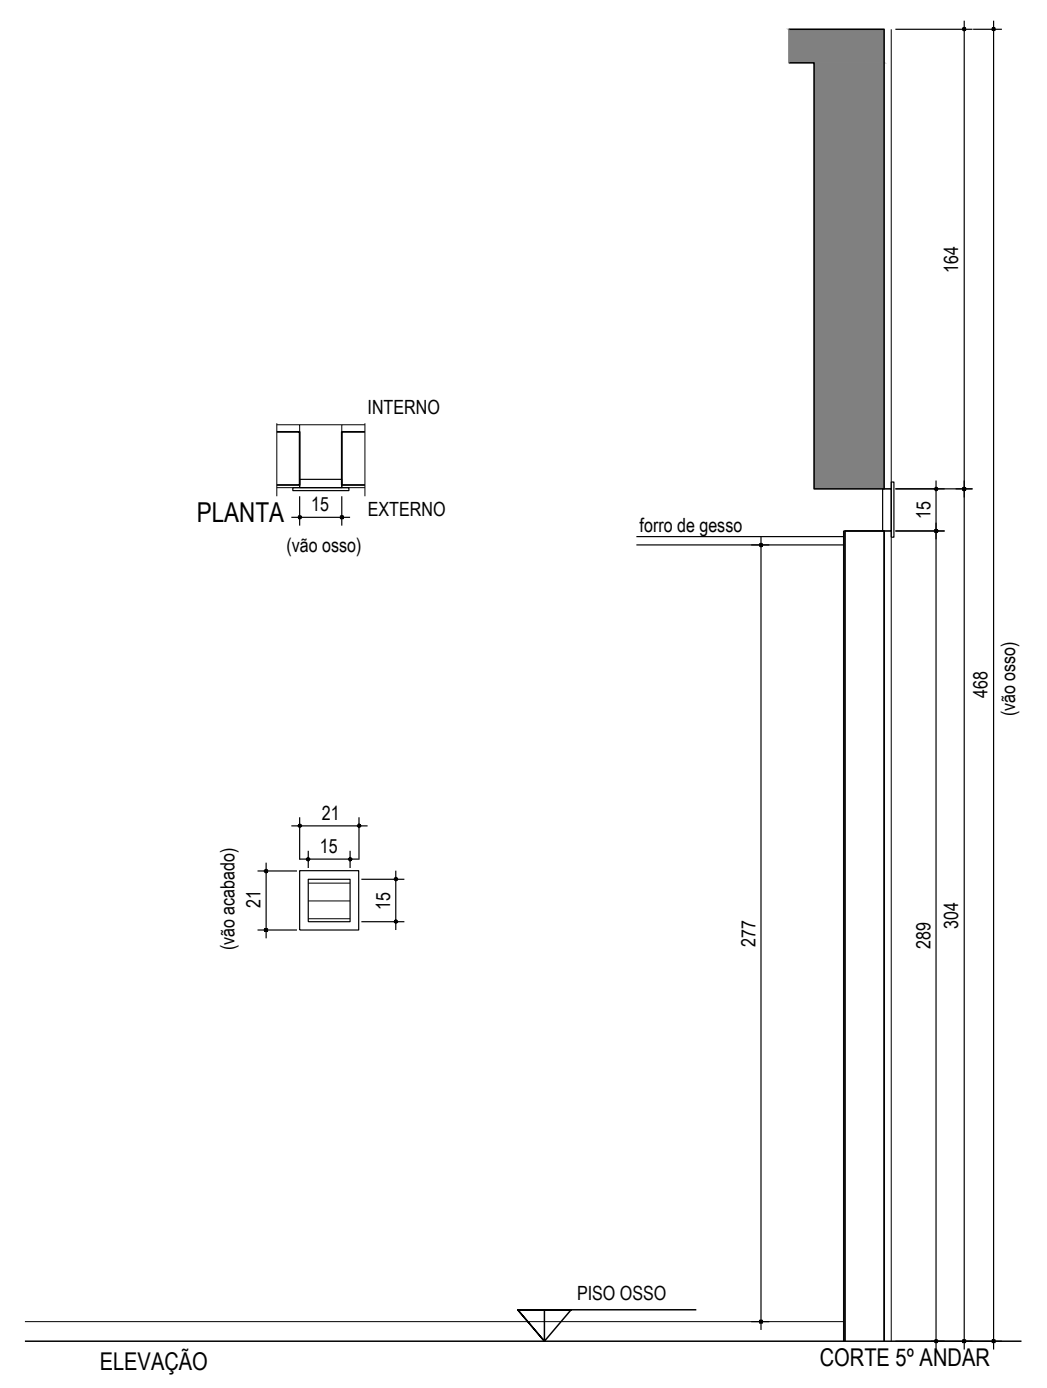
PLANTA
INTERNO
EXTERNO
forro de gesso
ELEVAÇÃO
PISO OSSO
CORTE 5º ANDAR

AL 37		AMBIENTE	PAVIMENTO	QUANT.
TIPO:	01 FOLHA FIXA	TERRAÇO	TIPO TORRE A / B	10 x 18 x 2 = 360
MATERIAL:	ALUMÍNIO ANODIZADO	TERRAÇO	DUPLEX INF. A / B	10 x 2 = 20
ACABAM.:	PINTURA	TERRAÇO	5º ANDAR A / B	5 x 2 = 10
COR:	GRAFITE - RAL 7024			
VIDRO:	-			
OBSERVAÇÃO:	COM VENTILAÇÃO PERMANENTE		TOTAL	390

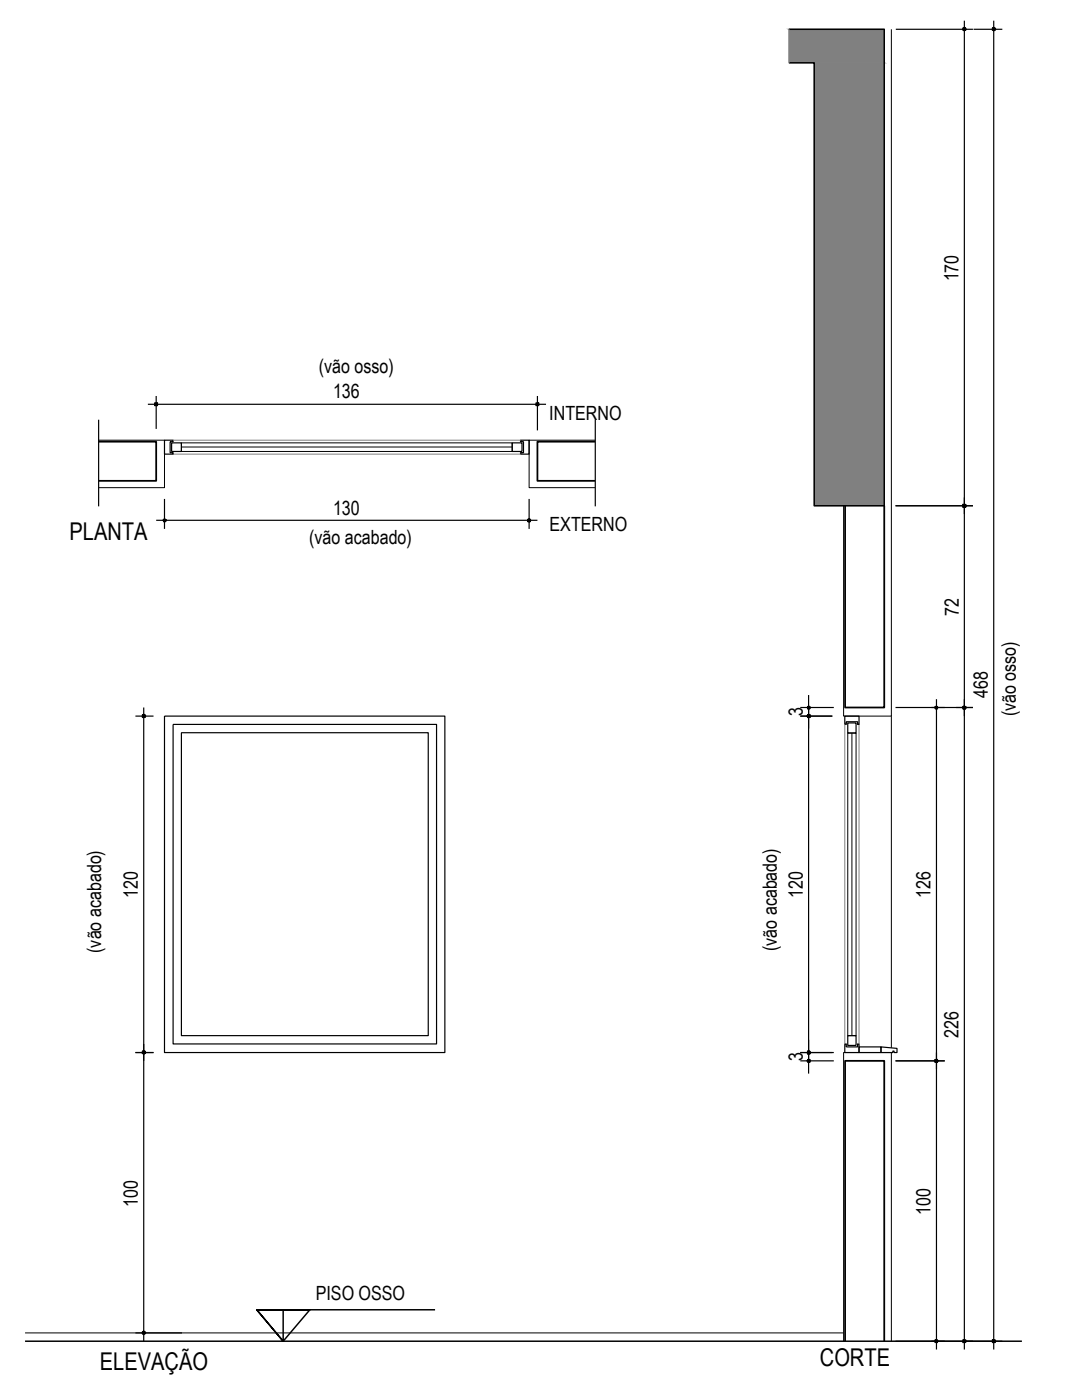
PLANTA
INTERNO
EXTERNO
ELEVAÇÃO
PISO OSSO
CORTE

AL 38		AMBIENTE	PAVIMENTO	QUANT.
TIPO:	CAIXILHO FIXO	LAZER	5º ANDAR A / B	1 x 2 = 2
MATERIAL:	ALUMÍNIO			
ACABAM.:	PINTURA ELETROSTÁTICA			
COR:	GRAFITE - RAL 7024			
VIDRO:	LISO E INCOLOR			
OBSERVAÇÃO:	-		TOTAL	2

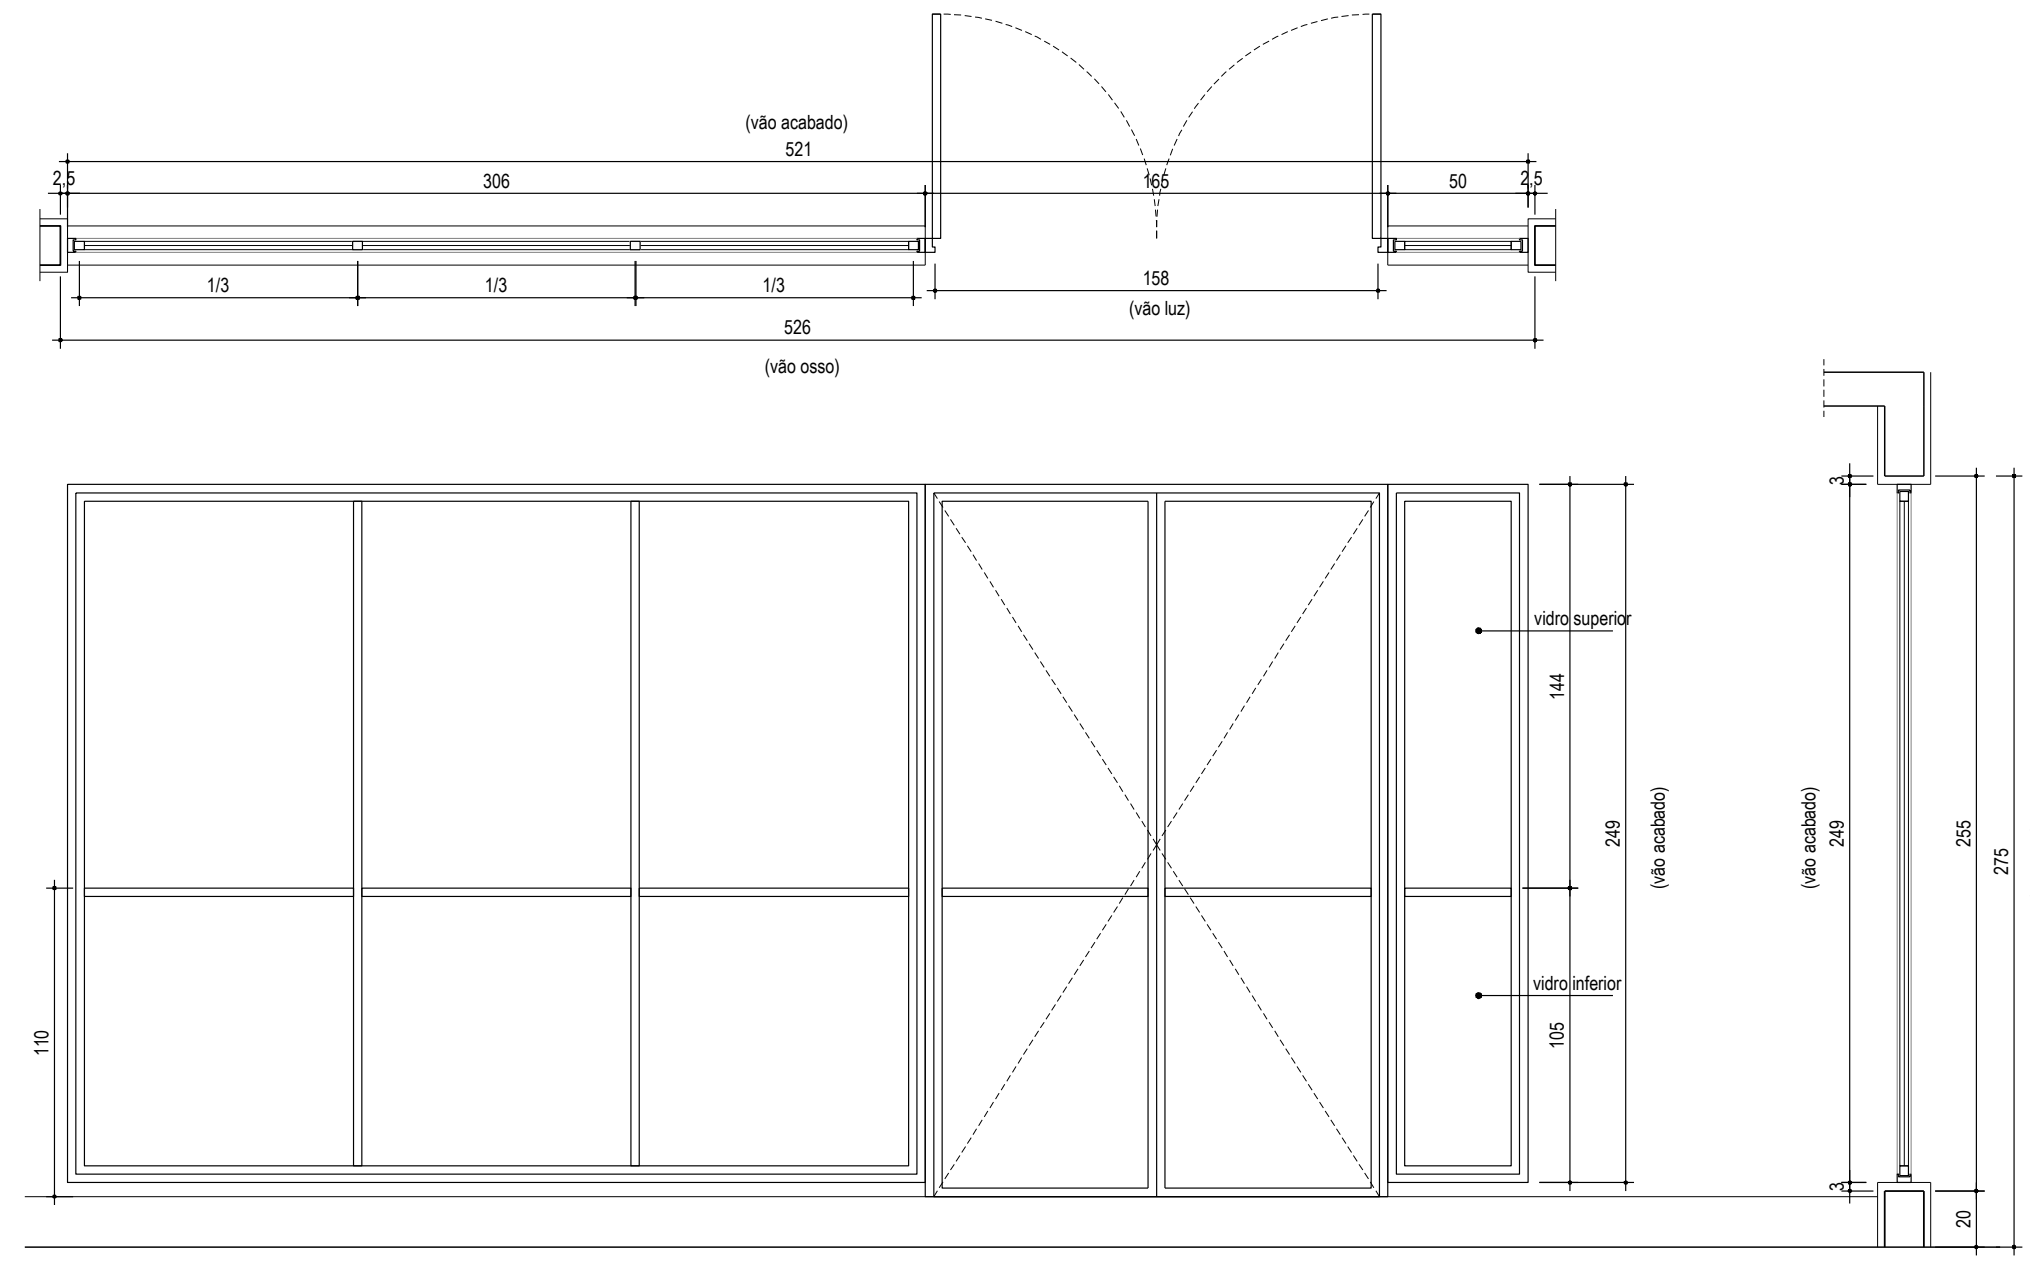
vidro superior
vidro inferior
105
20

AL 39		AMBIENTE	PAVIMENTO	QUANT.
TIPO:	02 FOLHAS DE ABRIR + 03 FOLHAS FIXAS	ACESSO ELEV.	PUC	1
MATERIAL:	ALUMÍNIO			
ACABAM.:	PINTURA ELETROSTÁTICA			
COR:	GRAFITE - RAL 7024			
VIDRO:	SUPERIOR - LISO E INCOLOR INFERIOR - INCOLOR LAMINADO OU TEMPERADO			
OBSERVAÇÃO:	-		TOTAL	1

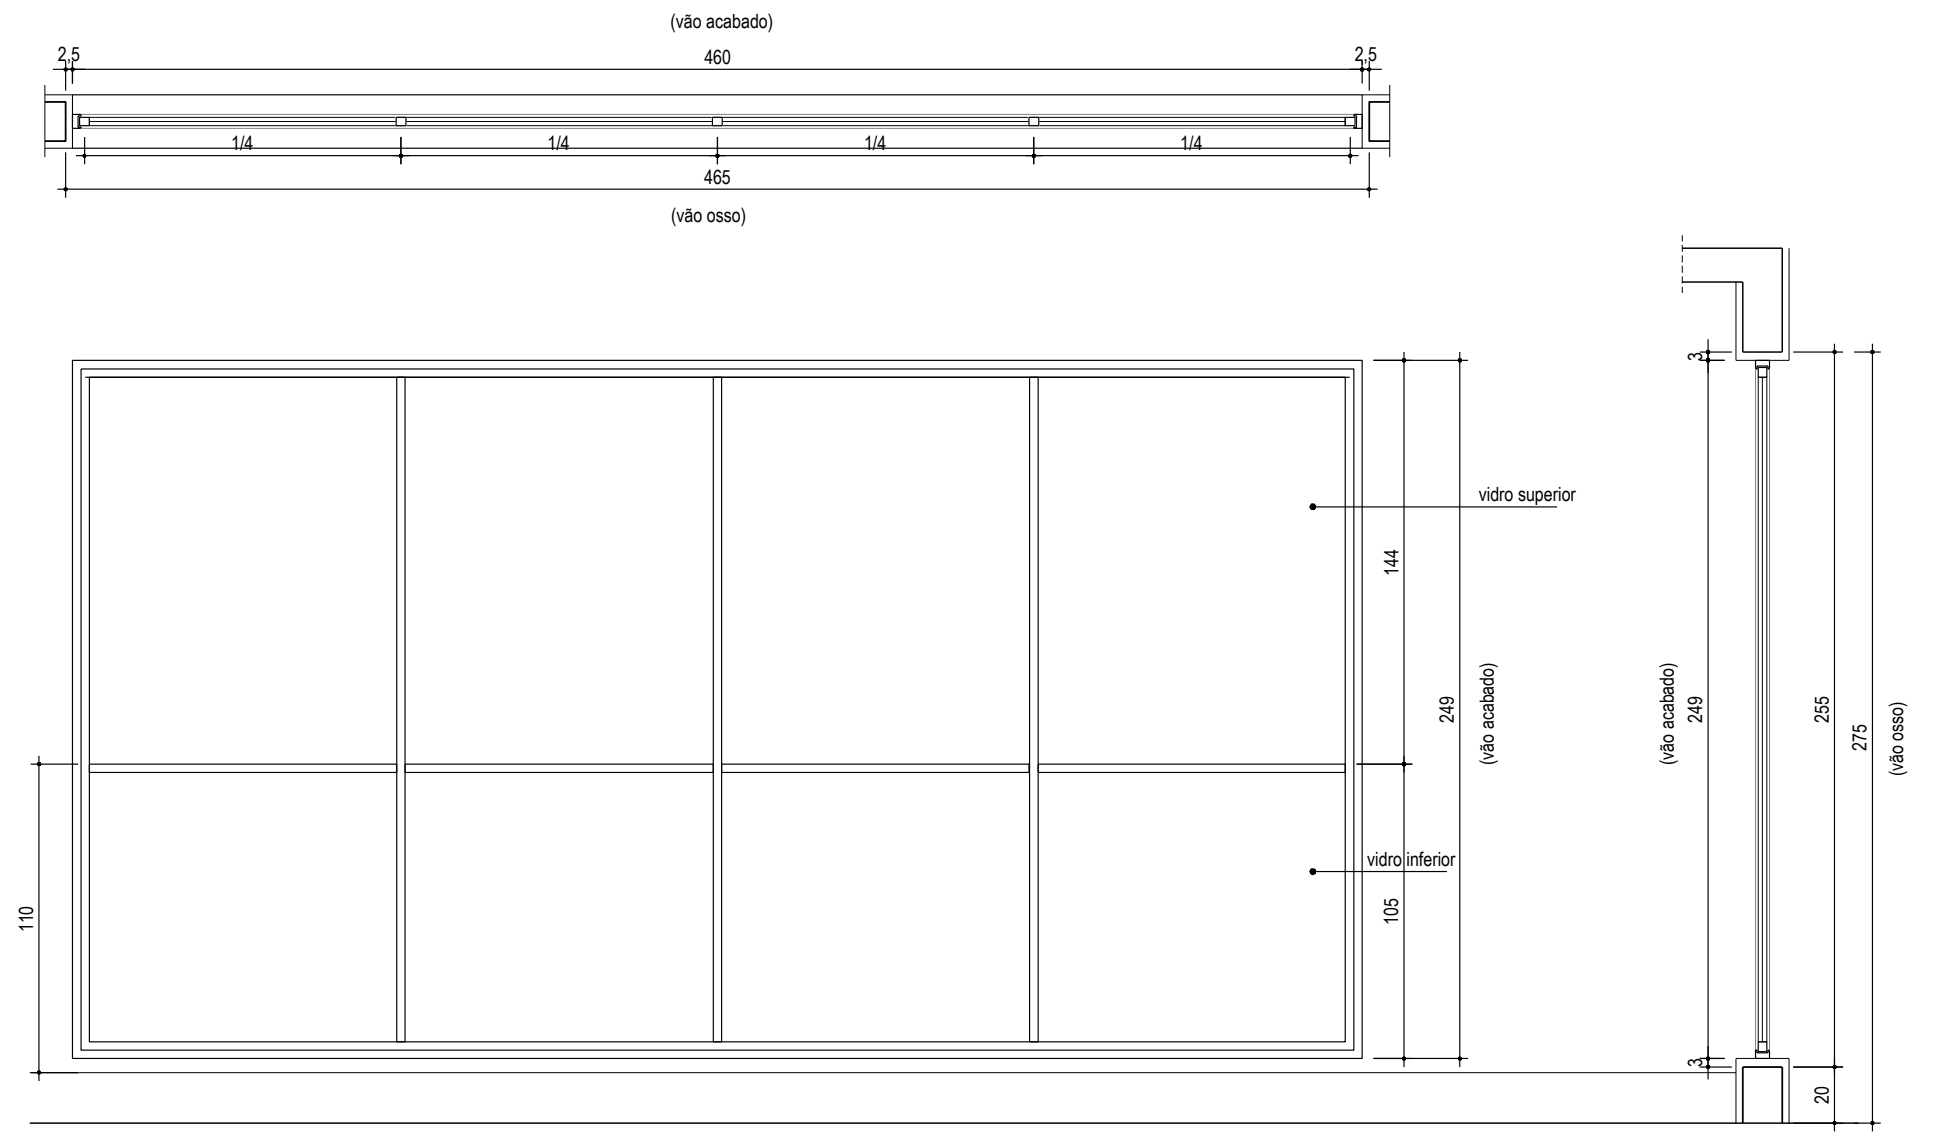
vidro superior
vidro inferior

AL 40		AMBIENTE	PAVIMENTO	QUANT.
TIPO:	04 FOLHAS FIXAS	ACESSO ELEV.	PUC	1
MATERIAL:	ALUMÍNIO			
ACABAM.:	PINTURA ELETROSTÁTICA			
COR:	GRAFITE - RAL 7024			
VIDRO:	SUPERIOR - LISO E INCOLOR INFERIOR - INCOLOR LAMINADO OU TEMPERADO			
OBSERVAÇÃO:	-		TOTAL	1

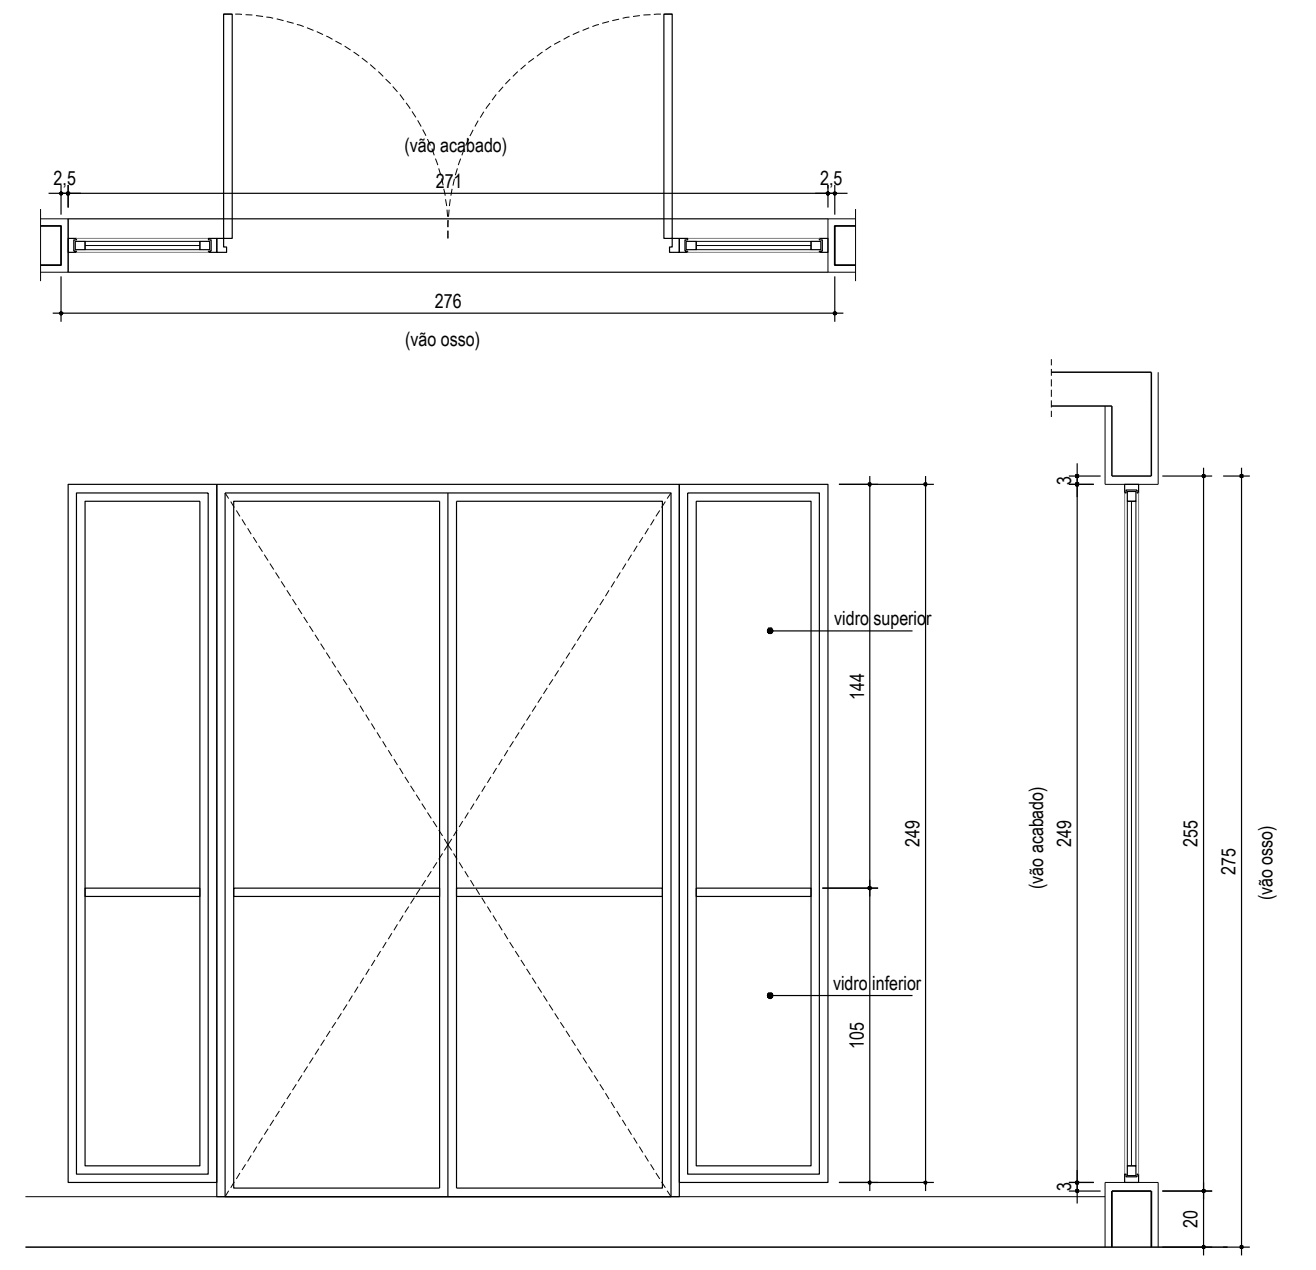
vidro superior
vidro inferior
105
20

AL 41		AMBIENTE	PAVIMENTO	QUANT.
TIPO:	02 FOLHAS DE ABRIR + 02 FOLHAS FIXAS	ACESSO ELEV.	PUC	1
MATERIAL:	ALUMÍNIO			
ACABAM.:	PINTURA ELETROSTÁTICA			
COR:	GRAFITE - RAL 7024			
VIDRO:	SUPERIOR - LISO E INCOLOR INFERIOR - INCOLOR LAMINADO OU TEMPERADO			
OBSERVAÇÃO:	-		TOTAL	1

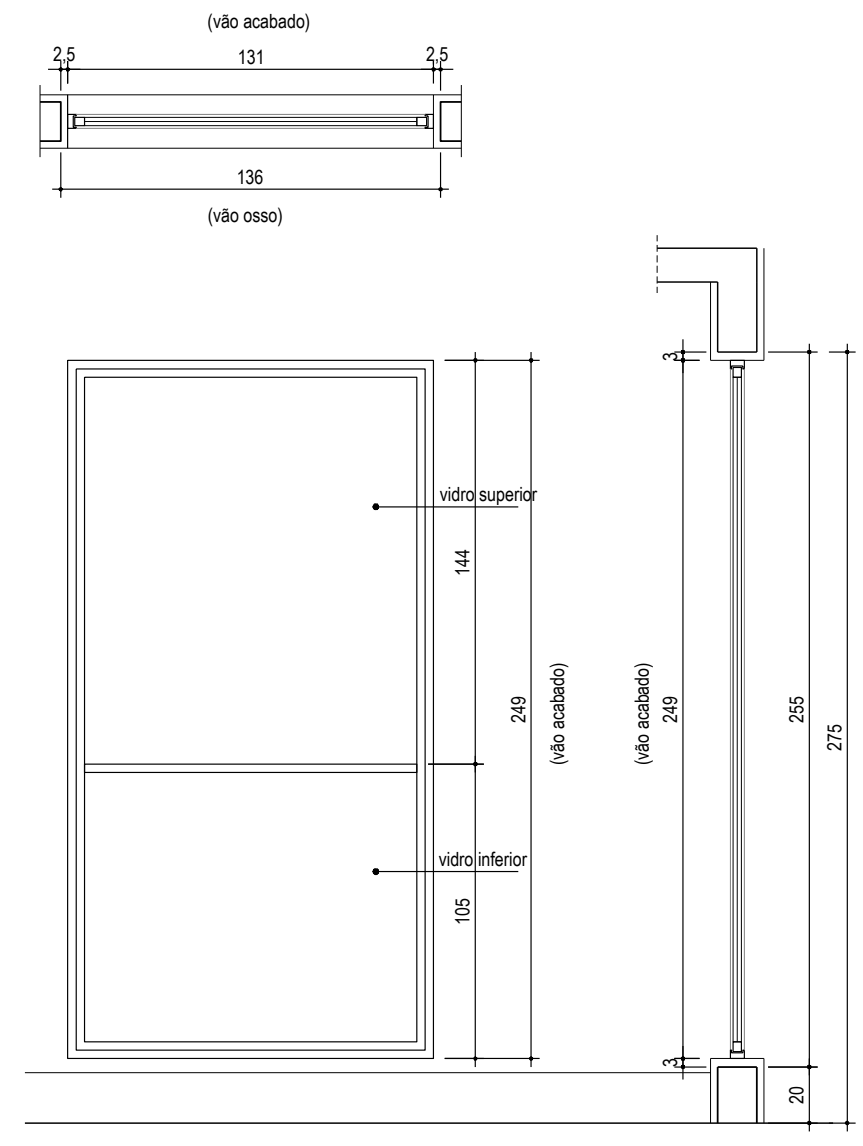
vidro superior
vidro inferior
105
20

AL 42		AMBIENTE	PAVIMENTO	QUANT.
TIPO:	01 FOLHA FIXA	ACESSO ELEV.	PUC	1
MATERIAL:	ALUMÍNIO			
ACABAM.:	PINTURA ELETROSTÁTICA			
COR:	GRAFITE - RAL 7024			
VIDRO:	SUPERIOR - LISO E INCOLOR INFERIOR - INCOLOR LAMINADO OU TEMPERADO			
OBSERVAÇÃO:	-		TOTAL	1

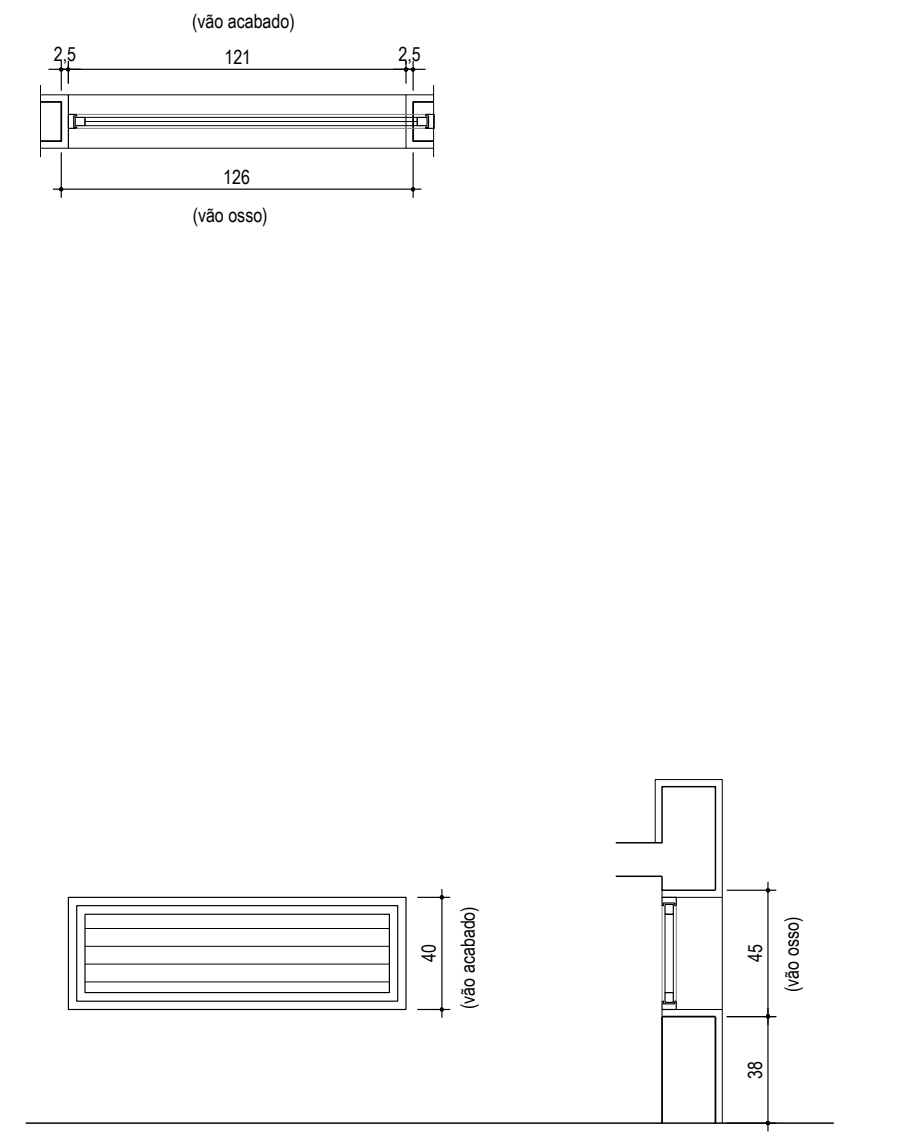
40
(vão acabado)
45
(vão osso)
38

AL 43		AMBIENTE	PAVIMENTO	QUANT.
TIPO:	01 FOLHA FIXA	ELEV. PUC	PUC	1
MATERIAL:	ALUMÍNIO			
ACABAM.:	PINTURA ELETROSTÁTICA			
COR:	GRAFITE - RAL 7024			
VIDRO:	SUPERIOR - LISO E INCOLOR INFERIOR - INCOLOR LAMINADO OU TEMPERADO			
OBSERVAÇÃO:	-		TOTAL	1

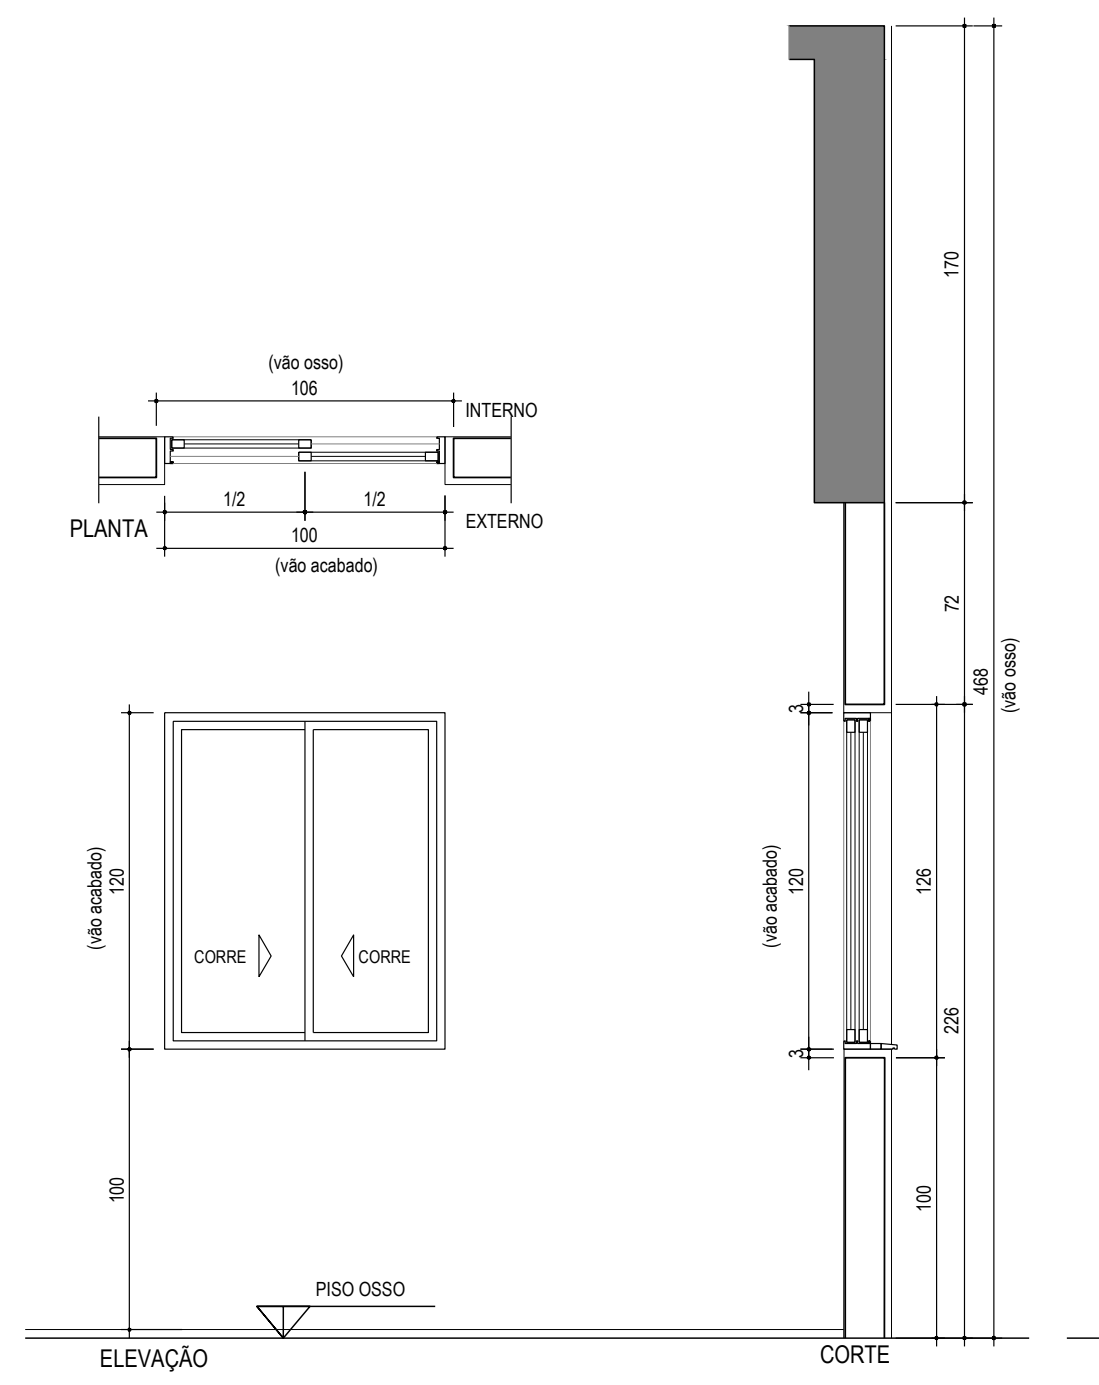
PLANTA
INTERNO
EXTERNO
CORRE
CORRE
ELEVAÇÃO
PISO OSSO
CORTE

AL 44		AMBIENTE	PAVIMENTO	QUANT.
TIPO:	02 FOLHAS DE CORRER	COPA - LAZER	5º ANDAR A	1
MATERIAL:	ALUMÍNIO			
ACABAM.:	PINTURA ELETROSTÁTICA			
COR:	GRAFITE - RAL 7024			
VIDRO:	LISO E INCOLOR			
OBSERVAÇÃO:	-		TOTAL	1

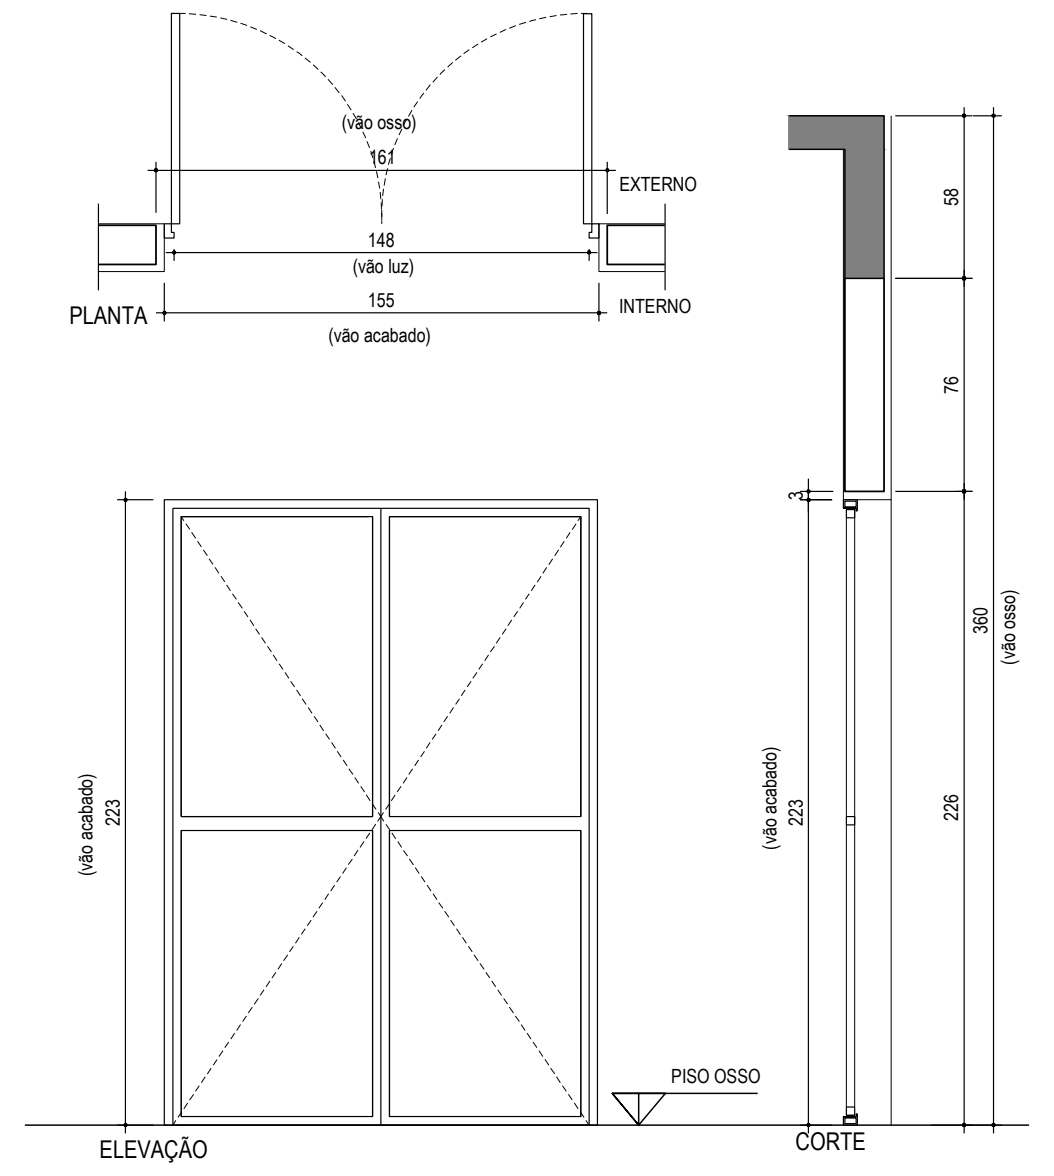
PLANTA
INTERNO
EXTERNO
ELEVAÇÃO
PISO OSSO
CORTE

AL 45		AMBIENTE	PAVIMENTO	QUANT.
TIPO:	01 FOLHA DE ABRIR	E.T.E.	1º ANDAR	1
MATERIAL:	ALUMÍNIO			
ACABAM.:	PINTURA ELETROSTÁTICA			
COR:	GRAFITE - RAL 7024			
VIDRO:	-			
OBSERVAÇÃO:	-		TOTAL	1

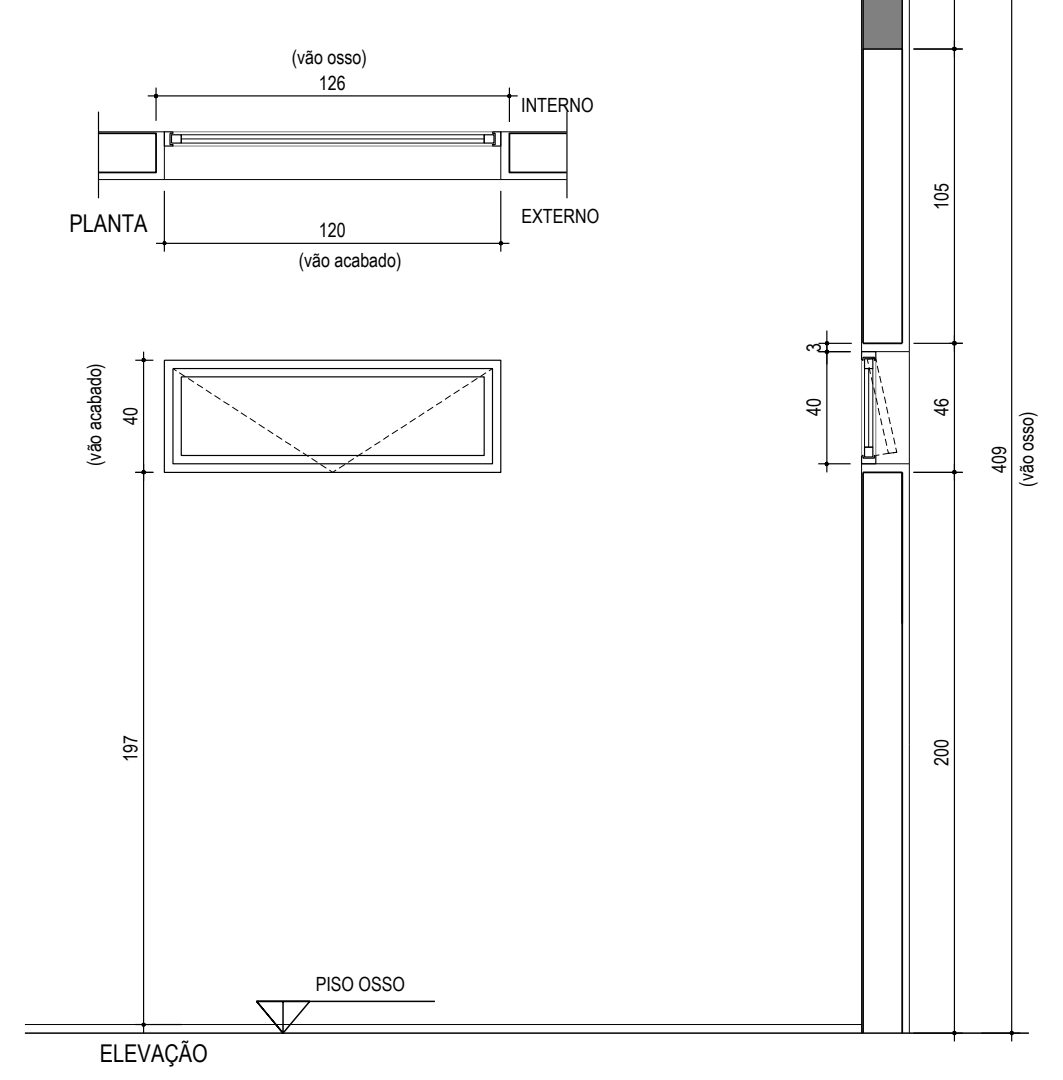
PLANTA
INTERNO
EXTERNO
ELEVAÇÃO
PISO OSSO

AL 46		AMBIENTE	PAVIMENTO	QUANT.
TIPO:	MAXIM AR	PORTARIA	1º ANDAR	1
MATERIAL:	ALUMÍNIO			
ACABAM.:	PINTURA ELETROSTÁTICA			
COR:	GRAFITE - RAL 7024			
VIDRO:	LISO E INCOLOR			
OBSERVAÇÃO:	HASTE MAIS BAIXA PARA ABERTURA		TOTAL	1

LEIS

NBR 15575:2013 - DESEMPENHO DE EDIFICAÇÕES HABITACIONAIS;
NBR 9050:2020 - ACESSIBILIDADE A EDIFICAÇÕES, MOBILIÁRIO, ESPAÇO E EQUIPAMENTOS URBANOS;
NBR 14718:2019 - GUARDA-CORPOS PARA EDIFICAÇÕES;
NBR 13103:2020 - INSTALAÇÃO DE APARELHOS A GÁS PARA USO RESIDENCIAL - REQUISITOS DOS AMBIENTES;
NBR 9077:2001 - SAÍDAS DE EMERGÊNCIA EM EDIFÍCIOS;
NBR NM 313 - ELEVADORES DE PASSAGEIROS;

VIDA ÚTIL DO PROJETO (VUP)

Conforme mínimo especificado na NBR 15575:2013- Desempenho de edificações habitacionais

- ESTRUTURA: >/ 50 anos;
- PISOS INTERNOS: >/ 13 anos;
- VEDAÇÃO VERTICAL EXTERNA: >/ 40 anos;
- VEDAÇÃO VERTICAL INTERNA: >/ 20 anos;
- COBERTURA: >/ 20 anos;
- HIDROSSANITÁRIO: >/ 20 anos;

TRRF DAS PAREDES

a. ESCADA DE EMERGÊNCIA, SALA DE PRESSURIZAÇÃO E CASA DE BOMBAS DE INCÊNDIO DEVEM TER TRRF DE 120 min;
b. ESTRUTURAS DA EDIFICAÇÃO DEVEM TER TRRF DE 120min;
c. ABERTURAS ENTRE LAJES (SHAFTS) DEVEM TER VEDAÇÃO COM MATERIAIS DE TRRF DE 120min;
d. AS PAREDES ENTRE AS UNIDADES E ENTRE AS UNIDADES E A ÁREA DE CIRCULAÇÃO DEVEM TER TRRF DE 60min;
e. COMPARTIMENTAÇÃO VERTICAL EXTERNA DE FACHADA COM VERGA-PEITORIL DE 1,20m COM TRRF DE 120 min;

LEGENDA DETALHE DE MADEIRA

PEM - PORTA ENTRADA DE MADEIRA
PIM - PORTA INTERNA DE MADEIRA
RU - RESISTENTE À UMIDADE
PIA - PORTA INSOLANTE ACÚSTICA

NOTAS

1 - TODAS AS MEDIDAS ESTÃO EM CENTÍMETROS.
2 - VER MEMORIAL DESCRITIVO DE ACABAMENTOS.
3 - VER CADERNOS DE DETALHES.
4 - ÁREAS EXTERNAS - VER PROJETO DE PAISAGISMO.
5 - ÁREAS SOCIAIS INTERNAS - VER PROJETO DE INTERIORES.
6 - CONSIDERAR AS MEDIDAS PARA AS VAGAS:
. VAGA = 250 x 500 cm
. VAGA P.C.D. = 370 x 500 cm

TABELA DE ACABAMENTOS

VER ESPECIFICAÇÃO COMPLETA DE MATERIAIS NOS CADERNOS DE DETALHES E NO MEMORIAL DE ACABAMENTOS DO CLIENTE. PARA O USO DE MATERIAIS SIMILARES CONSULTAR O COORDENADOR DE PROJETOS.

INDICAÇÃO DE NÍVEIS

00.00(NA) → NÍVEL ACABADO
00.00(NO) → NÍVEL OSSO

▨ - SINALIZAÇÃO TÁTIL

LEGENDA:

REPRESENTAÇÃO GRÁFICA

☐	ALVENARIA
▨	ENCHIMENTO
▒	FORRO / SANCA
🟦	AR CONDICIONADO PREVISÃO

PLANTAS DE REFERÊNCIA PARA BASE DE PROJETO

REVISÃO	DATA	DESCRIÇÃO	RESP.
01	08/05/2023	INSERIDO AL46	
00	01/03/2023	EMISSÃO INICIAL	

INCORPORAÇÃO
JERONIMO DA VEIGA
Empreendimentos e Participações Ltda.

CONSTRUÇÃO

PROJETISTA
ADESA ARQUITETURA
RUA PADRE GARCIA VELHO, 73 - CJ. 41
CEP: 05421- 030
FONE: 3032 4355 / 3032 4362

DISCIPLINA
ARQUITETURA

CÓDIGO/OBRA
DUO

FASE
LIBERADO OBRA

EMPREENDIMENTO
DUO
AV_LUZ

ASSUNTO
DETALHAMENTO
ALUMÍNIO_PARTE_II

FOLHA N.º
ARQ
120

RESPONSÁVEL: ADELINO SANTOS
SUPERVISOR: ADELINO SANTOS
COORDENADOR: ALISSA LOPES
REVISÃO: R01
PROJETISTA
ARQUIVO: DUO-ARQ-LO-120-DET-ALU-R01.dwg
ESCALA: 1:25
DATA: 08/03/2023

DIREITOS AUTORAIS RESERVADO A REPRODUÇÃO TOTAL OU PARCIAL SEM PRÉVIA AUTORIZAÇÃO, CONFORME RESOLUÇÃO N° 67, DE 5 DE DEZEMBRO DE 2013