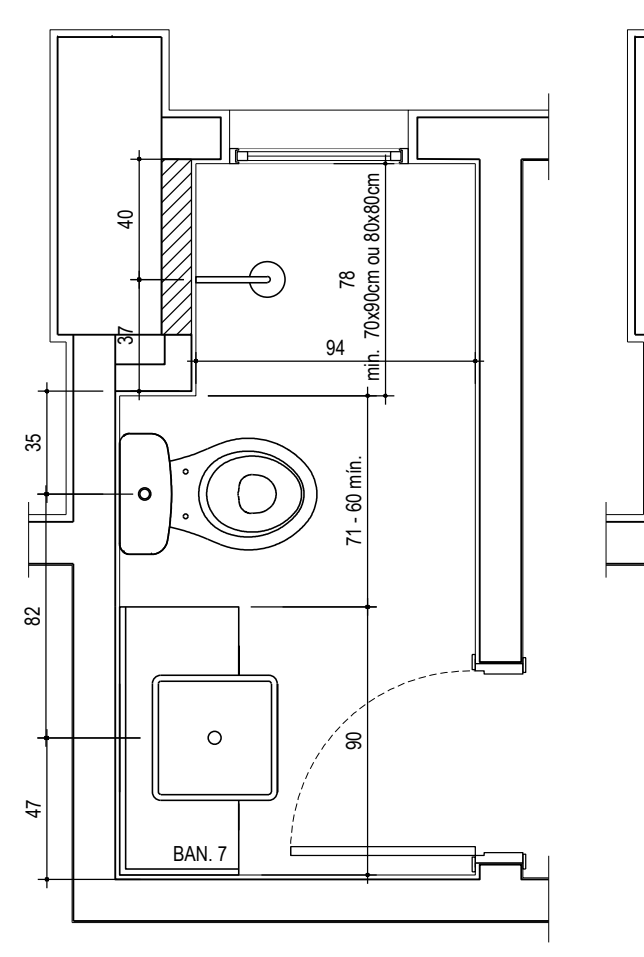

PLANTA BANHO 1 - HIDRÁULICA
TORRE A: APARTAMENTO FINAL 05
TORRE B: APARTAMENTO FINAL 01
5º PAVIMENTO

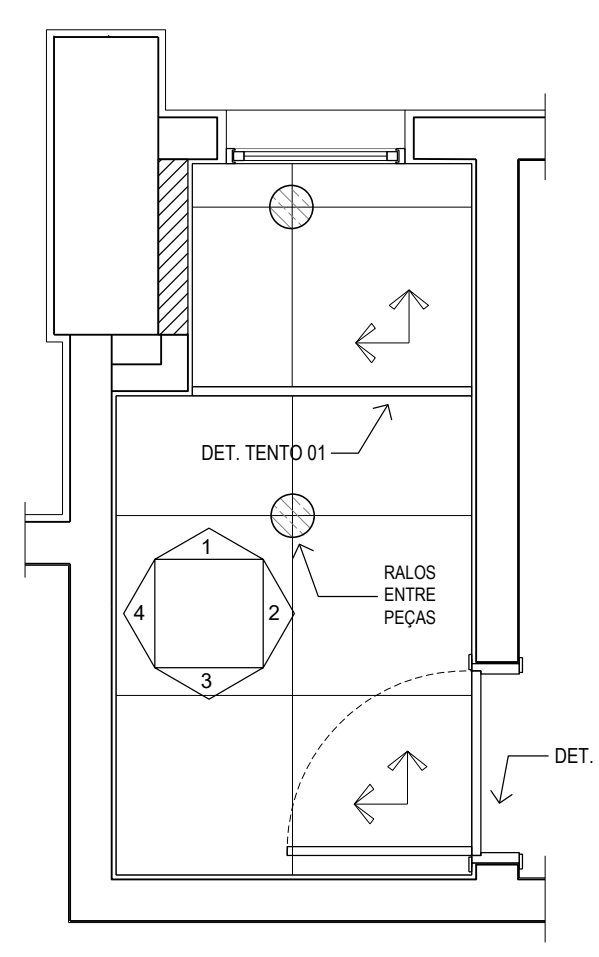
DET. TENTO 01
RALOS
ENTRE
PEÇAS
DET. BAG. 01

PLANTA BANHO 1 - PISO
TORRE A: APARTAMENTO FINAL 05
TORRE B: APARTAMENTO FINAL 01
5º PAVIMENTO

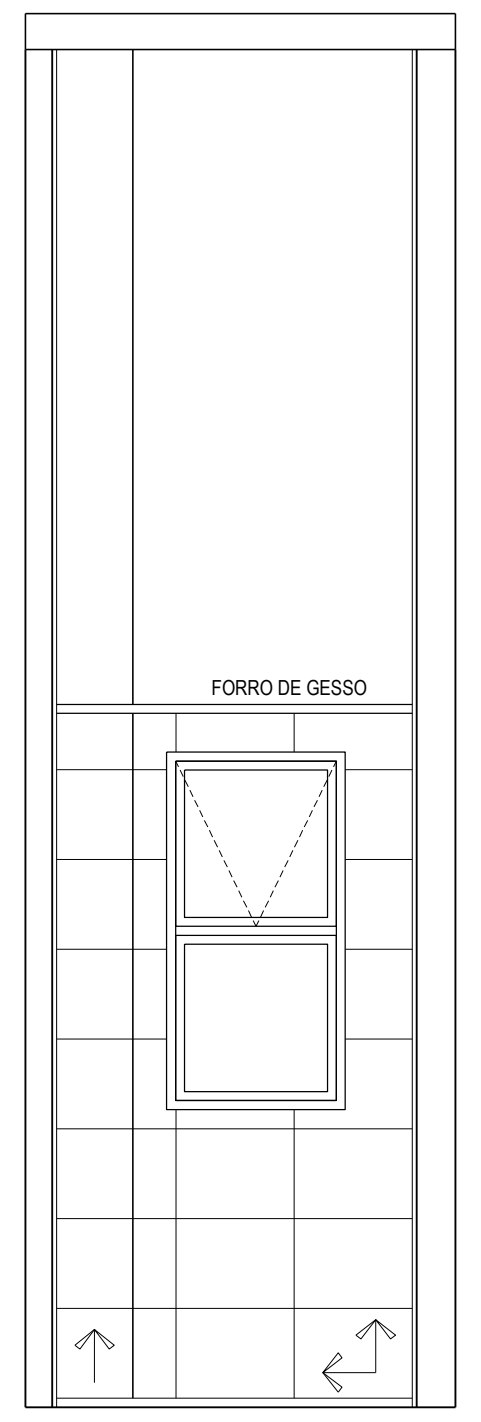
FORRO DE GESSO
VISTA 01 - BANHO 1
TORRE A: APARTAMENTO FINAL 05
TORRE B: APARTAMENTO FINAL 01
5º PAVIMENTO

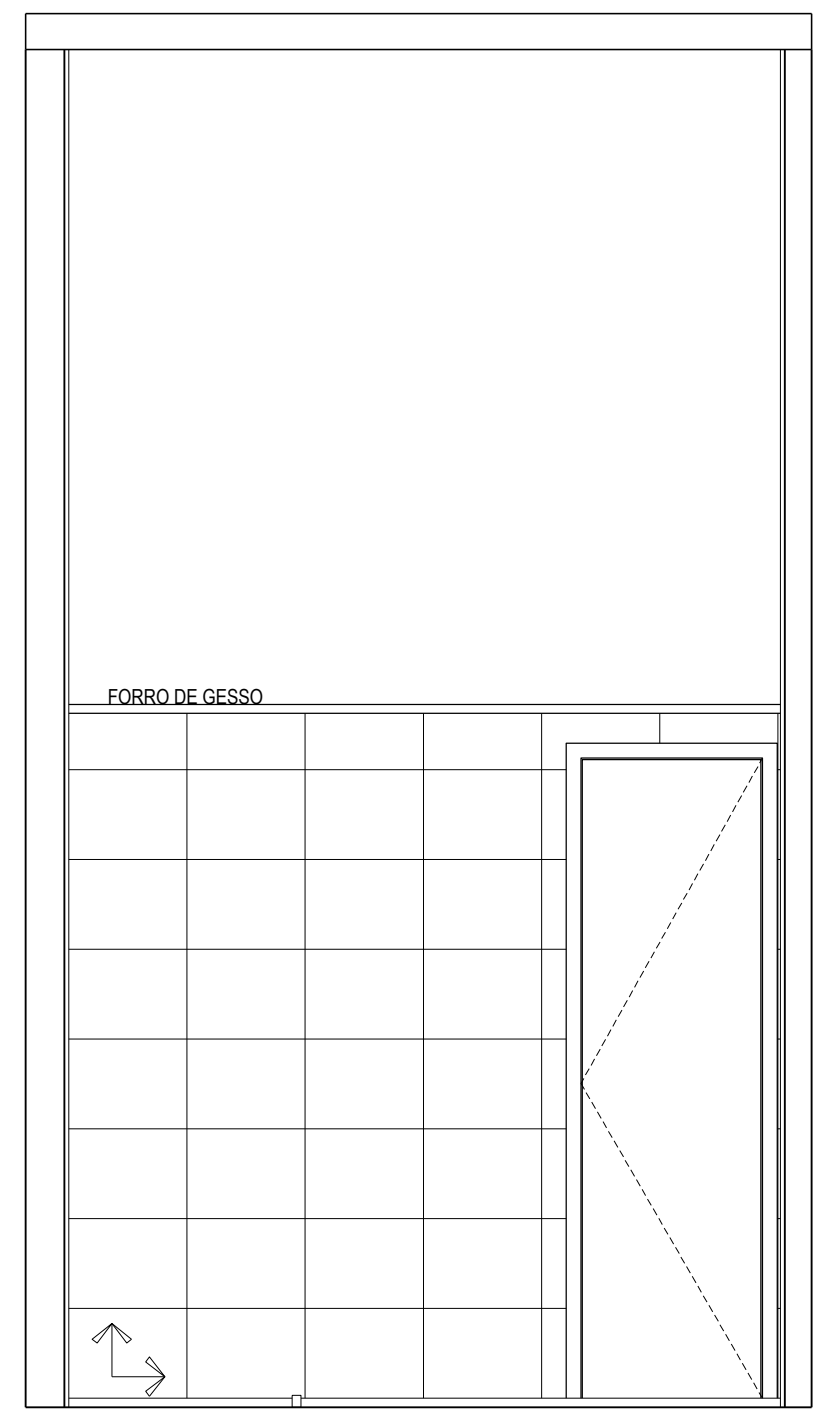
FORRO DE GESSO
VISTA 02 - BANHO 1
TORRE A: APARTAMENTO FINAL 05
TORRE B: APARTAMENTO FINAL 01
5º PAVIMENTO

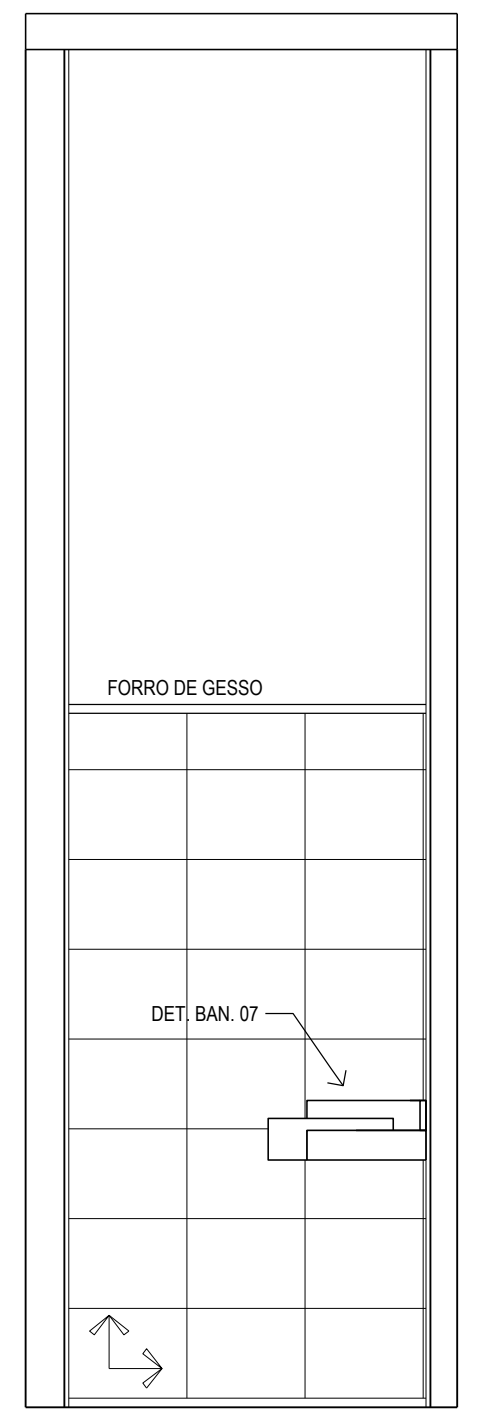
FORRO DE GESSO
DET. BAN. 07
VISTA 03 - BANHO 1
TORRE A: APARTAMENTO FINAL 05
TORRE B: APARTAMENTO FINAL 01
5º PAVIMENTO

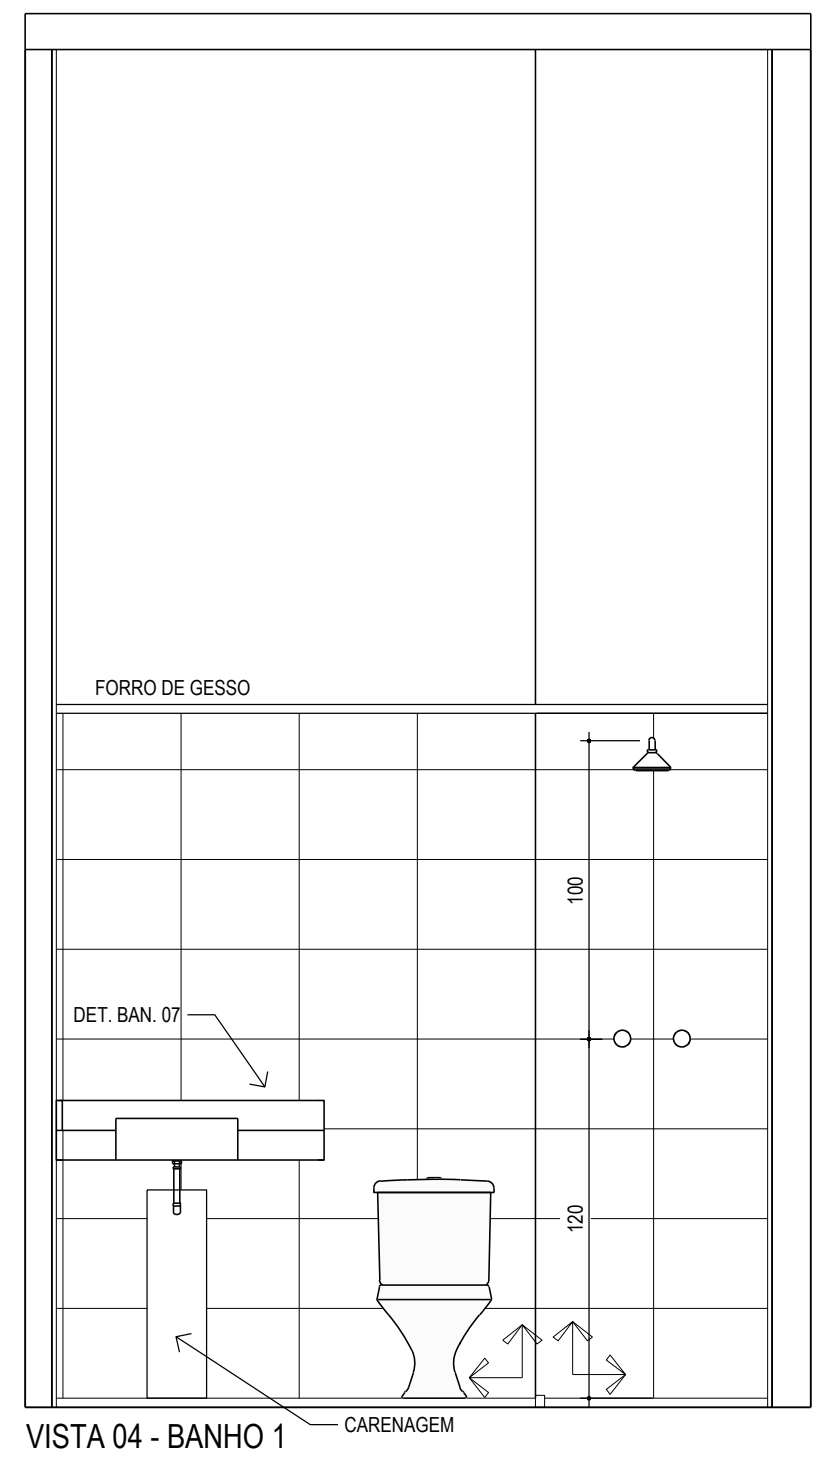
FORRO DE GESSO
DET. BAN. 07
120
CARENAGEM
VISTA 04 - BANHO 1
TORRE A: APARTAMENTO FINAL 05
TORRE B: APARTAMENTO FINAL 01
5º PAVIMENTO

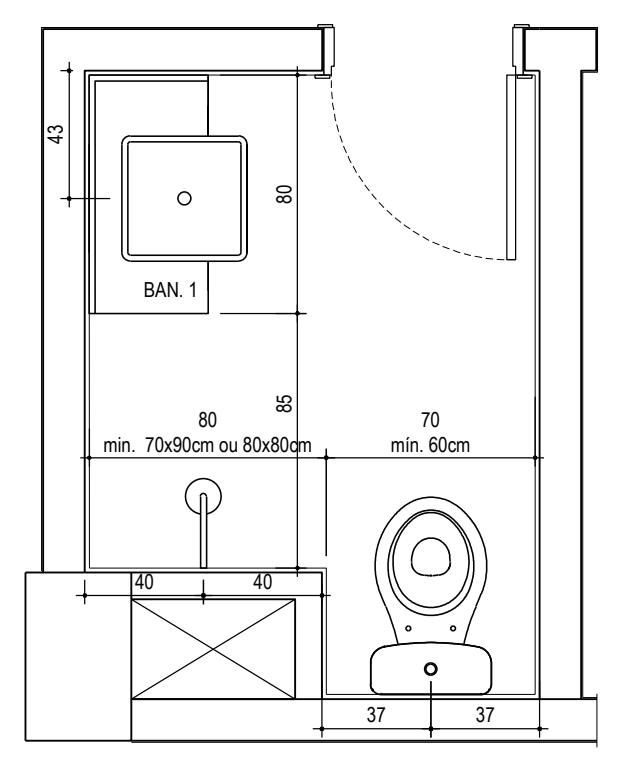
BAN. 1
80
min. 70x90cm ou 80x80cm
70
mín. 60cm
40
40
37
37
PLANTA BANHO 2 - HIDRÁULICA
TORRE A: APARTAMENTO FINAL 05
TORRE B: APARTAMENTO FINAL 01
5º PAVIMENTO

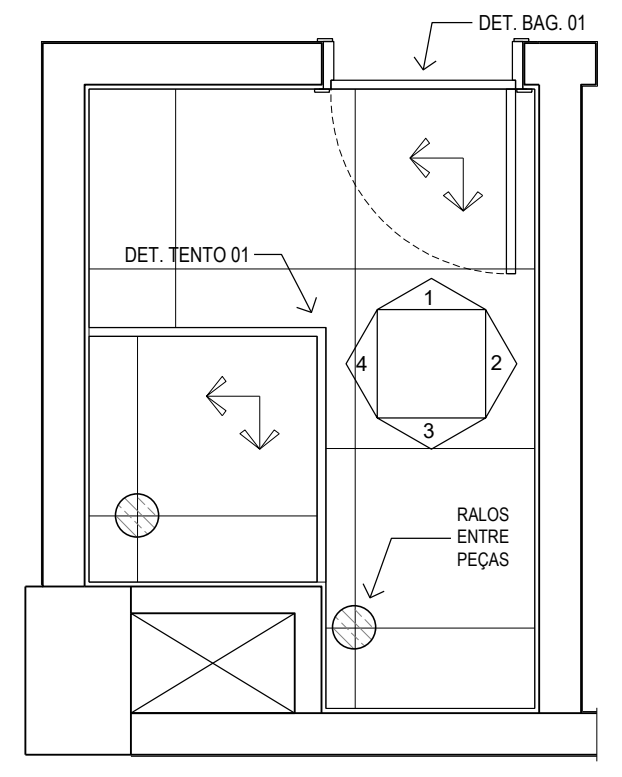
DET. BAG. 01
DET. TENTO 01
RALOS
ENTRE
PEÇAS
PLANTA BANHO 2 - PISO
TORRE A: APARTAMENTO FINAL 05
TORRE B: APARTAMENTO FINAL 01
5º PAVIMENTO

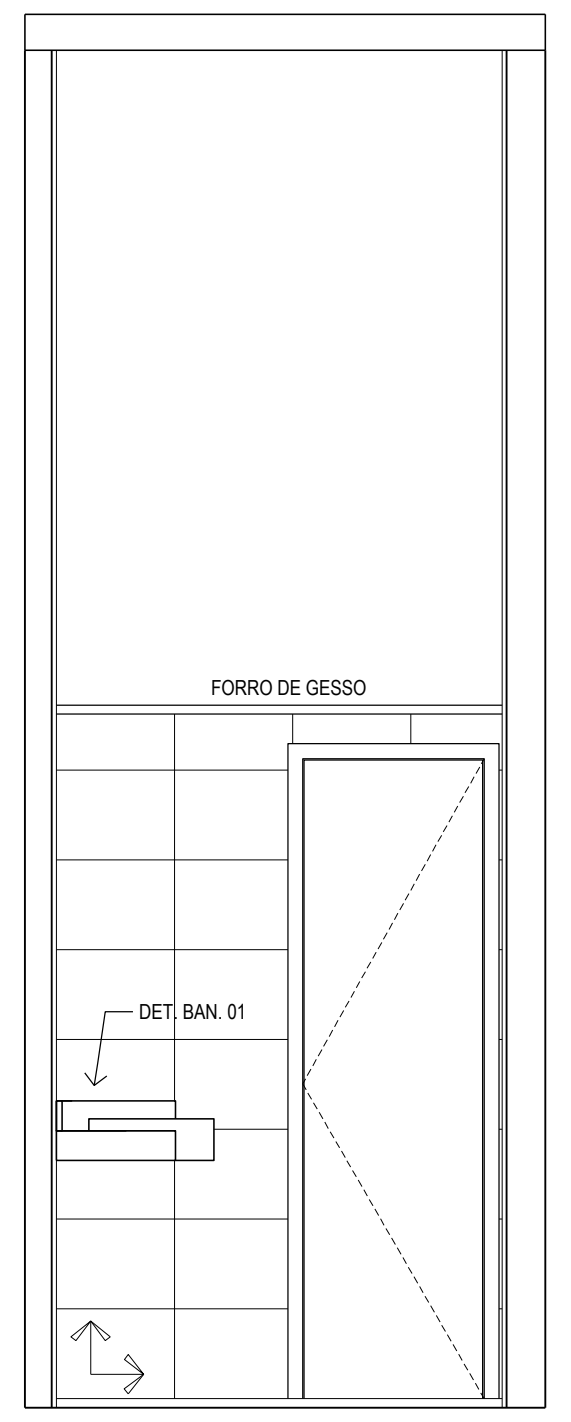
FORRO DE GESSO
DET. BAN. 01
VISTA 01 - BANHO 2
TORRE A: APARTAMENTO FINAL 05
TORRE B: APARTAMENTO FINAL 01
5º PAVIMENTO

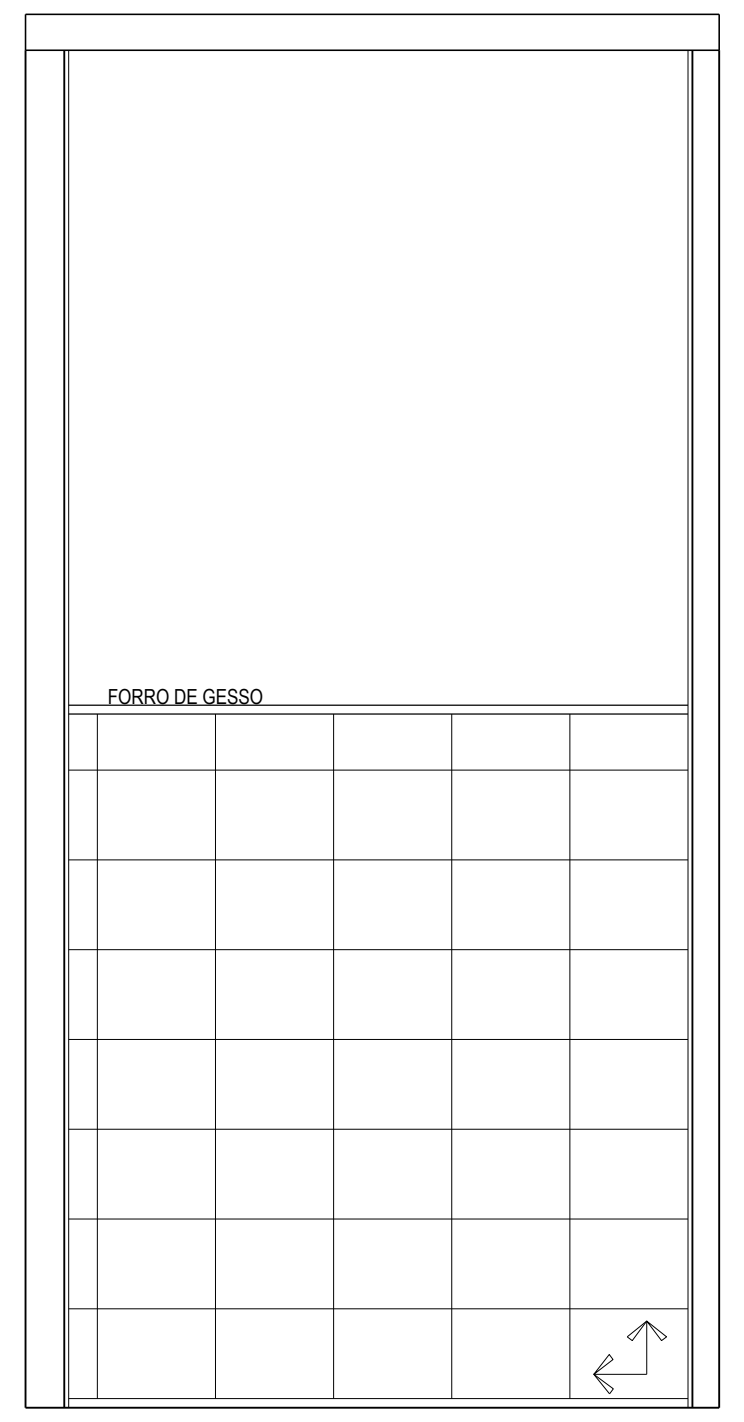
FORRO DE GESSO
VISTA 02 - BANHO 2
TORRE A: APARTAMENTO FINAL 05
TORRE B: APARTAMENTO FINAL 01
5º PAVIMENTO

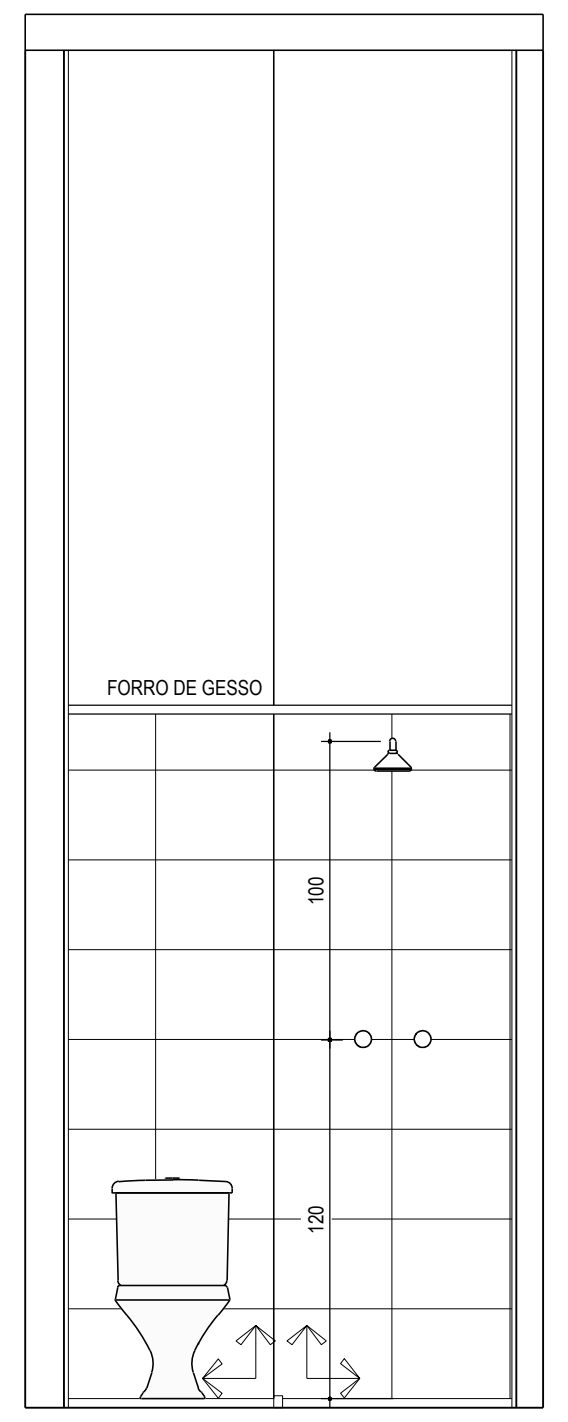
FORRO DE GESSO
120
VISTA 03 - BANHO 2
TORRE A: APARTAMENTO FINAL 05
TORRE B: APARTAMENTO FINAL 01
5º PAVIMENTO

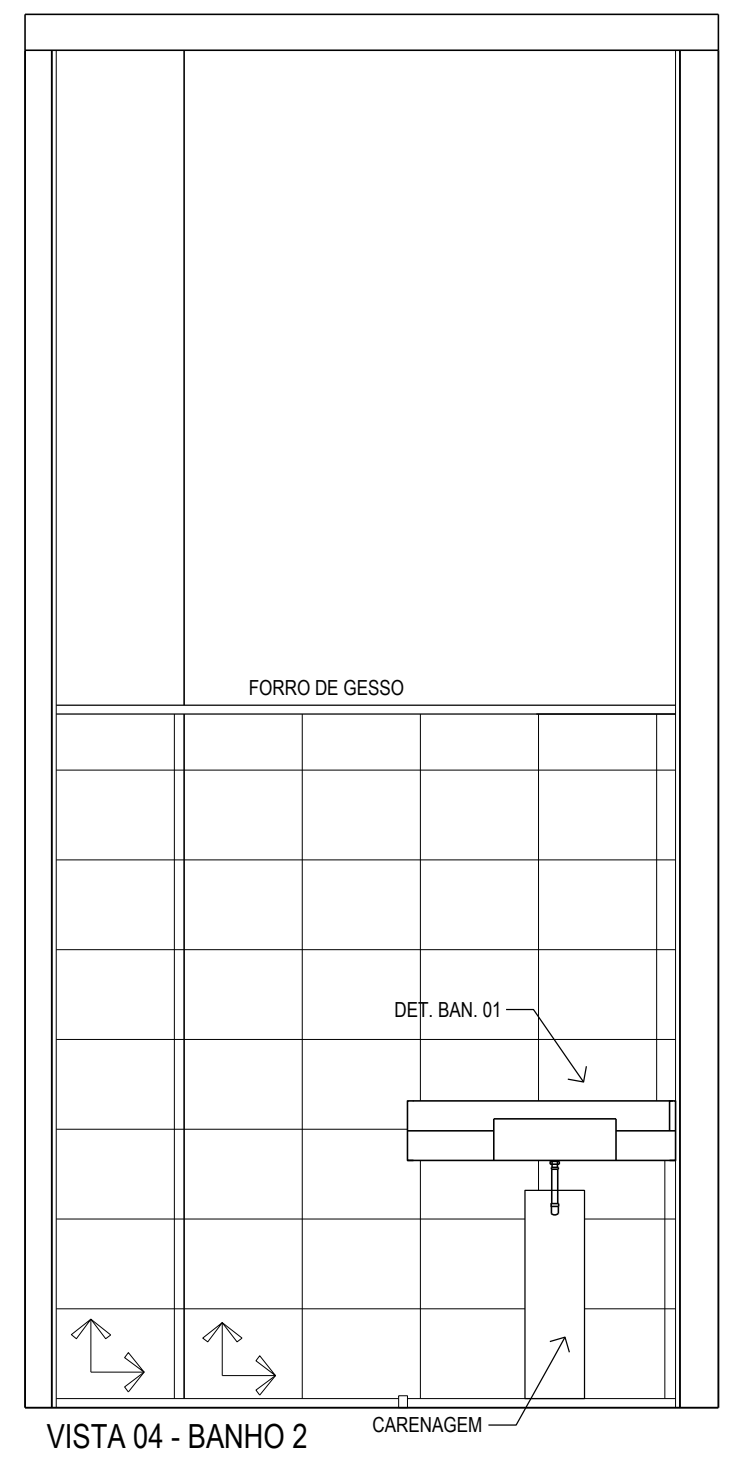
FORRO DE GESSO
DET. BAN. 01
CARENAGEM
VISTA 04 - BANHO 2
TORRE A: APARTAMENTO FINAL 05
TORRE B: APARTAMENTO FINAL 01
5º PAVIMENTO

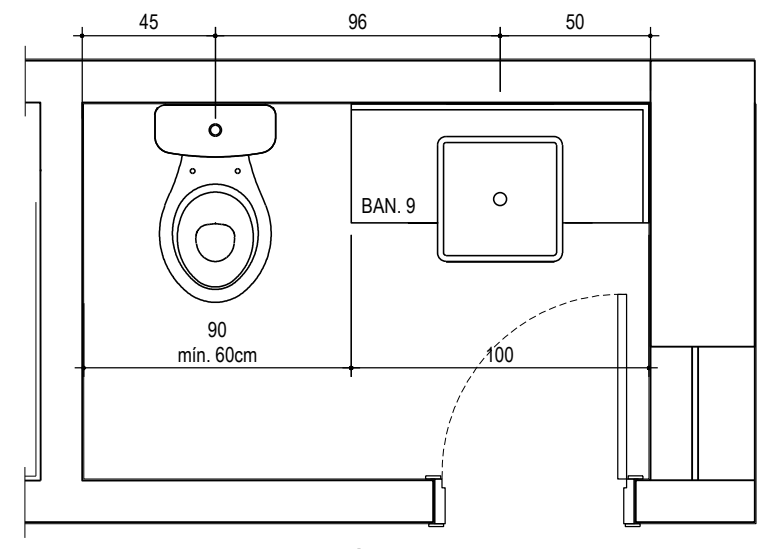
45
96
55
BAN. 9
90
mín. 60cm
100
PLANTA LAVABO - HIDRÁULICA
TORRE A: APARTAMENTO FINAL 02
TORRE B: APARTAMENTO FINAL 04
5º PAVIMENTO

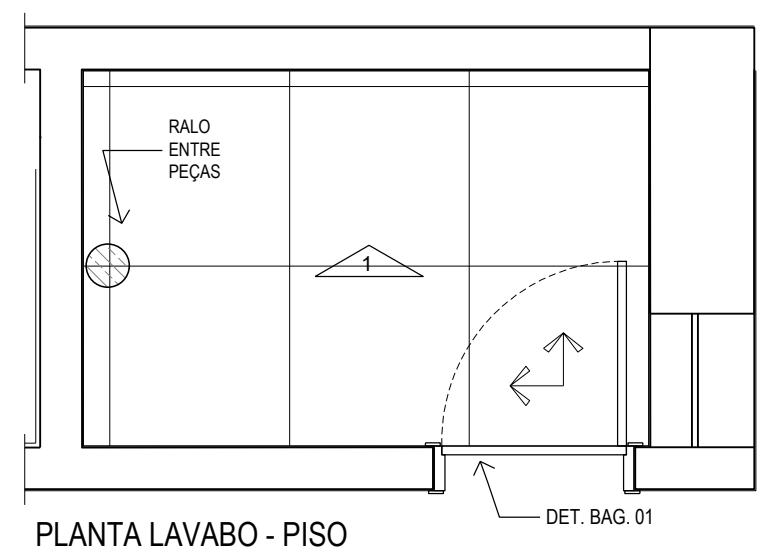
RALO
ENTRE
PEÇAS
1
DET. BAG. 01
PLANTA LAVABO - PISO
TORRE A: APARTAMENTO FINAL 02
TORRE B: APARTAMENTO FINAL 04
5º PAVIMENTO

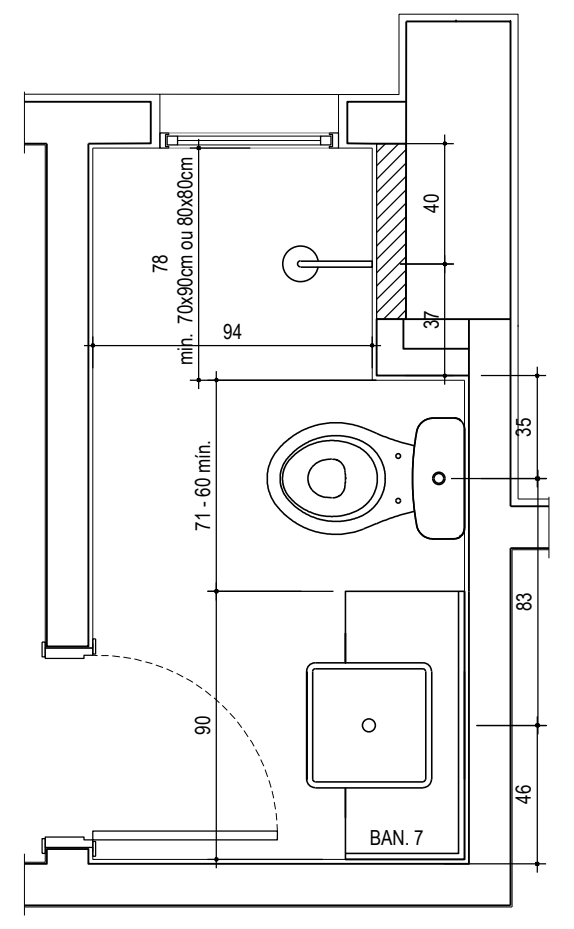
BAN. 7
90
83
46
PLANTA BANHO 1 - HIDRÁULICA
TORRE A: APARTAMENTO FINAL 01
TORRE B: APARTAMENTO FINAL 05
5º PAVIMENTO

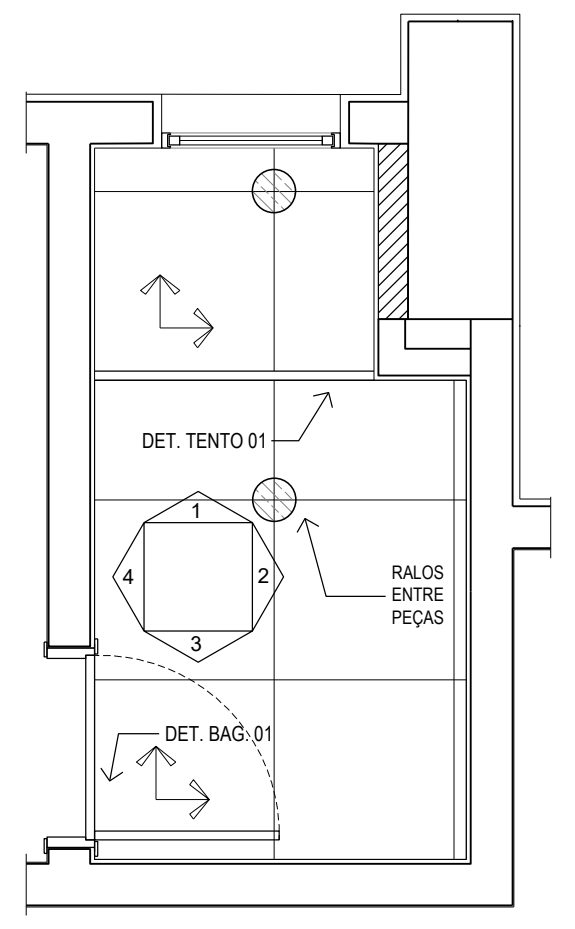
DET. TENTO 01
RALOS
ENTRE
PEÇAS
DET. BAG. 01
PLANTA BANHO 1 - PISO
TORRE A: APARTAMENTO FINAL 01
TORRE B: APARTAMENTO FINAL 05
5º PAVIMENTO

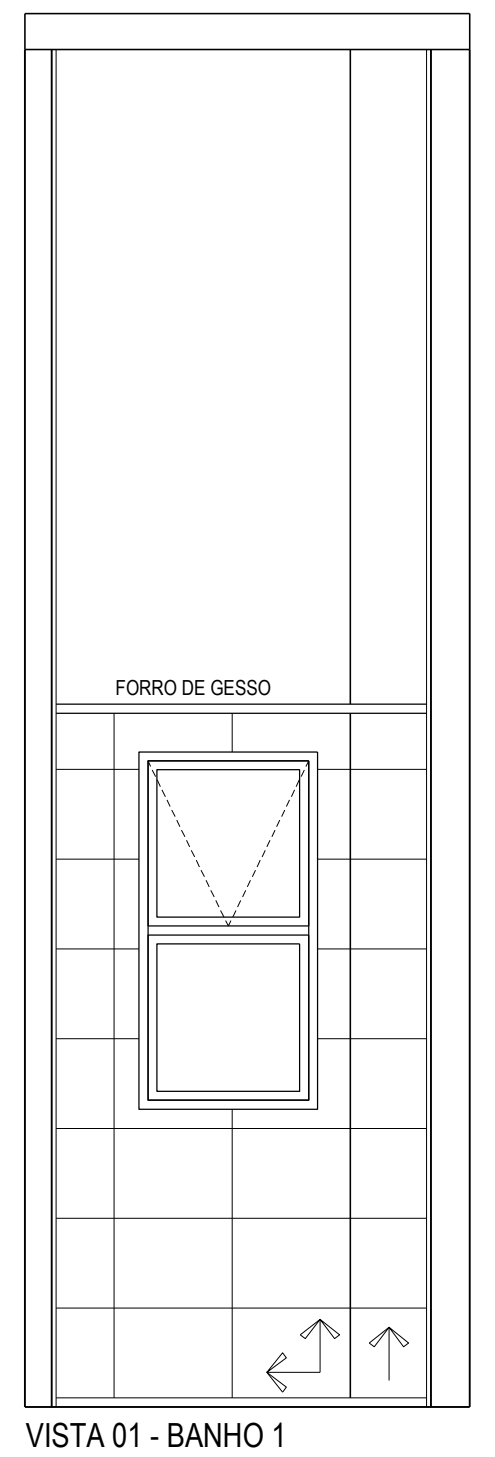
FORRO DE GESSO
VISTA 01 - BANHO 1
TORRE A: APARTAMENTO FINAL 01
TORRE B: APARTAMENTO FINAL 05
5º PAVIMENTO

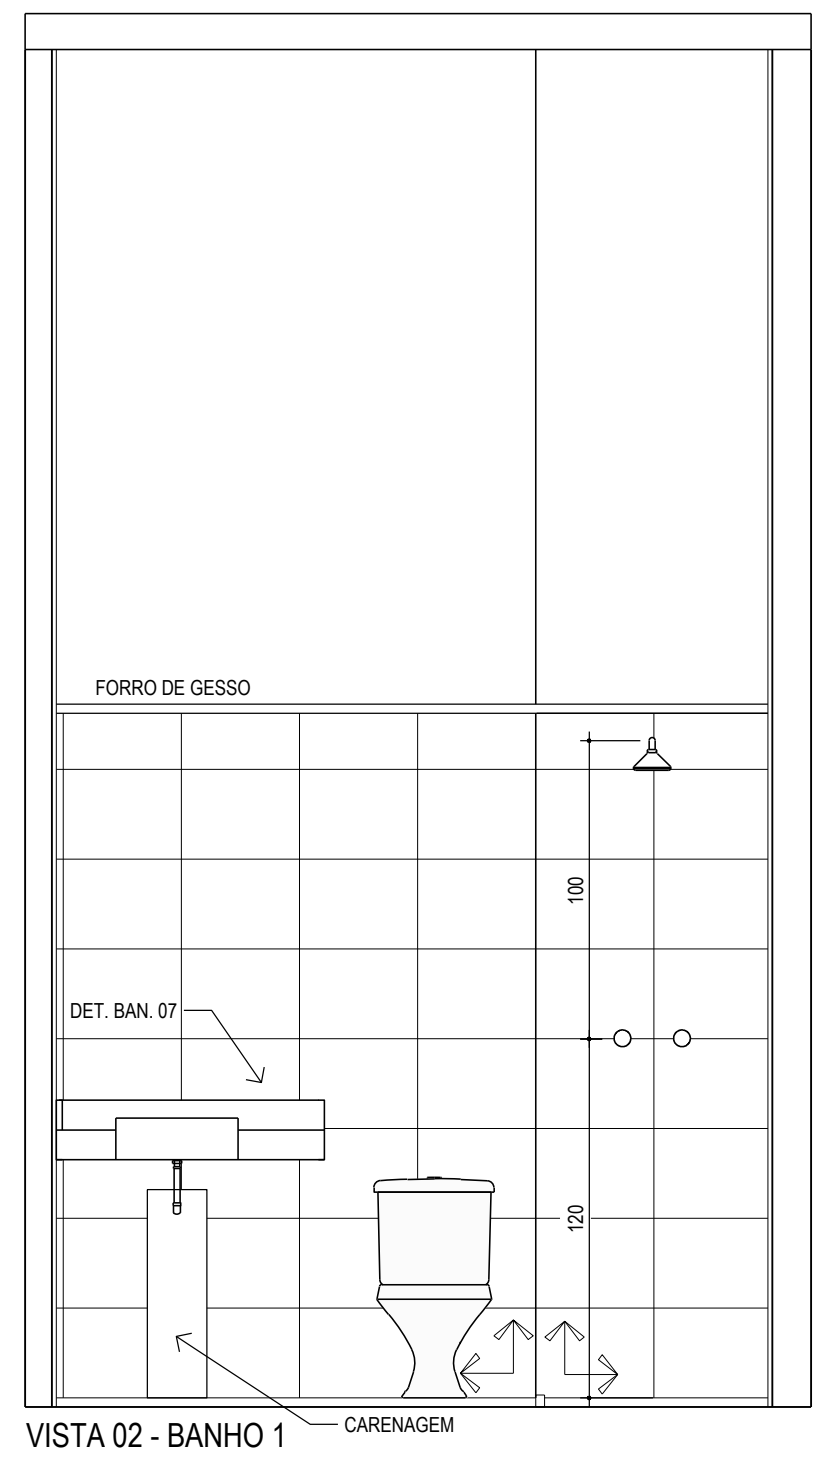
FORRO DE GESSO
DET. BAN. 07
120
CARENAGEM
VISTA 02 - BANHO 1
TORRE A: APARTAMENTO FINAL 01
TORRE B: APARTAMENTO FINAL 05
5º PAVIMENTO

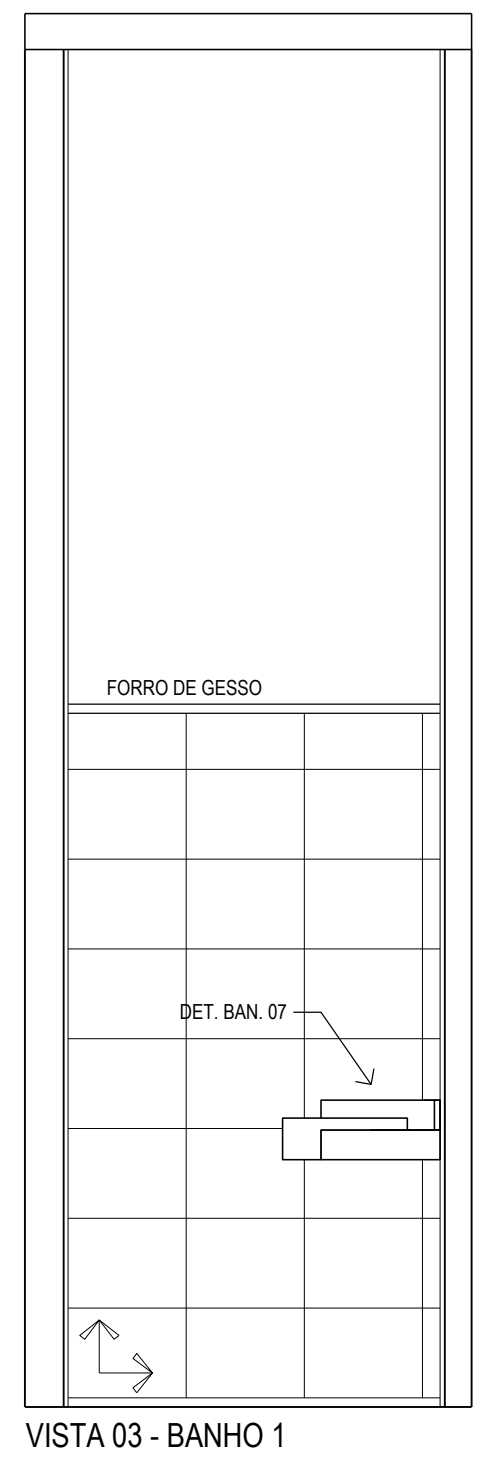
FORRO DE GESSO
DET. BAN. 07
VISTA 03 - BANHO 1
TORRE A: APARTAMENTO FINAL 01
TORRE B: APARTAMENTO FINAL 05
5º PAVIMENTO

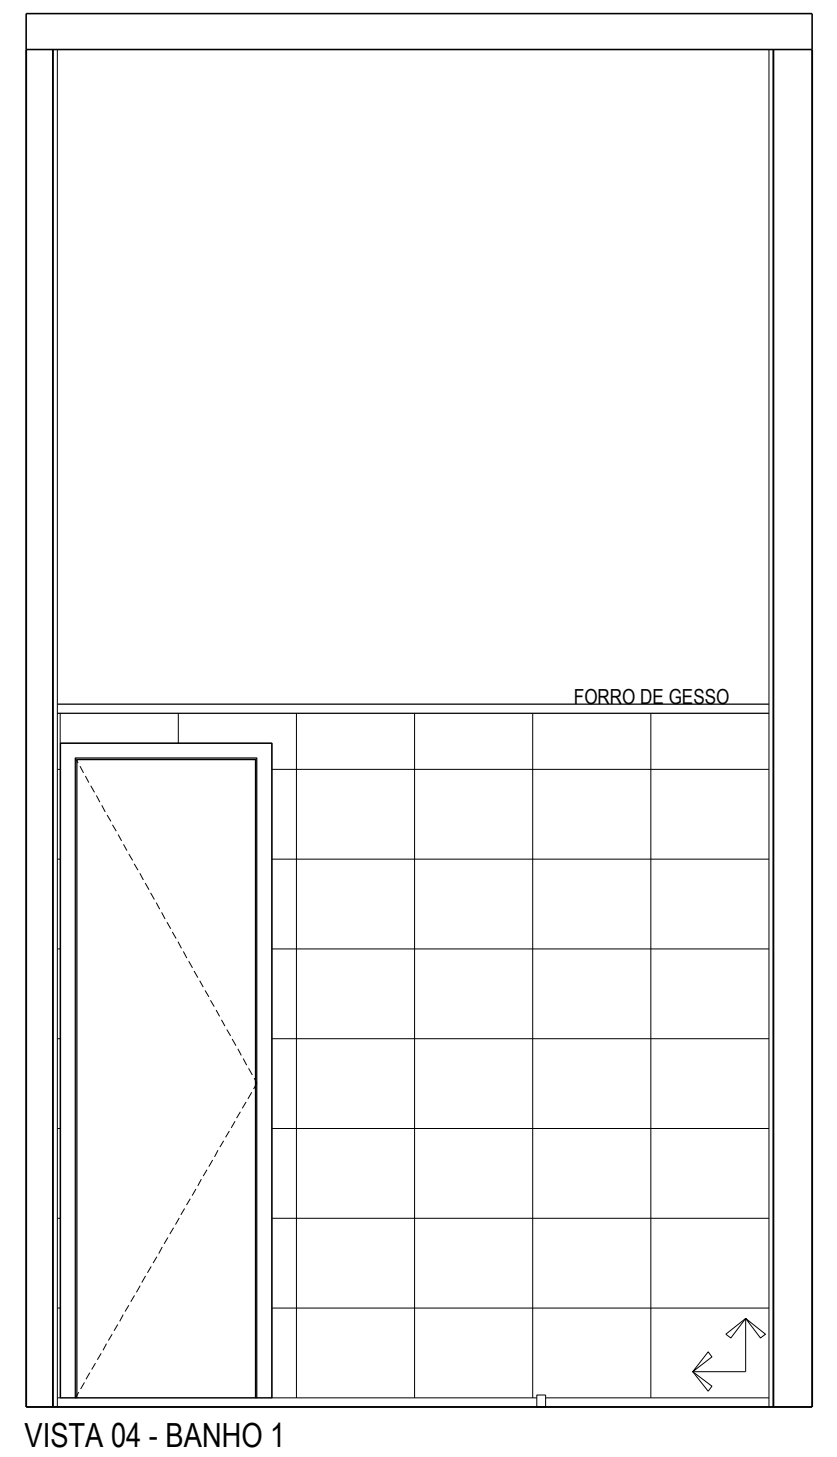
FORRO DE GESSO
VISTA 04 - BANHO 1
TORRE A: APARTAMENTO FINAL 01
TORRE B: APARTAMENTO FINAL 05
5º PAVIMENTO

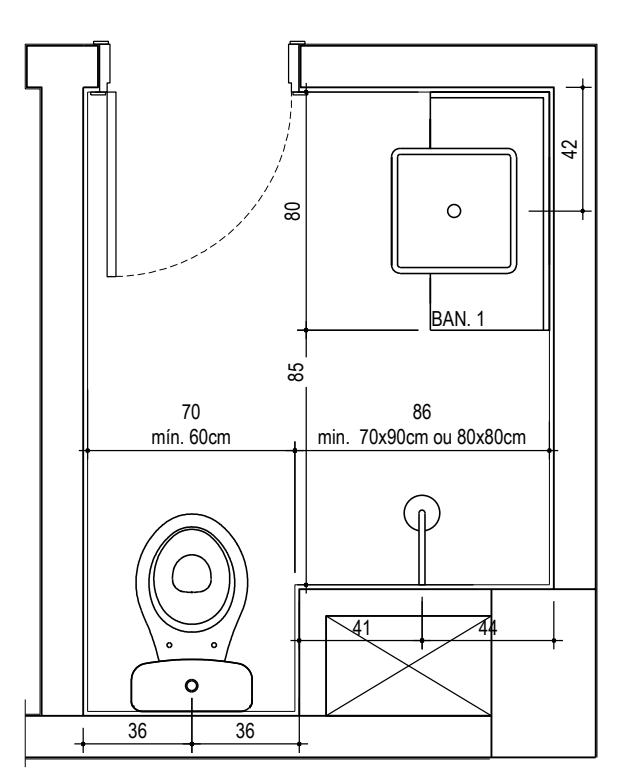
BAN. 1
70
mín. 60cm
86
min. 70x90cm ou 80x80cm
36
36
41
44
PLANTA BANHO 2 - HIDRÁULICA
TORRE A: APARTAMENTO FINAL 01
TORRE B: APARTAMENTO FINAL 05
5º PAVIMENTO

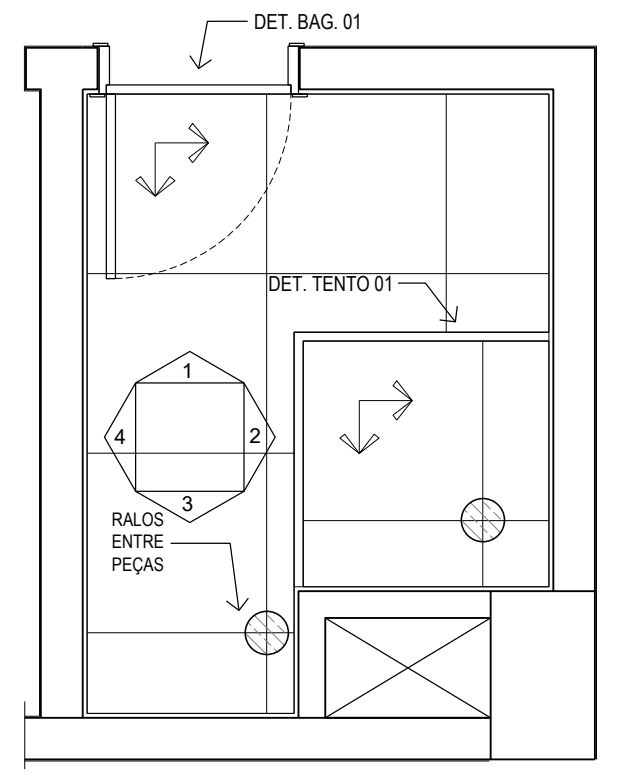
DET. BAG. 01
DET. TENTO 01
RALOS
ENTRE
PEÇAS
PLANTA BANHO 2 - PISO
TORRE A: APARTAMENTO FINAL 01
TORRE B: APARTAMENTO FINAL 05
5º PAVIMENTO

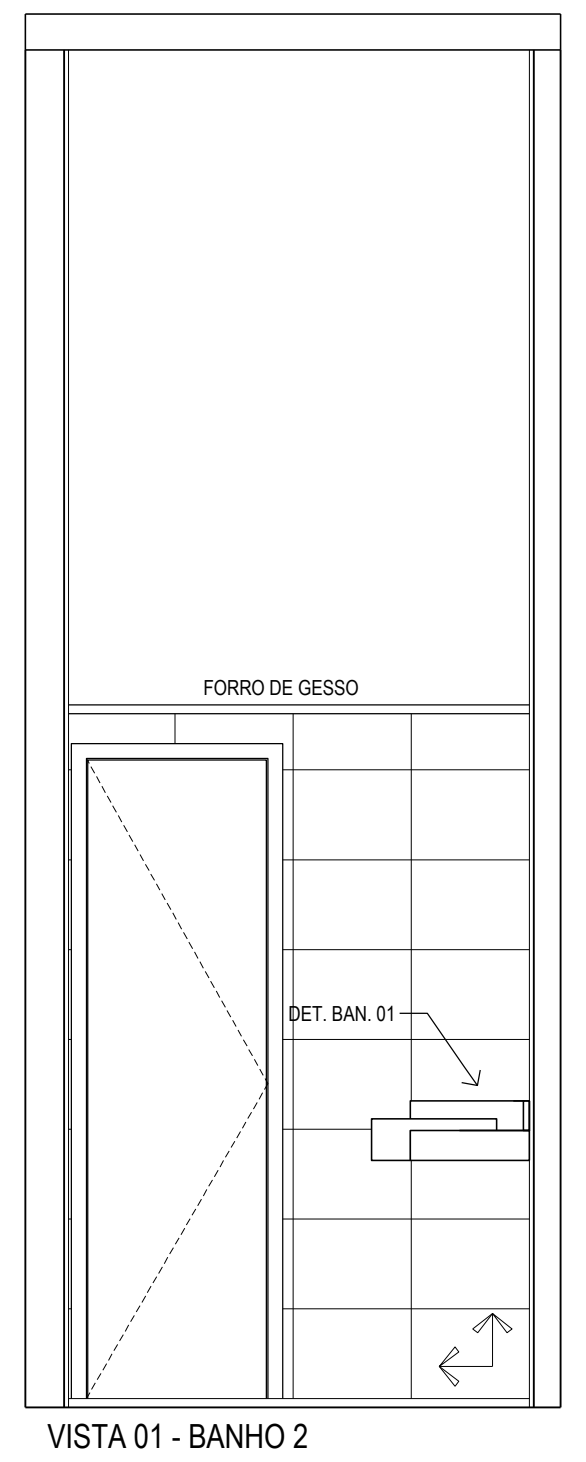
FORRO DE GESSO
DET. BAN. 01
VISTA 01 - BANHO 2
TORRE A: APARTAMENTO FINAL 01
TORRE B: APARTAMENTO FINAL 05
5º PAVIMENTO

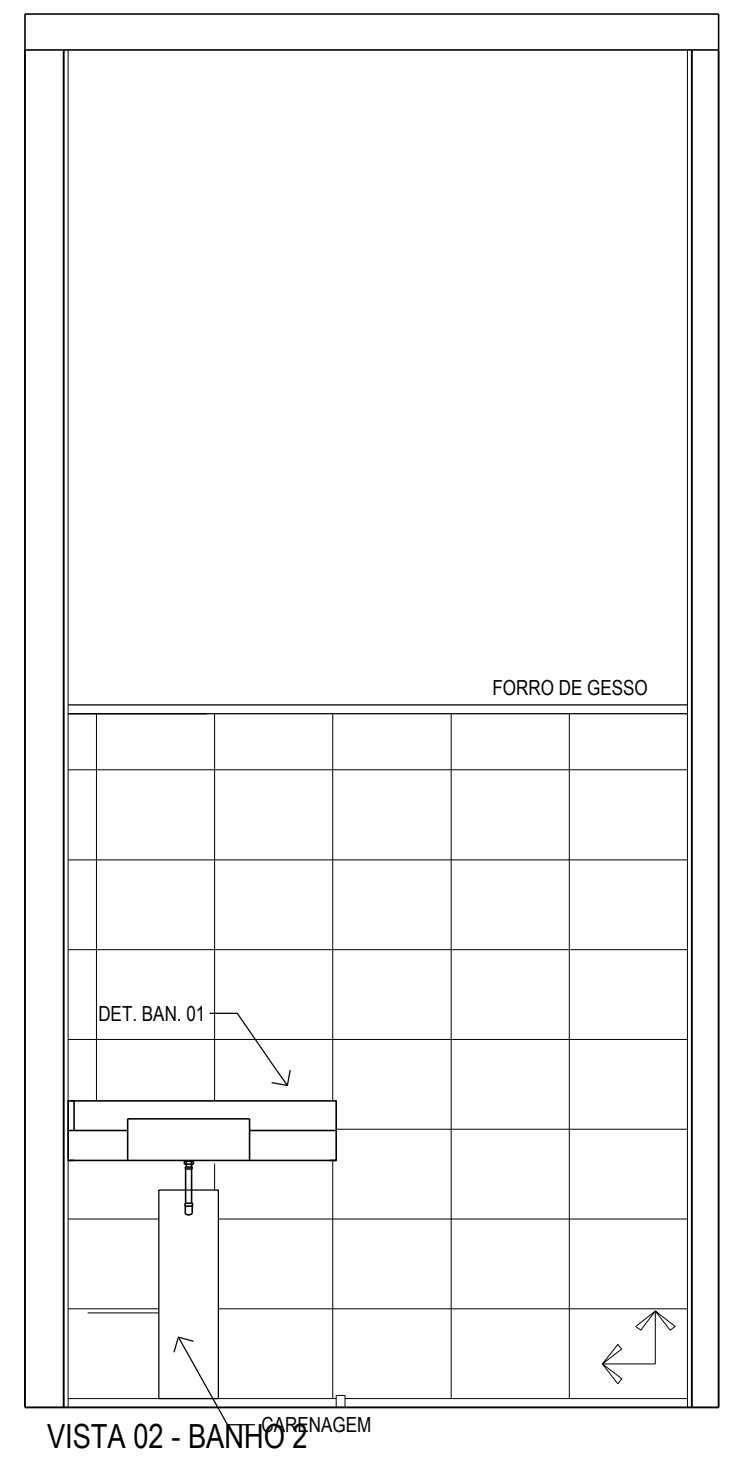
FORRO DE GESSO
DET. BAN. 01
CARENAGEM
VISTA 02 - BANHO 2
TORRE A: APARTAMENTO FINAL 01
TORRE B: APARTAMENTO FINAL 05
5º PAVIMENTO

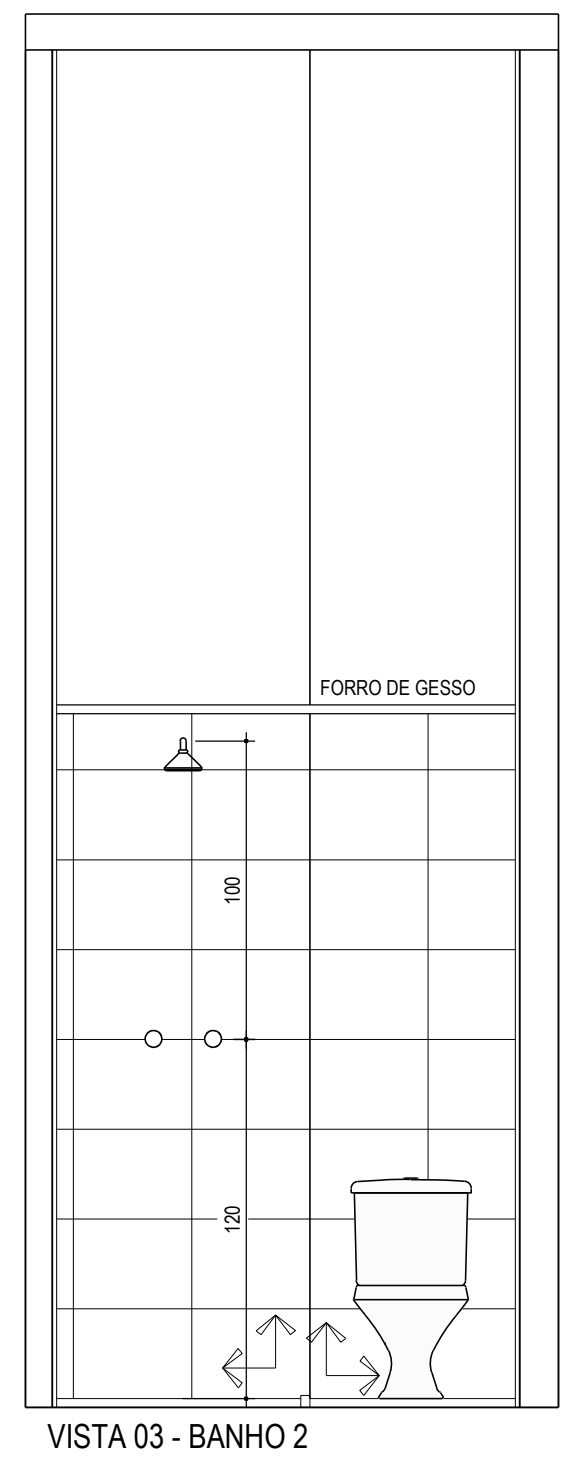
FORRO DE GESSO
120
VISTA 03 - BANHO 2
TORRE A: APARTAMENTO FINAL 01
TORRE B: APARTAMENTO FINAL 05
5º PAVIMENTO

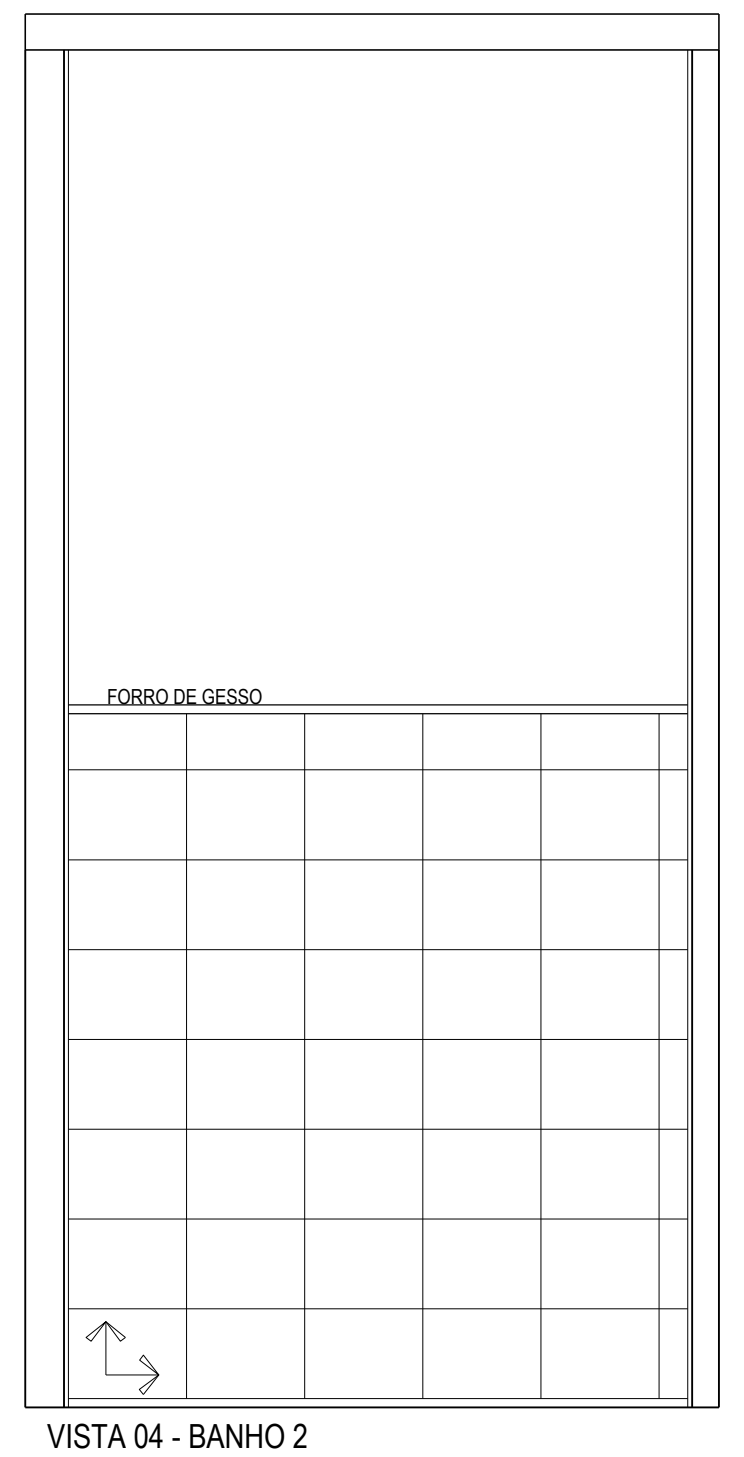
FORRO DE GESSO
VISTA 04 - BANHO 2
TORRE A: APARTAMENTO FINAL 01
TORRE B: APARTAMENTO FINAL 05
5º PAVIMENTO

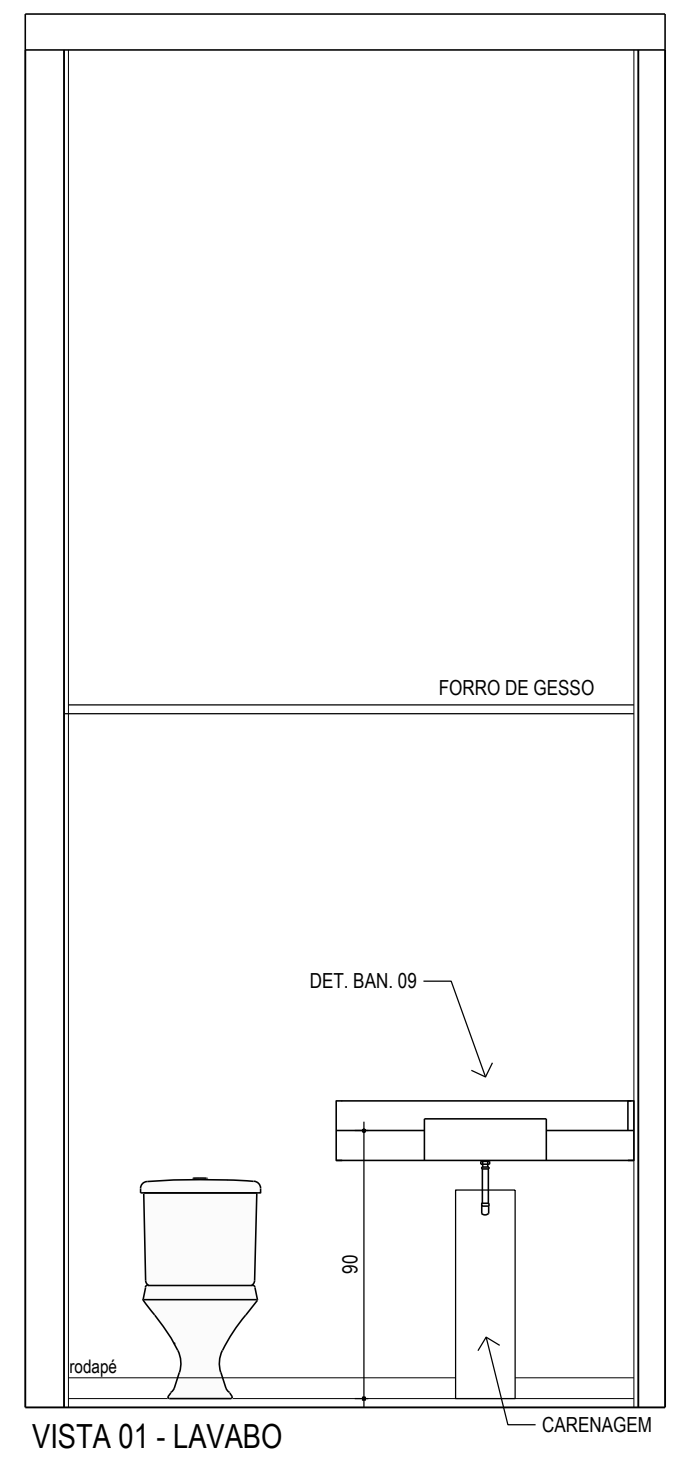
FORRO DE GESSO
DET. BAN. 09
90
rodapé
CARENAGEM
VISTA 01 - LAVABO
TORRE A: APARTAMENTO FINAL 02
TORRE B: APARTAMENTO FINAL 04
5º PAVIMENTO

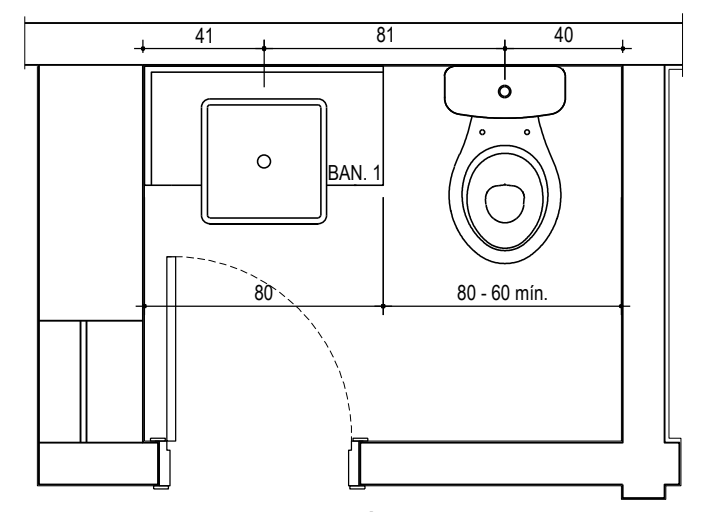
41
81
40
BAN. 1
80
80 - 60 min.
PLANTA LAVABO - HIDRÁULICA
TORRE A: APARTAMENTO FINAL 04
TORRE B: APARTAMENTO FINAL 02
5º PAVIMENTO

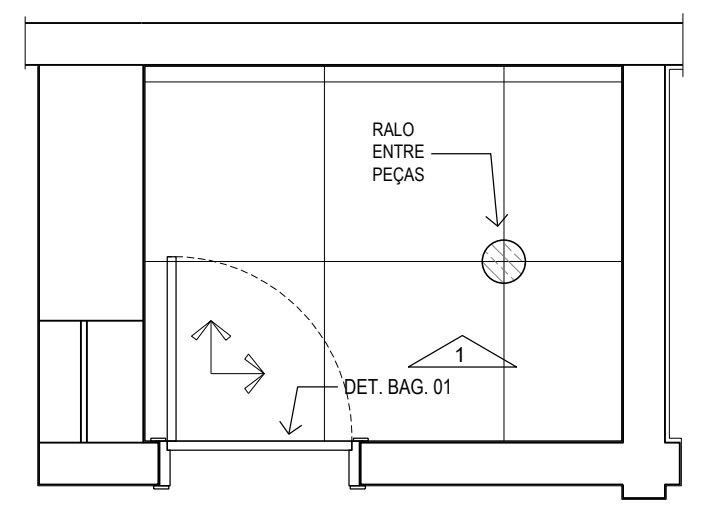
RALO
ENTRE
PEÇAS
1
DET. BAG. 01
PLANTA LAVABO -PISO
TORRE A: APARTAMENTO FINAL 04
TORRE B: APARTAMENTO FINAL 02
5º PAVIMENTO

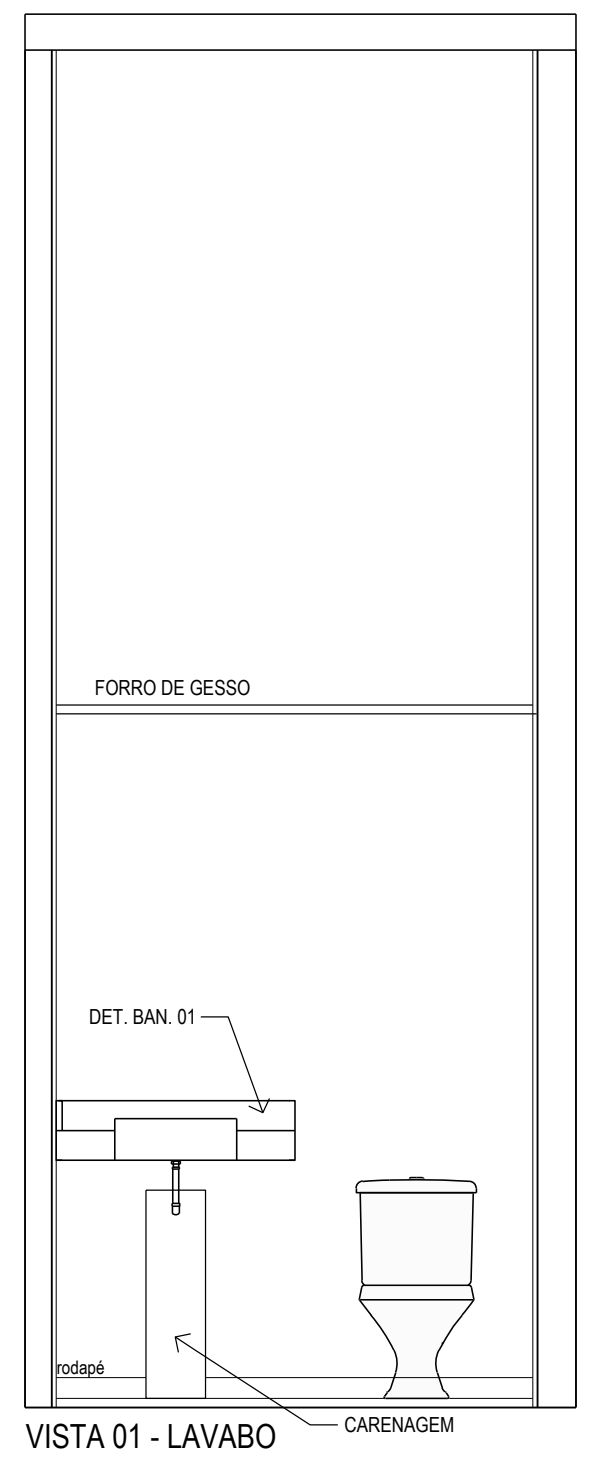
FORRO DE GESSO
DET. BAN. 01
rodapé
CARENAGEM
VISTA 01 - LAVABO
TORRE A: APARTAMENTO FINAL 04
TORRE B: APARTAMENTO FINAL 02
5º PAVIMENTO

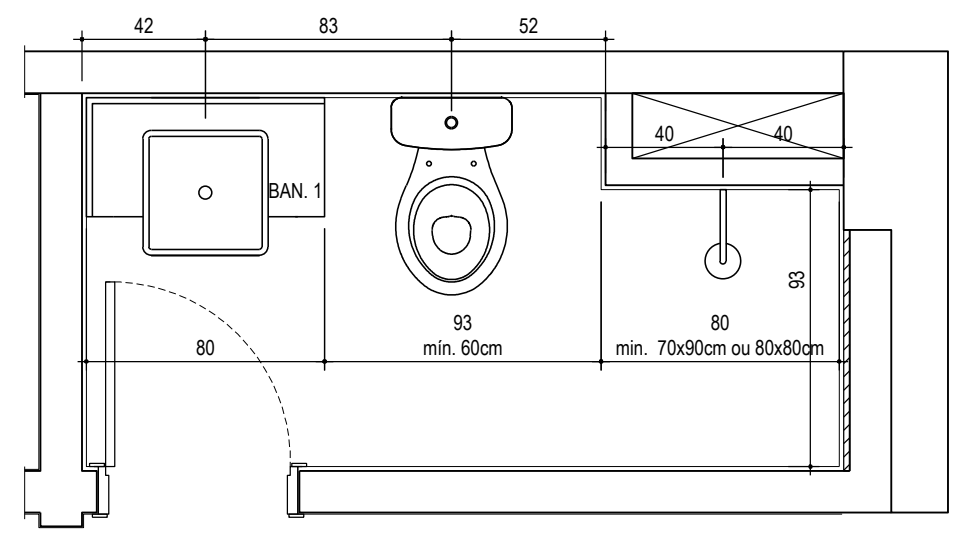
42
83
52
BAN. 1
80
93
mín. 60cm
80
min. 70x90cm ou 80x80cm
93
PLANTA BANHO - HIDRÁULICA
TORRE A: APARTAMENTO FINAL 04
TORRE B: APARTAMENTO FINAL 02
5º PAVIMENTO

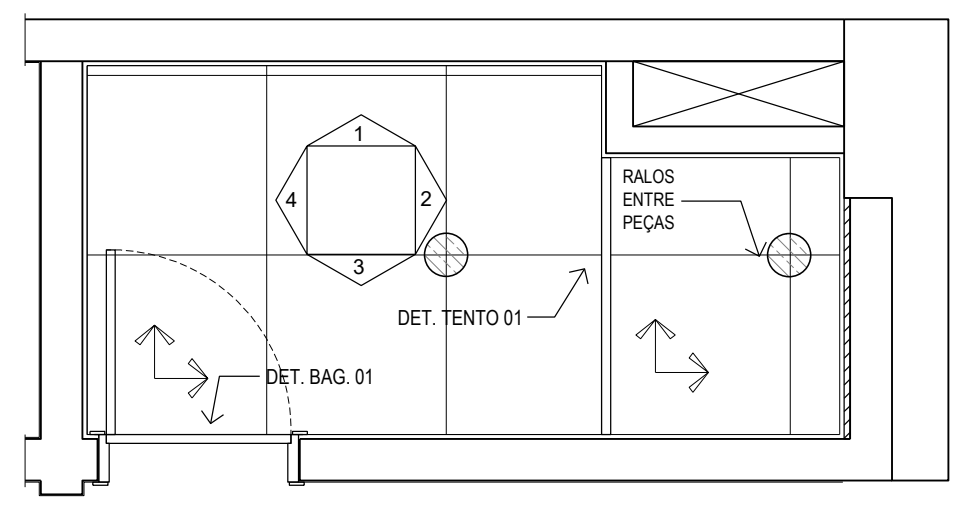
RALOS
ENTRE
PEÇAS
DET. TENTO 01
DET. BAG. 01
PLANTA BANHO - PISO
TORRE A: APARTAMENTO FINAL 04
TORRE B: APARTAMENTO FINAL 02
5º PAVIMENTO

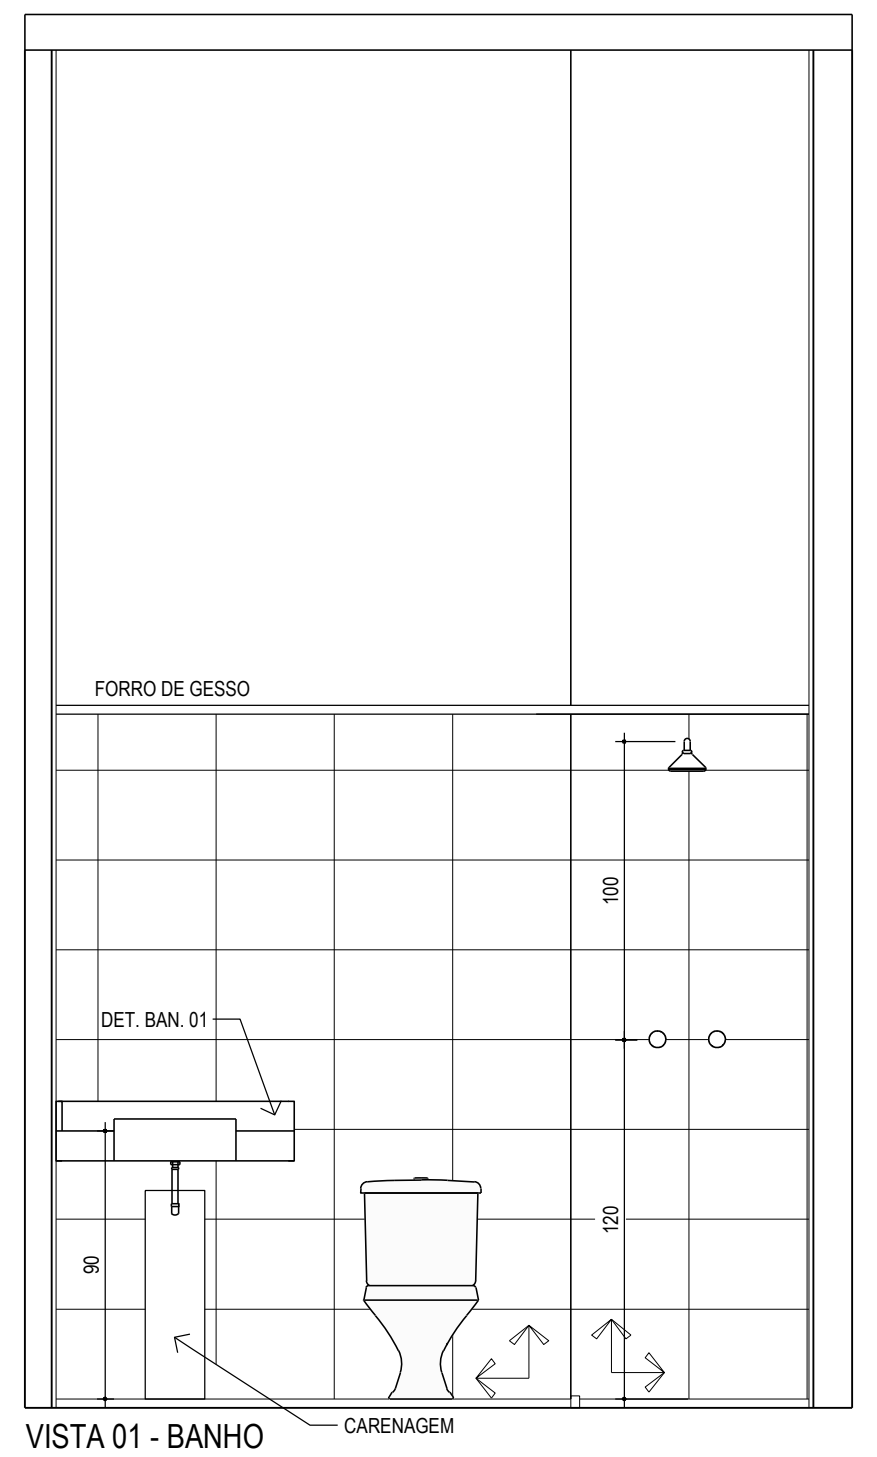
FORRO DE GESSO
DET. BAN. 01
90
120
CARENAGEM
VISTA 01 - BANHO
TORRE A: APARTAMENTO FINAL 04
TORRE B: APARTAMENTO FINAL 02
5º PAVIMENTO

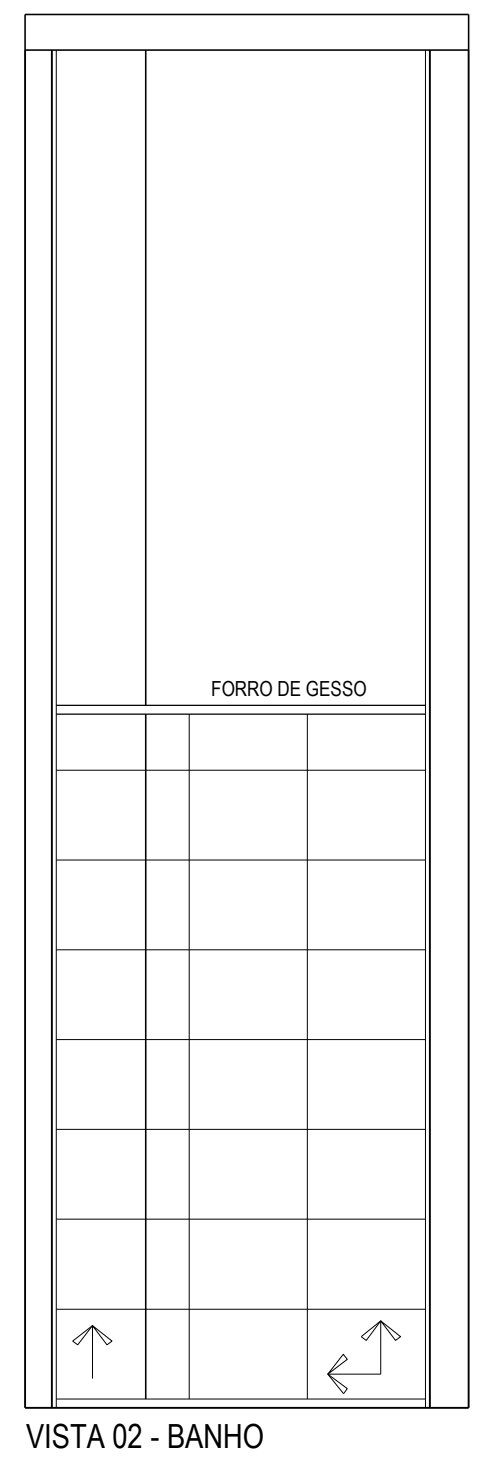
FORRO DE GESSO
VISTA 02 - BANHO
TORRE A: APARTAMENTO FINAL 04
TORRE B: APARTAMENTO FINAL 02
5º PAVIMENTO

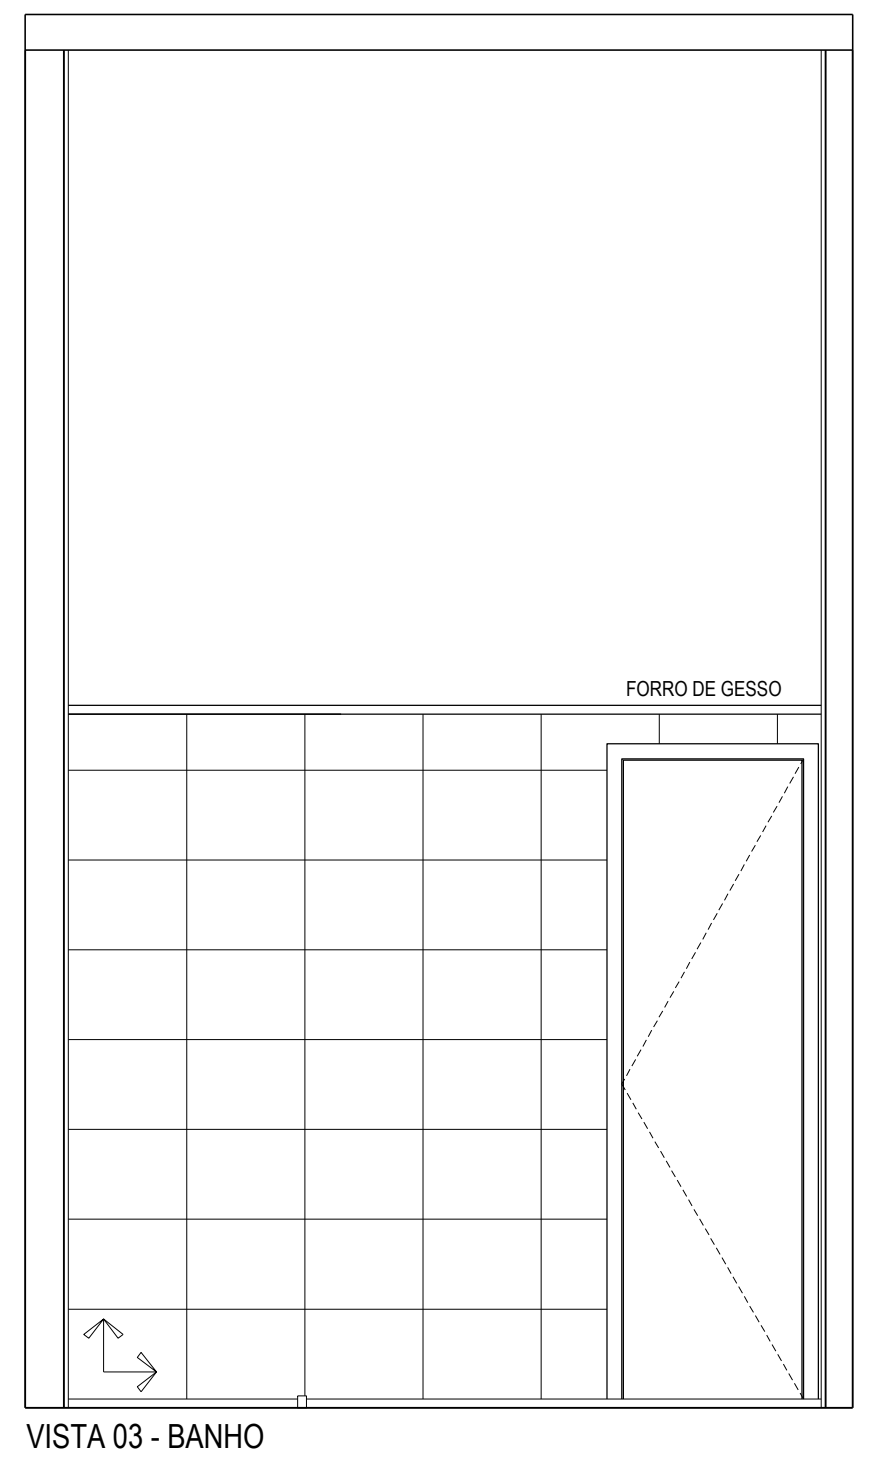
FORRO DE GESSO
VISTA 03 - BANHO
TORRE A: APARTAMENTO FINAL 04
TORRE B: APARTAMENTO FINAL 02
5º PAVIMENTO

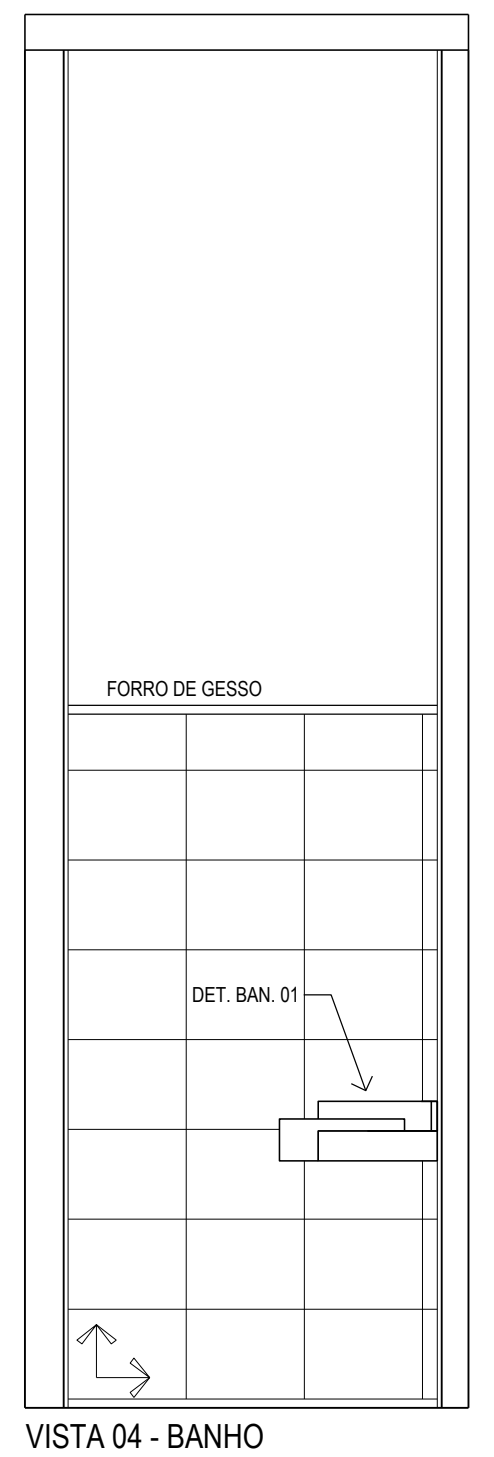
FORRO DE GESSO
DET. BAN. 01
VISTA 04 - BANHO
TORRE A: APARTAMENTO FINAL 04
TORRE B: APARTAMENTO FINAL 02
5º PAVIMENTO

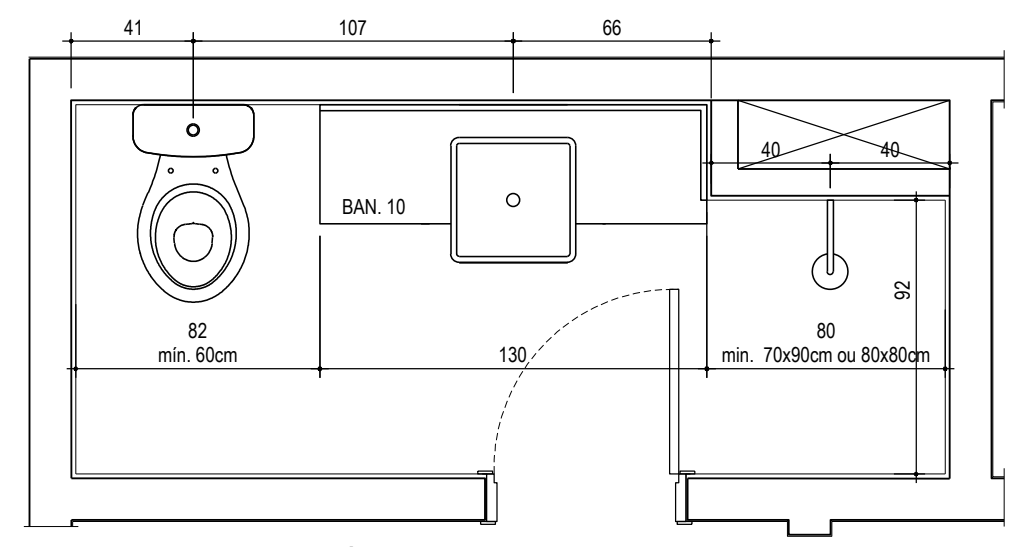
41
107
38
BAN. 10
82
mín. 60cm
130
80
min. 70x90cm ou 80x80cm
92
PLANTA BANHO - HIDRÁULICA
TORRE A: APARTAMENTO FINAL 02
TORRE B: APARTAMENTO FINAL 04
5º PAVIMENTO

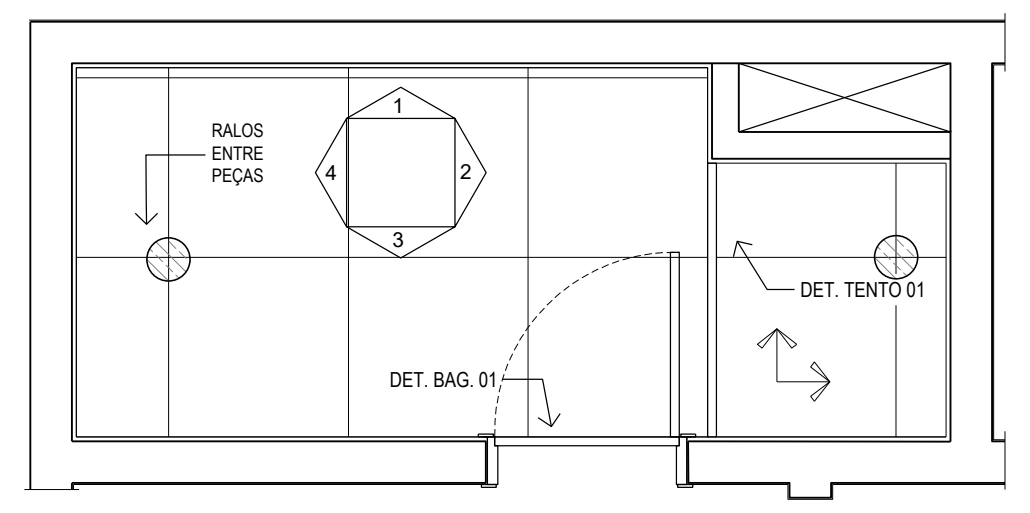
RALOS
ENTRE
PEÇAS
DET. TENTO 01
DET. BAG. 01
PLANTA BANHO - PISO
TORRE A: APARTAMENTO FINAL 02
TORRE B: APARTAMENTO FINAL 04
5º PAVIMENTO

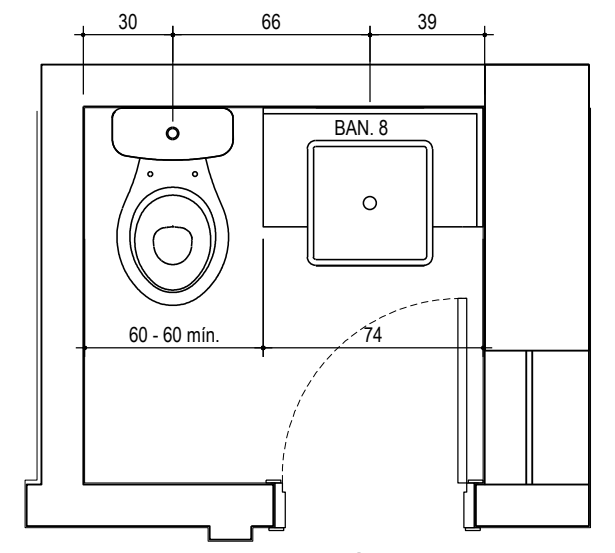
30
68
39
BAN. 8
60 - 60 min.
74
PLANTA LAVABO - HIDRÁULICA
TORRES A E B: APARTAMENTO FINAL 03
5º PAVIMENTO

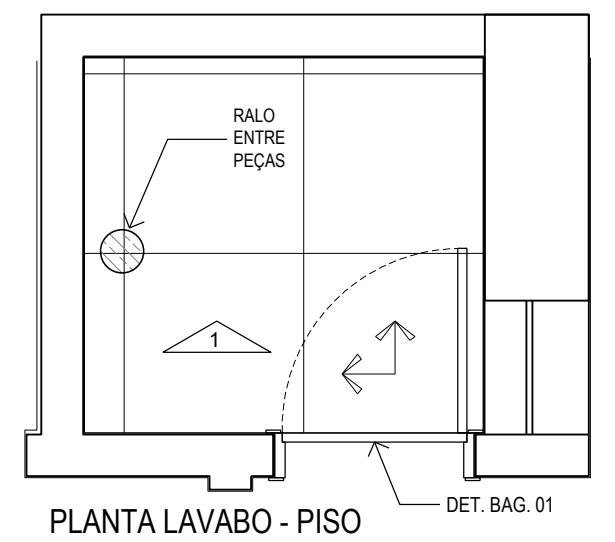
RALO
ENTRE
PEÇAS
1
DET. BAG. 01
PLANTA LAVABO - PISO
TORRES A E B: APARTAMENTO FINAL 03
5º PAVIMENTO

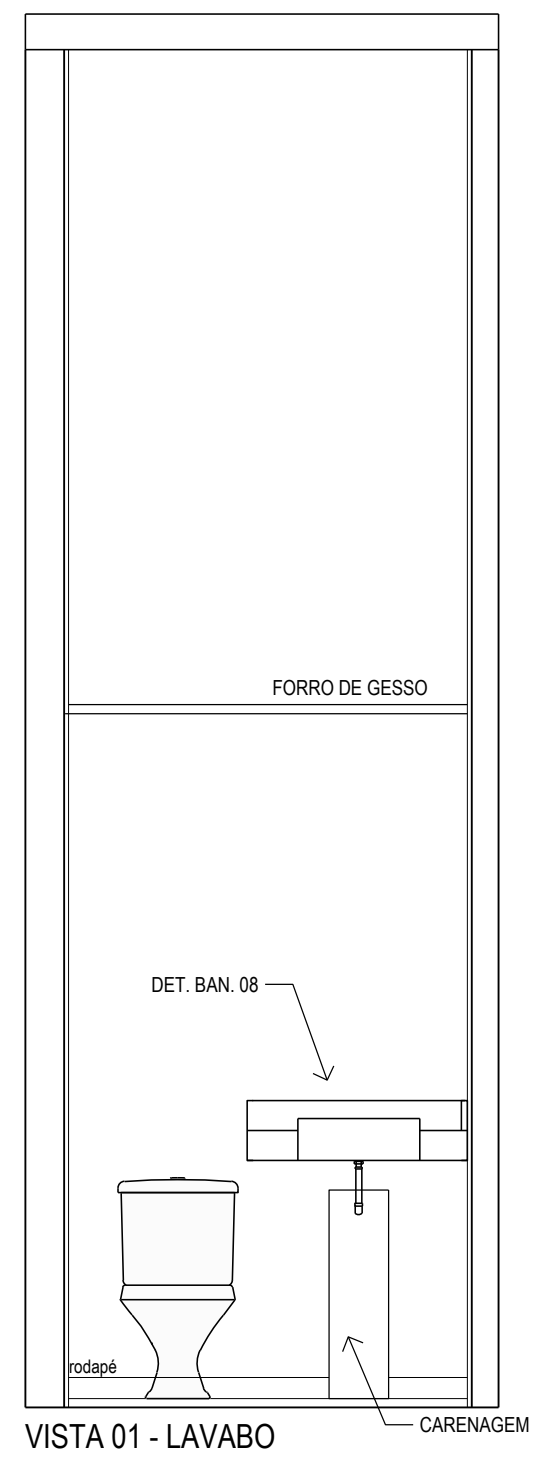
FORRO DE GESSO
DET. BAN. 08
rodapé
CARENAGEM
VISTA 01 - LAVABO
TORRES A E B: APARTAMENTO FINAL 03
5º PAVIMENTO

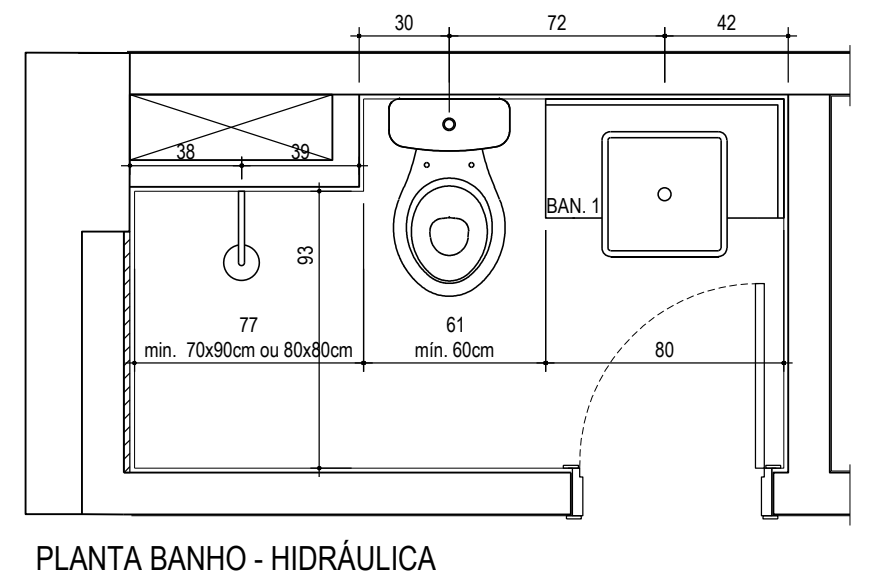
30
72
42
BAN. 1
77
min. 70x90cm ou 80x80cm
61
mín. 60cm
93
80
PLANTA BANHO - HIDRÁULICA
TORRES A E B: APARTAMENTO FINAL 03
5º PAVIMENTO

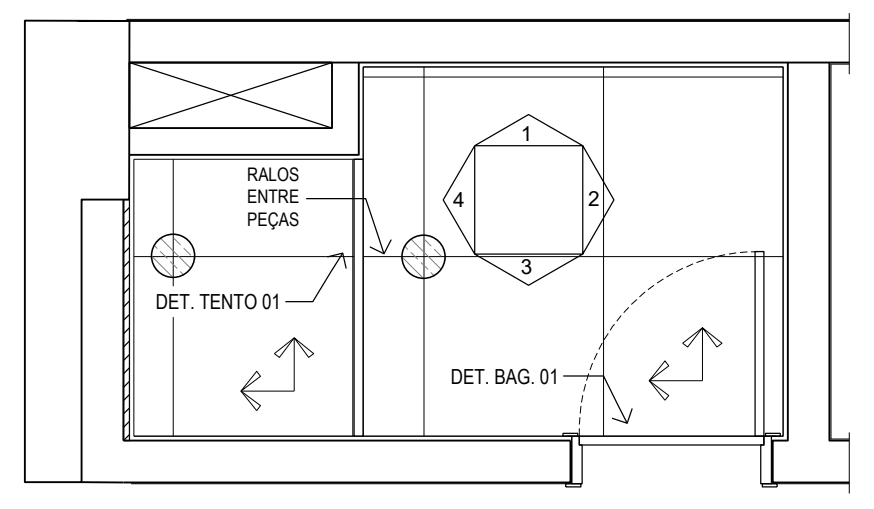
RALOS
ENTRE
PEÇAS
DET. TENTO 01
DET. BAG. 01
PLANTA BANHO - PISO
TORRES A E B: APARTAMENTO FINAL 03
5º PAVIMENTO

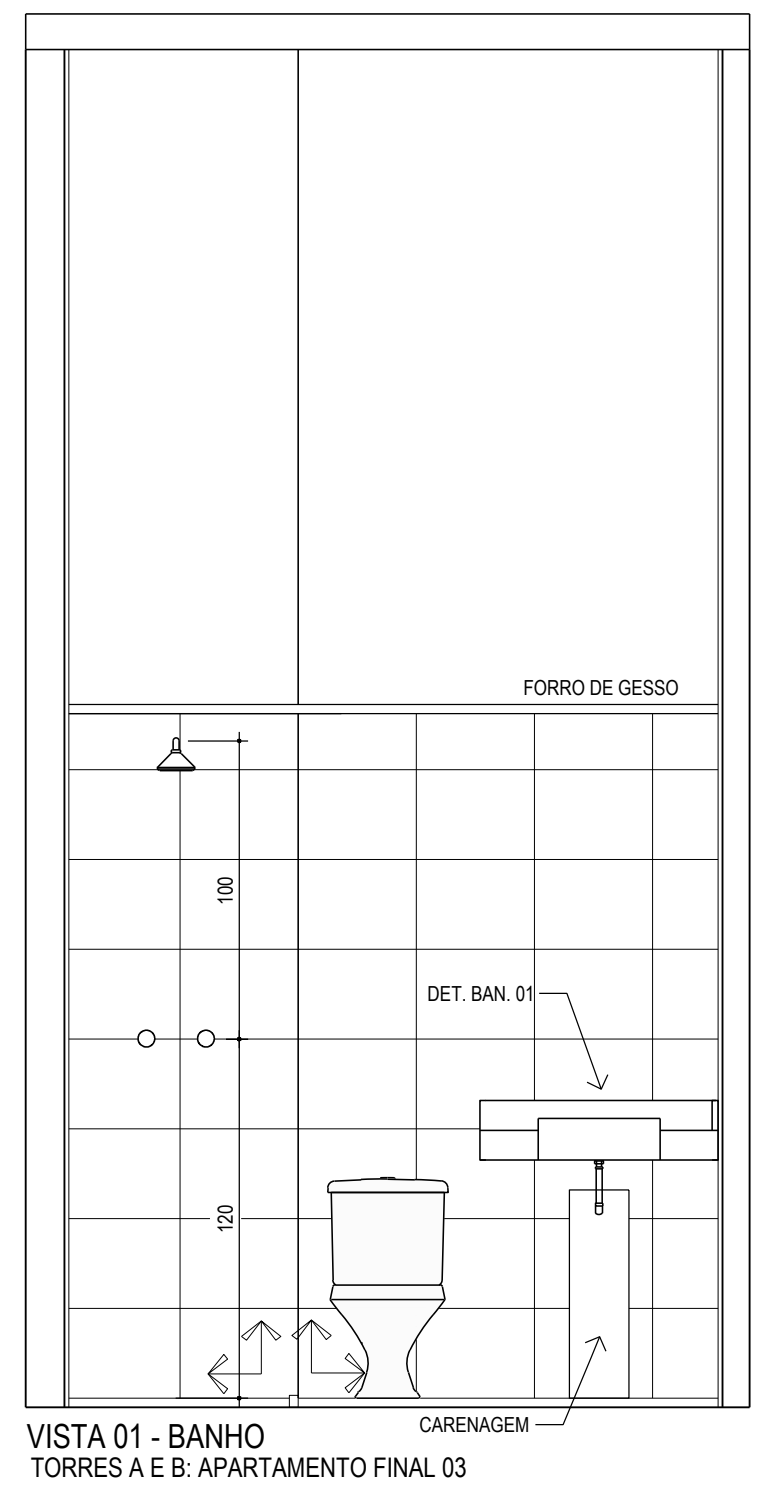
FORRO DE GESSO
DET. BAN. 01
120
CARENAGEM
VISTA 01 - BANHO
TORRES A E B: APARTAMENTO FINAL 03
5º PAVIMENTO

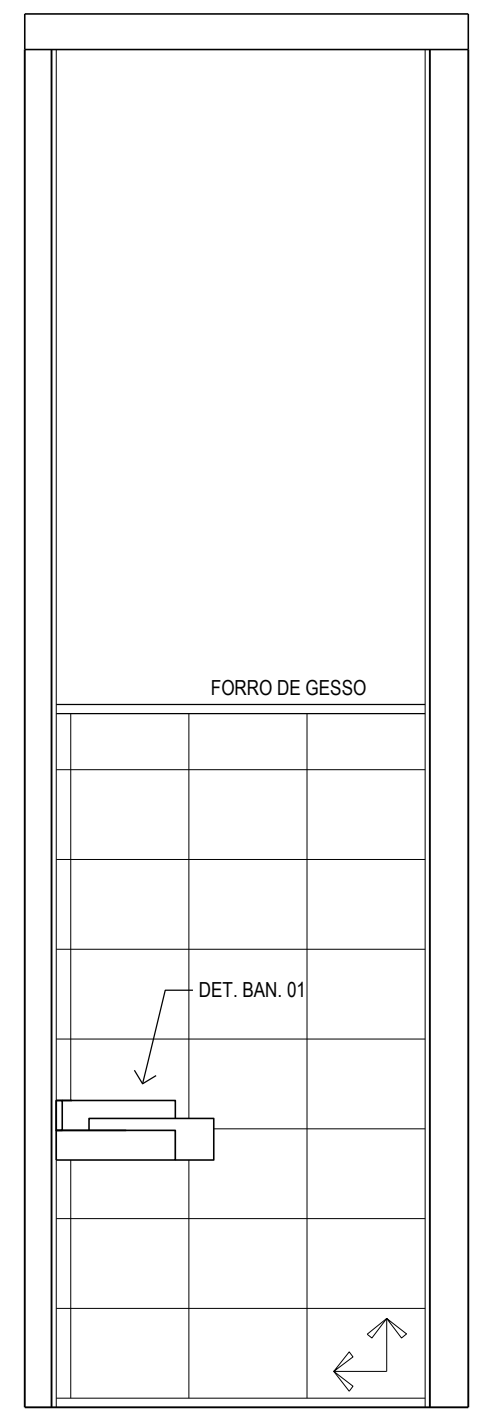
FORRO DE GESSO
DET. BAN. 01
VISTA 02 - BANHO
TORRES A E B: APARTAMENTO FINAL 03
5º PAVIMENTO

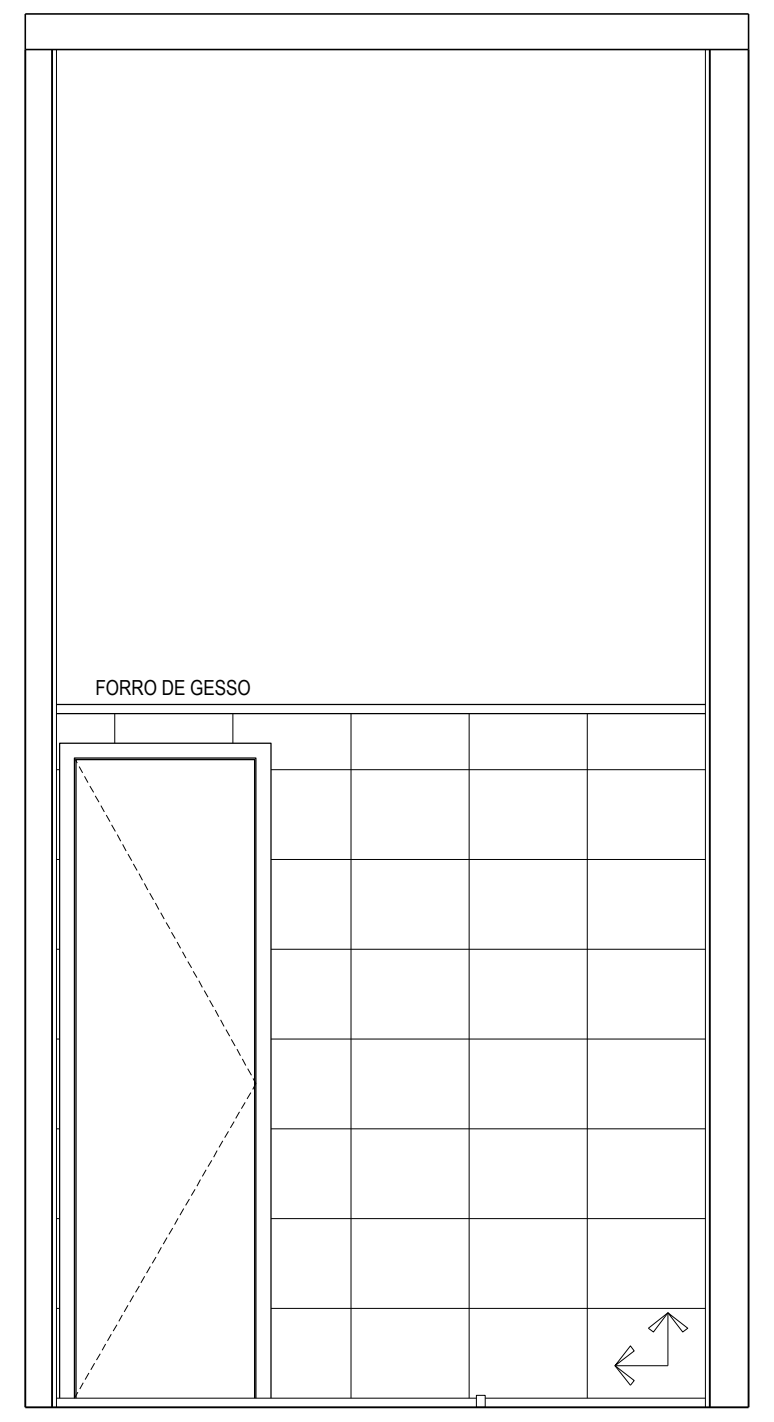
FORRO DE GESSO
VISTA 03 - BANHO
TORRES A E B: APARTAMENTO FINAL 03
5º PAVIMENTO

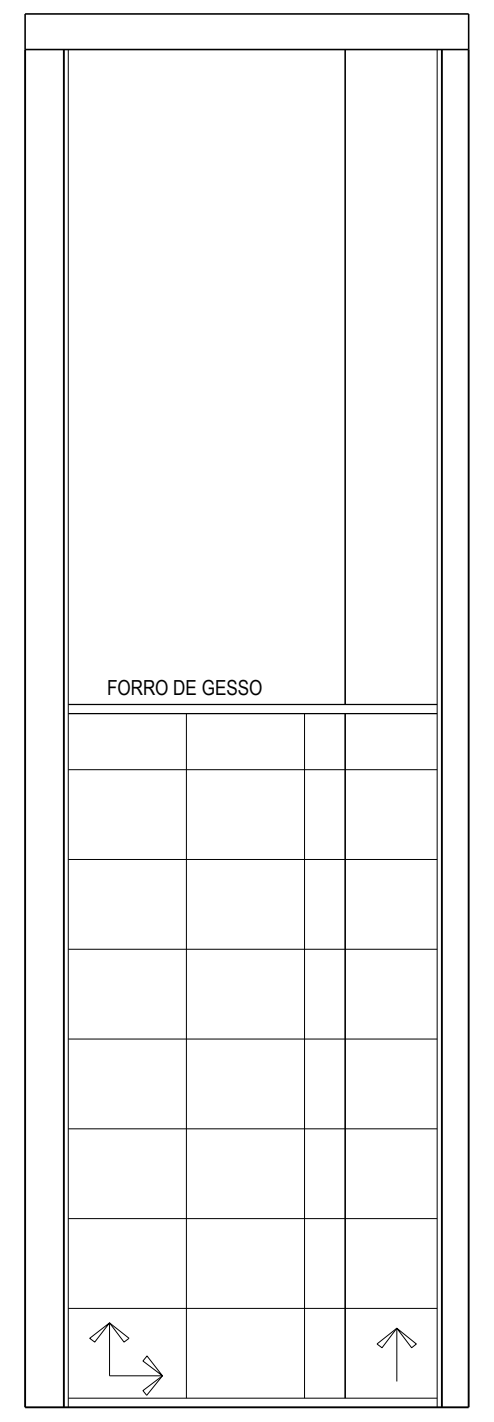
FORRO DE GESSO
VISTA 04 - BANHO
TORRES A E B: APARTAMENTO FINAL 03
5º PAVIMENTO

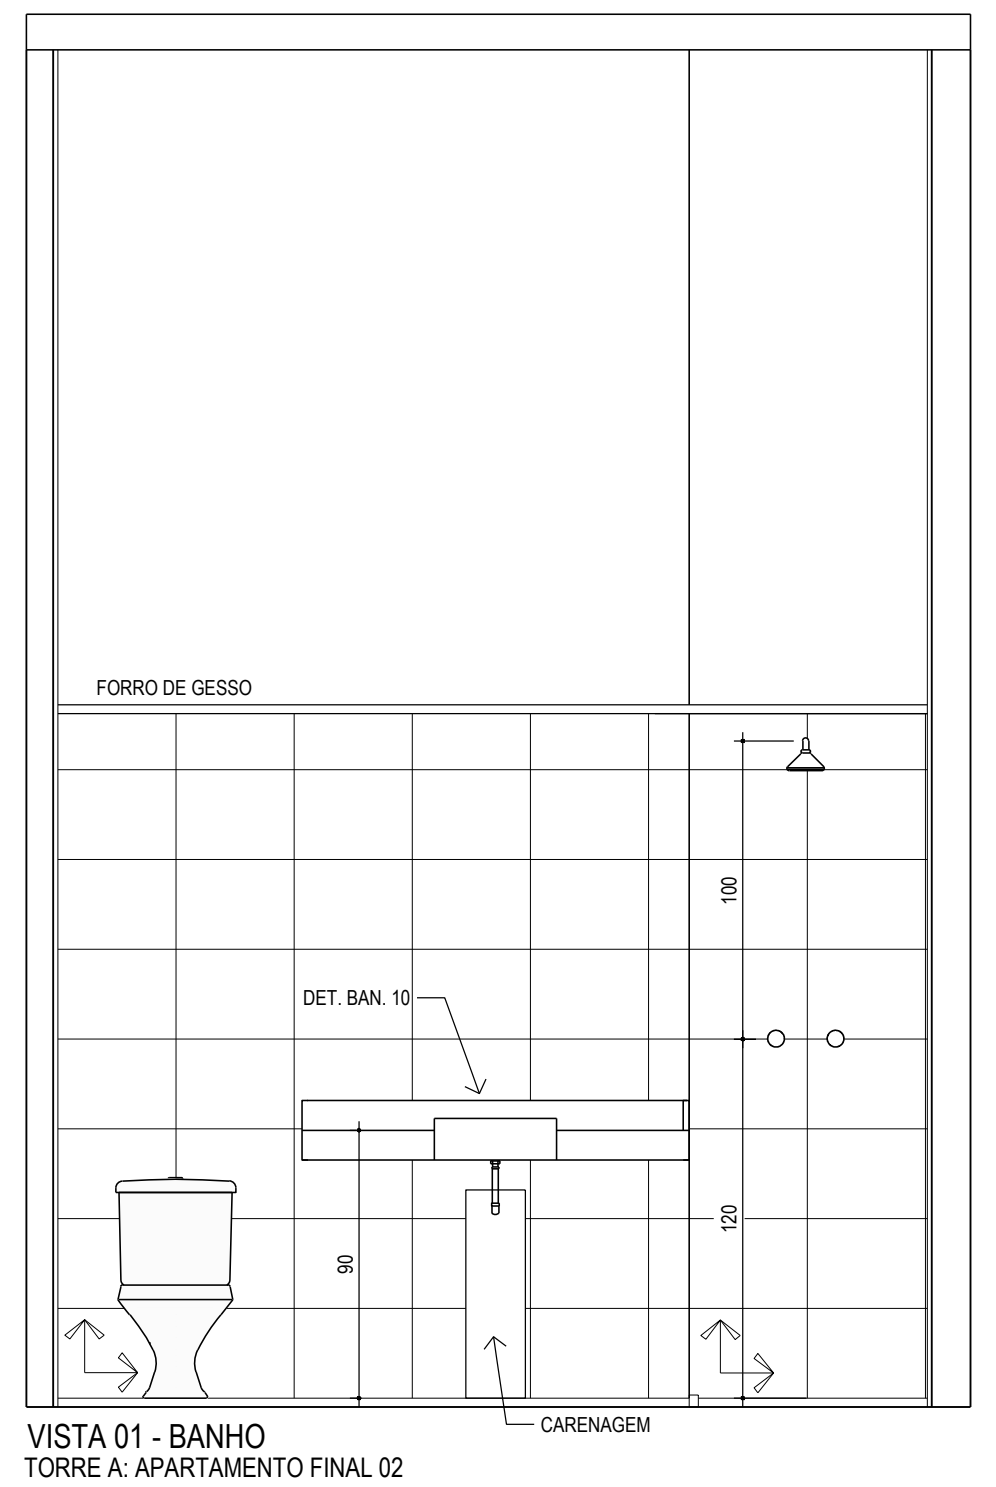
FORRO DE GESSO
DET. BAN. 10
90
120
CARENAGEM
VISTA 01 - BANHO
TORRE A: APARTAMENTO FINAL 02
TORRE B: APARTAMENTO FINAL 04
5º PAVIMENTO

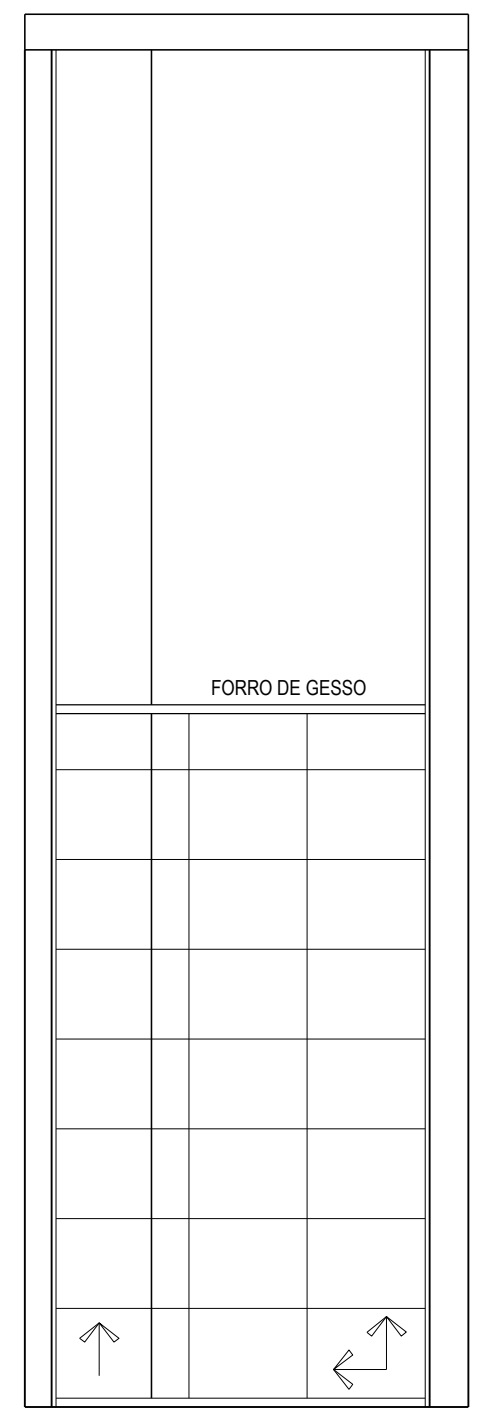
FORRO DE GESSO
VISTA 02 - BANHO
TORRE A: APARTAMENTO FINAL 02
TORRE B: APARTAMENTO FINAL 04
5º PAVIMENTO

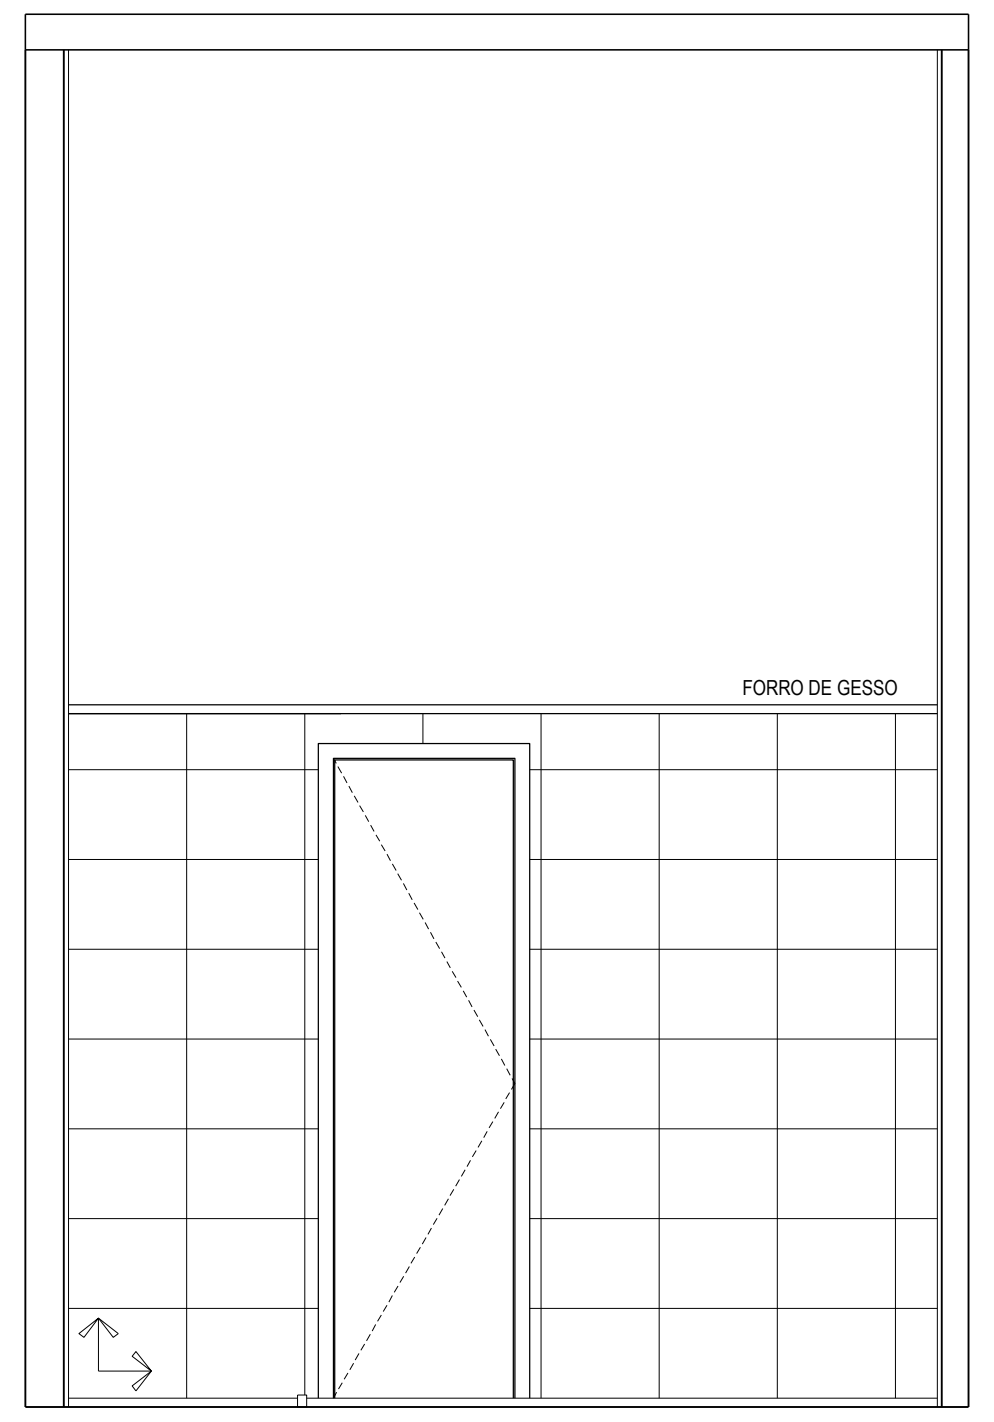
FORRO DE GESSO
VISTA 03 - BANHO
TORRE A: APARTAMENTO FINAL 02
TORRE B: APARTAMENTO FINAL 04
5º PAVIMENTO

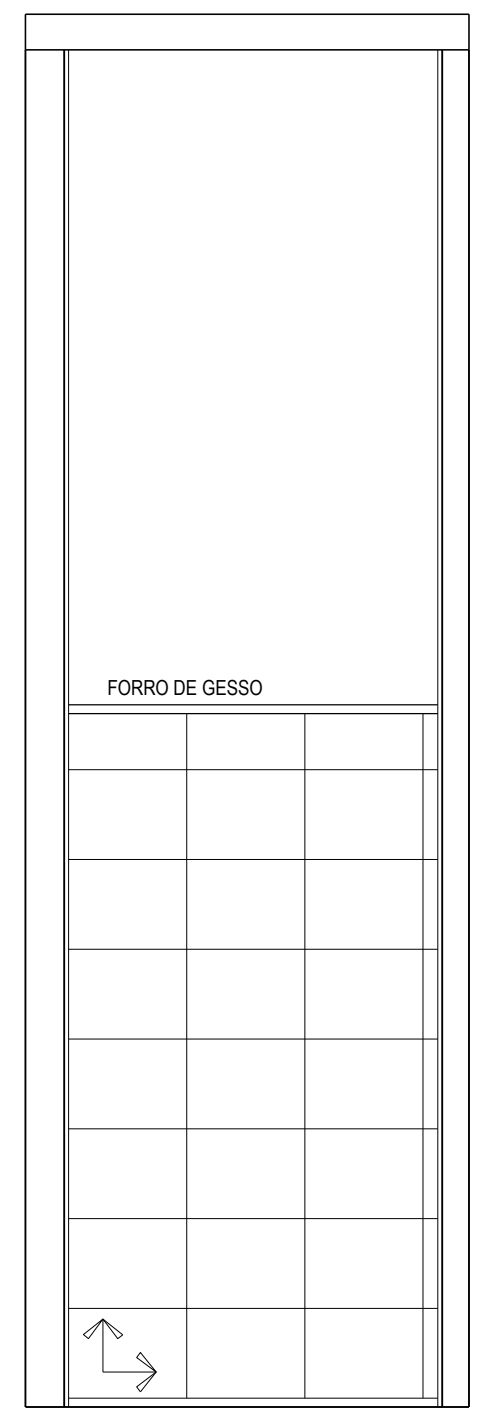
FORRO DE GESSO
VISTA 04 - BANHO
TORRE A: APARTAMENTO FINAL 04
TORRE B: APARTAMENTO FINAL 02
5º PAVIMENTO

PLANTAS DE REFERÊNCIA PARA BASE DE PROJETO

REVISÃO	DATA	DESCRIÇÃO	RESP.
00	01/03/2023	EMISSÃO INICIAL	

INCORPORAÇÃO
JERONIMO DA VEIGA
Empreendimentos e Participações Ltda.

CONSTRUÇÃO

PROJETISTA
ADESA ARQUITETURA
RUA PADRE GARCIA VELHO, 73 - CJ. 41
CEP: 05421- 030
FONE: 3032 4355 / 3032 4362

DISCIPLINA
ARQUITETURA

CÓDIGO/OBRA
DUO

FASE
LIBERADO OBRA

EMPREENDIMENTO
DUO
AV_LUZ

ASSUNTO
DETALHAMENTO
ÁREAS_MOLHADAS_PUC

FOLHA N.º
ARQ
126

RESPONSÁVEL
ADELINO SANTOS

SUPERVISOR
ADELINO SANTOS

COORDENADOR
ALISSA LOPES

REVISÃO
R00

PROJETISTA

ARQUIVO
DUO-ARQ-LO-126-DET-AMO-R00.dwg

ESCALA
1:25

DATA
01/03/2023

DIREITOS AUTORAIS RESERVADO A REPRODUÇÃO TOTAL OU PARCIAL SEM PRÉVIA AUTORIZAÇÃO, CONFORME RESOLUÇÃO N° 67, DE 5 DE DEZEMBRO DE 2013