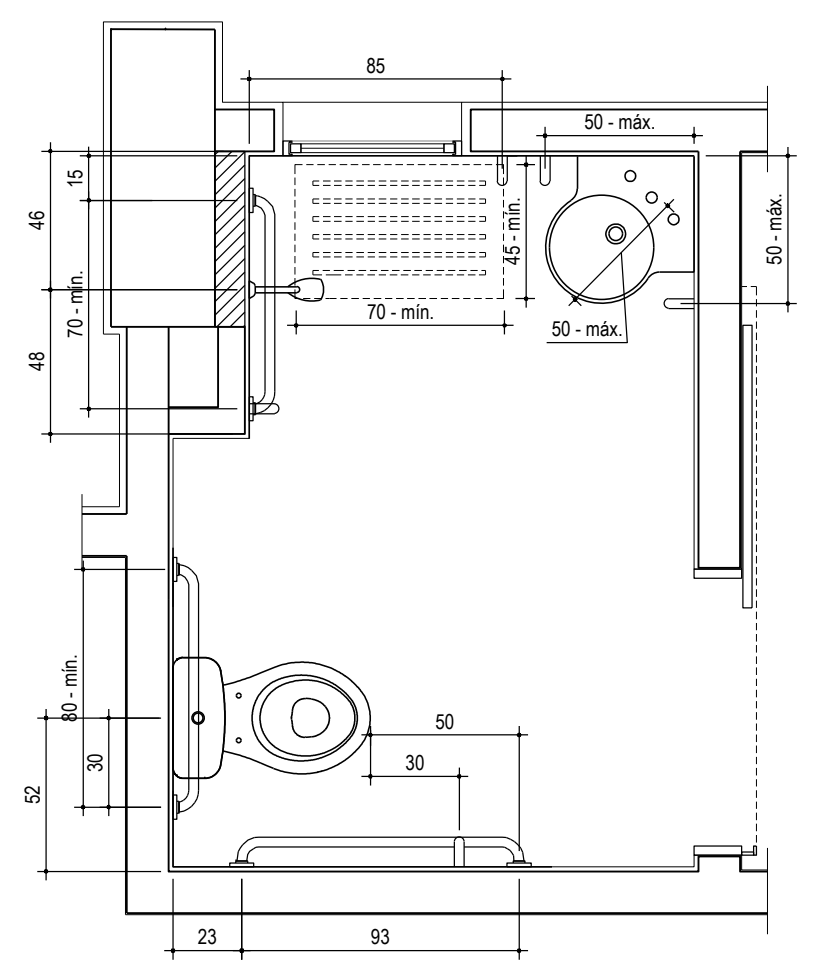
85
30 - máx.
70 - mín.
50 - máx.
50
30
23
93

PLANTA BANHO 2 - HIDRÁULICA
OPÇÃO DE VENDAS
TORRE A: APARTAMENTO FINAL 05
TORRE B: APARTAMENTO FINAL 01
5º PAVIMENTO

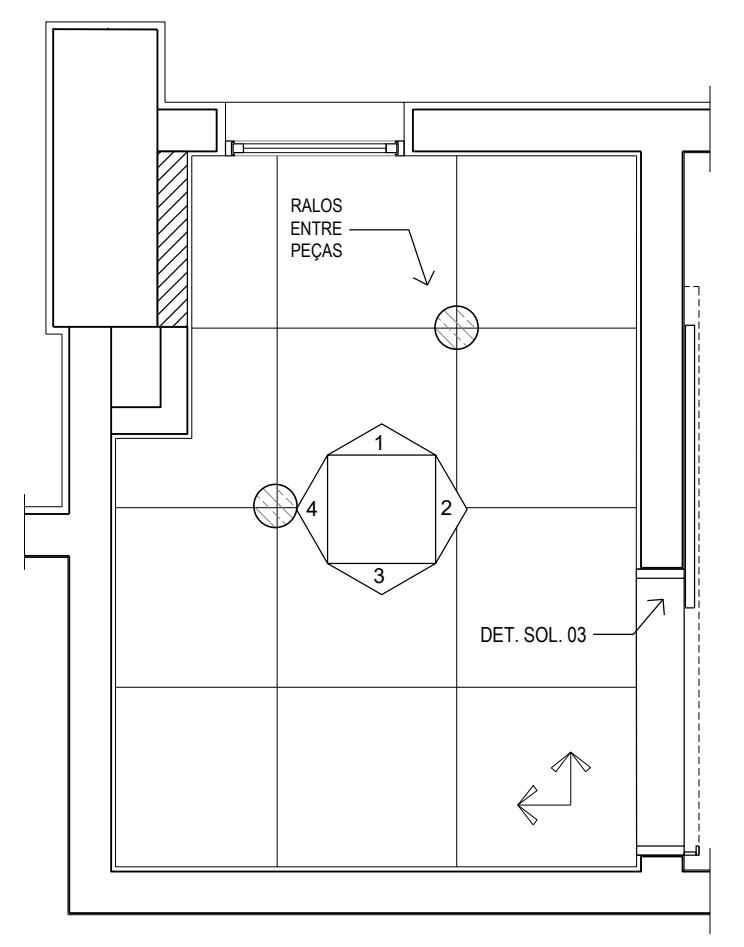
RALOS ENTRE PEÇAS
DET. SOL. 03

PLANTA BANHO 2 - PISO
OPÇÃO DE VENDAS
TORRE A: APARTAMENTO FINAL 05
TORRE B: APARTAMENTO FINAL 01
5º PAVIMENTO

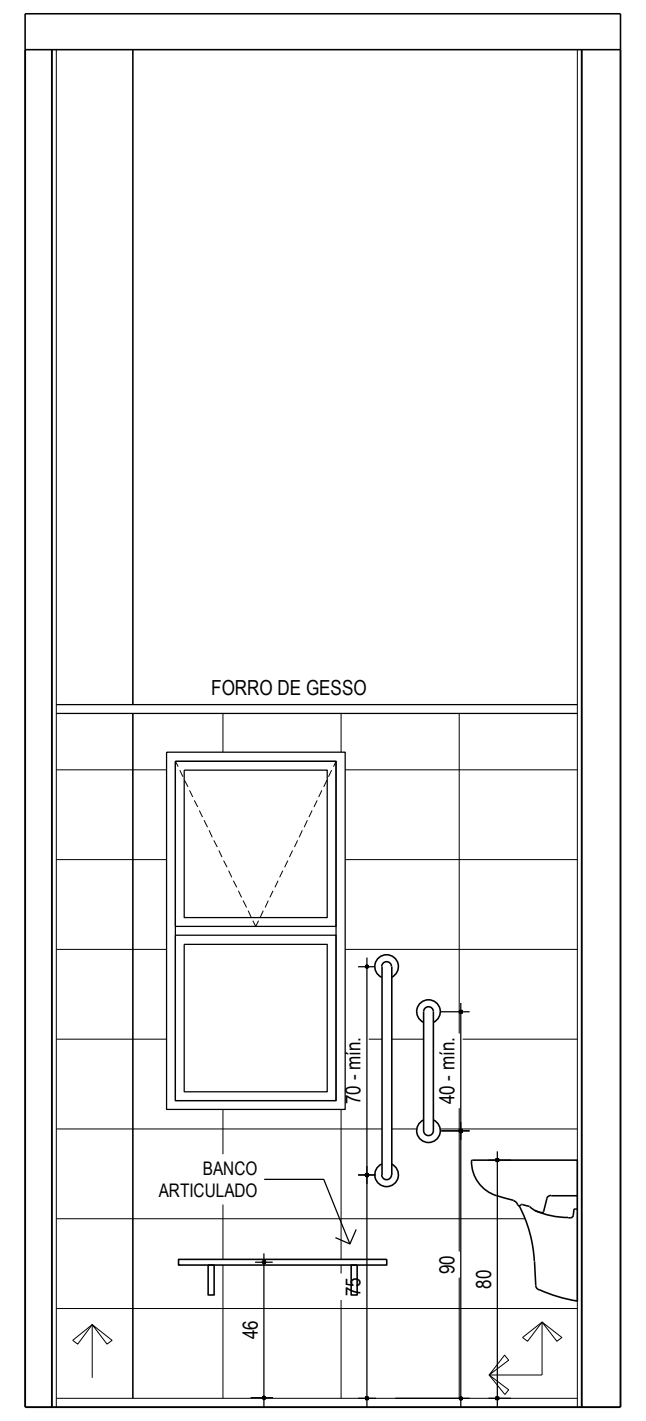
FORRO DE GESSO
BANCO ARTICULADO
46
90
80

VISTA 01 - BANHO 2
OPÇÃO DE VENDAS
TORRE A: APARTAMENTO FINAL 05
TORRE B: APARTAMENTO FINAL 01
5º PAVIMENTO

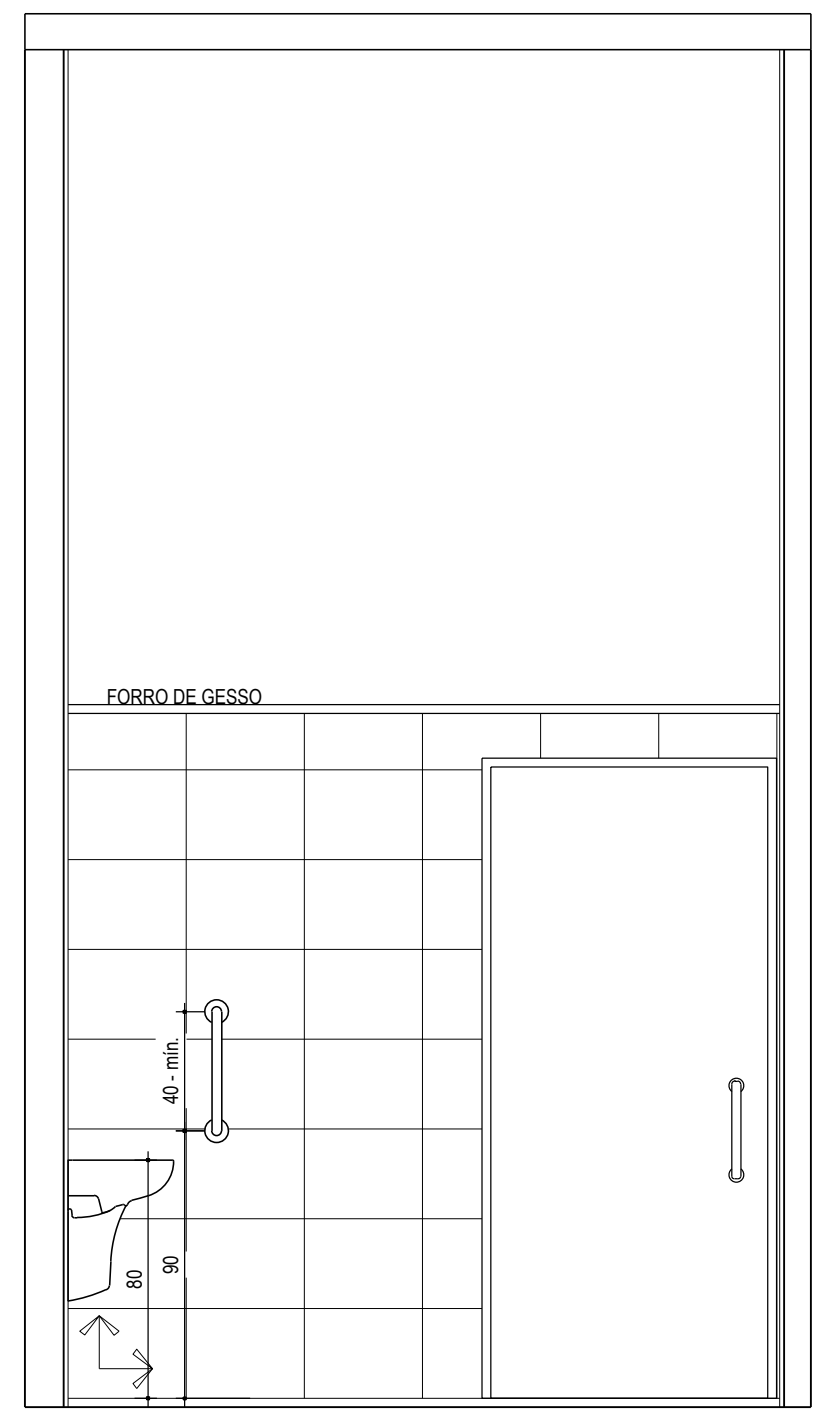
FORRO DE GESSO
80
90

VISTA 02 - BANHO 2
OPÇÃO DE VENDAS
TORRE A: APARTAMENTO FINAL 05
TORRE B: APARTAMENTO FINAL 01
5º PAVIMENTO

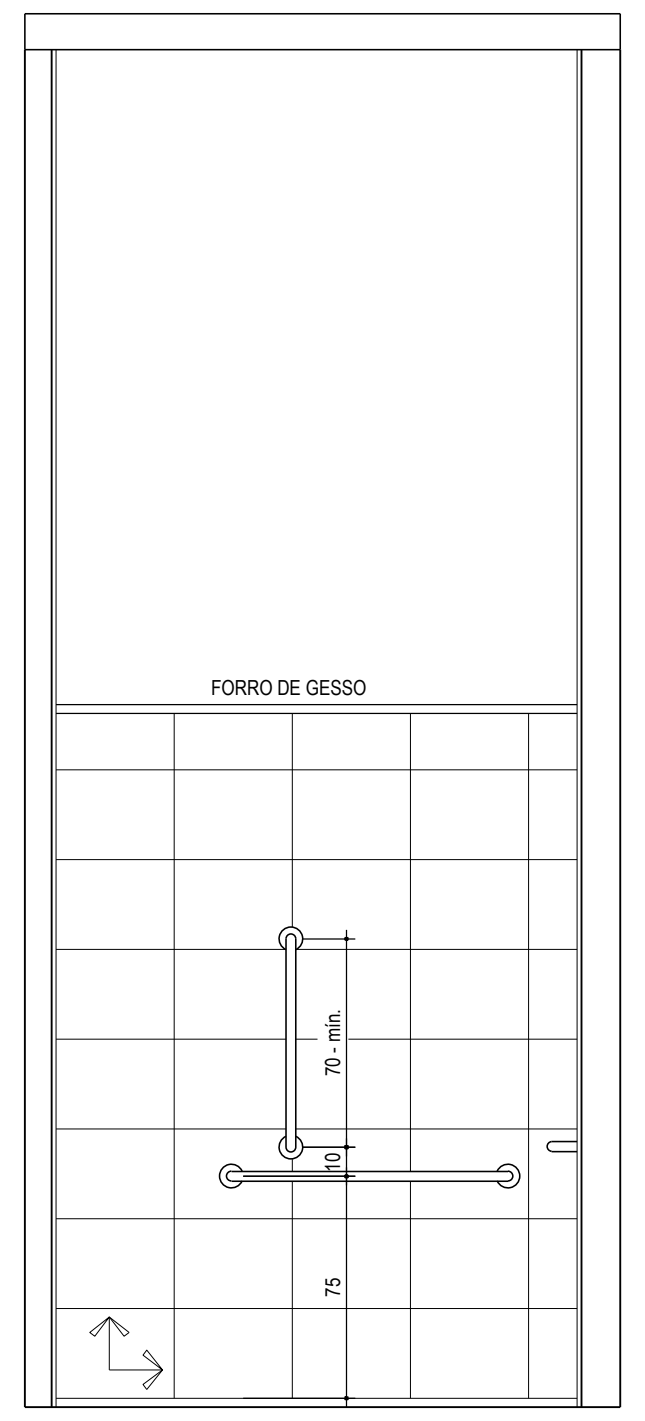
FORRO DE GESSO
75

VISTA 03 - BANHO 2
OPÇÃO DE VENDAS
TORRE A: APARTAMENTO FINAL 05
TORRE B: APARTAMENTO FINAL 01
5º PAVIMENTO

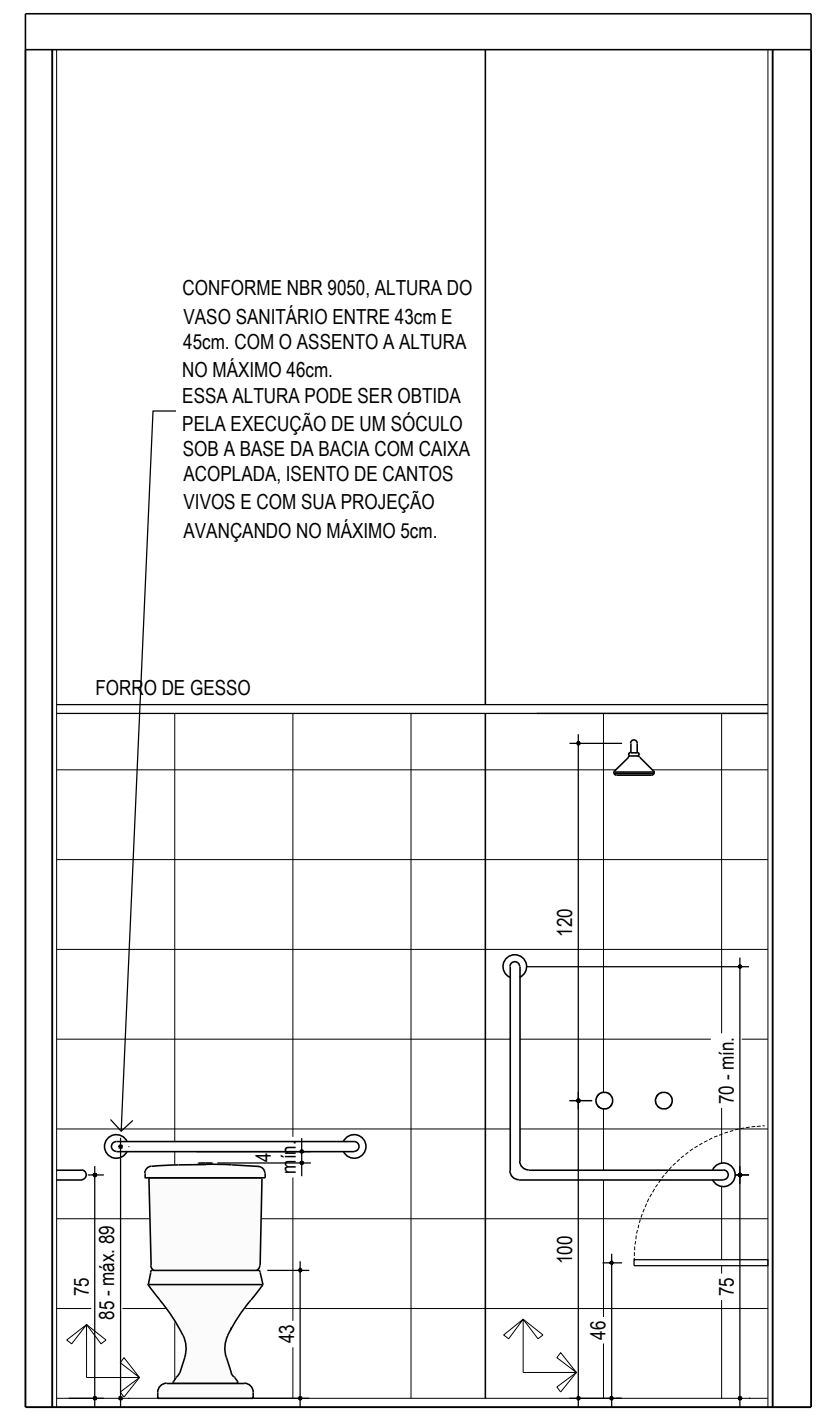
CONFORME NBR 9050, ALTURA DO VASO SANITÁRIO ENTRE 43cm E 45cm. COM O ASSENTO A ALTURA NO MÁXIMO 46cm. ESSA ALTURA PODE SER OBTIDA PELA EXECUÇÃO DE UM SÓCULO SOB A BASE DA BACIA COM CAIXA ACOPLADA, ISENTO DE CANTOS VIVOS E COM SUA PROJEÇÃO AVANÇANDO NO MÁXIMO 5cm.
FORRO DE GESSO
85 - máx. 89
43
100
46

VISTA 04 - BANHO 2
OPÇÃO DE VENDAS
TORRE A: APARTAMENTO FINAL 05
TORRE B: APARTAMENTO FINAL 01
5º PAVIMENTO

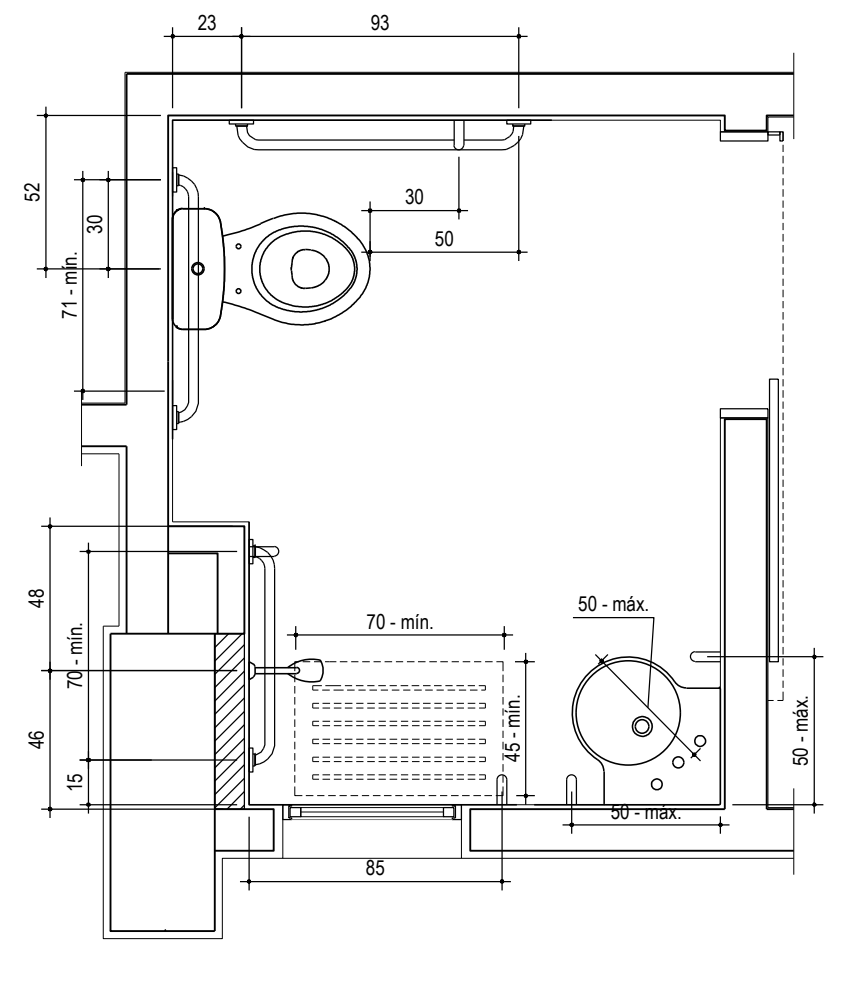
70 - mín.
50 - máx.
45 - mín.
85

PLANTA BANHO 2 - HIDRÁULICA
OPÇÃO DE VENDAS
TORRE A: APARTAMENTO FINAL 01
TORRE B: APARTAMENTO FINAL 05
5º PAVIMENTO

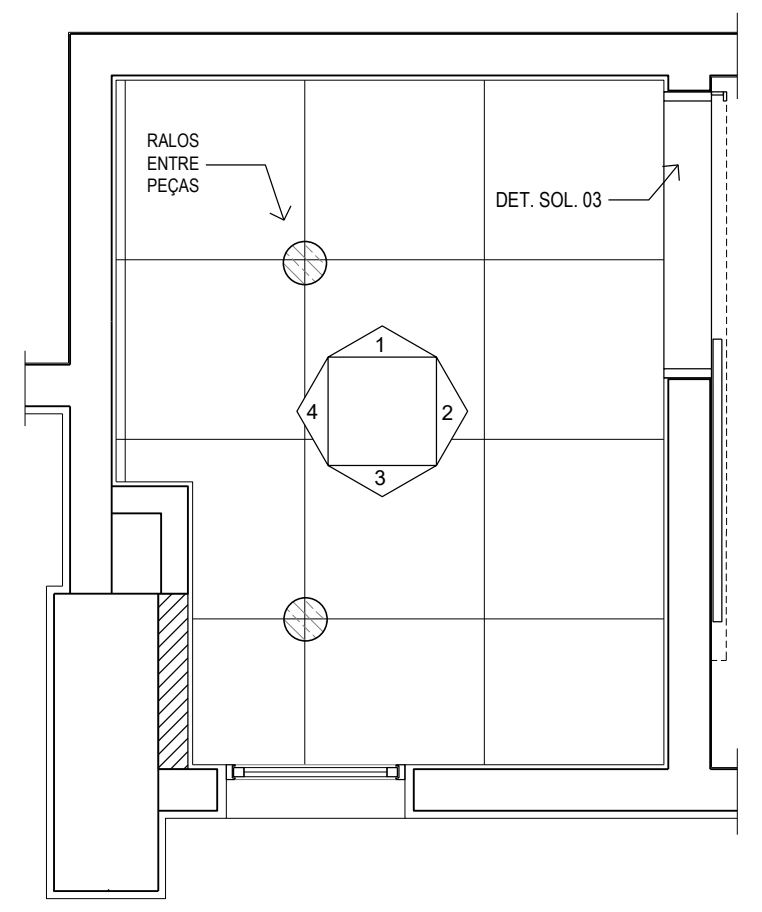
RALOS ENTRE PEÇAS
DET. SOL. 03

PLANTA BANHO 2 - PISO
OPÇÃO DE VENDAS
TORRE A: APARTAMENTO FINAL 01
TORRE B: APARTAMENTO FINAL 05
5º PAVIMENTO

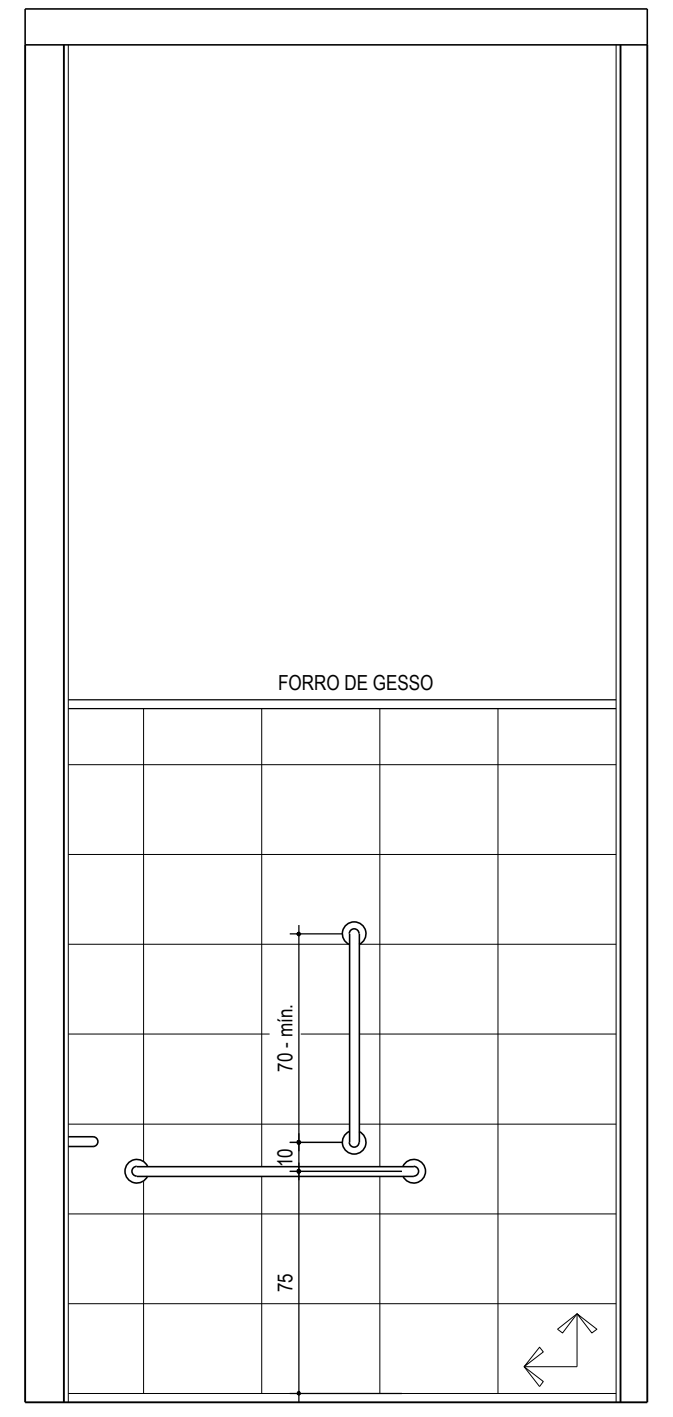
FORRO DE GESSO
75

VISTA 01 - BANHO 2
OPÇÃO DE VENDAS
TORRE A: APARTAMENTO FINAL 01
TORRE B: APARTAMENTO FINAL 05
5º PAVIMENTO

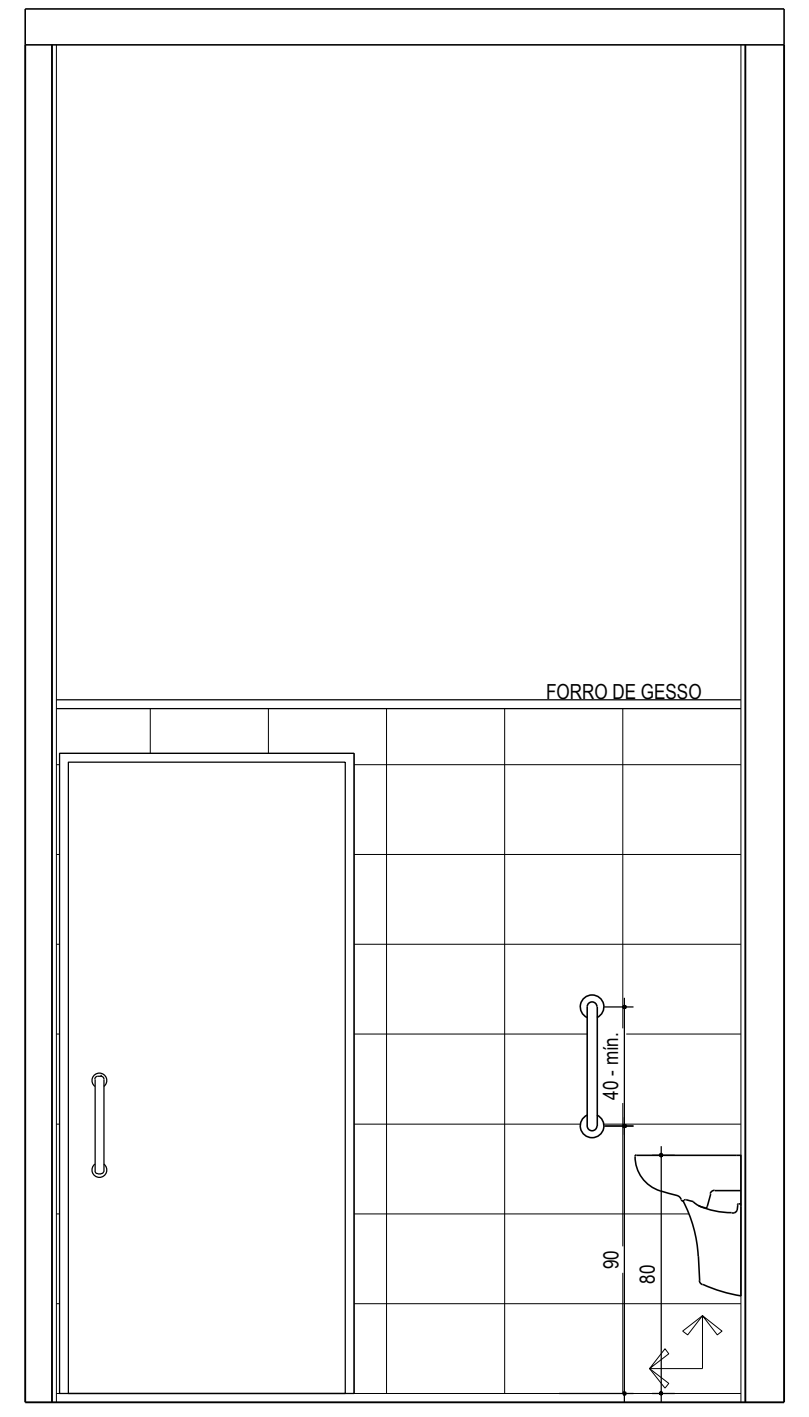
FORRO DE GESSO
90
80

VISTA 02 - BANHO 2
OPÇÃO DE VENDAS
TORRE A: APARTAMENTO FINAL 01
TORRE B: APARTAMENTO FINAL 05
5º PAVIMENTO

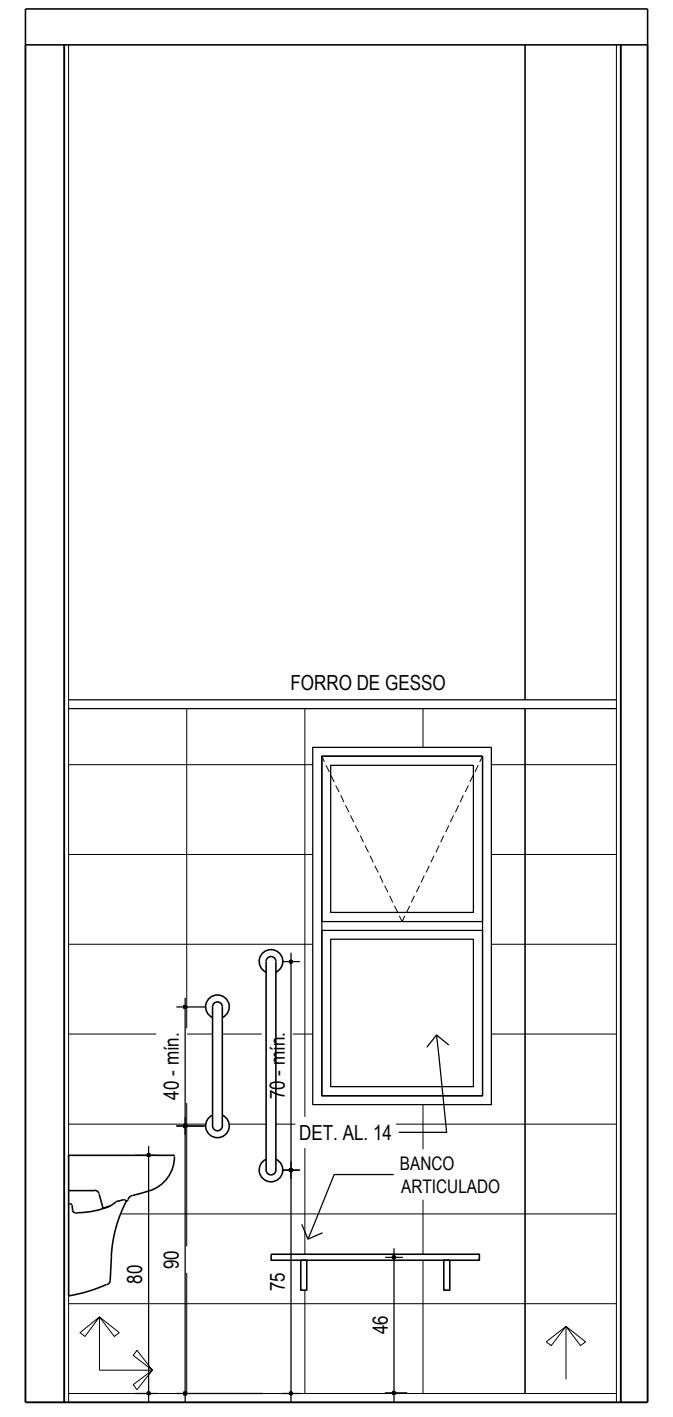
FORRO DE GESSO
DET. AL. 14
BANCO ARTICULADO

VISTA 03 - BANHO 2
OPÇÃO DE VENDAS
TORRE A: APARTAMENTO FINAL 01
TORRE B: APARTAMENTO FINAL 05
5º PAVIMENTO

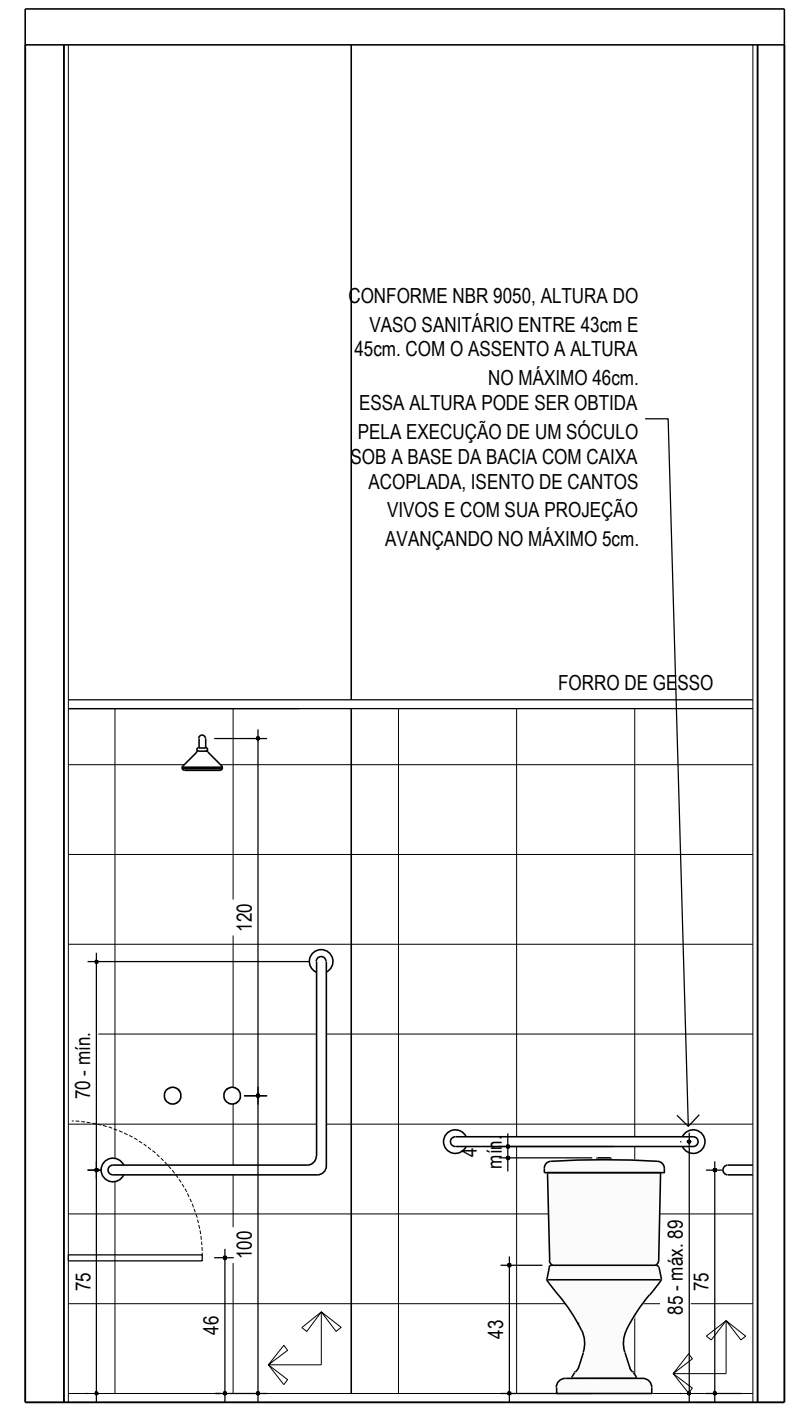
CONFORME NBR 9050, ALTURA DO VASO SANITÁRIO ENTRE 43cm E 45cm. COM O ASSENTO A ALTURA NO MÁXIMO 46cm. ESSA ALTURA PODE SER OBTIDA PELA EXECUÇÃO DE UM SÓCULO SOB A BASE DA BACIA COM CAIXA ACOPLADA, ISENTO DE CANTOS VIVOS E COM SUA PROJEÇÃO AVANÇANDO NO MÁXIMO 5cm.
FORRO DE GESSO
85 - máx. 89

VISTA 04 - BANHO 2
OPÇÃO DE VENDAS
TORRE A: APARTAMENTO FINAL 01
TORRE B: APARTAMENTO FINAL 05
5º PAVIMENTO

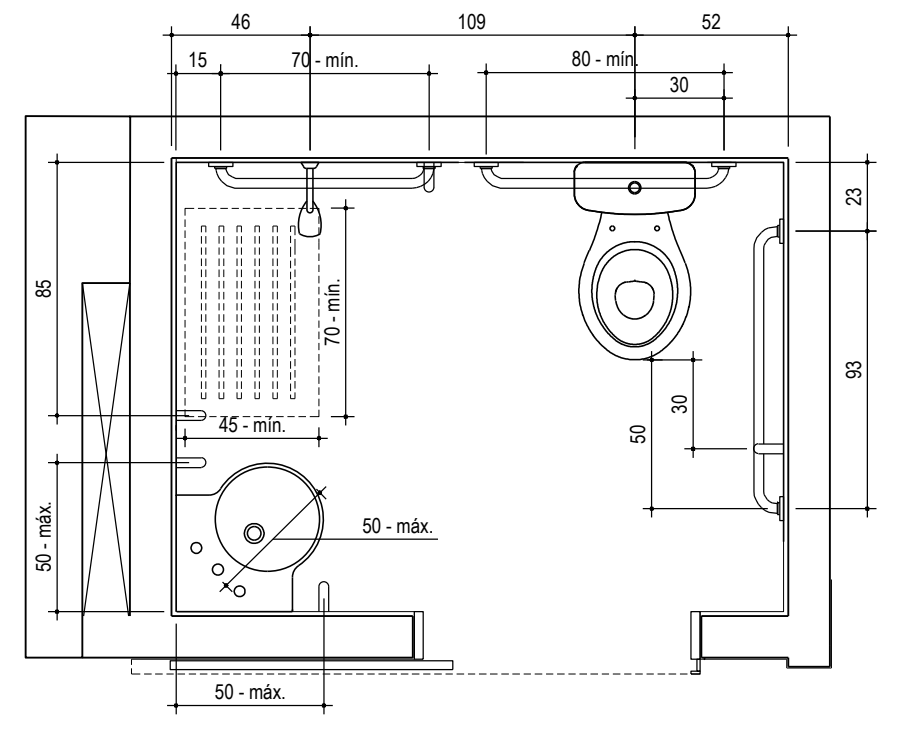
45 - mín.
50 - máx.

PLANTA BANHO - HIDRÁULICA
OPÇÃO DE VENDAS
TORRES A E B: APARTAMENTO FINAL 03
5º PAVIMENTO

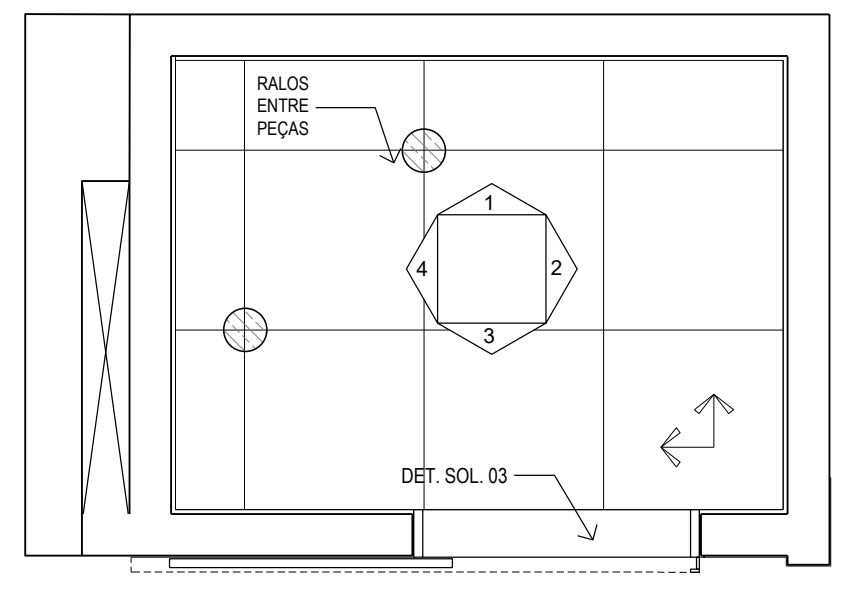
RALOS ENTRE PEÇAS
DET. SOL. 03

PLANTA BANHO - PISO
OPÇÃO DE VENDAS
TORRES A E B: APARTAMENTO FINAL 03
5º PAVIMENTO

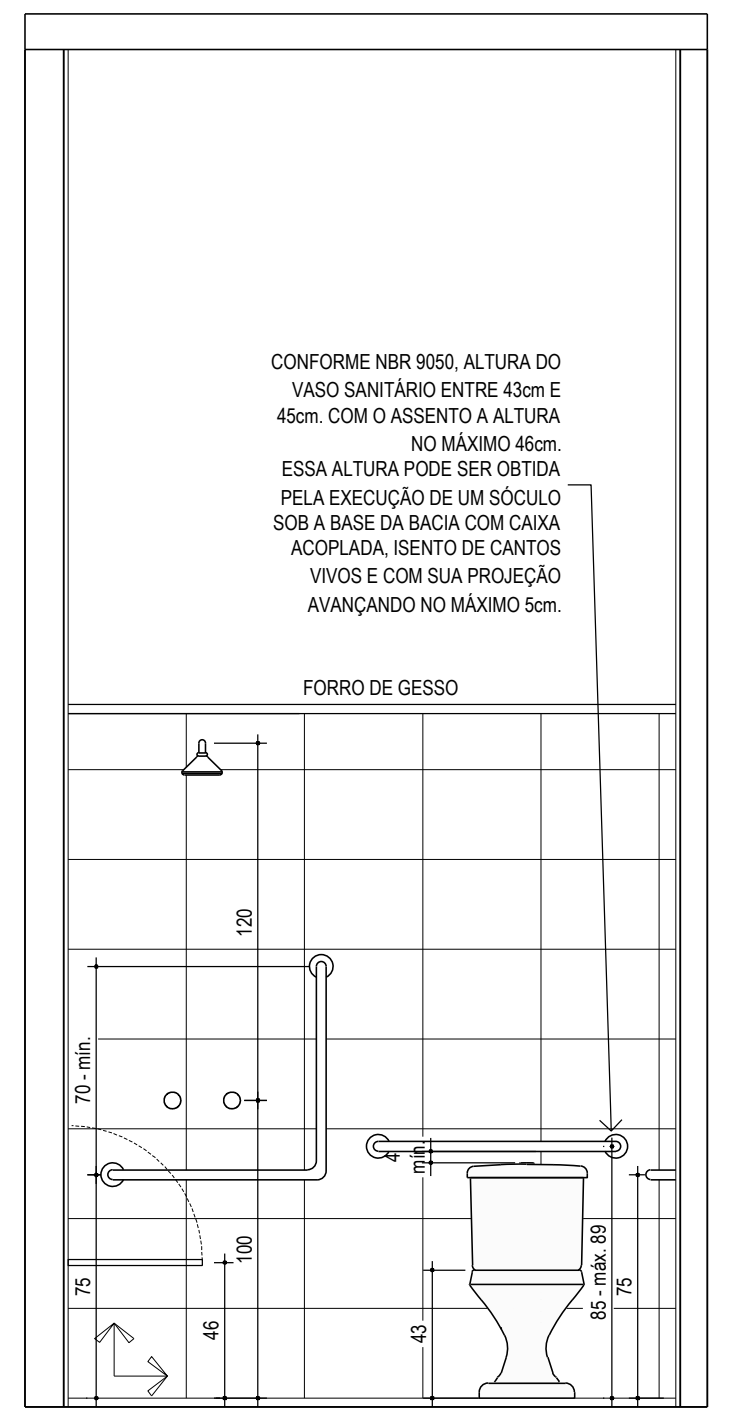
CONFORME NBR 9050, ALTURA DO VASO SANITÁRIO ENTRE 43cm E 45cm. COM O ASSENTO A ALTURA NO MÁXIMO 46cm. ESSA ALTURA PODE SER OBTIDA PELA EXECUÇÃO DE UM SÓCULO SOB A BASE DA BACIA COM CAIXA ACOPLADA, ISENTO DE CANTOS VIVOS E COM SUA PROJEÇÃO AVANÇANDO NO MÁXIMO 5cm.
FORRO DE GESSO
85 - máx. 89

VISTA 01 - BANHO
OPÇÃO DE VENDAS
TORRES A E B: APARTAMENTO FINAL 03
5º PAVIMENTO

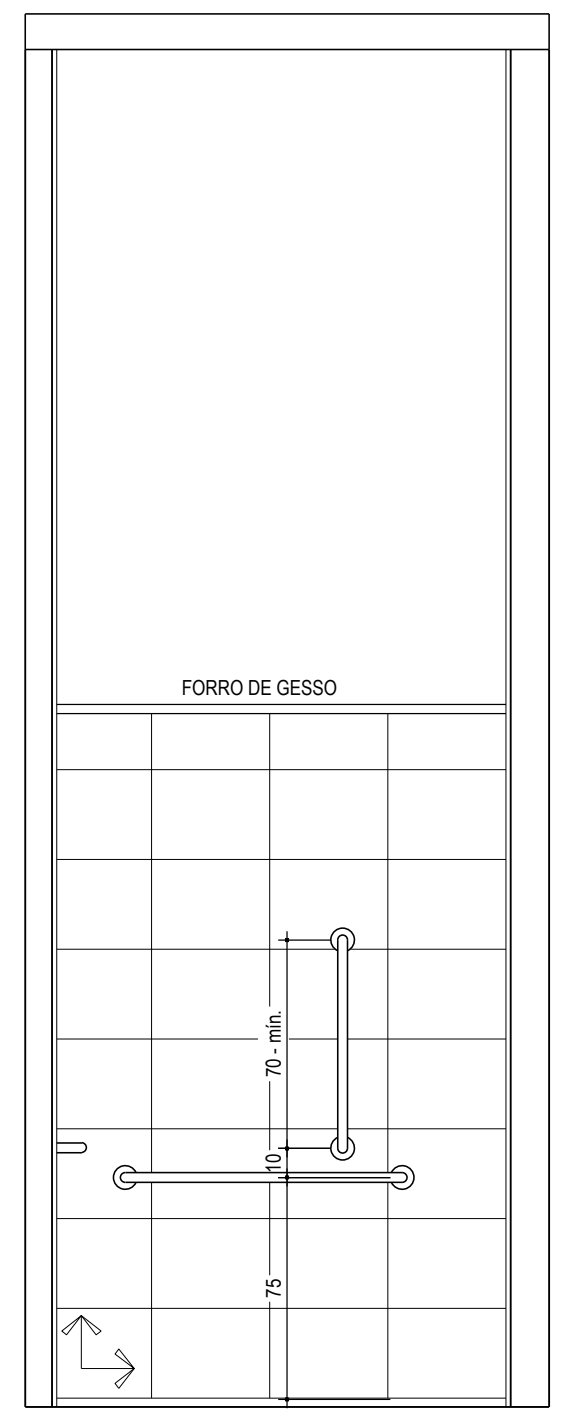
FORRO DE GESSO
75

VISTA 04 - BANHO
OPÇÃO DE VENDAS
TORRES A E B: APARTAMENTO FINAL 03
5º PAVIMENTO

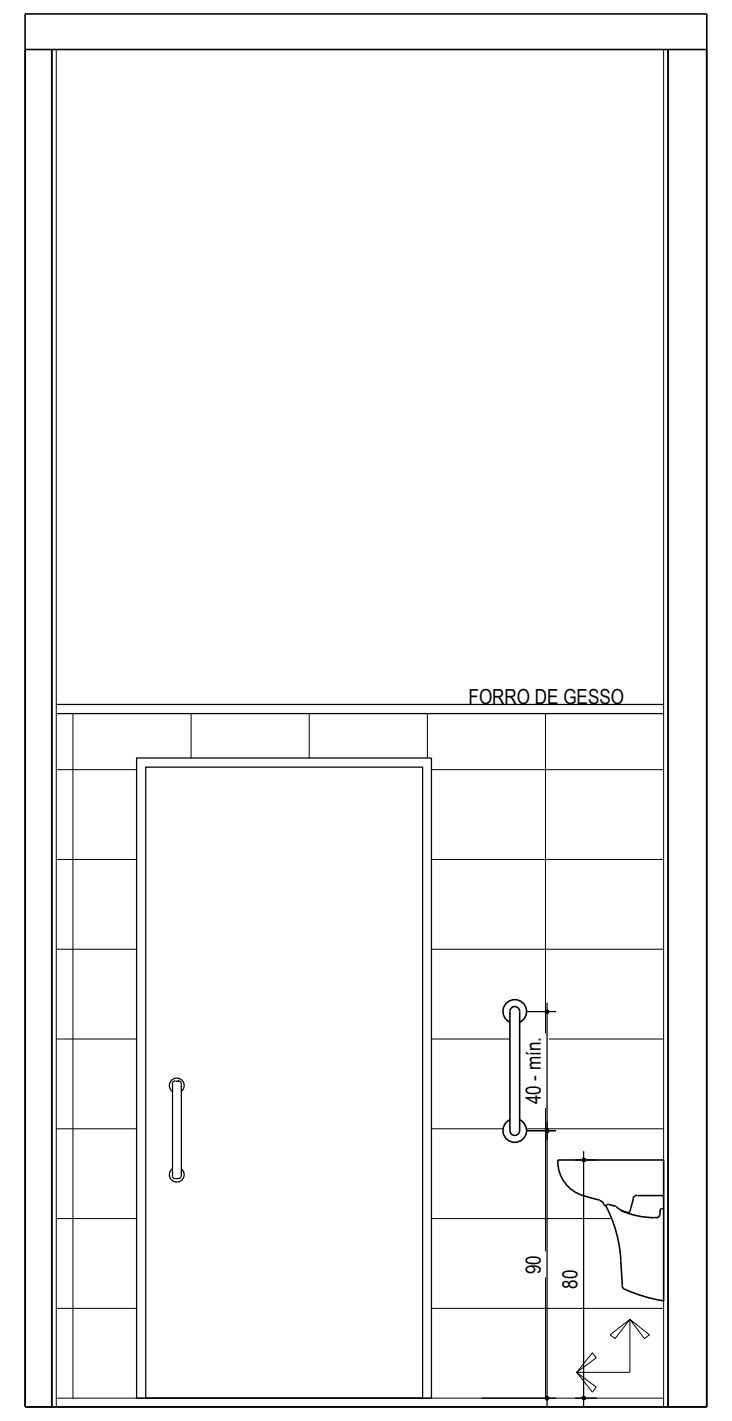
FORRO DE GESSO
90
80

VISTA 03 - BANHO
OPÇÃO DE VENDAS
TORRES A E B: APARTAMENTO FINAL 03
5º PAVIMENTO

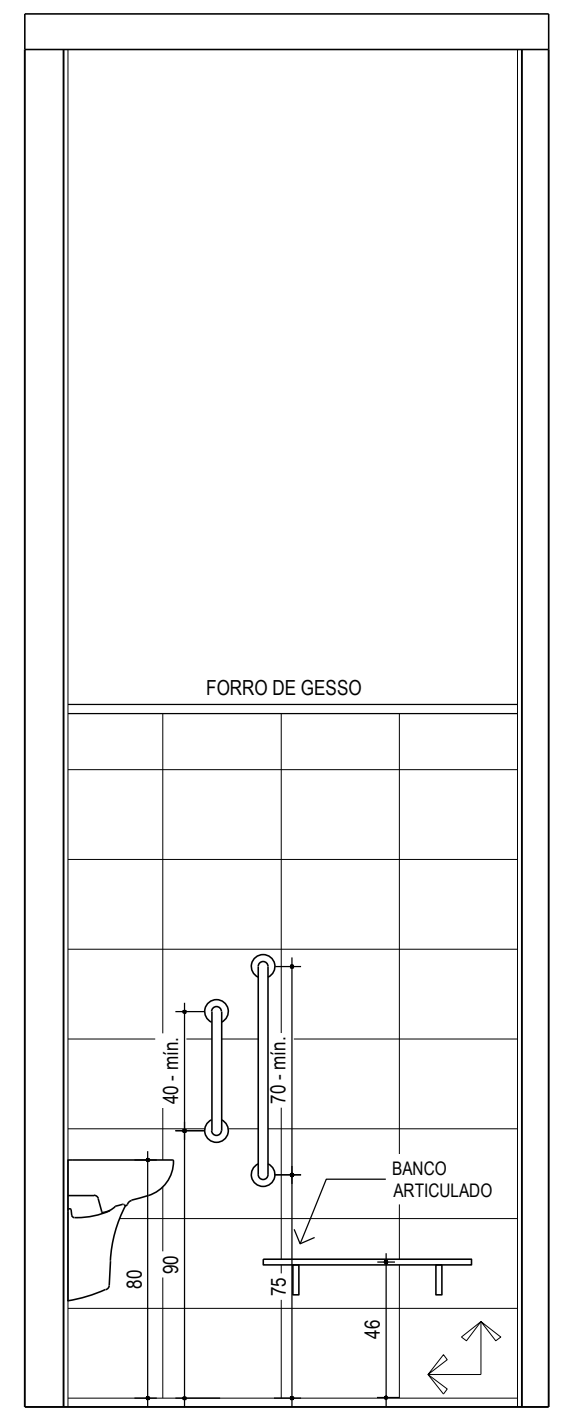
FORRO DE GESSO
BANCO ARTICULADO

VISTA 02 - BANHO
OPÇÃO DE VENDAS
TORRES A E B: APARTAMENTO FINAL 03
5º PAVIMENTO

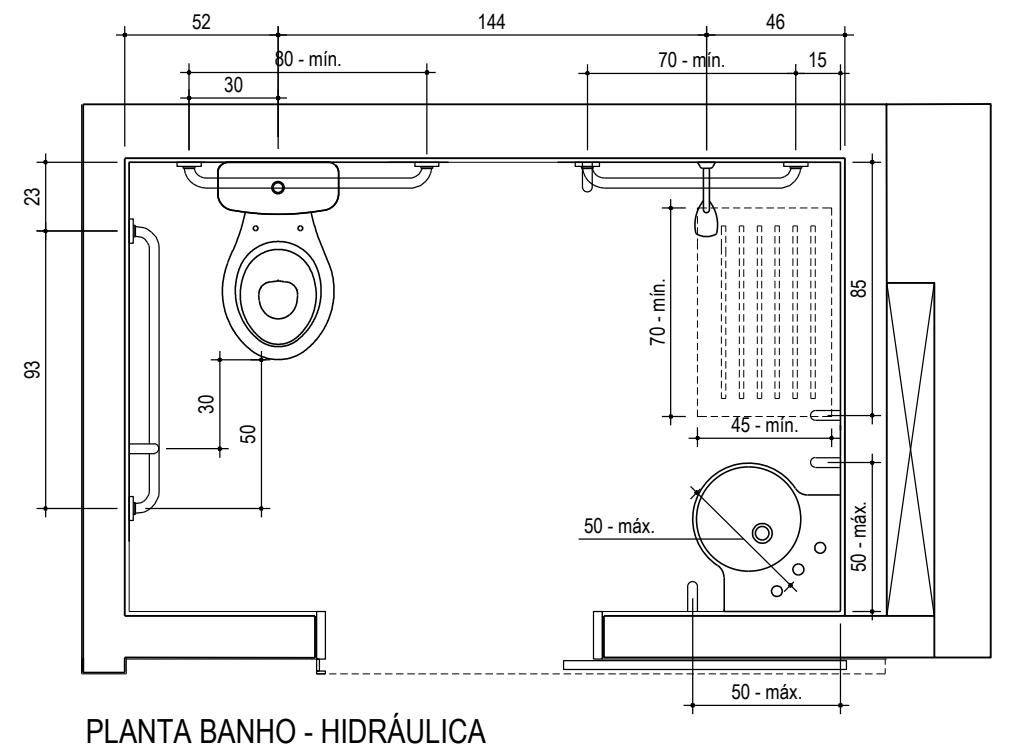
45 - mín.
50 - máx.

PLANTA BANHO - HIDRÁULICA
OPÇÃO DE VENDAS
TORRE A: APARTAMENTO FINAL 04
TORRE B: APARTAMENTO FINAL 02
5º PAVIMENTO

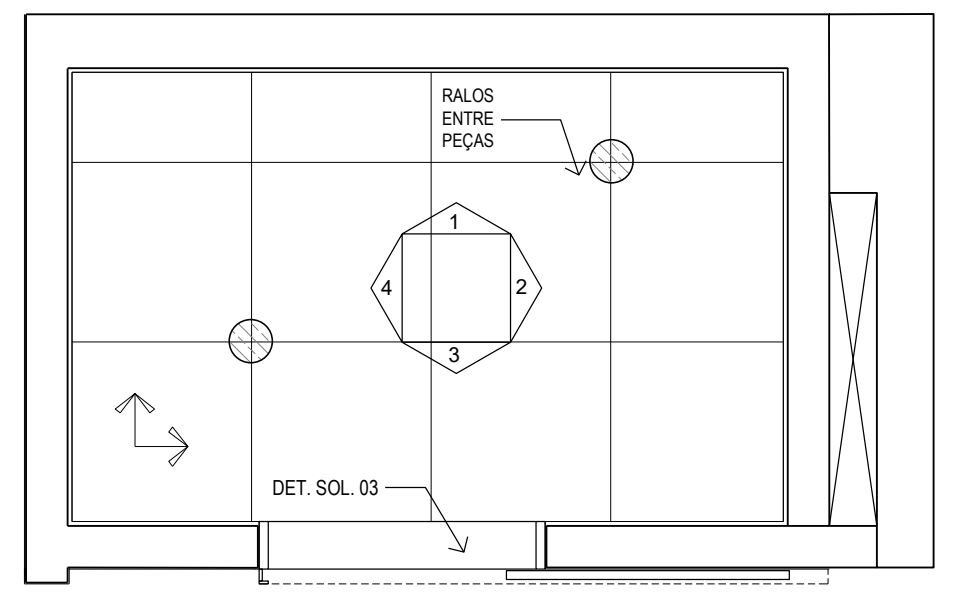
RALOS ENTRE PEÇAS
DET. SOL. 03

PLANTA BANHO -PISO
OPÇÃO DE VENDAS
TORRE A: APARTAMENTO FINAL 04
TORRE B: APARTAMENTO FINAL 02
5º PAVIMENTO

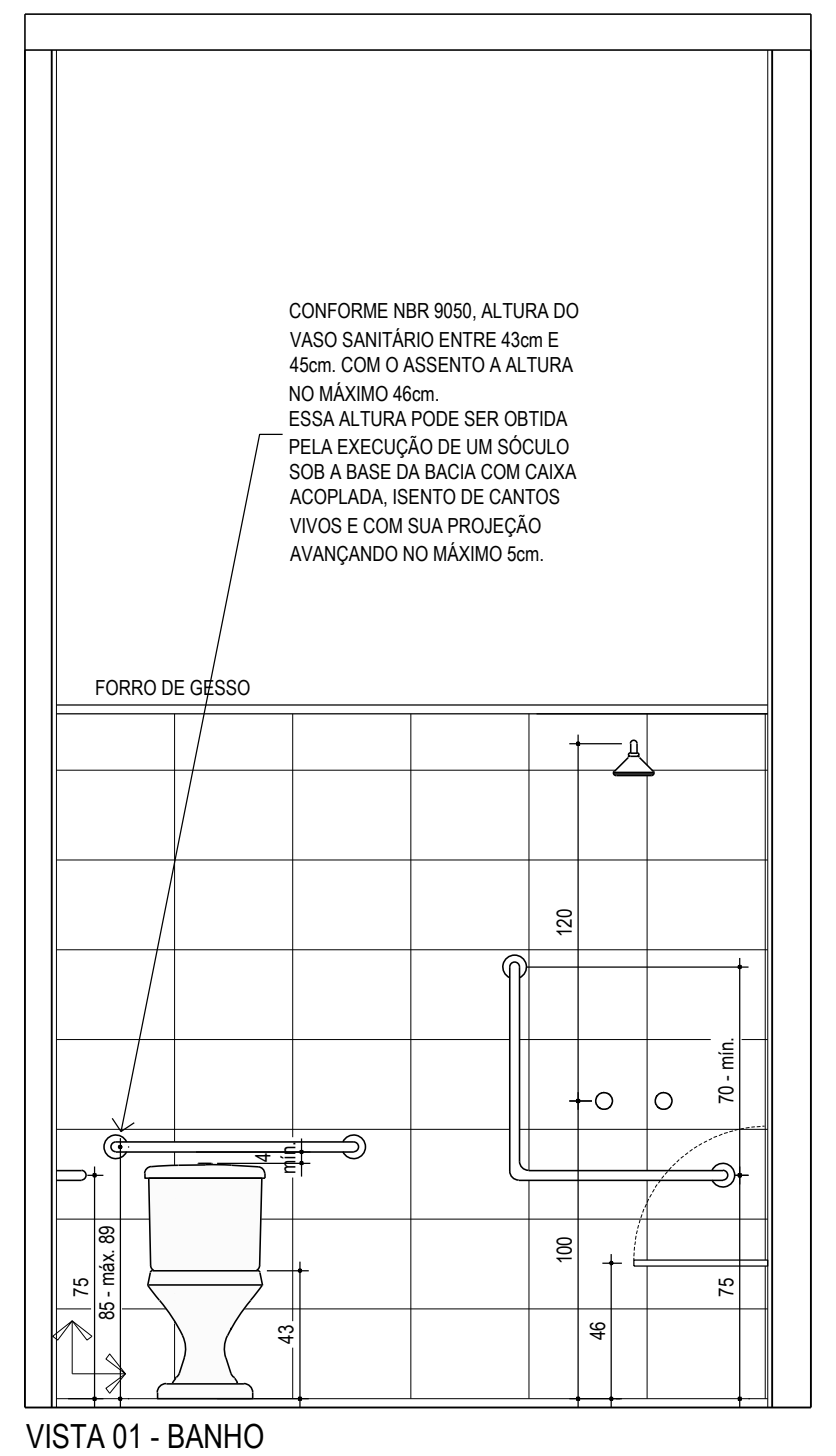
CONFORME NBR 9050, ALTURA DO VASO SANITÁRIO ENTRE 43cm E 45cm. COM O ASSENTO A ALTURA NO MÁXIMO 46cm. ESSA ALTURA PODE SER OBTIDA PELA EXECUÇÃO DE UM SÓCULO SOB A BASE DA BACIA COM CAIXA ACOPLADA, ISENTO DE CANTOS VIVOS E COM SUA PROJEÇÃO AVANÇANDO NO MÁXIMO 5cm.
FORRO DE GESSO
85 - máx. 89

VISTA 01 - BANHO
OPÇÃO DE VENDAS
TORRE A: APARTAMENTO FINAL 04
TORRE B: APARTAMENTO FINAL 02
5º PAVIMENTO

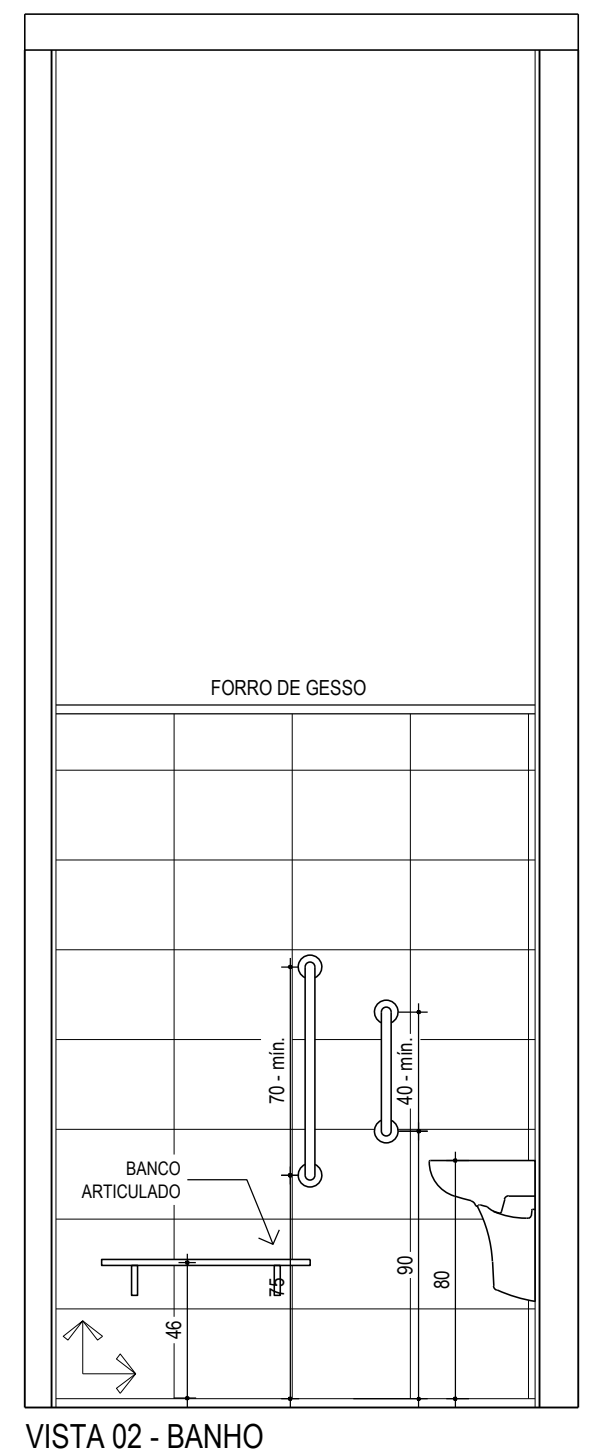
FORRO DE GESSO
BANCO ARTICULADO

VISTA 02 - BANHO
OPÇÃO DE VENDAS
TORRE A: APARTAMENTO FINAL 04
TORRE B: APARTAMENTO FINAL 02
5º PAVIMENTO

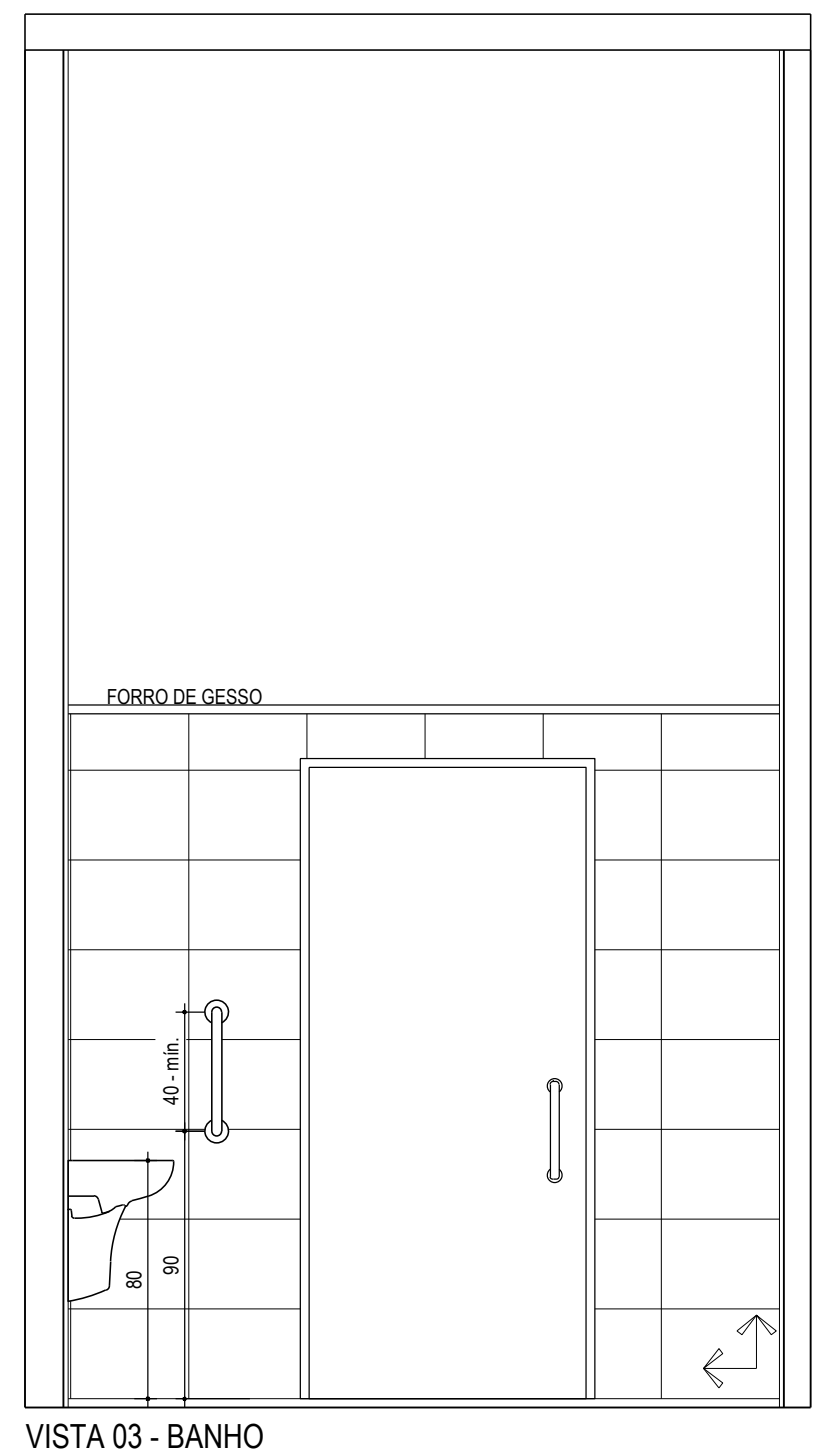
FORRO DE GESSO

VISTA 03 - BANHO
OPÇÃO DE VENDAS
TORRE A: APARTAMENTO FINAL 04
TORRE B: APARTAMENTO FINAL 02
5º PAVIMENTO

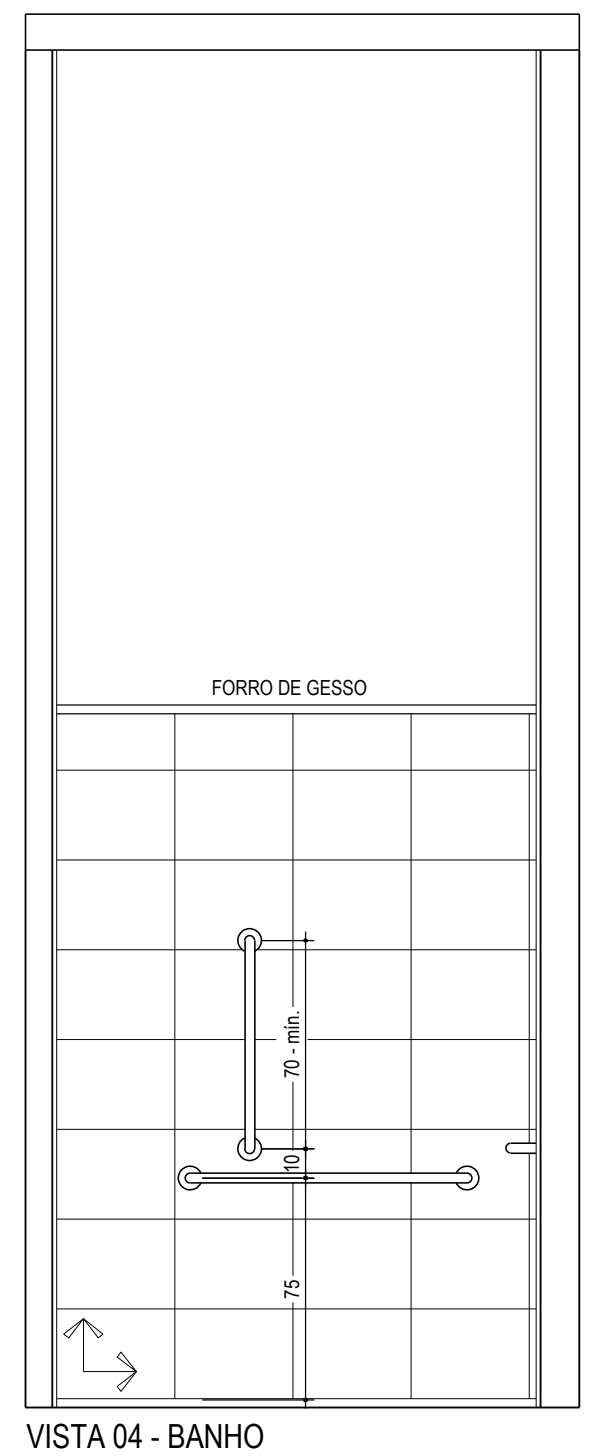
FORRO DE GESSO

VISTA 04 - BANHO
OPÇÃO DE VENDAS
TORRE A: APARTAMENTO FINAL 04
TORRE B: APARTAMENTO FINAL 02
5º PAVIMENTO

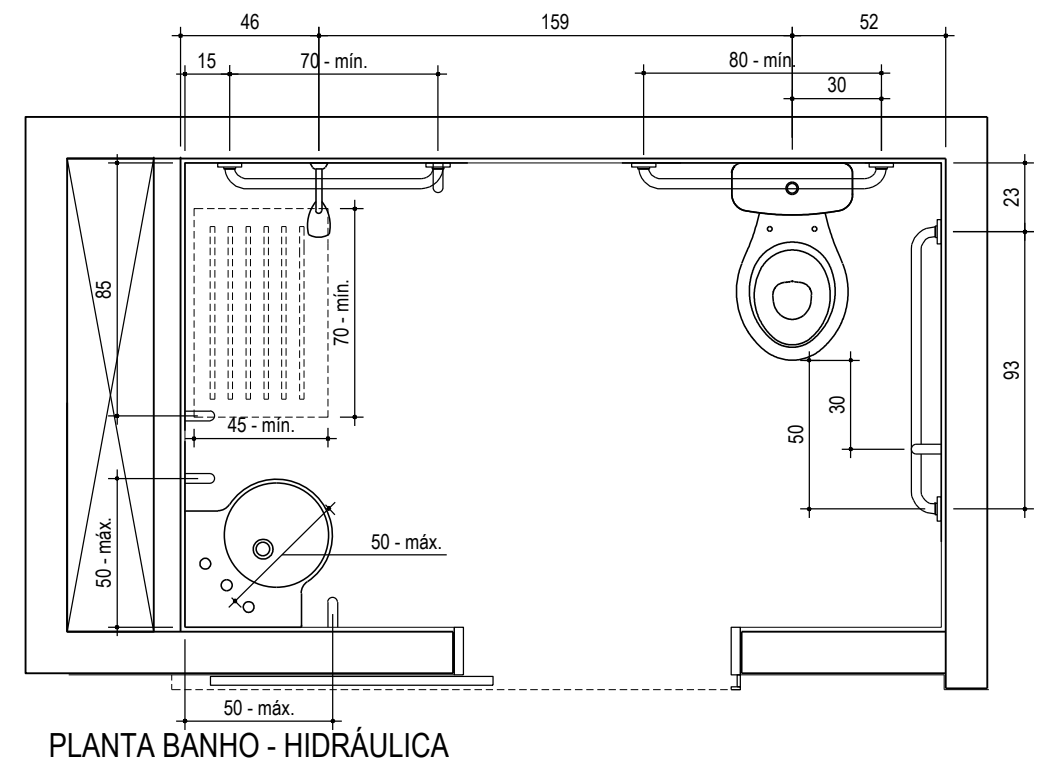
45 - mín.
50 - máx.

PLANTA BANHO - HIDRÁULICA
OPÇÃO DE VENDAS
TORRE A: APARTAMENTO FINAL 02
TORRE B: APARTAMENTO FINAL 04
5º PAVIMENTO

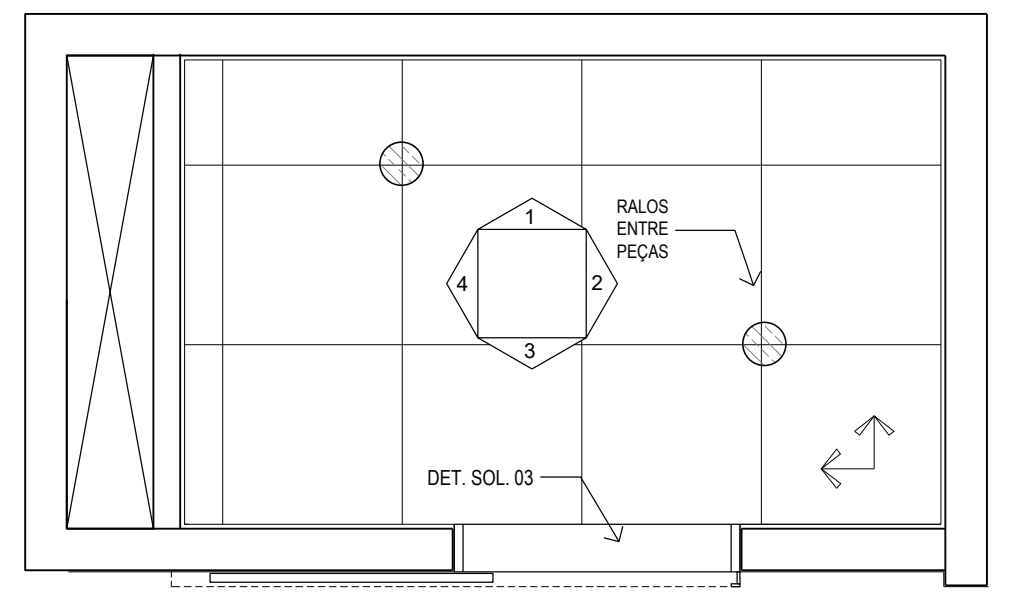
RALOS ENTRE PEÇAS
DET. SOL. 03

PLANTA BANHO -PISO
OPÇÃO DE VENDAS
TORRE A: APARTAMENTO FINAL 02
TORRE B: APARTAMENTO FINAL 04
5º PAVIMENTO

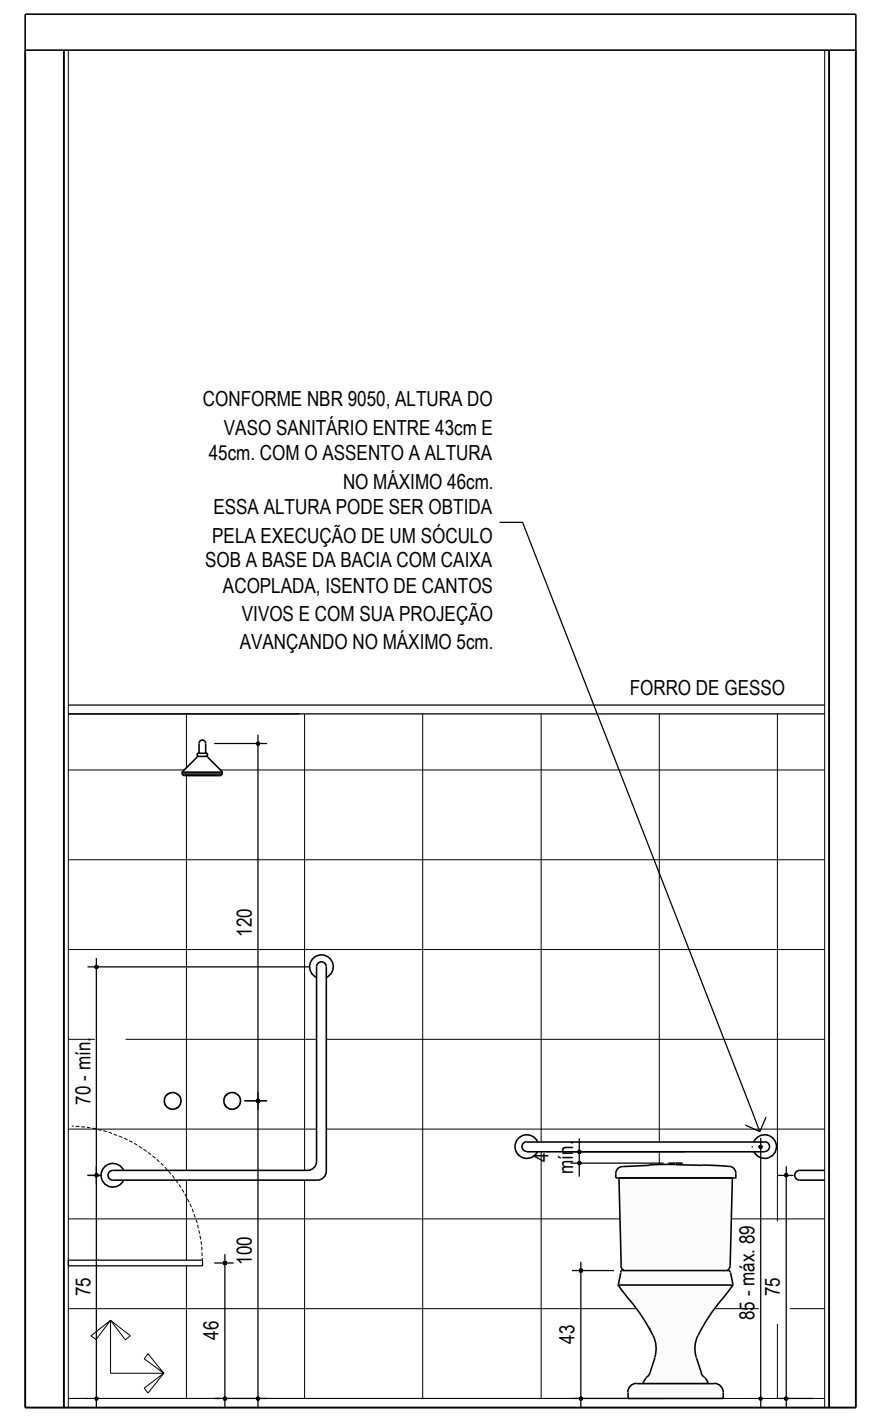
CONFORME NBR 9050, ALTURA DO VASO SANITÁRIO ENTRE 43cm E 45cm. COM O ASSENTO A ALTURA NO MÁXIMO 46cm. ESSA ALTURA PODE SER OBTIDA PELA EXECUÇÃO DE UM SÓCULO SOB A BASE DA BACIA COM CAIXA ACOPLADA, ISENTO DE CANTOS VIVOS E COM SUA PROJEÇÃO AVANÇANDO NO MÁXIMO 5cm.
FORRO DE GESSO
85 - máx. 89

VISTA 01 - BANHO
OPÇÃO DE VENDAS
TORRE A: APARTAMENTO FINAL 02
TORRE B: APARTAMENTO FINAL 04
5º PAVIMENTO

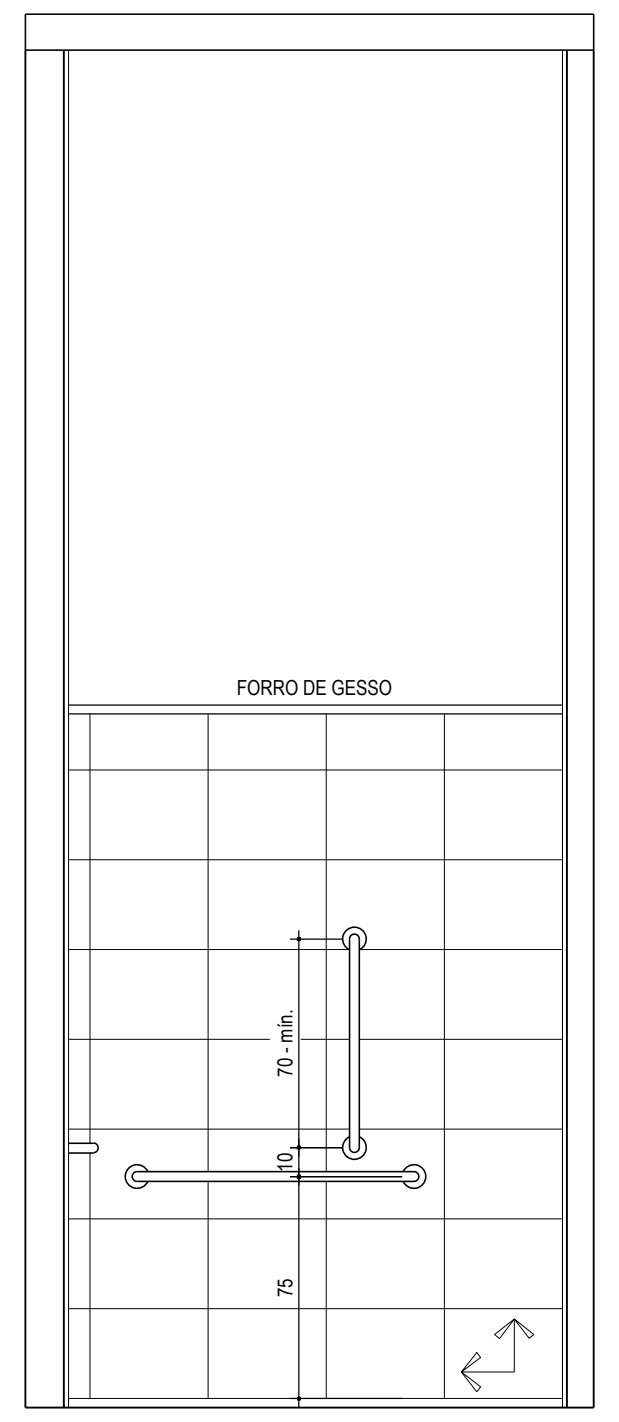
FORRO DE GESSO

VISTA 02 - BANHO
OPÇÃO DE VENDAS
TORRE A: APARTAMENTO FINAL 02
TORRE B: APARTAMENTO FINAL 04
5º PAVIMENTO

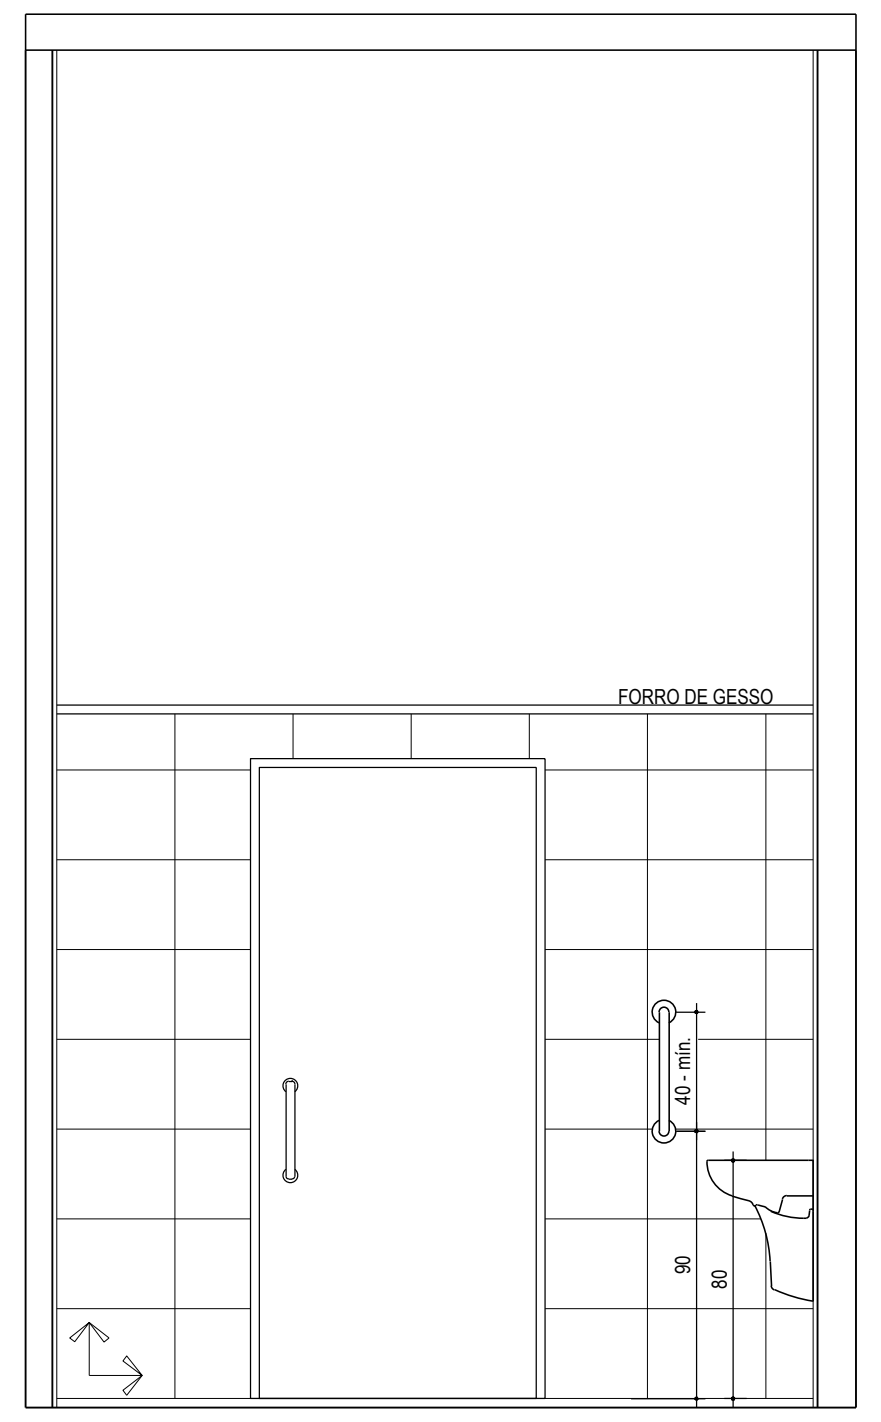
FORRO DE GESSO

VISTA 03 - BANHO
OPÇÃO DE VENDAS
TORRE A: APARTAMENTO FINAL 02
TORRE B: APARTAMENTO FINAL 04
5º PAVIMENTO

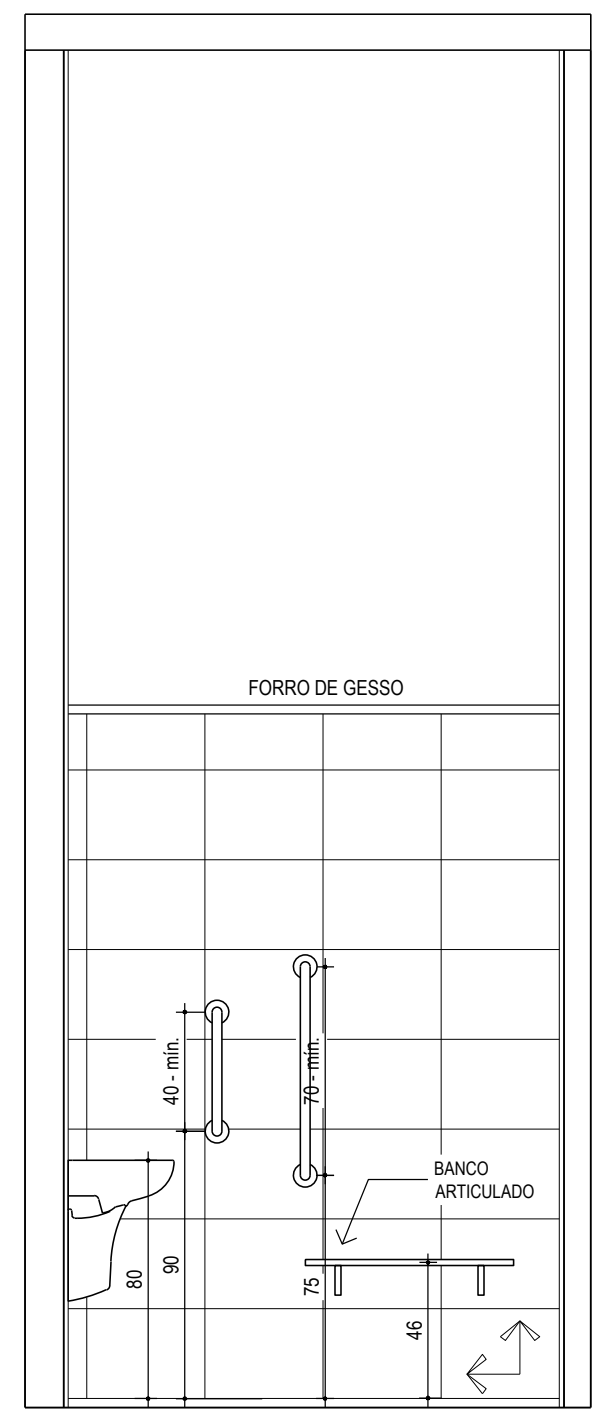
FORRO DE GESSO
BANCO ARTICULADO

VISTA 04 - BANHO
OPÇÃO DE VENDAS
TORRE A: APARTAMENTO FINAL 02
TORRE B: APARTAMENTO FINAL 04
5º PAVIMENTO

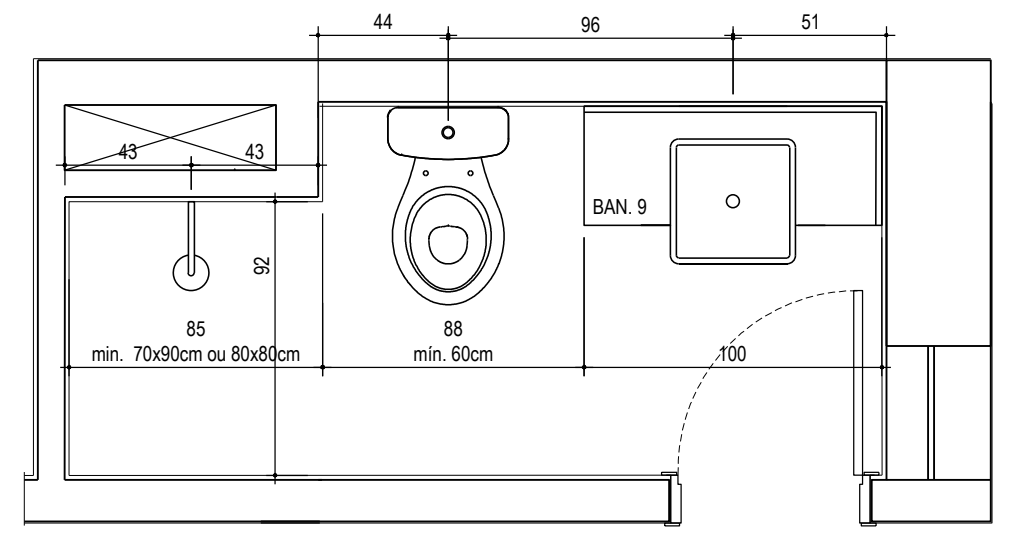
44
96
51
BAN. 9
85
min. 70x90cm ou 80x80cm
88
min. 60cm
100

PLANTA BANHO 1 - HIDRÁULICA
OPÇÃO DE VENDAS
TORRE A: APARTAMENTO FINAL 02
TORRE B: APARTAMENTO FINAL 04
5º PAVIMENTO

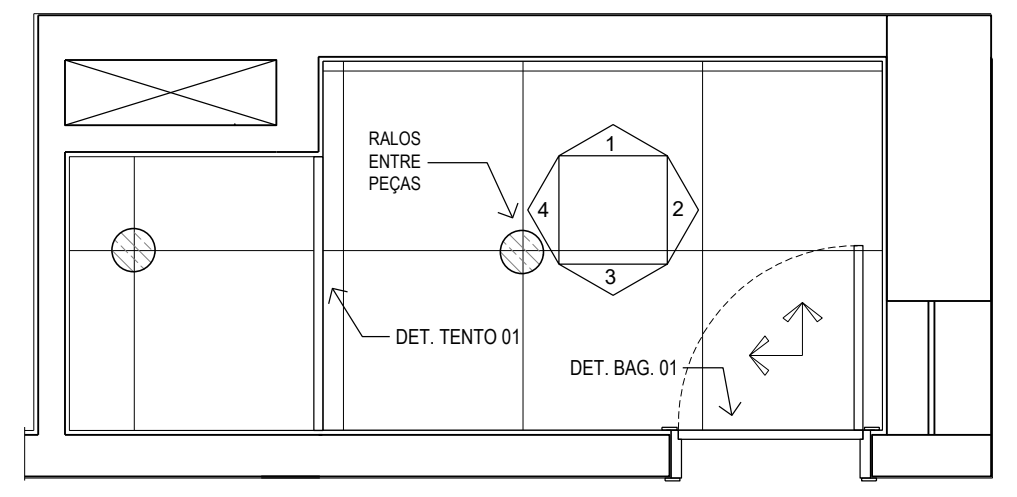
RALOS ENTRE PEÇAS
DET. TENTO 01
DET. BAG. 01

PLANTA BANHO 1 - PISO
OPÇÃO DE VENDAS
TORRE A: APARTAMENTO FINAL 02
TORRE B: APARTAMENTO FINAL 04
5º PAVIMENTO

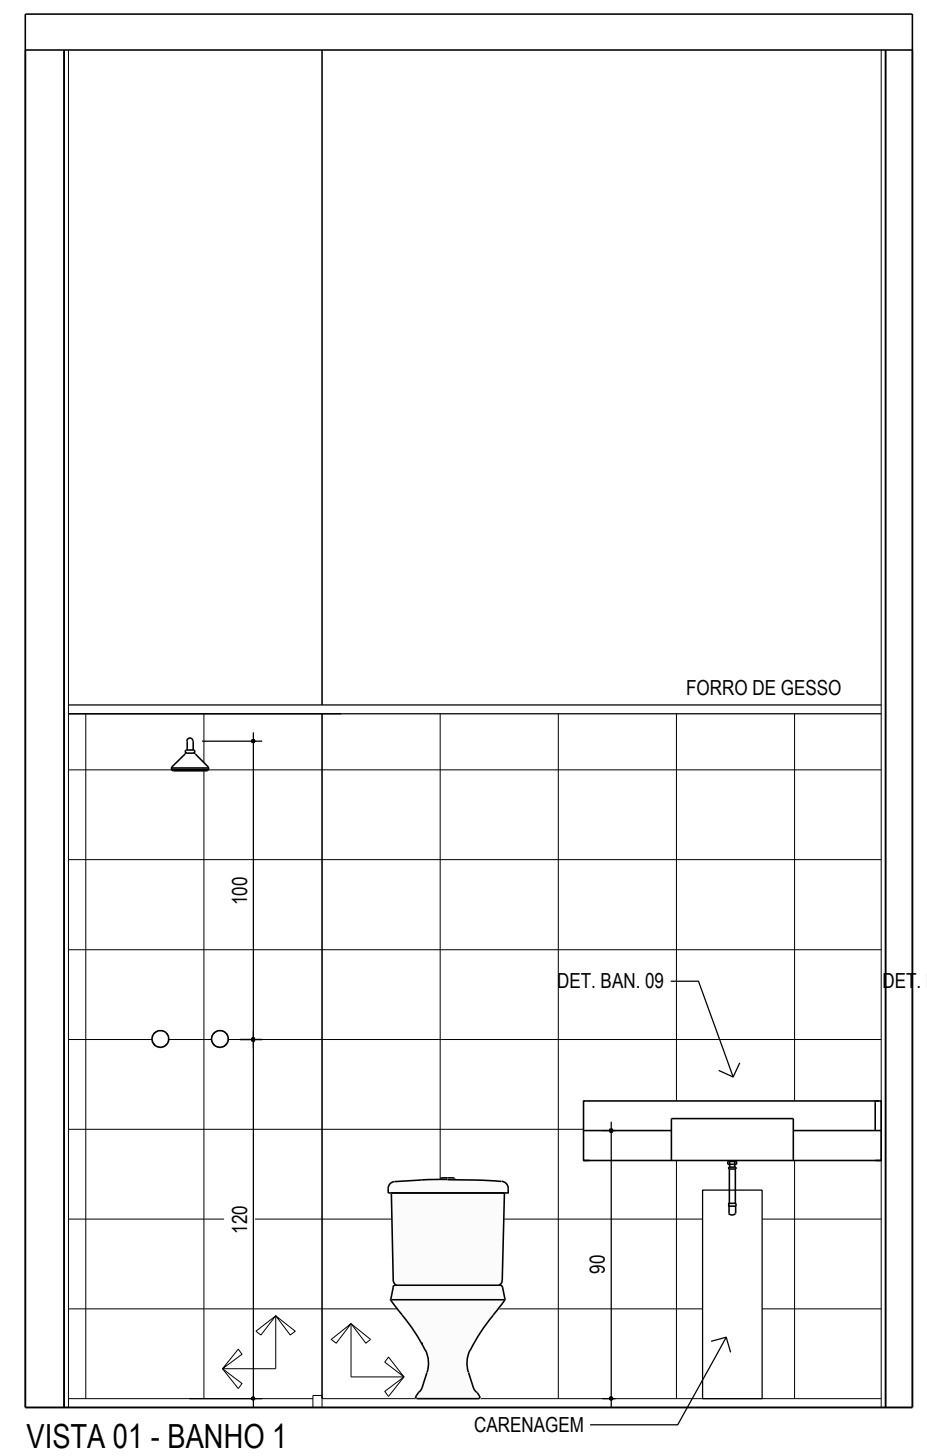
FORRO DE GESSO
DET. BAN. 09
120
90
CARENAGEM

VISTA 01 - BANHO 1
OPÇÃO DE VENDAS
TORRE A: APARTAMENTO FINAL 02
TORRE B: APARTAMENTO FINAL 04
5º PAVIMENTO

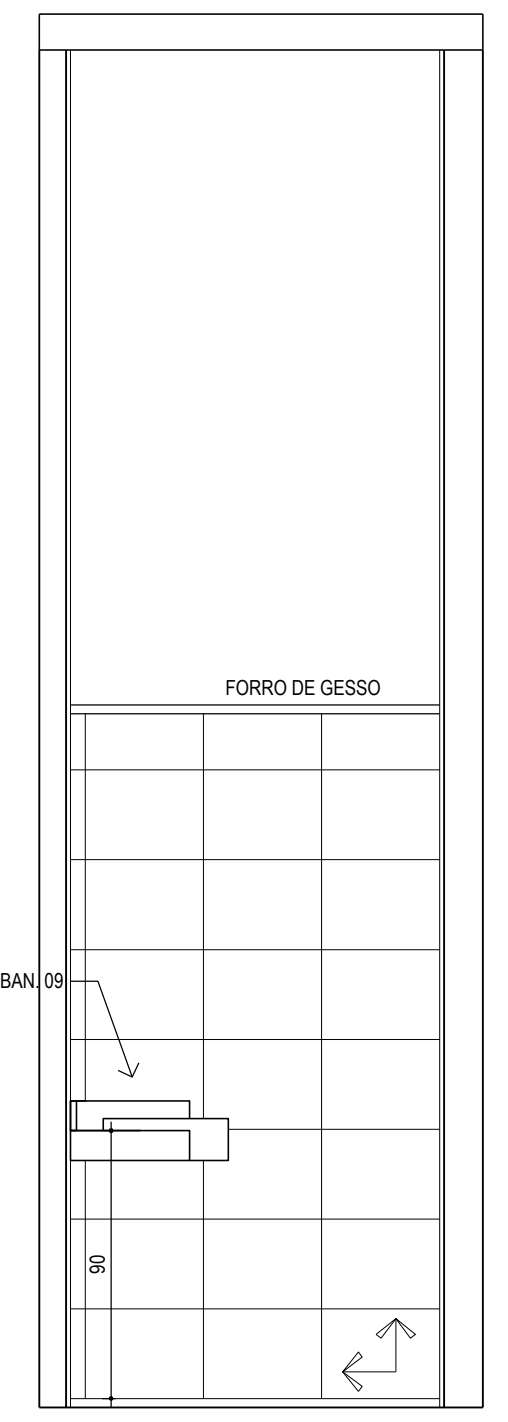
FORRO DE GESSO
DET. BAN. 09
90

VISTA 02 - BANHO 1
OPÇÃO DE VENDAS
TORRE A: APARTAMENTO FINAL 02
TORRE B: APARTAMENTO FINAL 04
5º PAVIMENTO

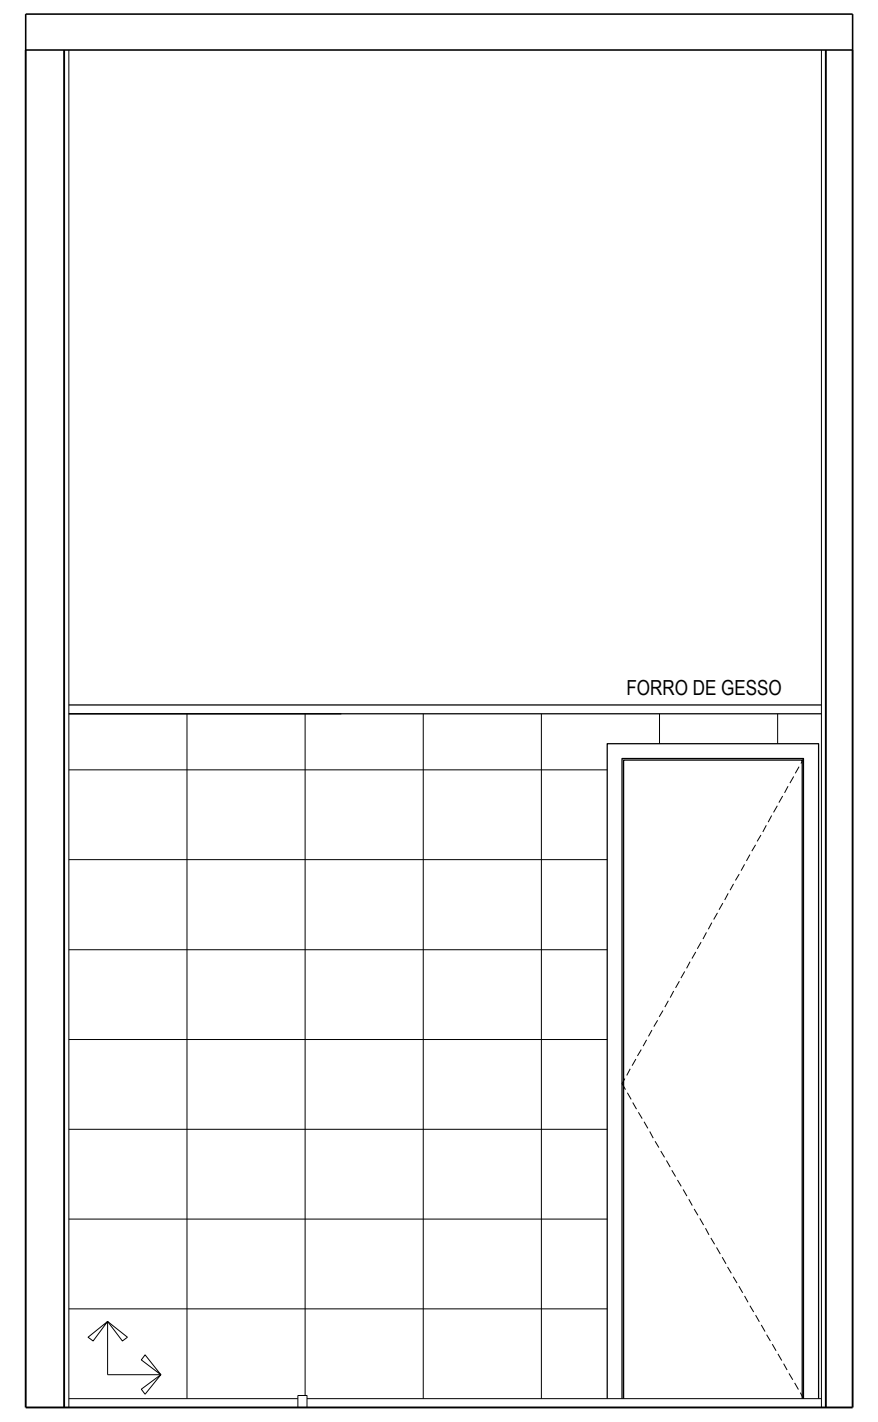
FORRO DE GESSO

VISTA 03 - BANHO 1
OPÇÃO DE VENDAS
TORRE A: APARTAMENTO FINAL 02
TORRE B: APARTAMENTO FINAL 04
5º PAVIMENTO

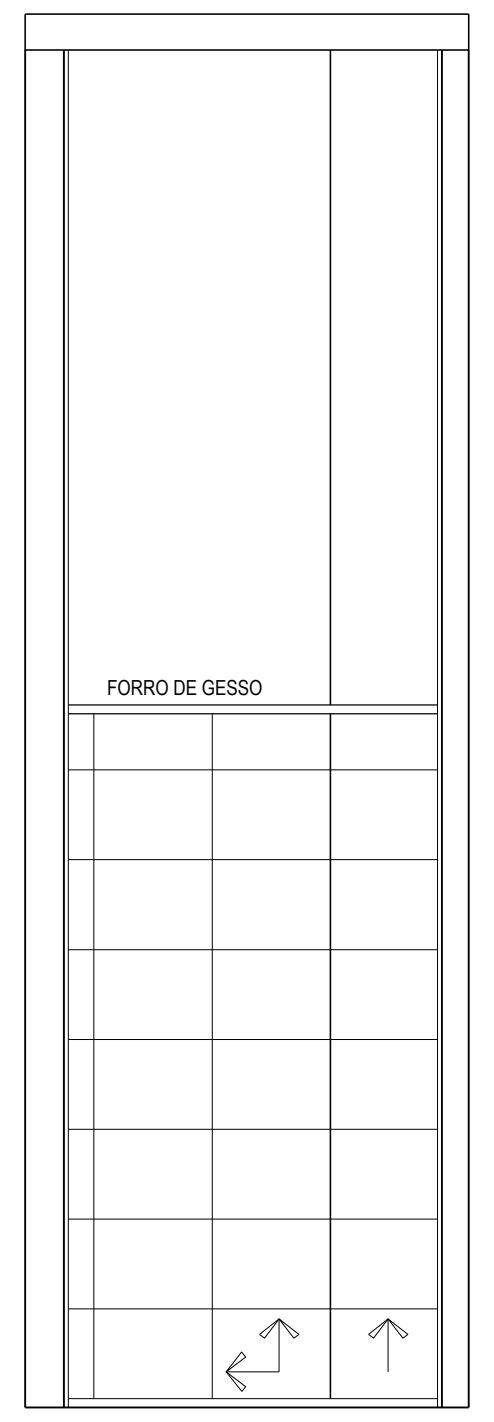
FORRO DE GESSO

VISTA 04 - BANHO 1
OPÇÃO DE VENDAS
TORRE A: APARTAMENTO FINAL 02
TORRE B: APARTAMENTO FINAL 04
5º PAVIMENTO

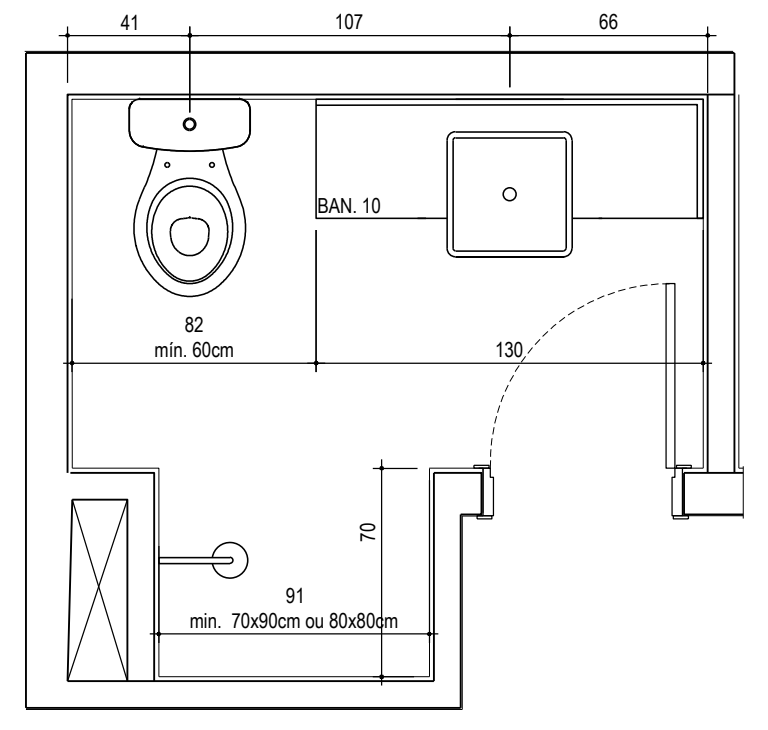
41
107
66
BAN. 10
82
min. 60cm
130
91
min. 70x90cm ou 80x80cm

PLANTA BANHO 2 - HIDRÁULICA
OPÇÃO DE VENDAS
TORRE A: APARTAMENTO FINAL 02
TORRE B: APARTAMENTO FINAL 04
5º PAVIMENTO

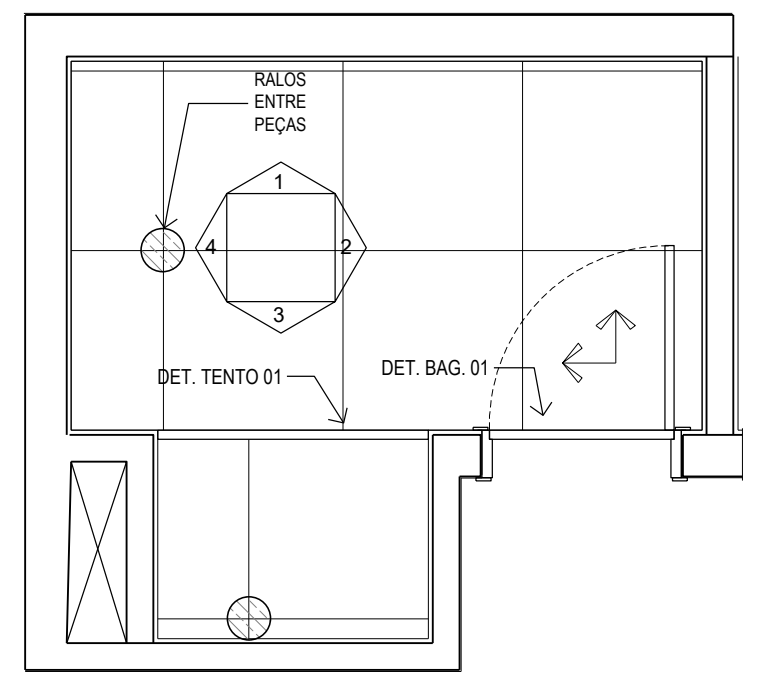
RALOS ENTRE PEÇAS
DET. TENTO 01
DET. BAG. 01

PLANTA BANHO 2 - PISO
OPÇÃO DE VENDAS
TORRE A: APARTAMENTO FINAL 02
TORRE B: APARTAMENTO FINAL 04
5º PAVIMENTO

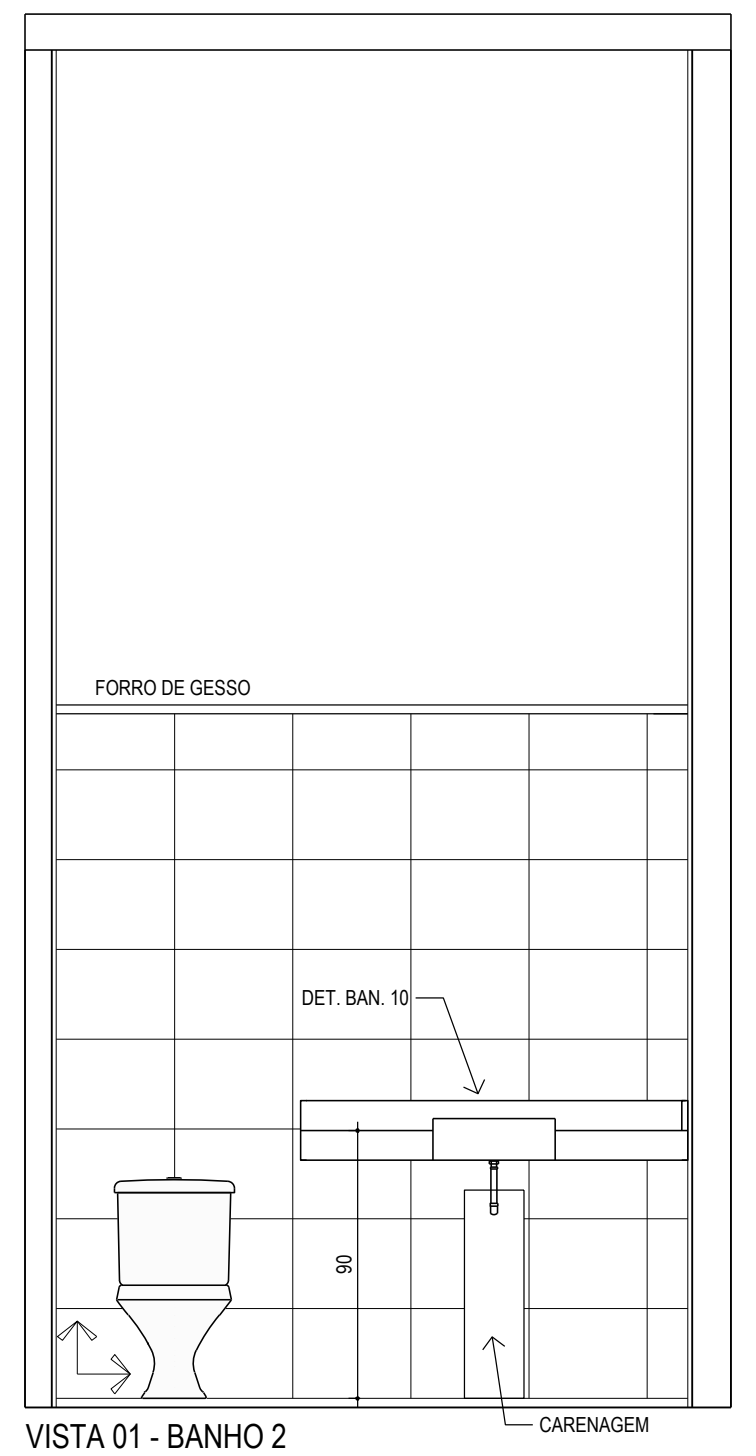
FORRO DE GESSO
DET. BAN. 10
90
CARENAGEM

VISTA 01 - BANHO 2
OPÇÃO DE VENDAS
TORRE A: APARTAMENTO FINAL 02
TORRE B: APARTAMENTO FINAL 04
5º PAVIMENTO

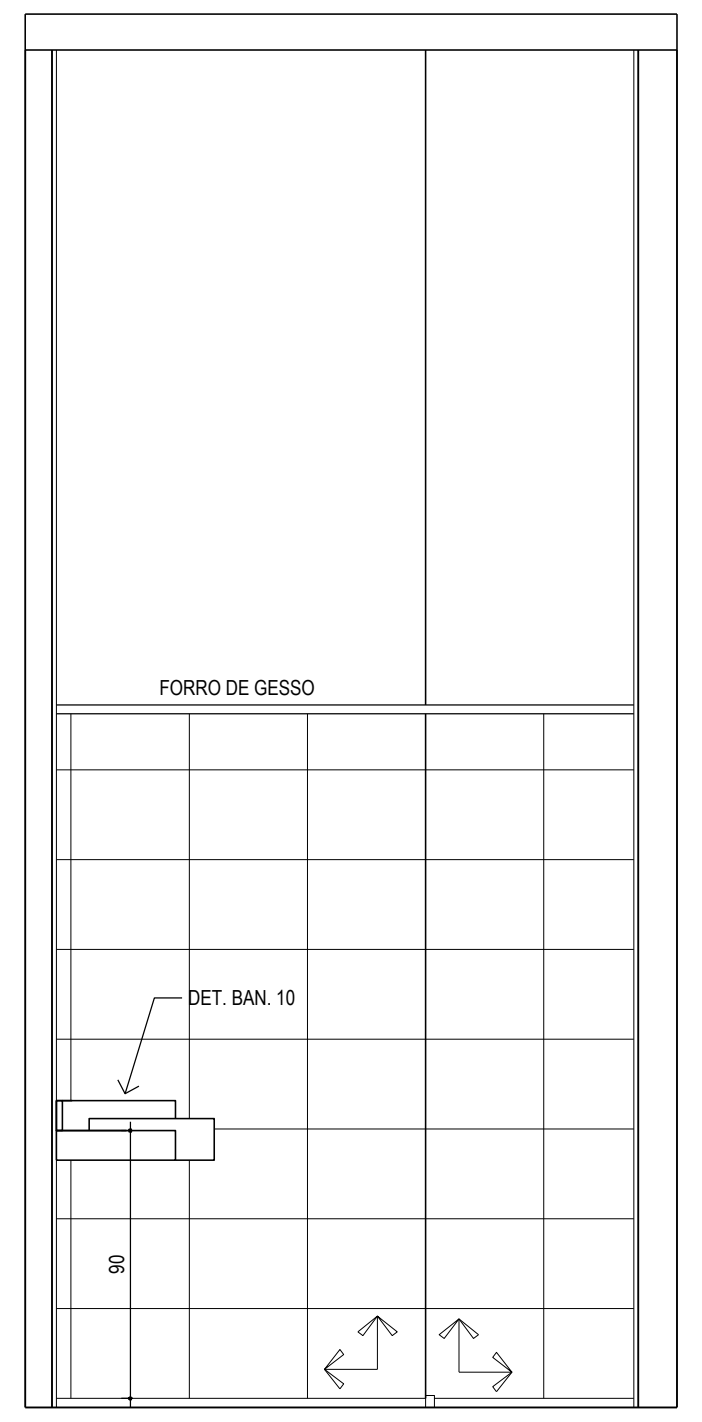
FORRO DE GESSO
DET. BAN. 10
90

VISTA 02 - BANHO 2
OPÇÃO DE VENDAS
TORRE A: APARTAMENTO FINAL 02
TORRE B: APARTAMENTO FINAL 04
5º PAVIMENTO

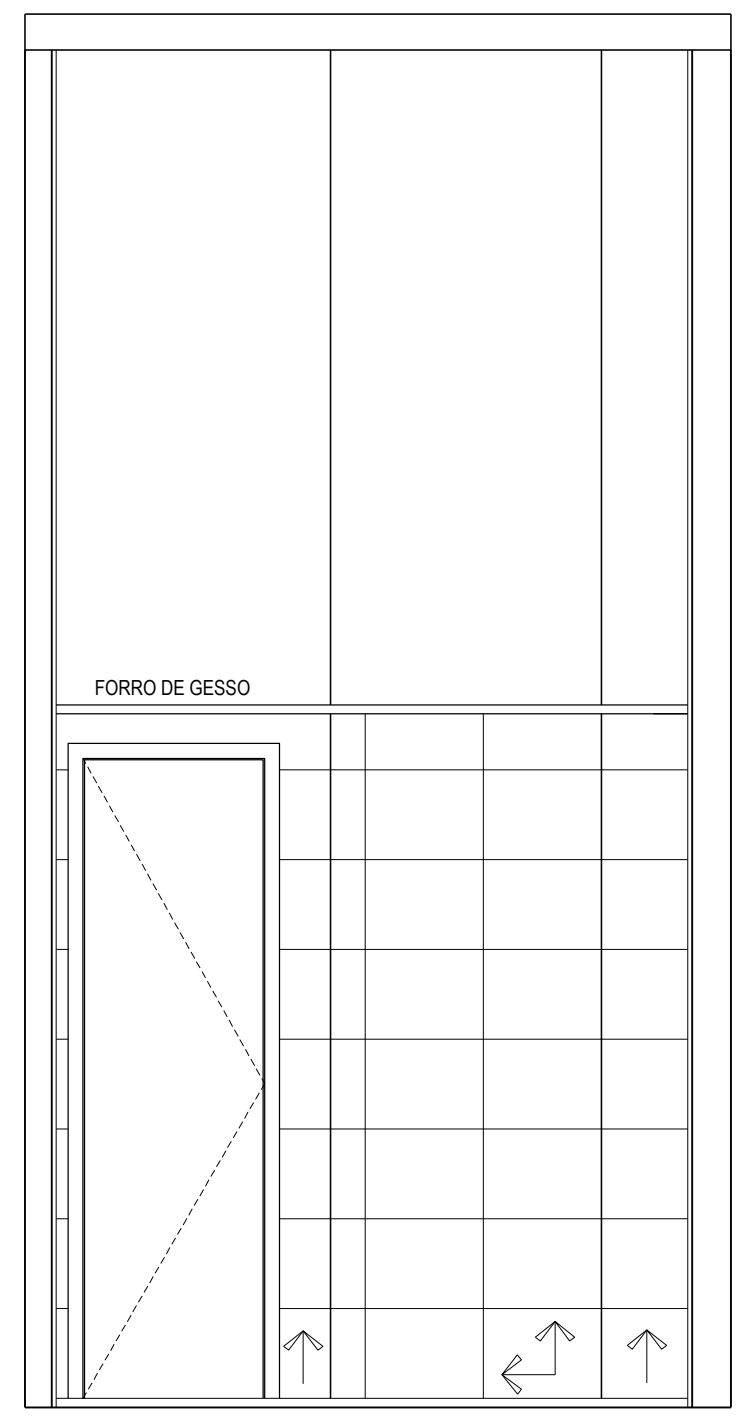
FORRO DE GESSO

VISTA 03 - BANHO 2
OPÇÃO DE VENDAS
TORRE A: APARTAMENTO FINAL 02
TORRE B: APARTAMENTO FINAL 04
5º PAVIMENTO

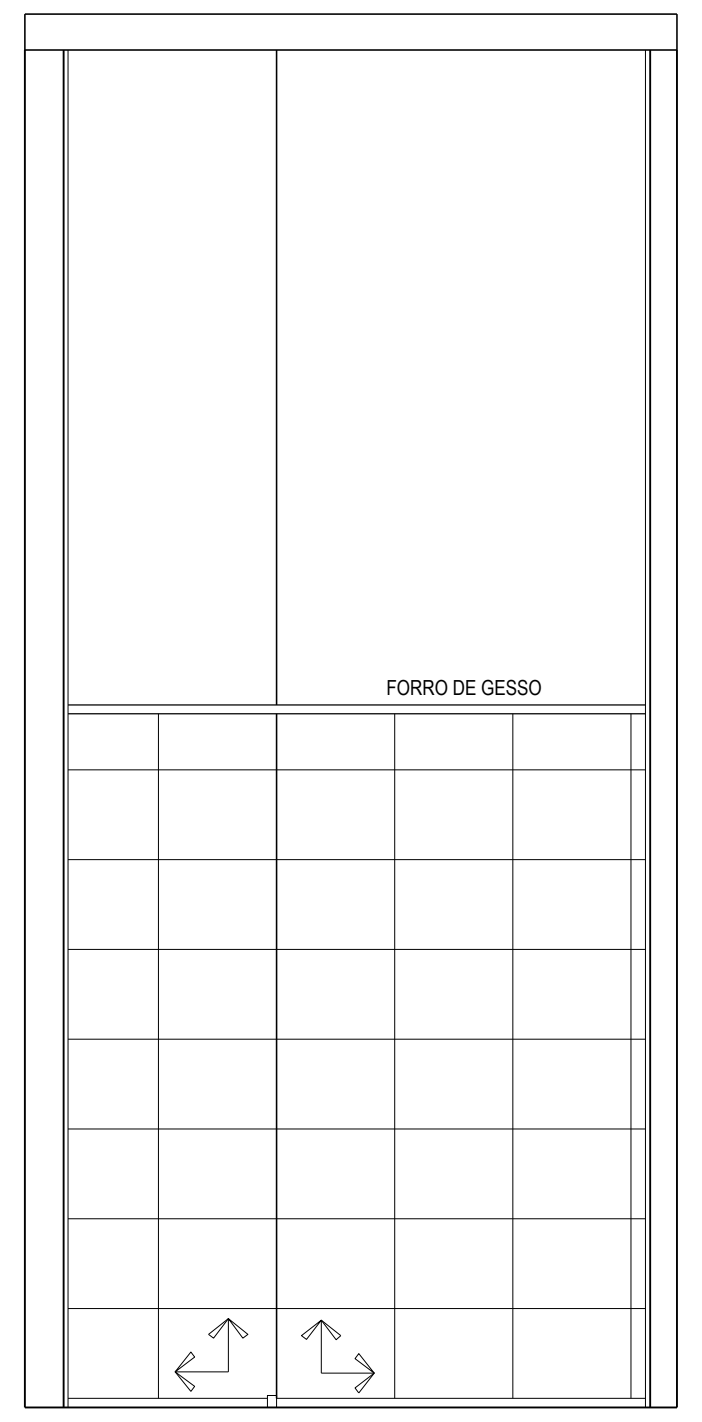
FORRO DE GESSO

VISTA 04 - BANHO 2
OPÇÃO DE VENDAS
TORRE A: APARTAMENTO FINAL 02
TORRE B: APARTAMENTO FINAL 04
5º PAVIMENTO

PLANTAS DE REFERÊNCIA PARA BASE DE PROJETO

REVISÃO	DATA	DESCRIÇÃO	RESP.
00	01/03/2023	EMISSÃO INICIAL	

INCORPORAÇÃO
JERONIMO DA VEIGA
Empreendimentos e Participações Ltda.

CONSTRUÇÃO

PROJETISTA
ADESA ARQUITETURA
RUA PADRE GARCIA VELHO, 73 - CJ. 41
CEP: 05421- 030
FONE: 3032 4355 / 3032 4362

DISCIPLINA
ARQUITETURA

CÓDIGO/OBRA
DUO

FASE
LIBERADO OBRA

EMPREENDIMENTO
DUO
AV_LUZ

ASSUNTO
DETALHAMENTO
ÁREAS_MOLHADAS_PUC_OPÇÃO

FOLHA N.º
ARQ
127

RESPONSÁVEL	SUPERVISOR	COORDENADOR	REVISÃO
ADELINO SANTOS	ADELINO SANTOS	ALISSA LOPES	R00

PROJETISTA	ARQUIVO	ESCALA	DATA
	DUO-ARQ-LO-127-DET-AMO-R00.dwg	1:25	01/03/2023

DIREITOS AUTORAIS RESERVADO A REPRODUÇÃO TOTAL OU PARCIAL SEM PRÉVIA AUTORIZAÇÃO, CONFORME RESOLUÇÃO N° 67, DE 5 DE DEZEMBRO DE 2013