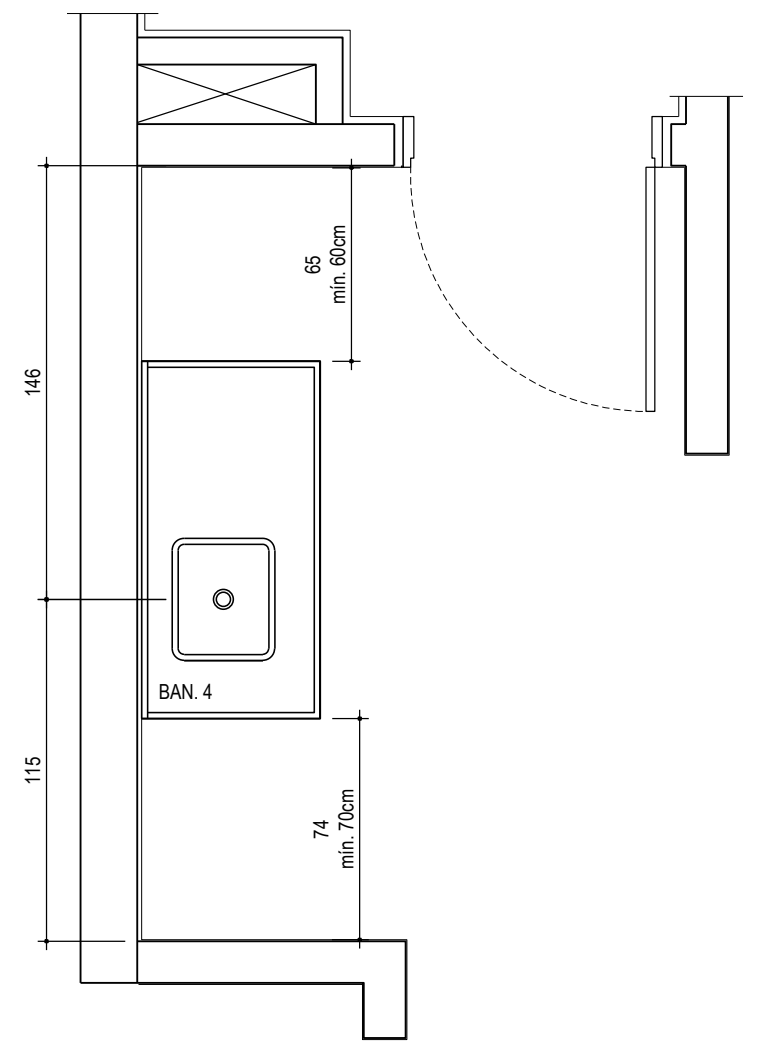

PLANTA COZINHA
TORRES A E B: APTO FINAIS 01 E 05
5º PAVIMENTO

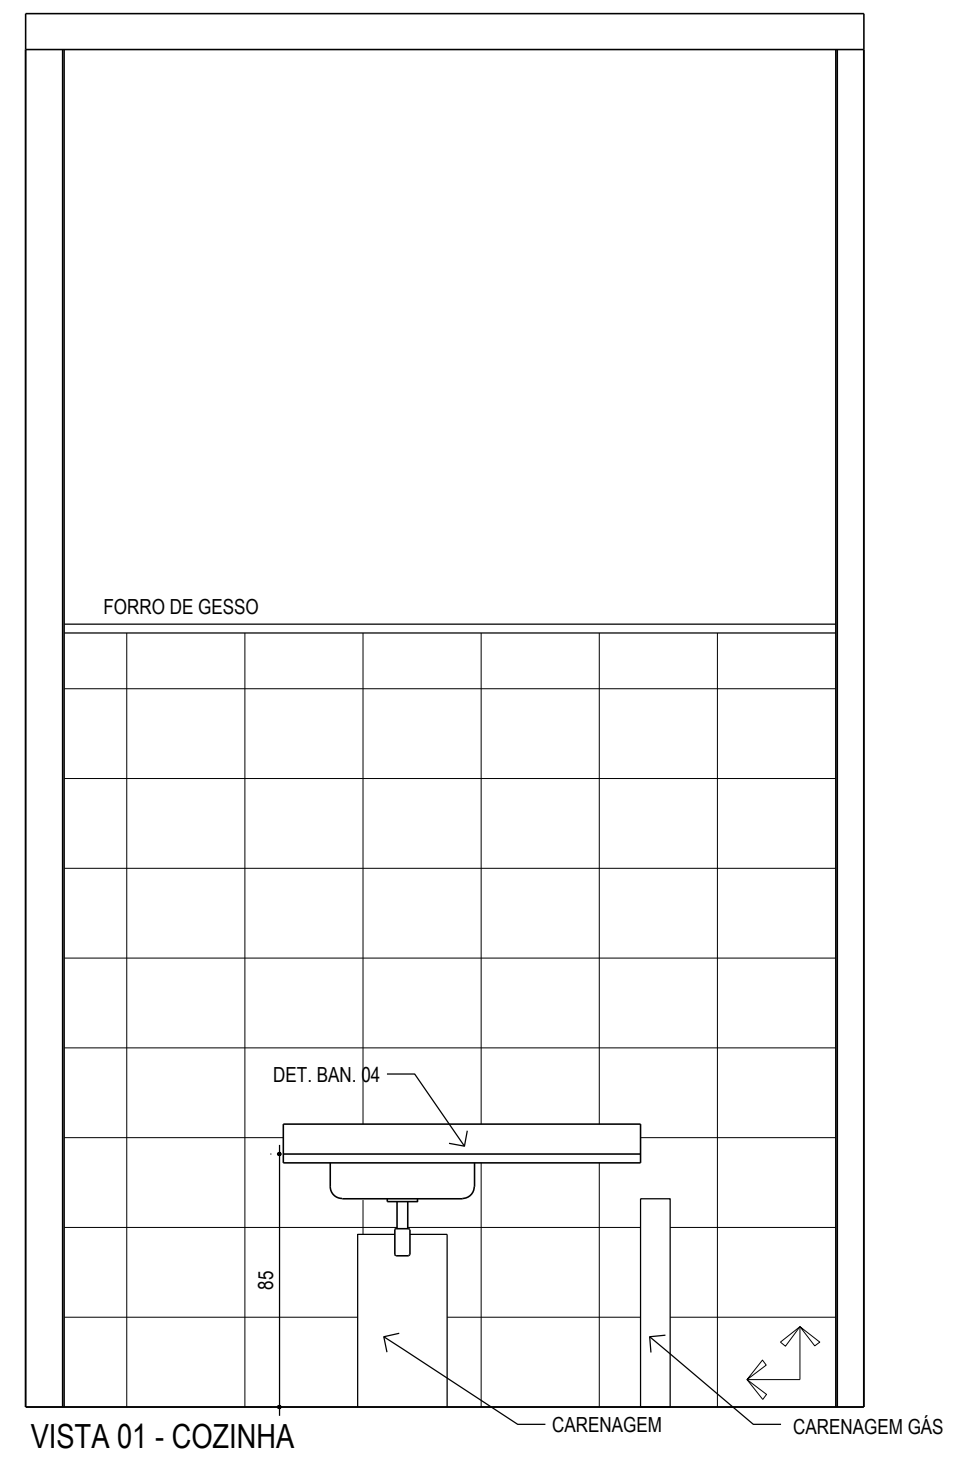

VISTA 01 - COZINHA
TORRES A E B: APTO FINAIS 01 E 05
5º PAVIMENTO

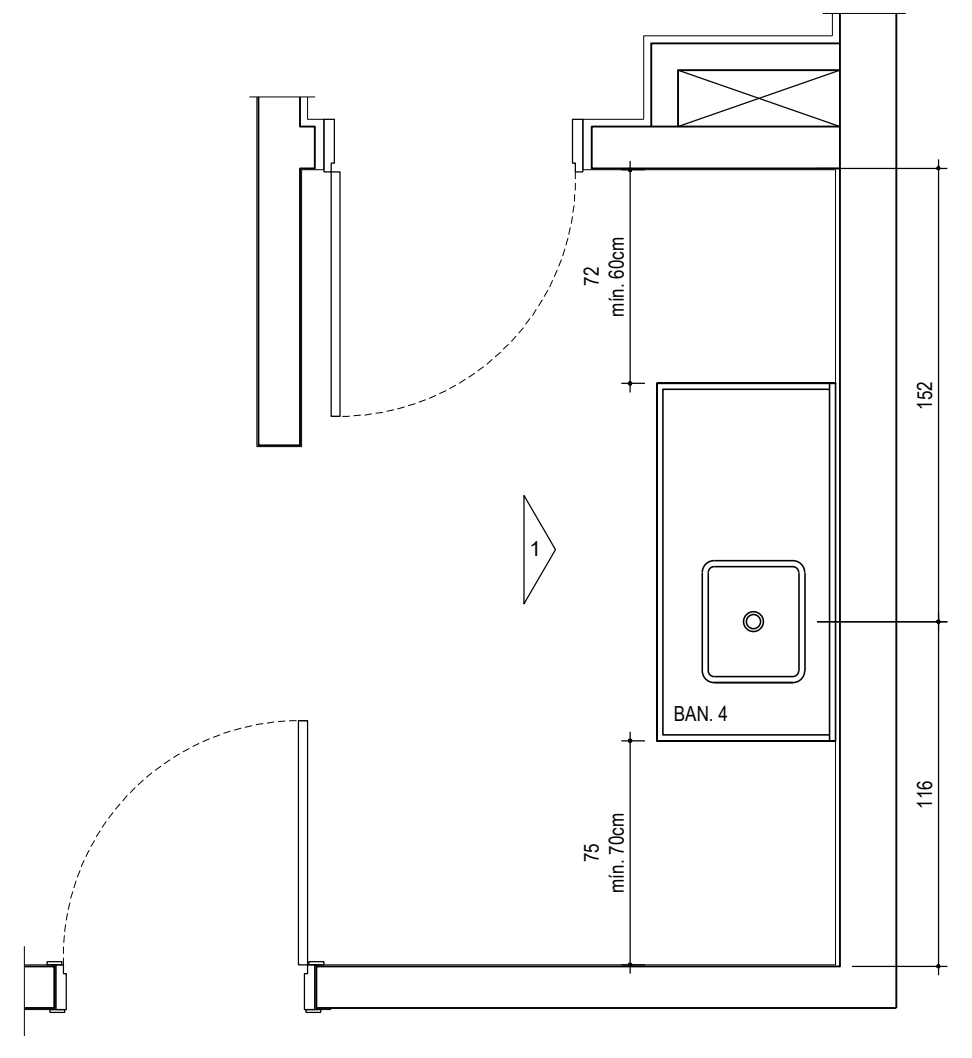

PLANTA COZINHA
TORRES A E B: APTO FINAIS 02, 03 E 04
5º PAVIMENTO

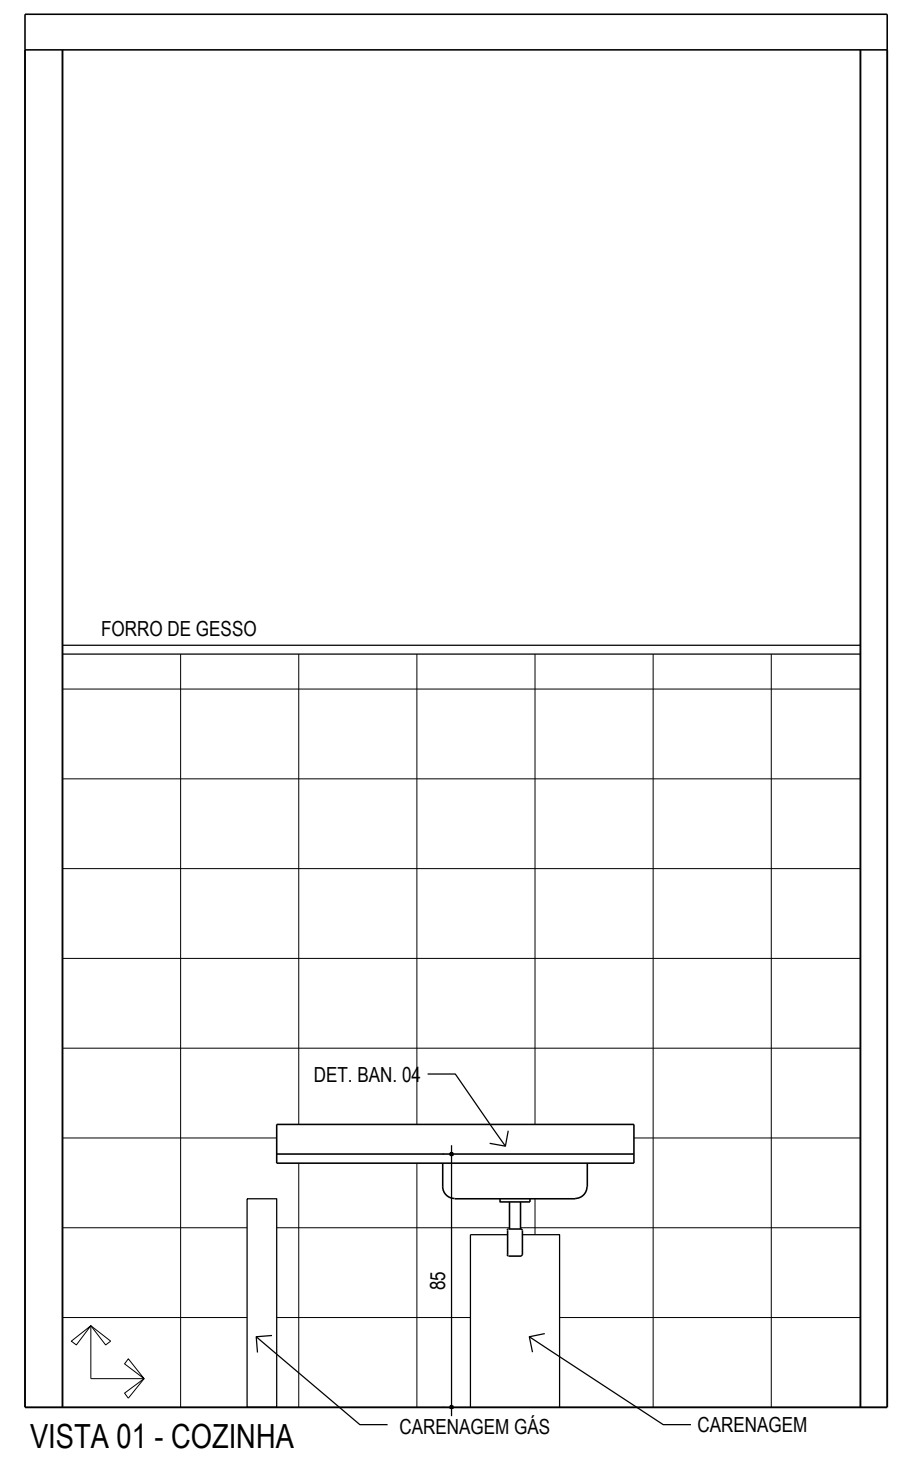

VISTA 01 - COZINHA
TORRES A E B: APTO FINAIS 02, 03 E 04
5º PAVIMENTO

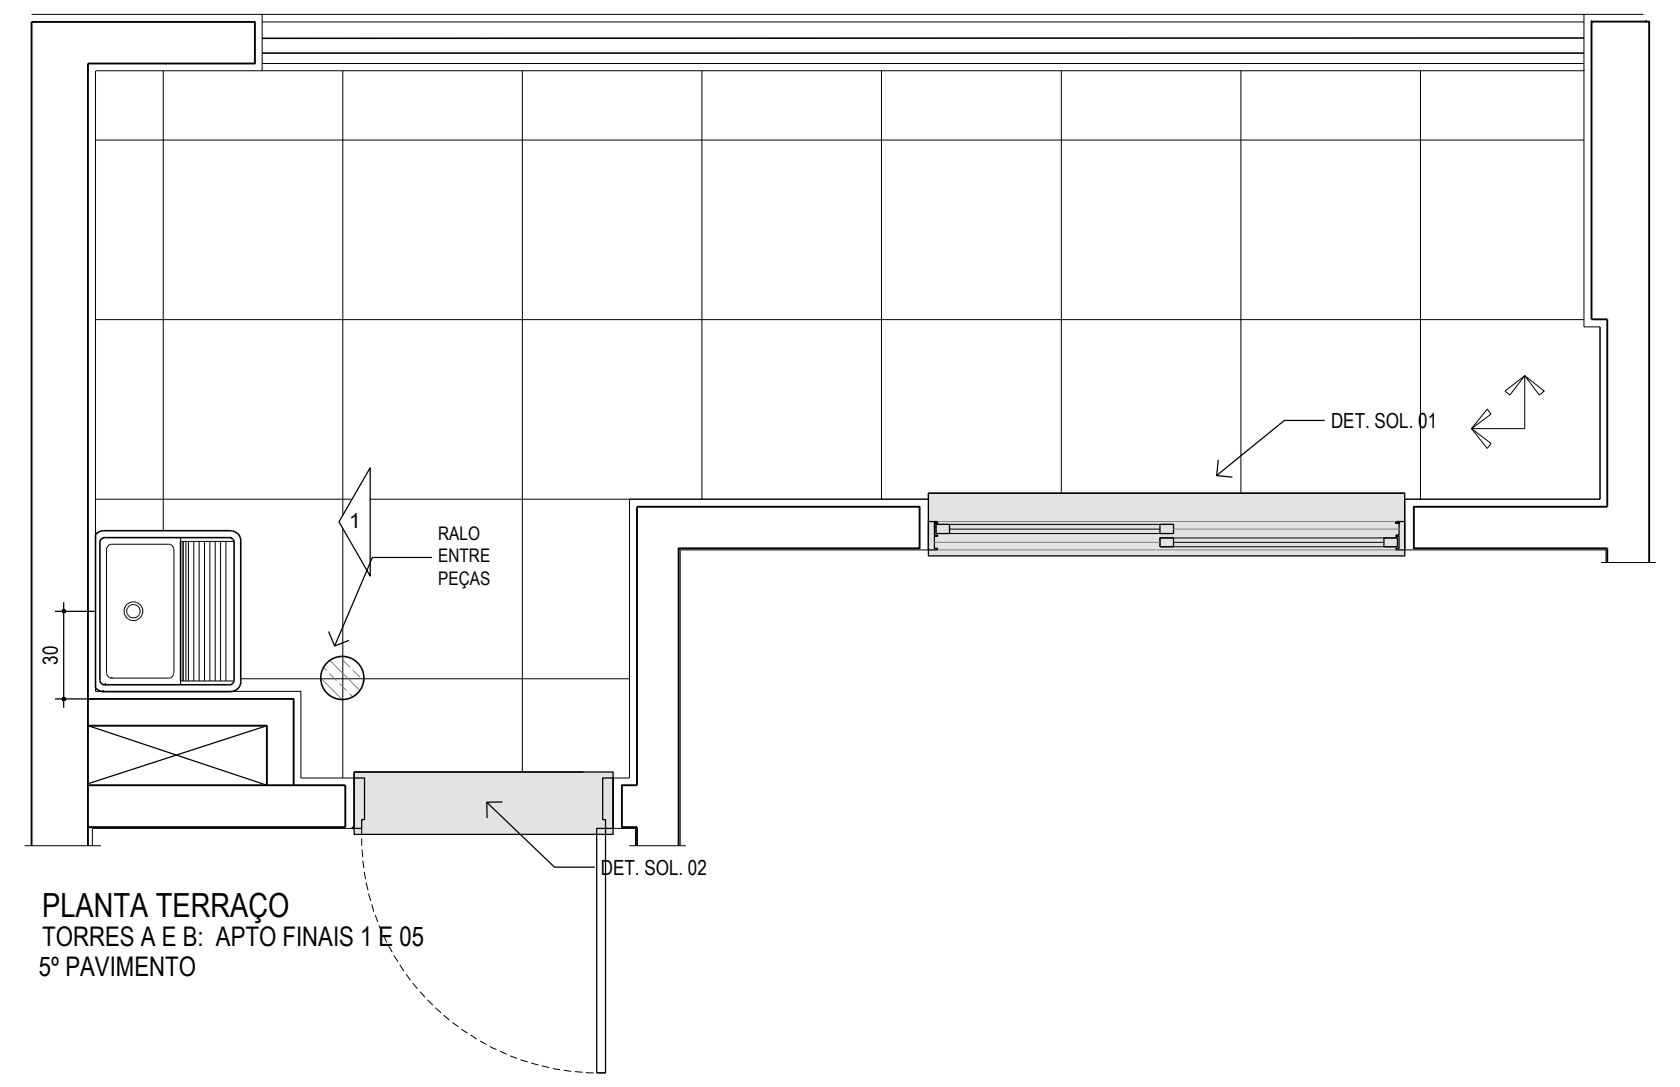

PLANTA TERRAÇO
TORRES A E B: APTO FINAIS 1 E 05
5º PAVIMENTO

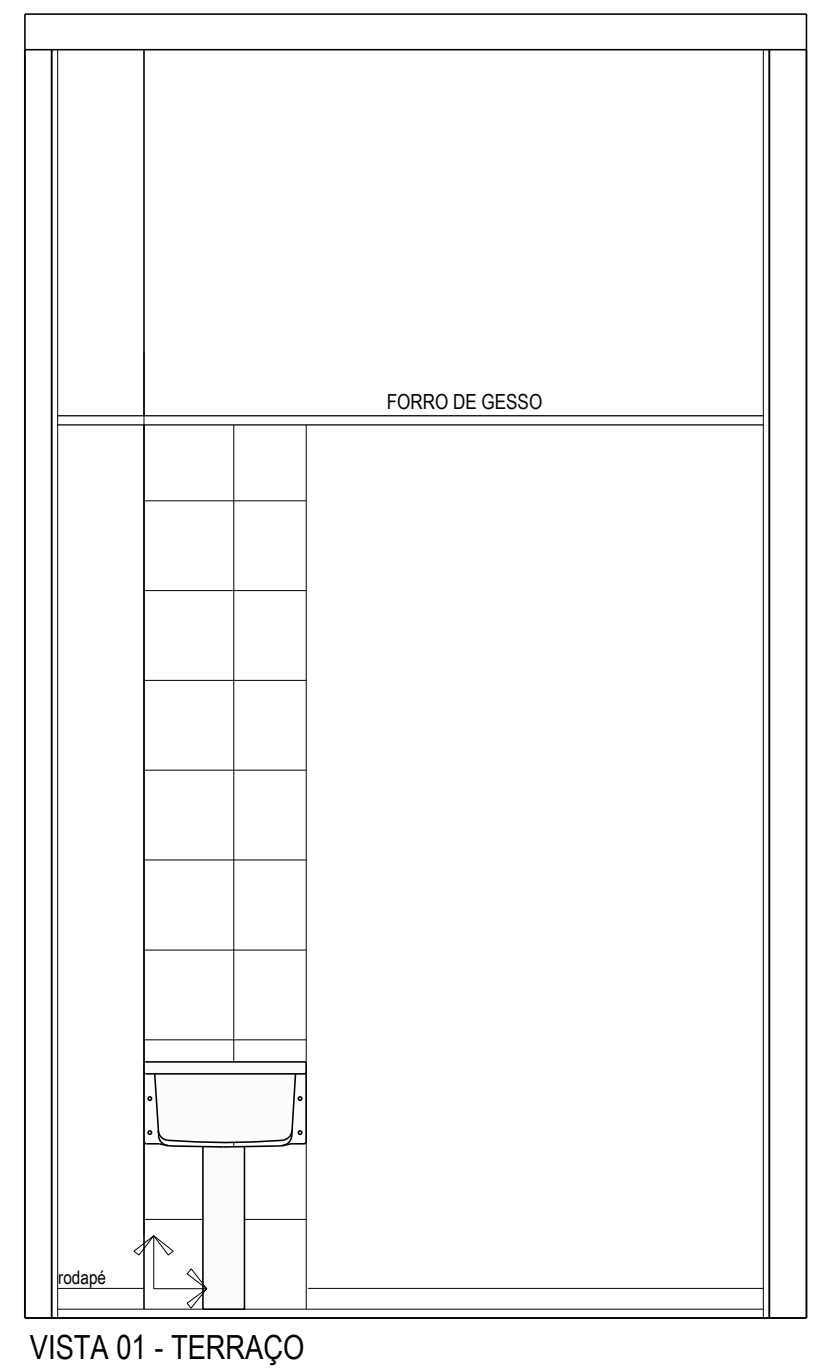

VISTA 01 - TERRAÇO
TORRES A E B: APTO FINAIS 1 E 05
5º PAVIMENTO

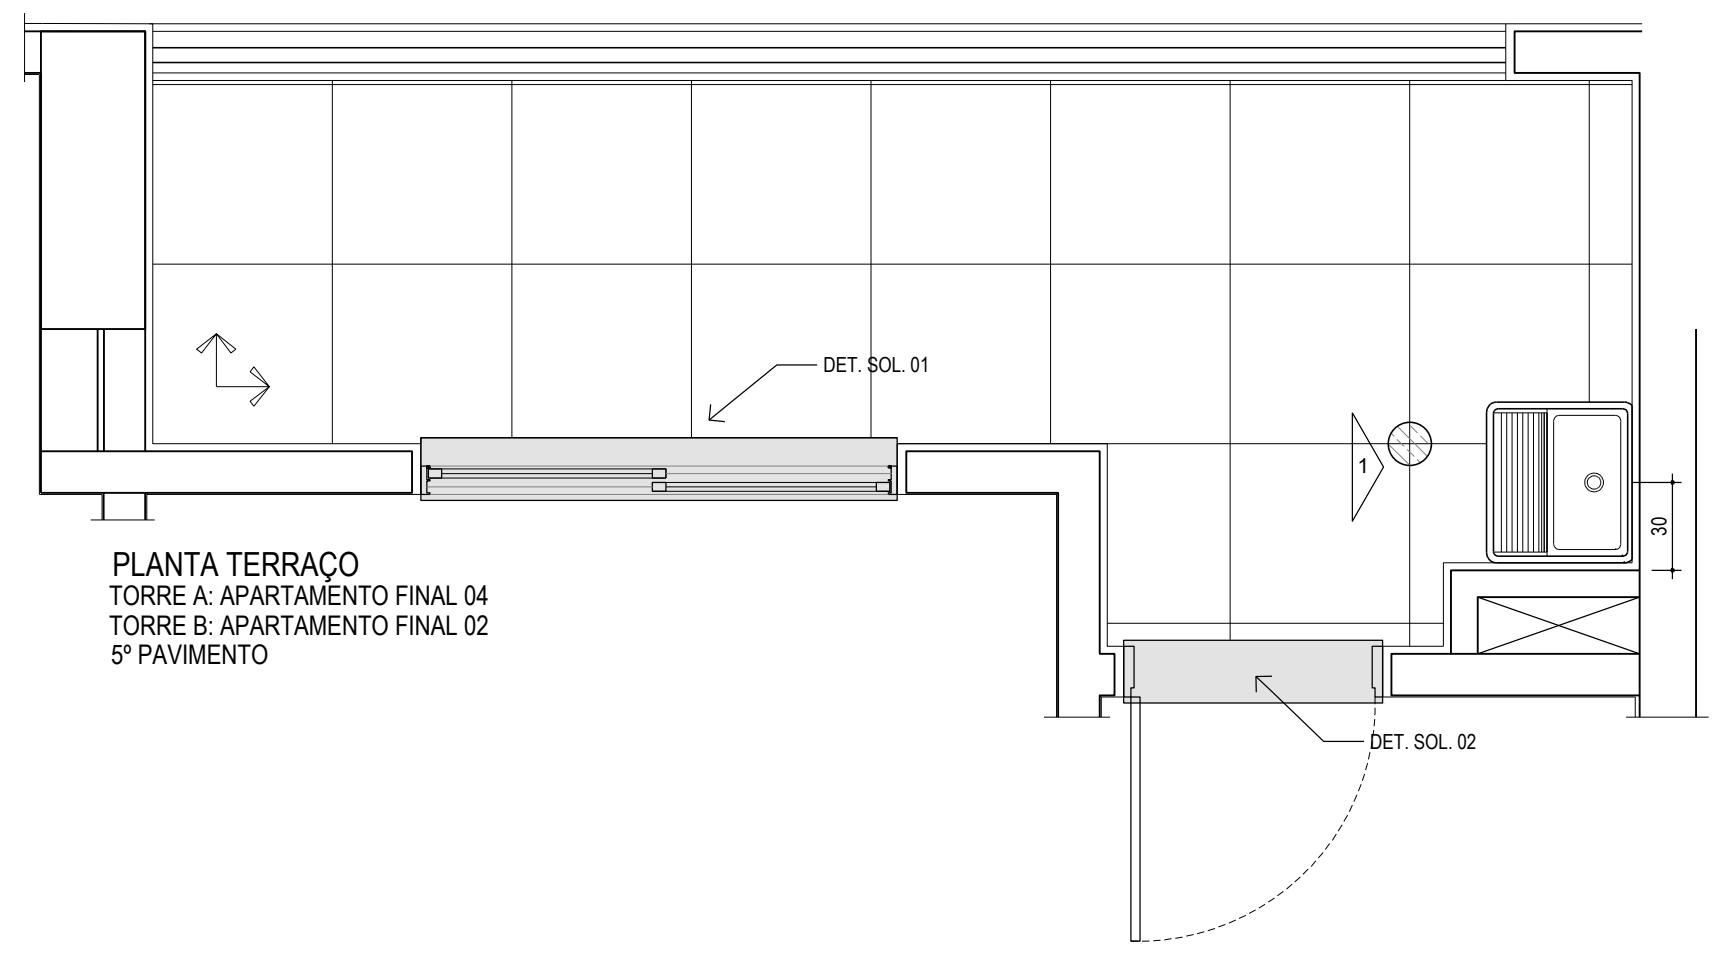

PLANTA TERRAÇO
TORRE A: APARTAMENTO FINAL 04
TORRE B: APARTAMENTO FINAL 02
5º PAVIMENTO

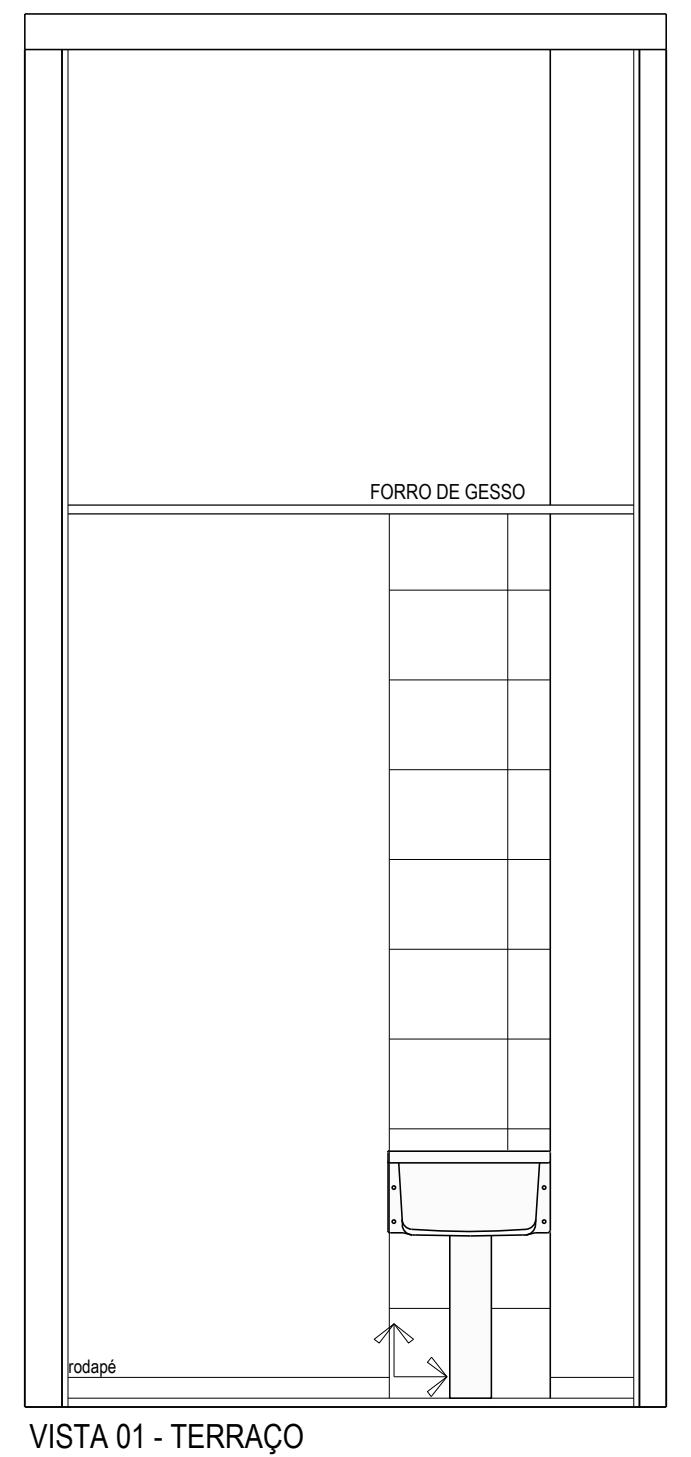

VISTA 01 - TERRAÇO
TORRE A: APARTAMENTO FINAL 04
TORRE B: APARTAMENTO FINAL 02
5º PAVIMENTO

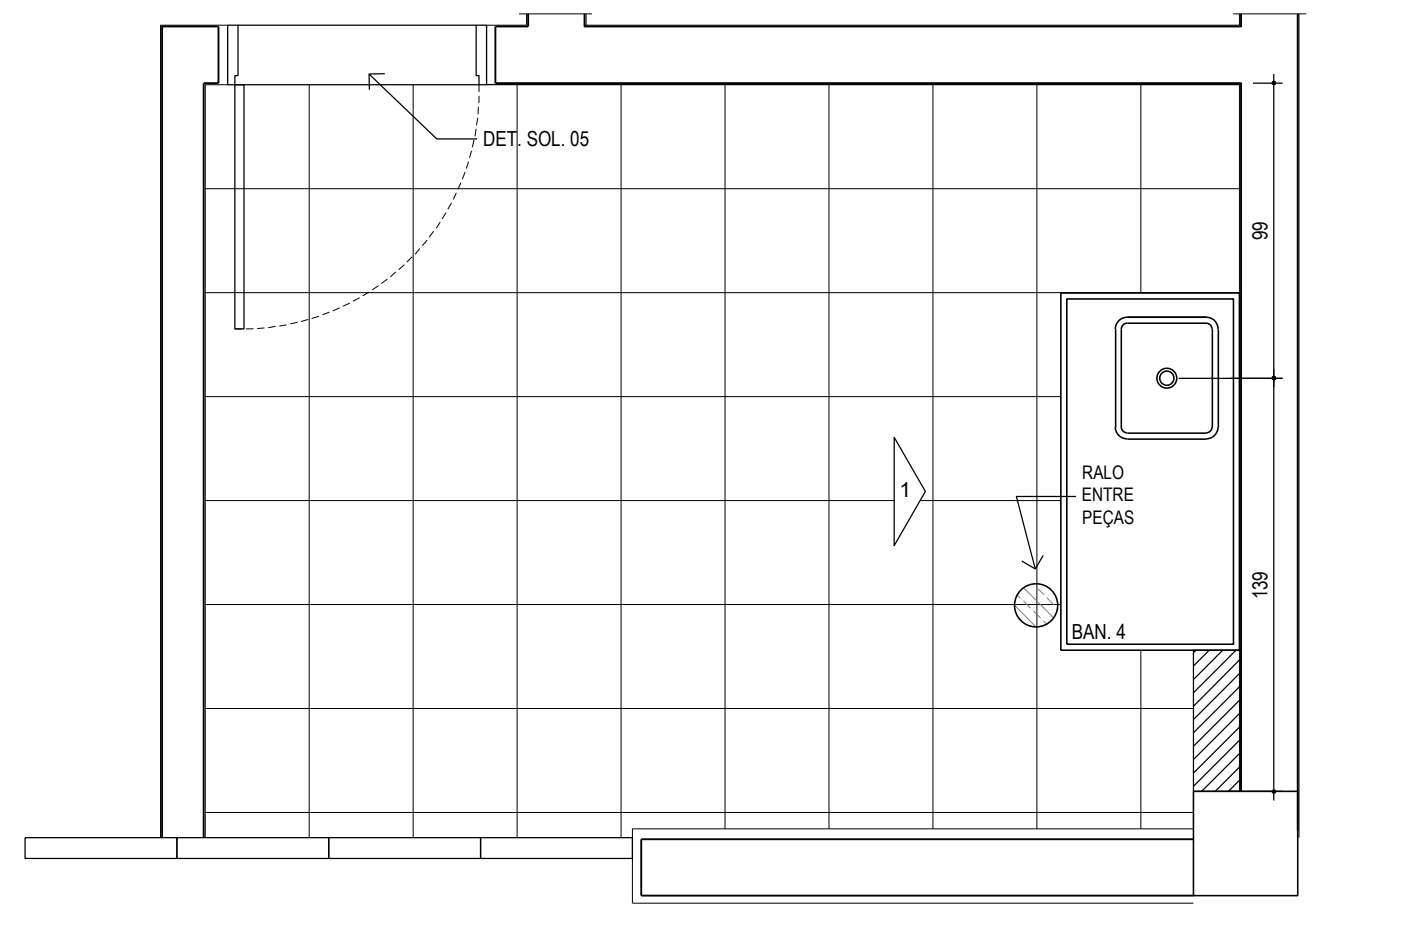

PLANTA COPA DE FUNCIONÁRIOS
4º PAVIMENTO

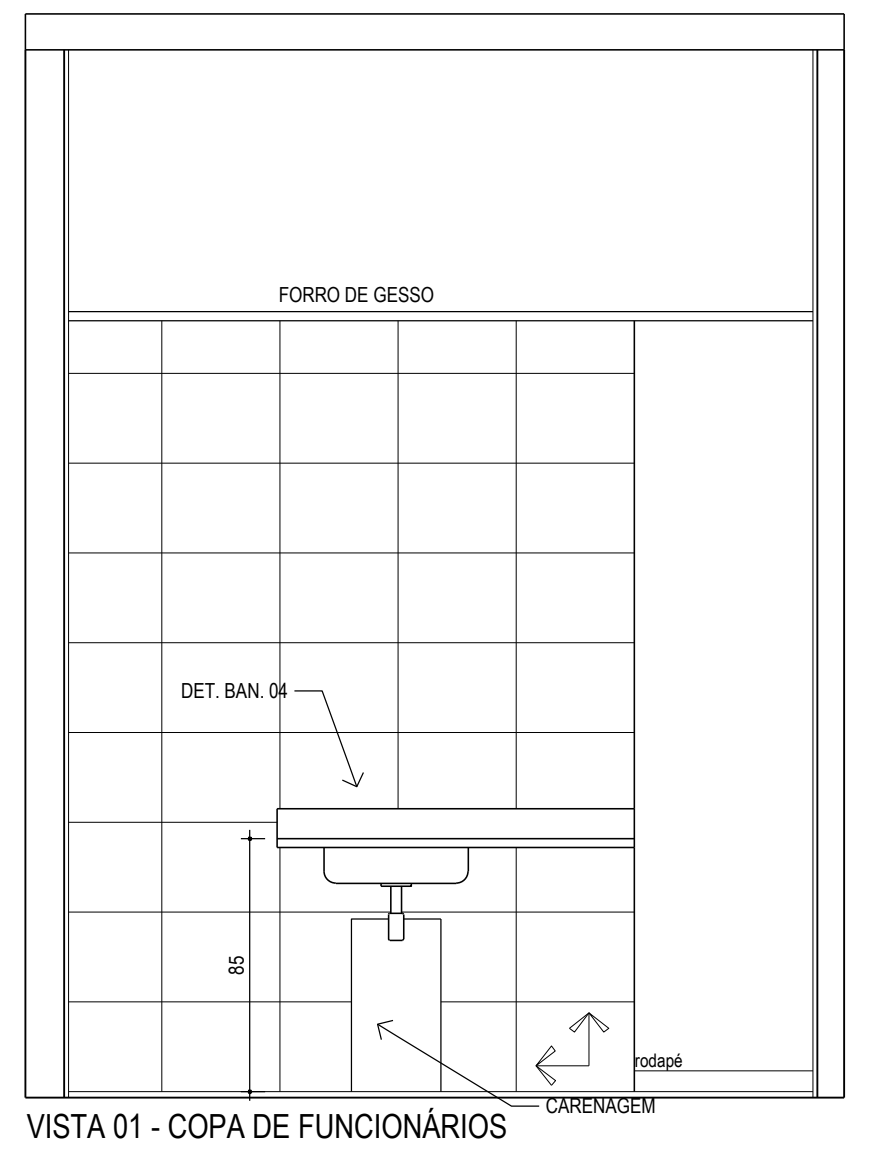

VISTA 01 - COPA DE FUNCIONÁRIOS
4º PAVIMENTO

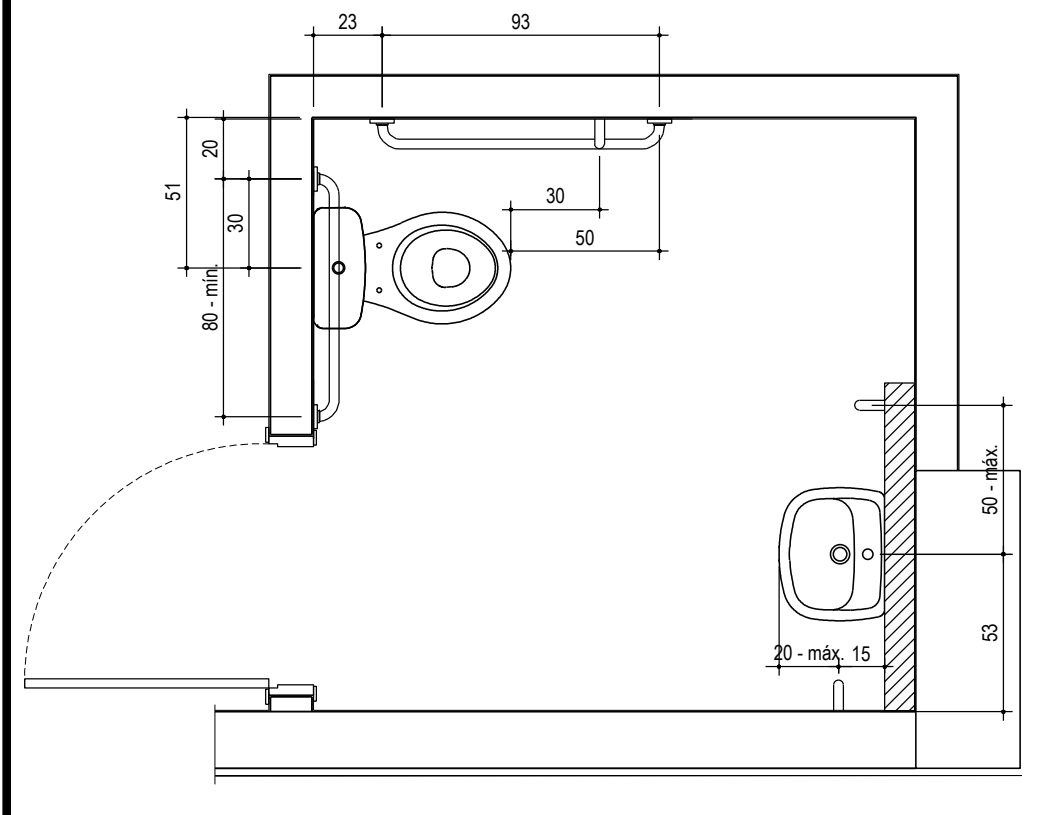

PLANTA W.C. P.C.D. - HIDRÁULICA
4º PAVIMENTO

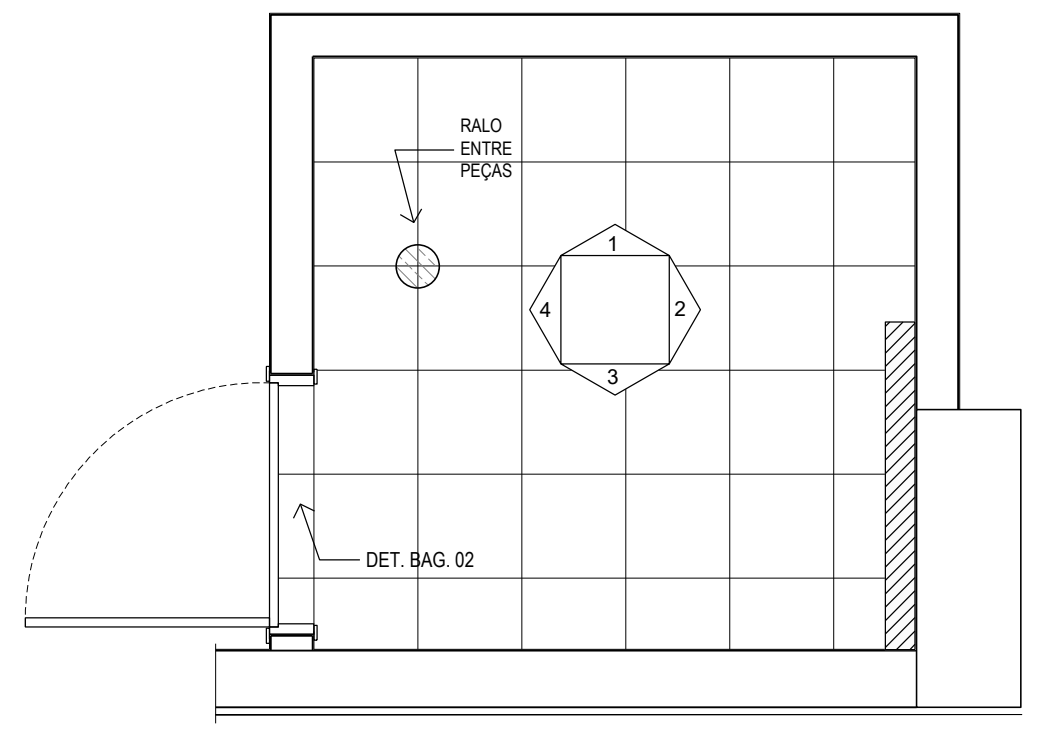

PLANTA W.C. P.C.D. - PISO
4º PAVIMENTO

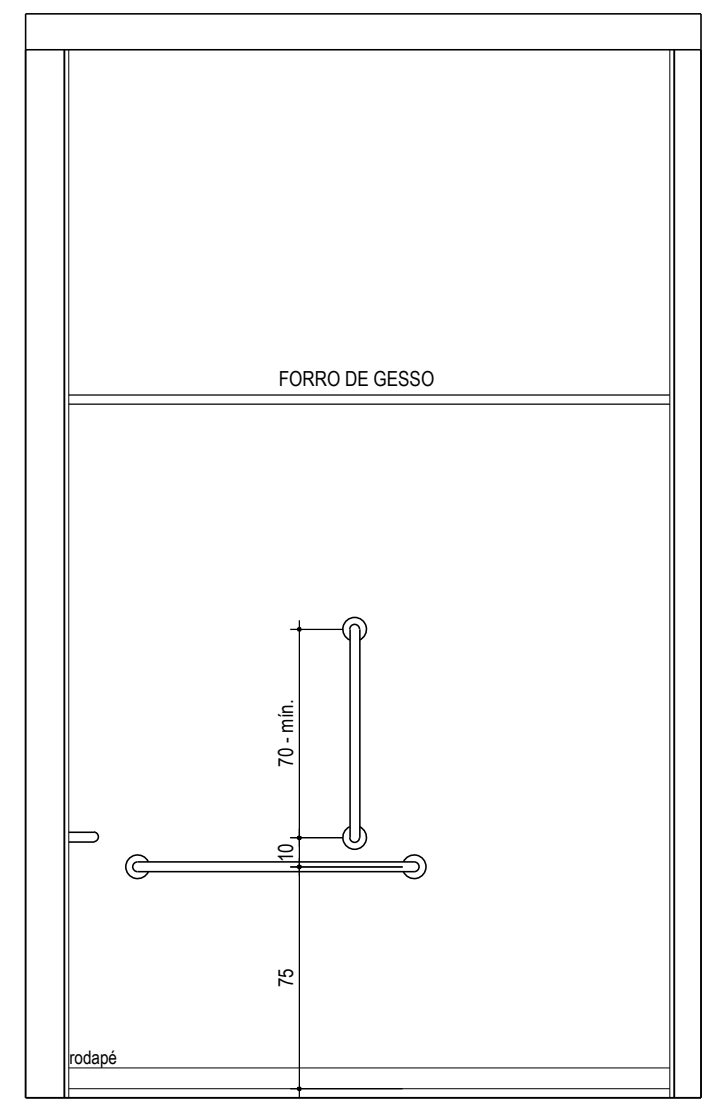

VISTA 01 - W.C. P.C.D.
4º PAVIMENTO

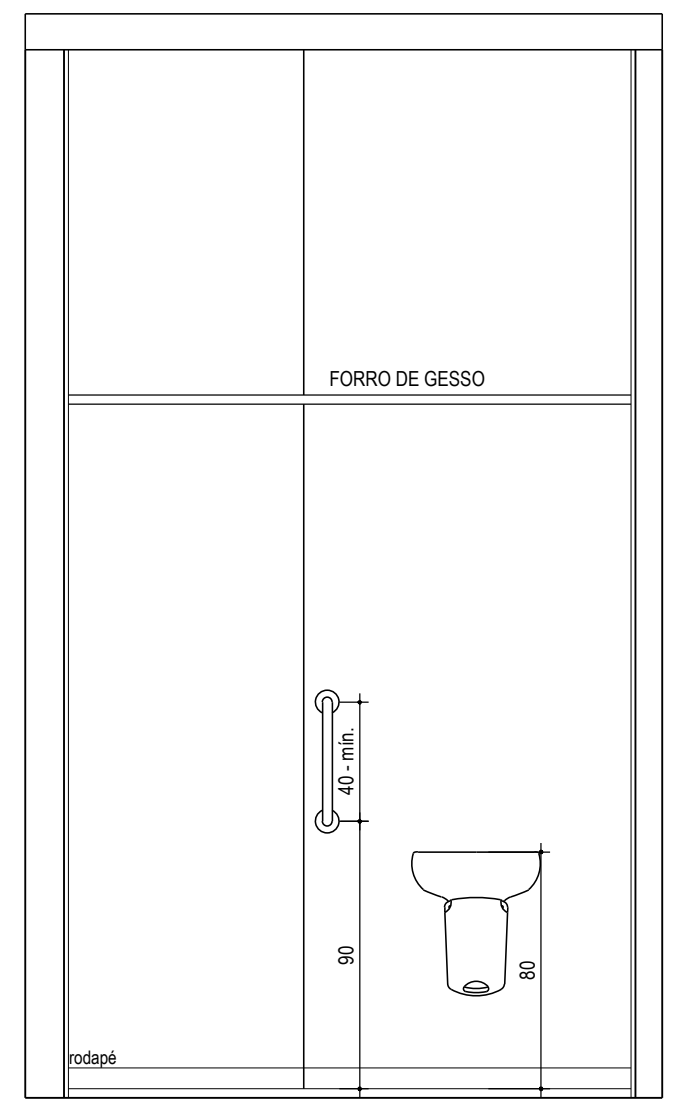

VISTA 02 - W.C. P.C.D.
4º PAVIMENTO

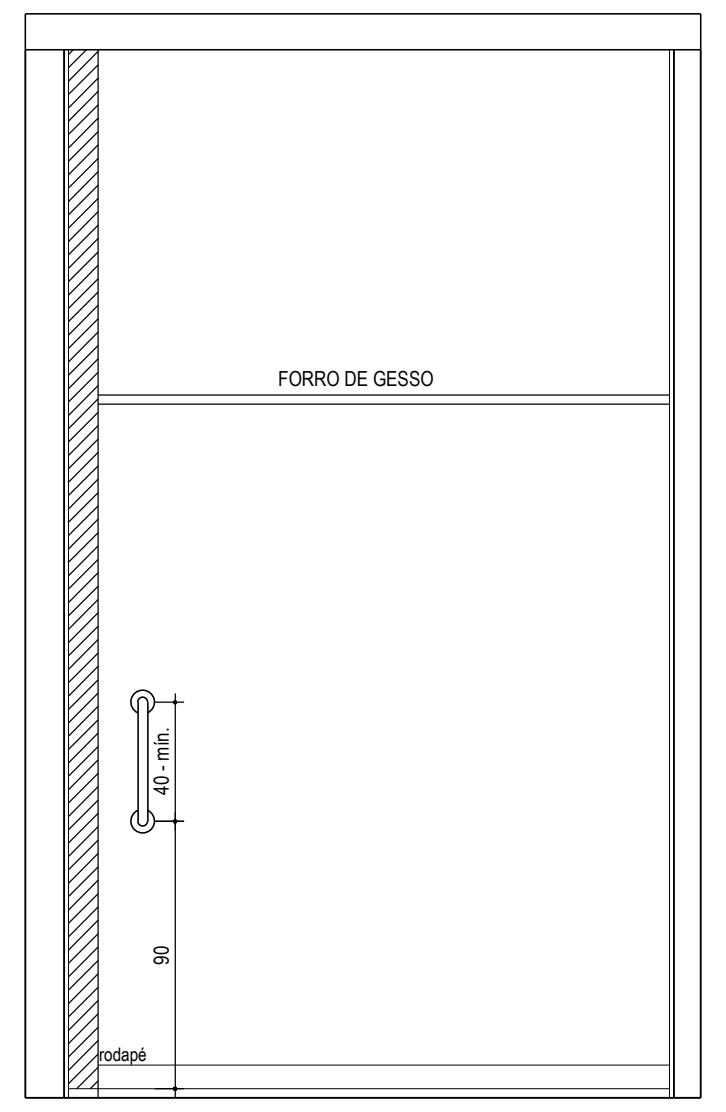

VISTA 03 - W.C. P.C.D.
4º PAVIMENTO

CONFORME NBR 9050, ALTURA DO VASO SANITÁRIO ENTRE 43cm E 45cm. COM O ASSENTO A ALTURA NO MÁXIMO 46cm. ESSA ALTURA PODE SER OBTIDA PELA EXECUÇÃO DE UM SÓCULO SOB A BASE DA BACIA COM CAIXA ACOPLADA, ISENTO DE CANTOS VIVOS E COM SUA PROJEÇÃO AVANÇANDO NO MÁXIMO 5cm.

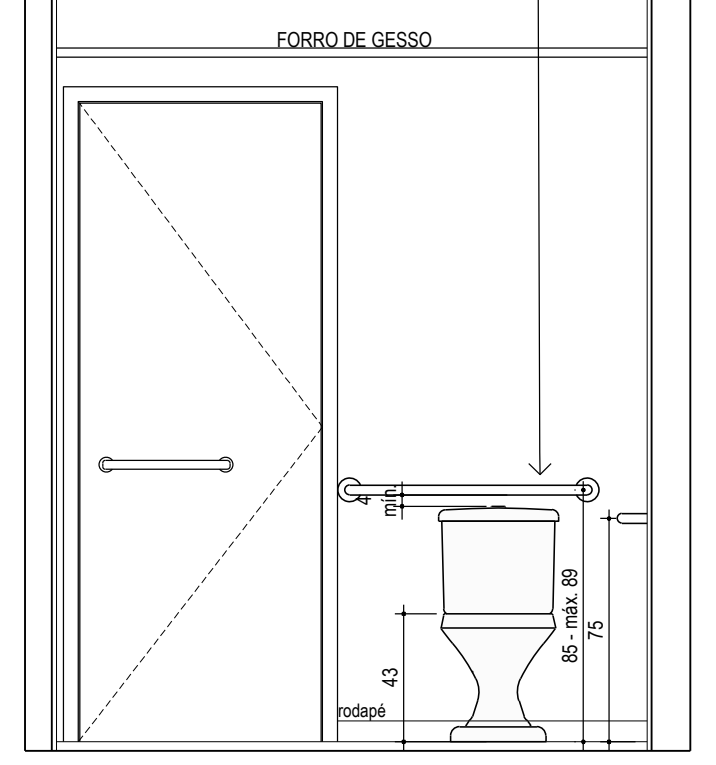

VISTA 04 - W.C. P.C.D.
4º PAVIMENTO

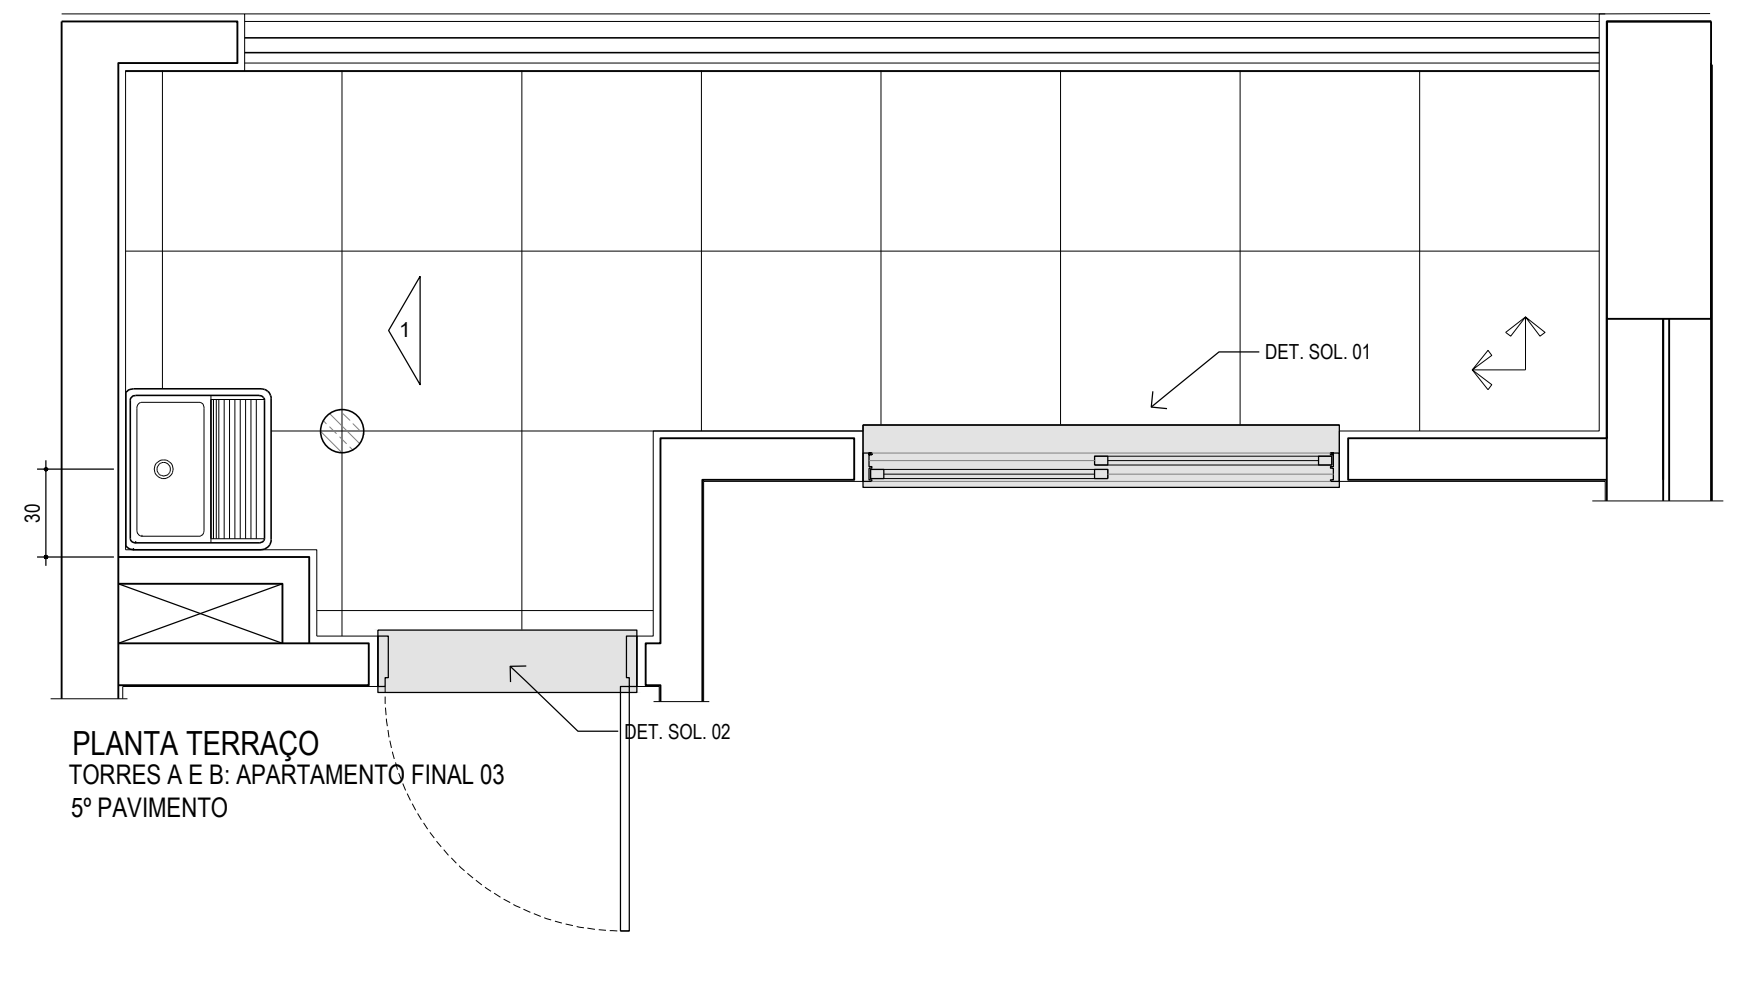

PLANTA TERRAÇO
TORRES A E B: APARTAMENTO FINAL 03
5º PAVIMENTO

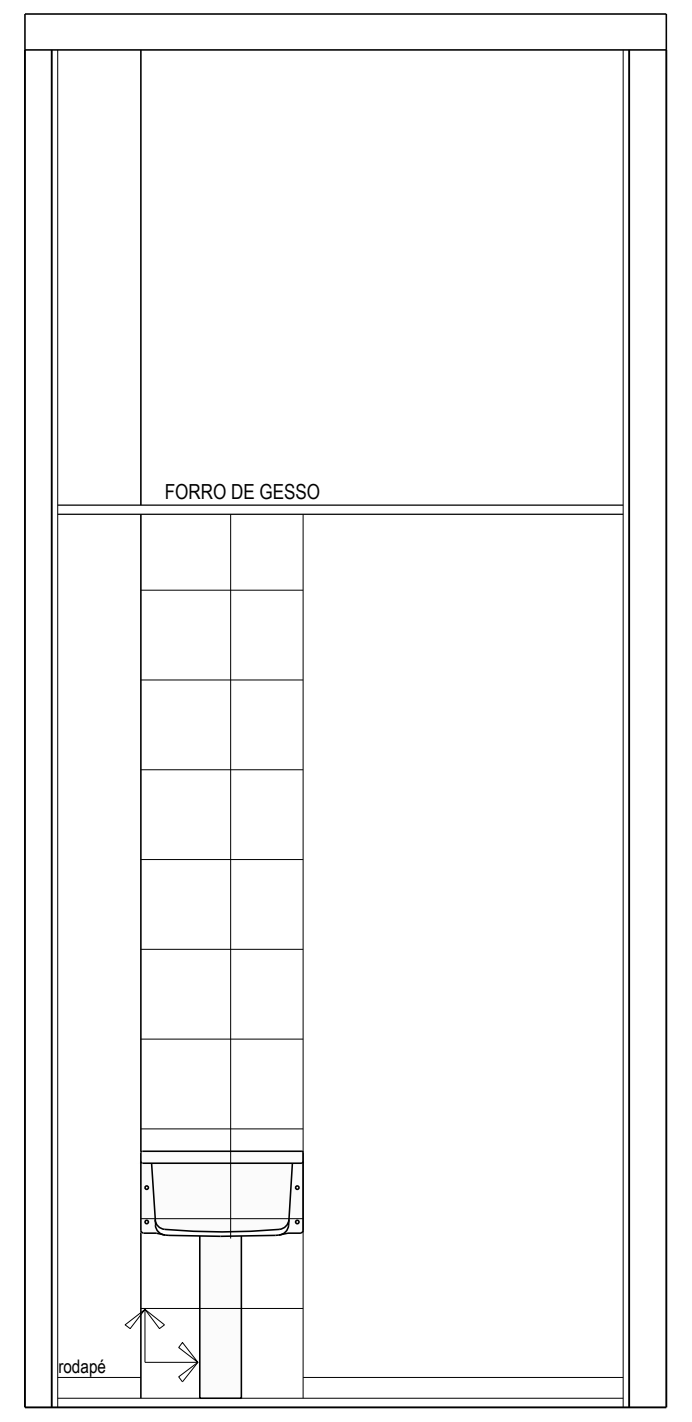

VISTA 01 - TERRAÇO
TORRES A E B: APARTAMENTO FINAL 03
5º PAVIMENTO

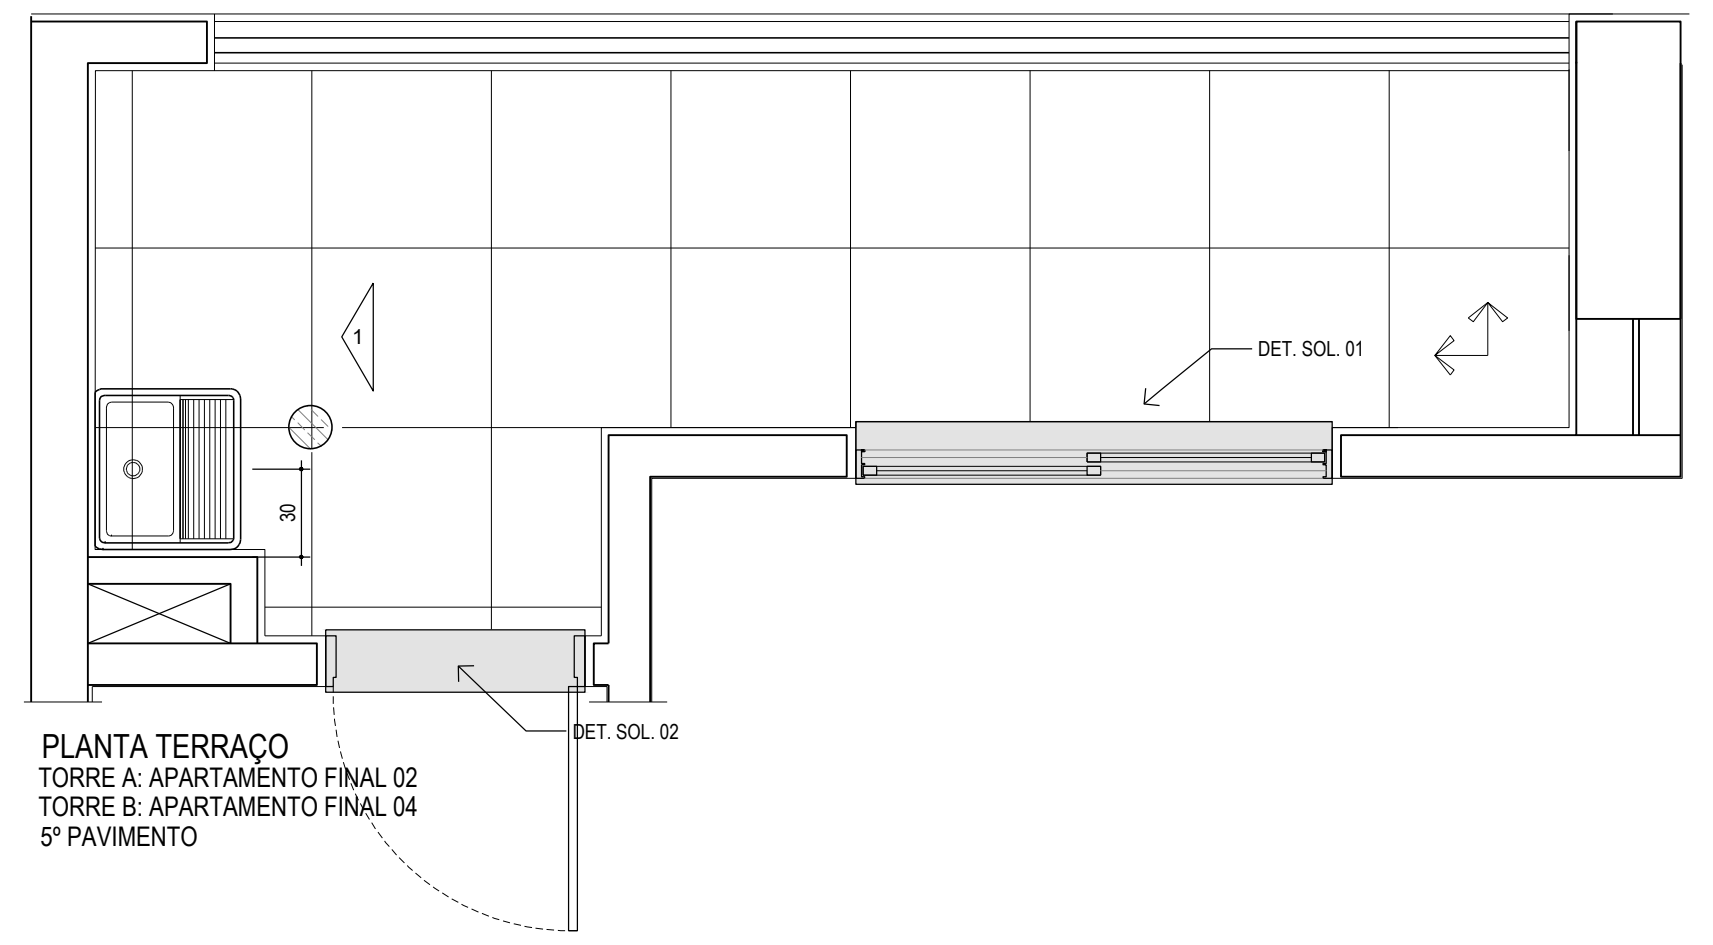

PLANTA TERRAÇO
TORRE A: APARTAMENTO FINAL 02
TORRE B: APARTAMENTO FINAL 04
5º PAVIMENTO

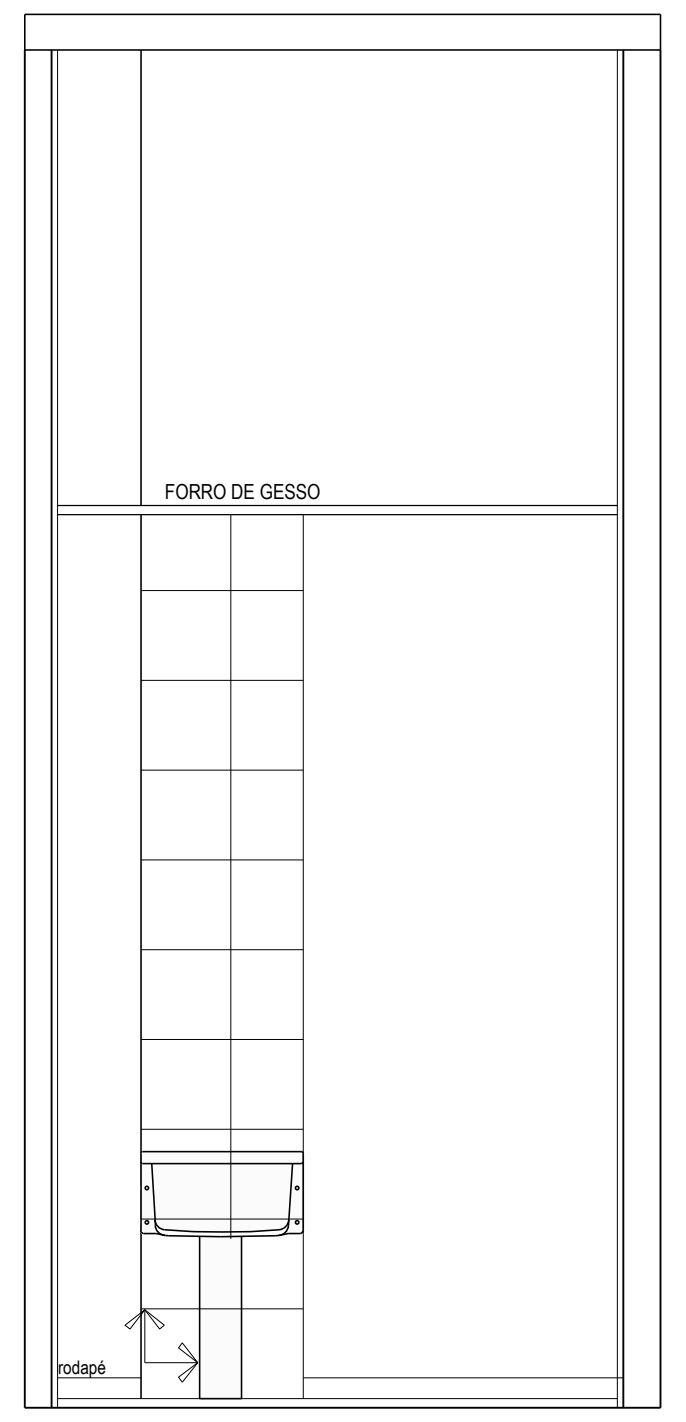

VISTA 01 - TERRAÇO
TORRE A: APARTAMENTO FINAL 02
TORRE B: APARTAMENTO FINAL 04
5º PAVIMENTO

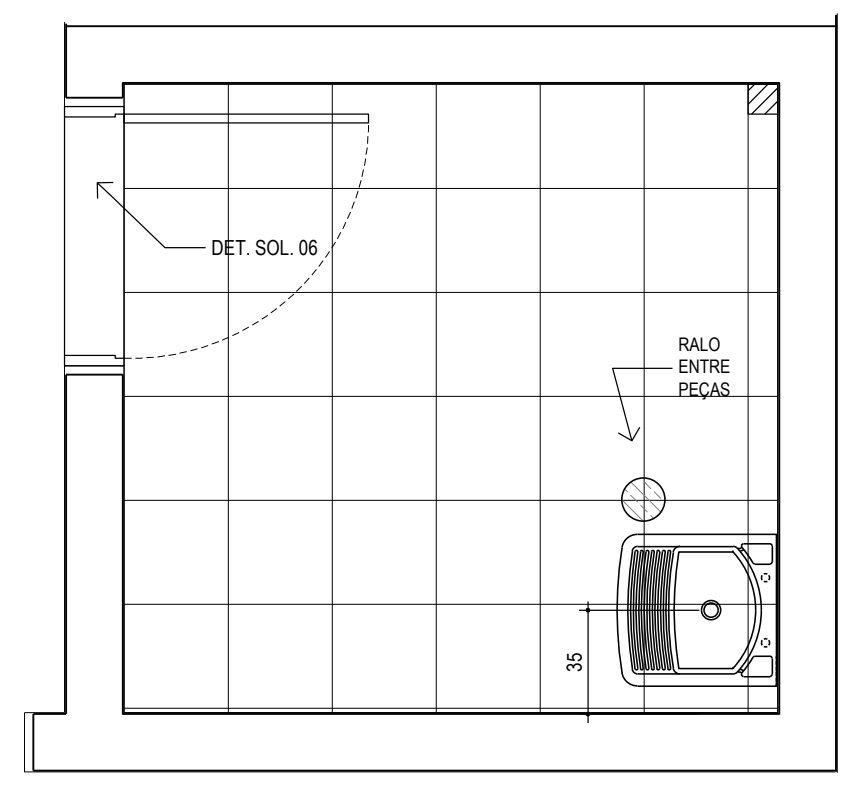

PLANTA D.M.L.
4º PAVIMENTO

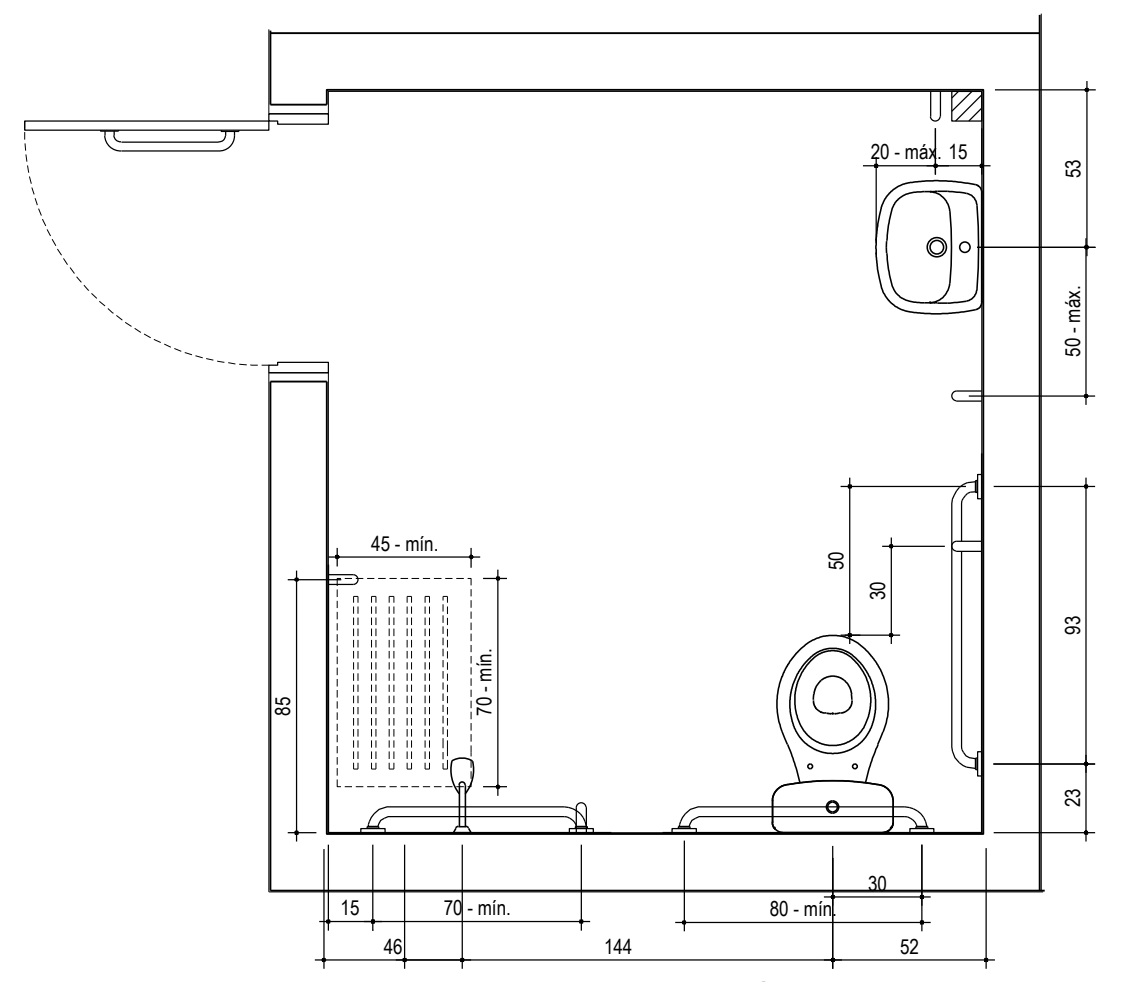

PLANTA VEST. FUNC. MASC. - HIDRÁULICA
3º PAVIMENTO

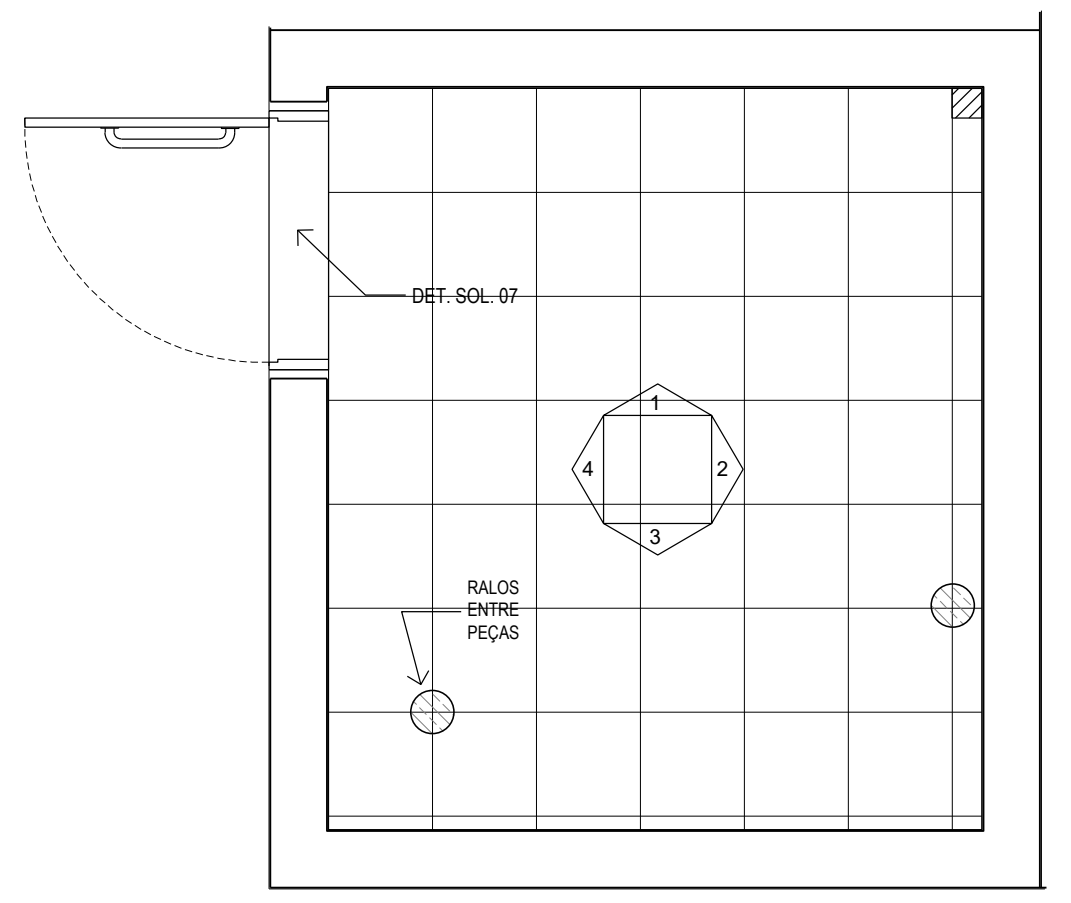

PLANTA VEST. FUNC. MASC. - PISO
3º PAVIMENTO

ITEM 7.12.2 DA NBR 9050 / 2015
O CHUVEIRO DEVE SER EQUIPADO COM DESVIADOR PARA DUCHA MANUAL, E O CONTROLE DE FLUXO (DUCHA / CHUVEIRO) DEVE SER NA DUCHA MANUAL. A FUNÇÃO CHUVEIRO PODE SER EXERCIDA POR DUCHA MANUAL, FIXADA EM BARRA DESLIZANTE, PERMITINDO REGULAGENS DE ALTURA APROPRIADAS ÀS DIVERSAS NECESSIDADES DOS USUÁRIOS.

CONFORME NBR 9050, ALTURA DO VASO SANITÁRIO ENTRE 43cm E 45cm. COM O ASSENTO A ALTURA NO MÁXIMO 46cm.
ESSA ALTURA PODE SER OBTIDA PELA EXECUÇÃO DE UM SÓCULO SOB A BASE DA BACIA COM CAIXA ACOPLADA, ISENTO DE CANTOS VIVOS E COM SUA PROJEÇÃO AVANÇANDO NO MÁXIMO 5cm.

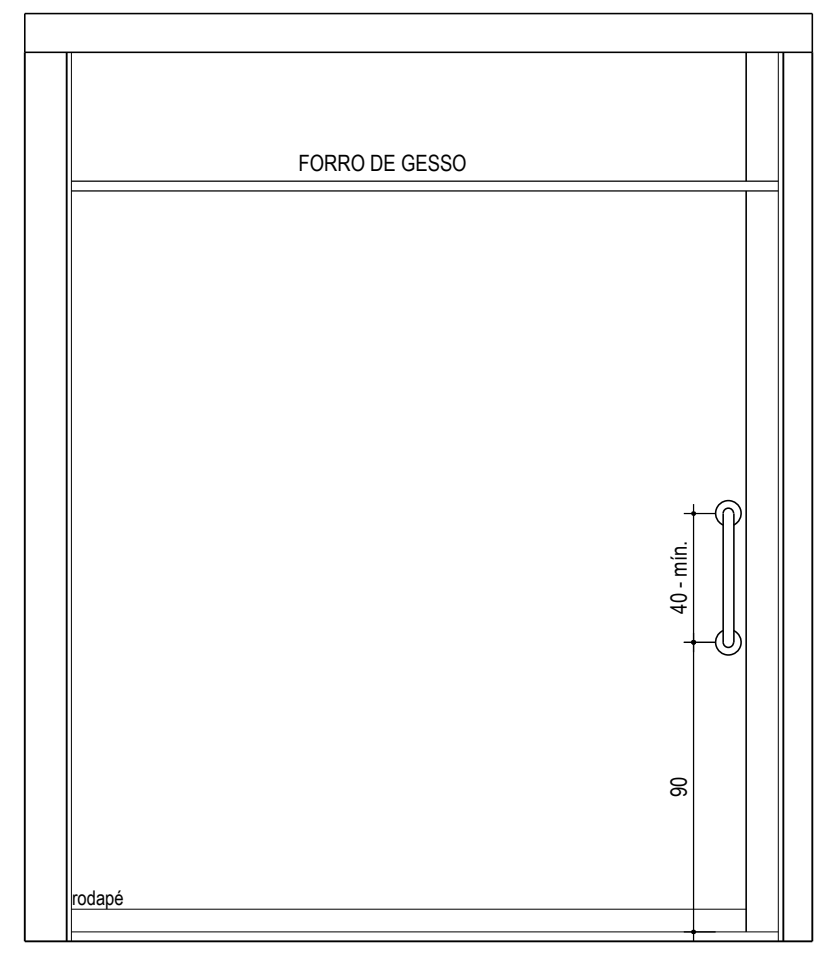

VISTA 01 - VEST. FUNC. MASC.
4º PAVIMENTO

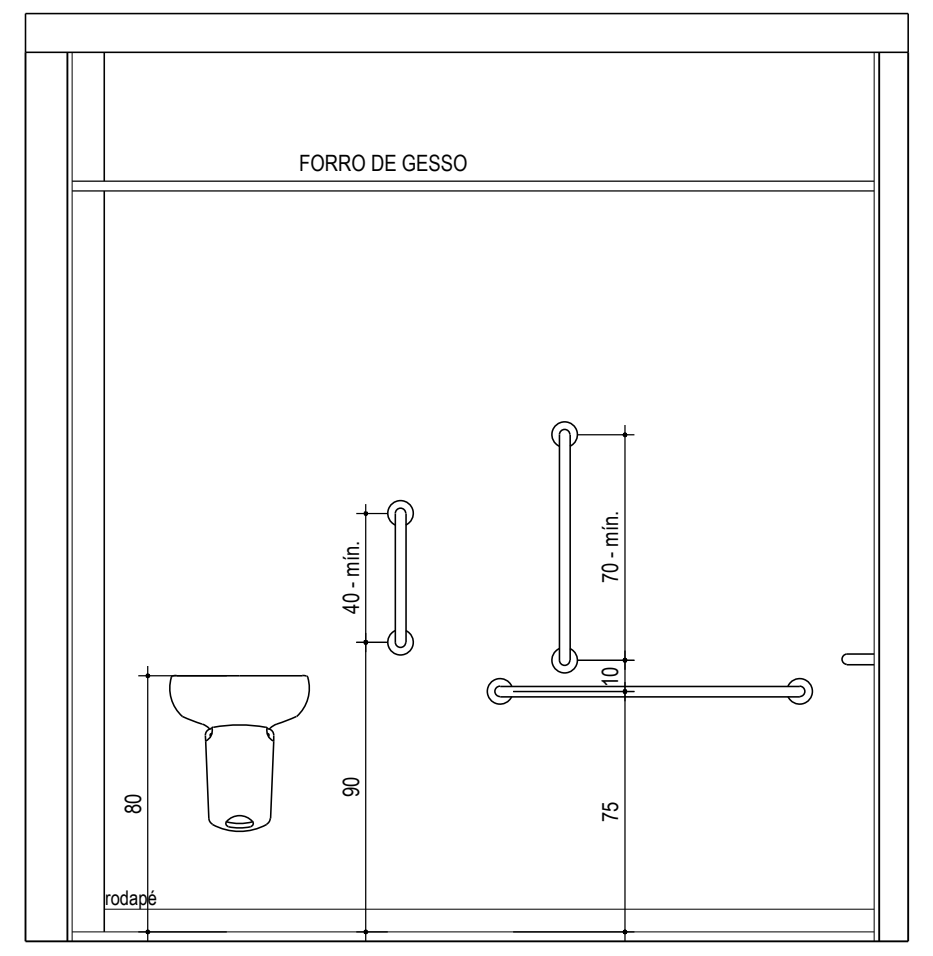

VISTA 02 - VEST. FUNC. MASC.
4º PAVIMENTO

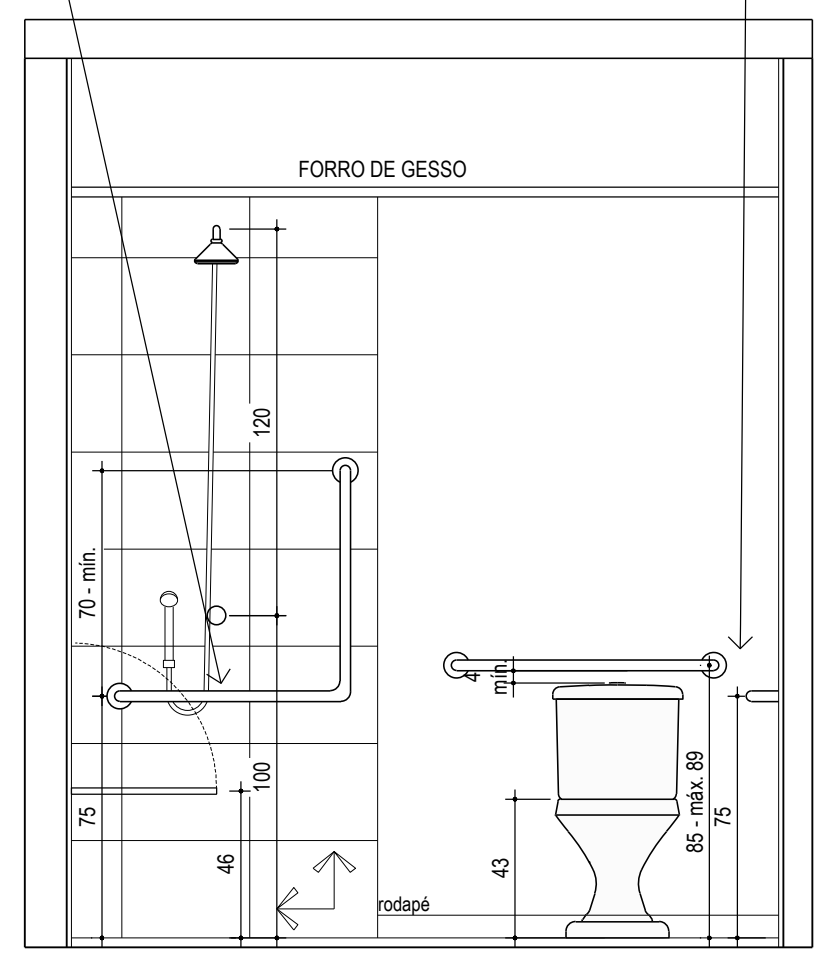

VISTA 03 - VEST. FUNC. MASC.
4º PAVIMENTO

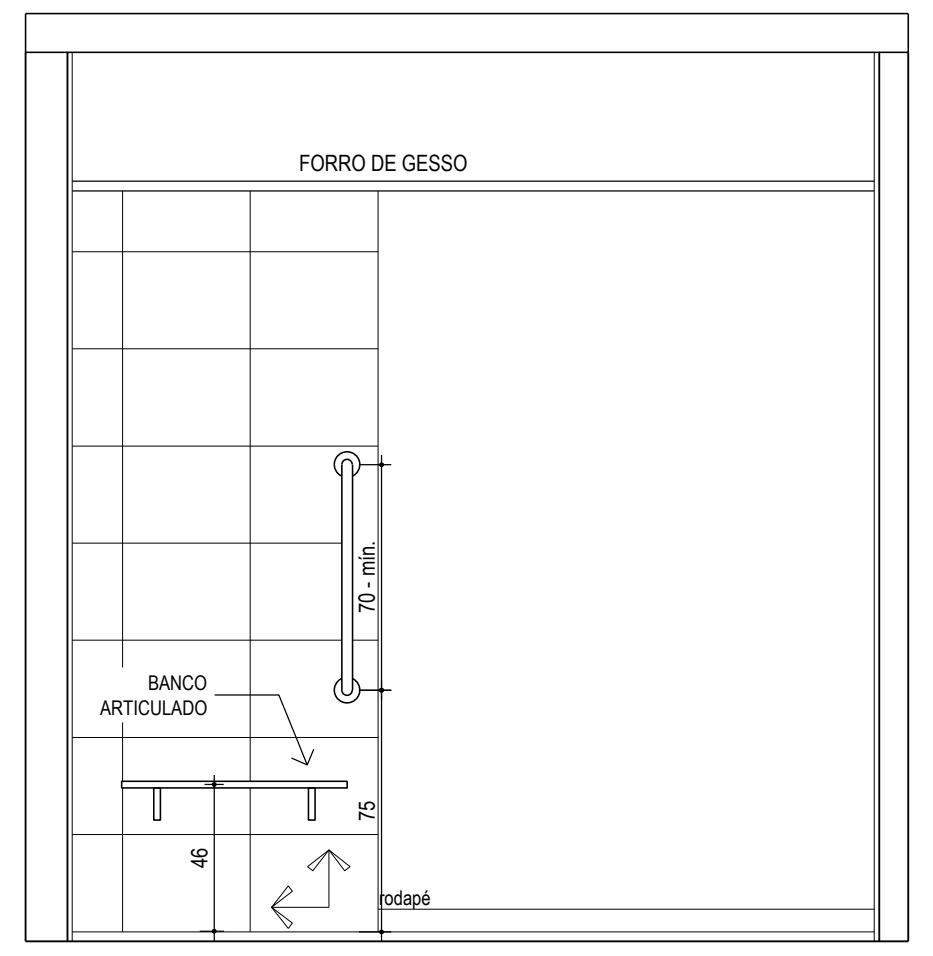

VISTA 04 - VEST. FUNC. MASC.
4º PAVIMENTO

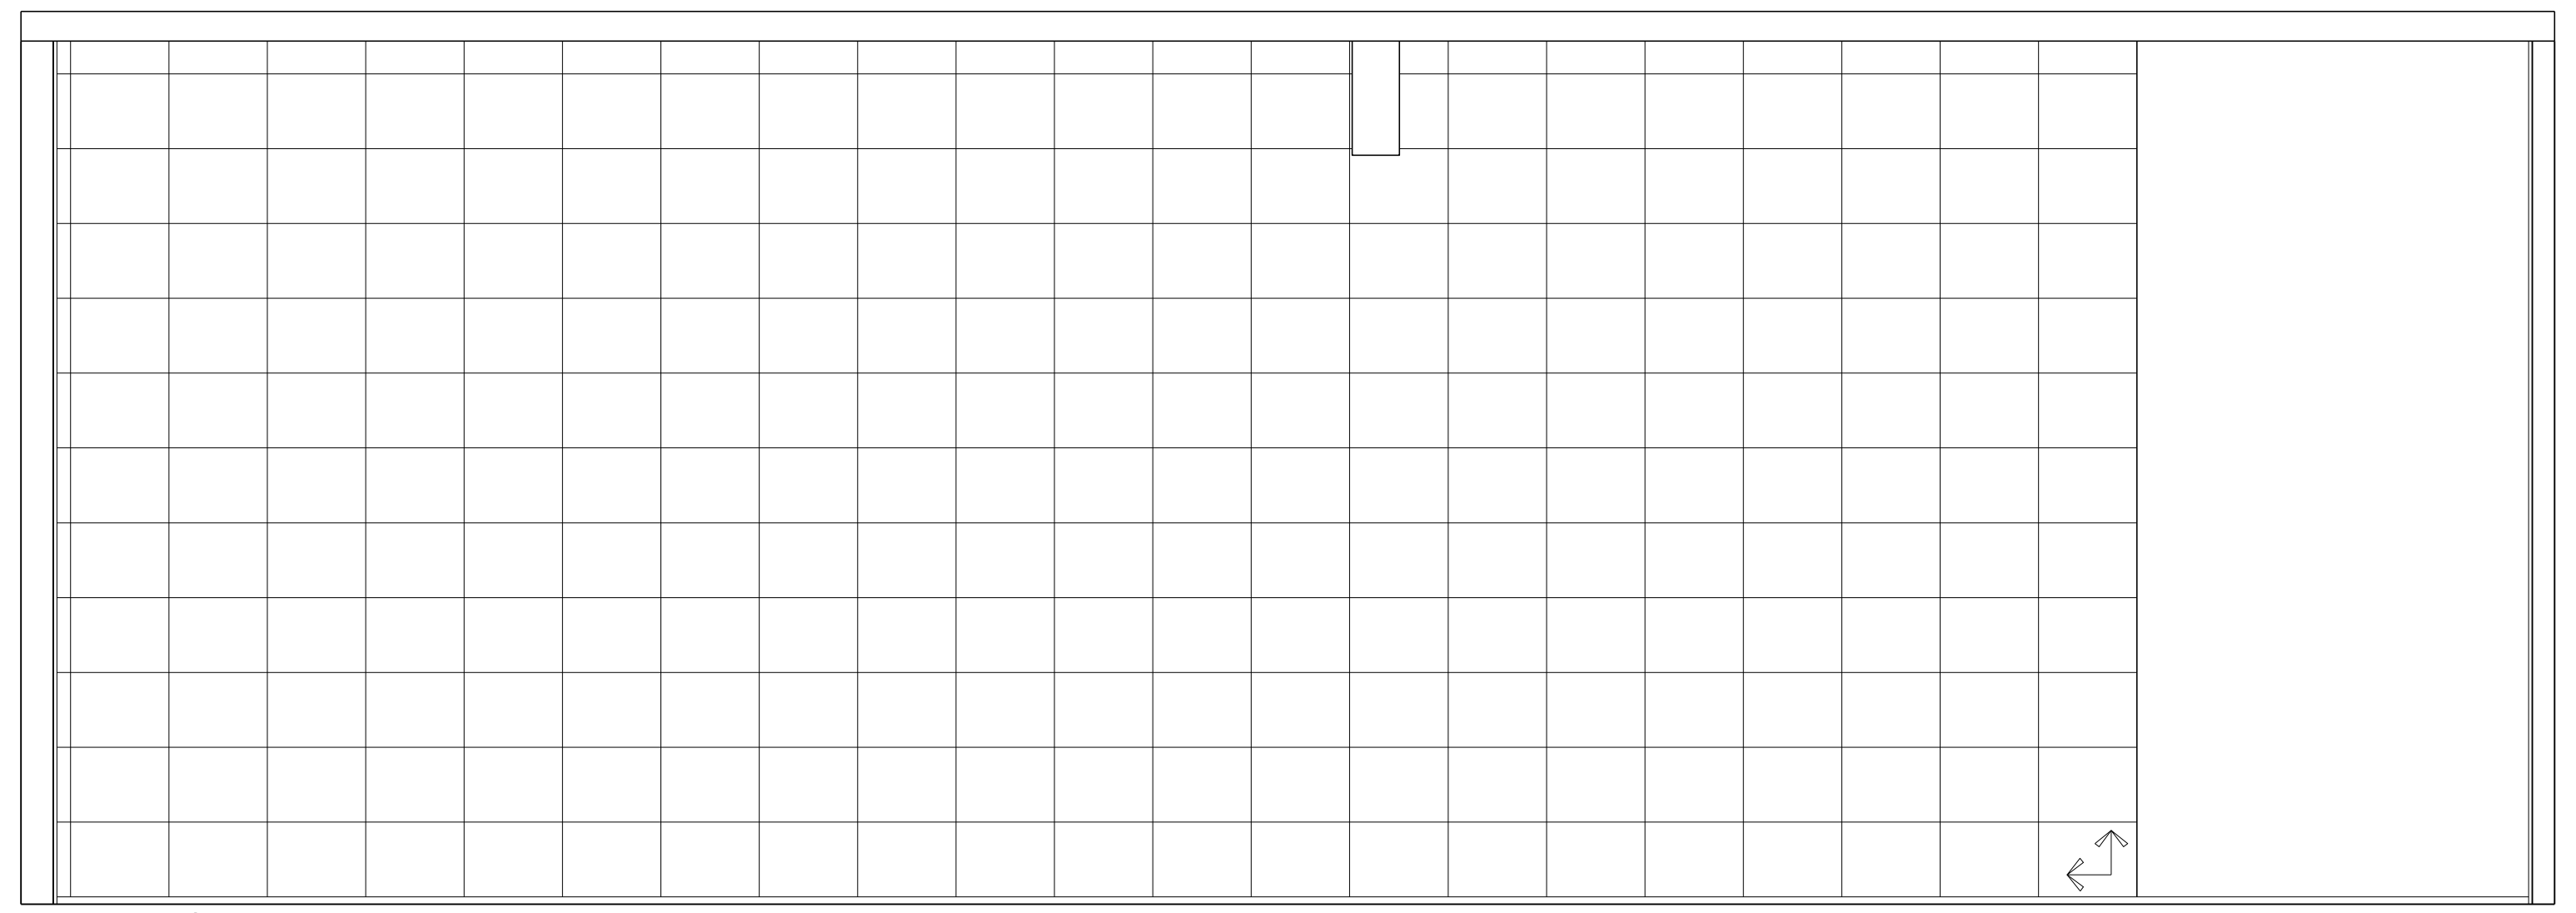

VISTA 01 - DEPÓSITO DE LIXO
1º PAVIMENTO

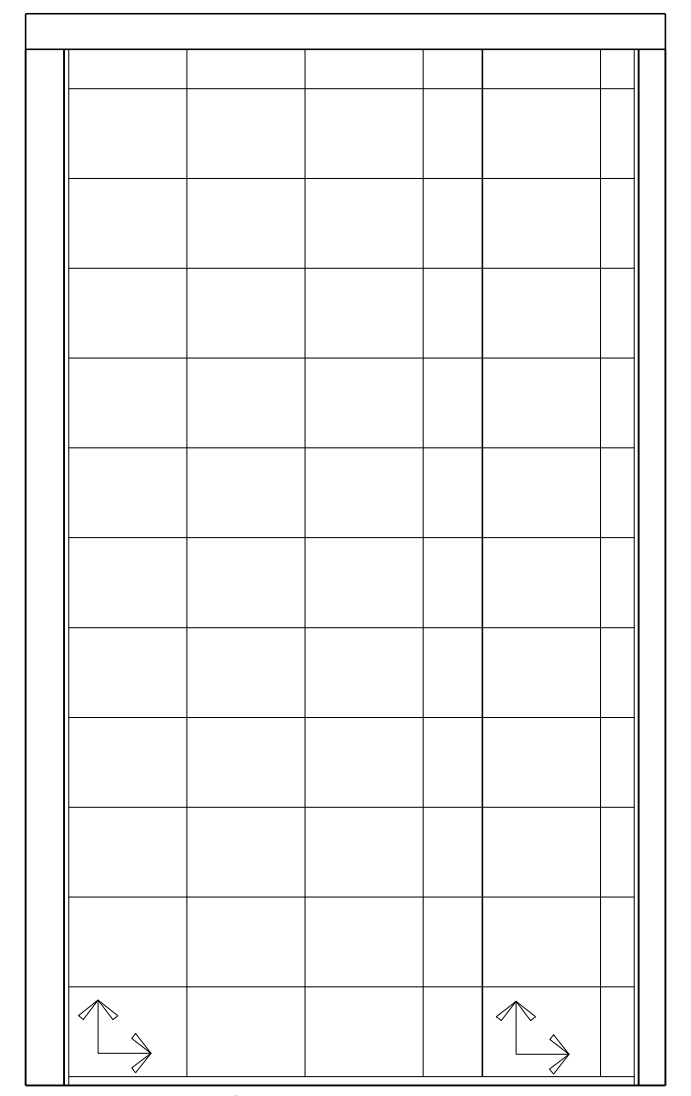

VISTA 02 - DEPÓSITO DE LIXO
1º PAVIMENTO

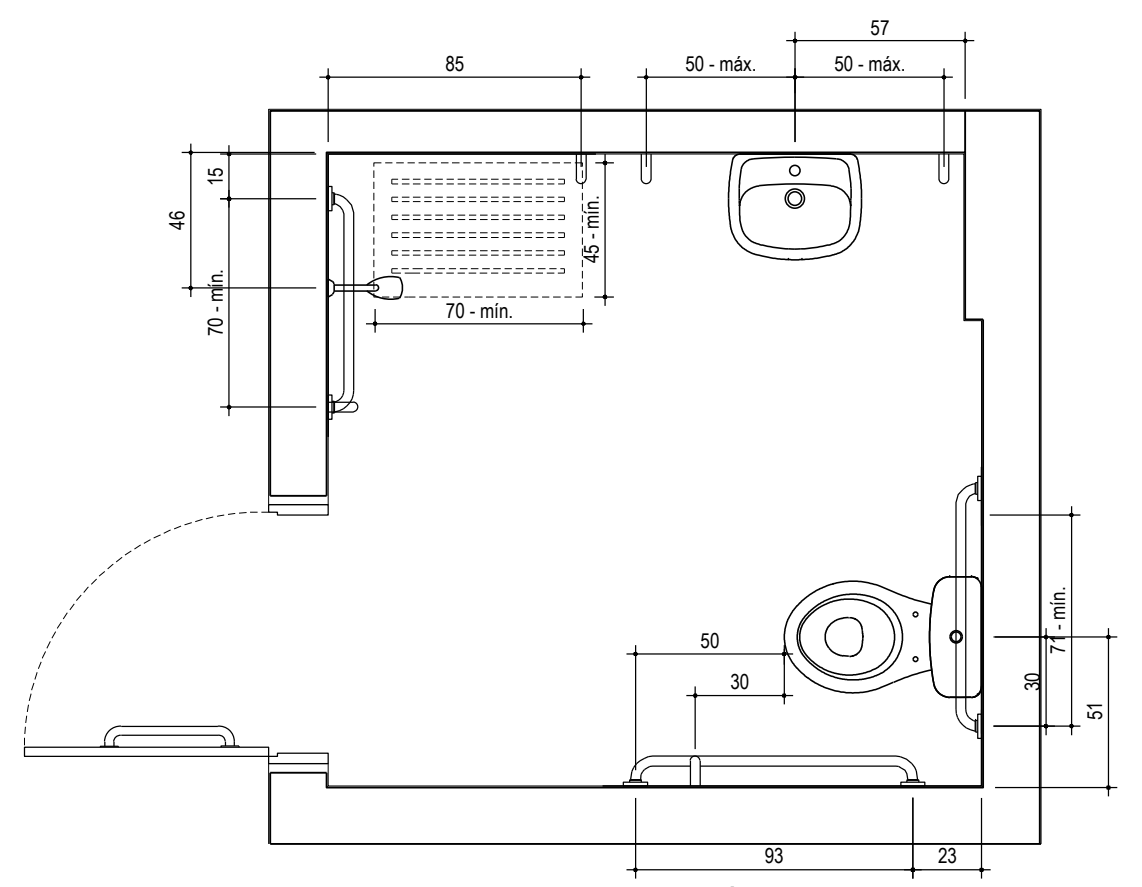

PLANTA VEST. FUNC. FEM. - HIDRÁULICA
3º PAVIMENTO

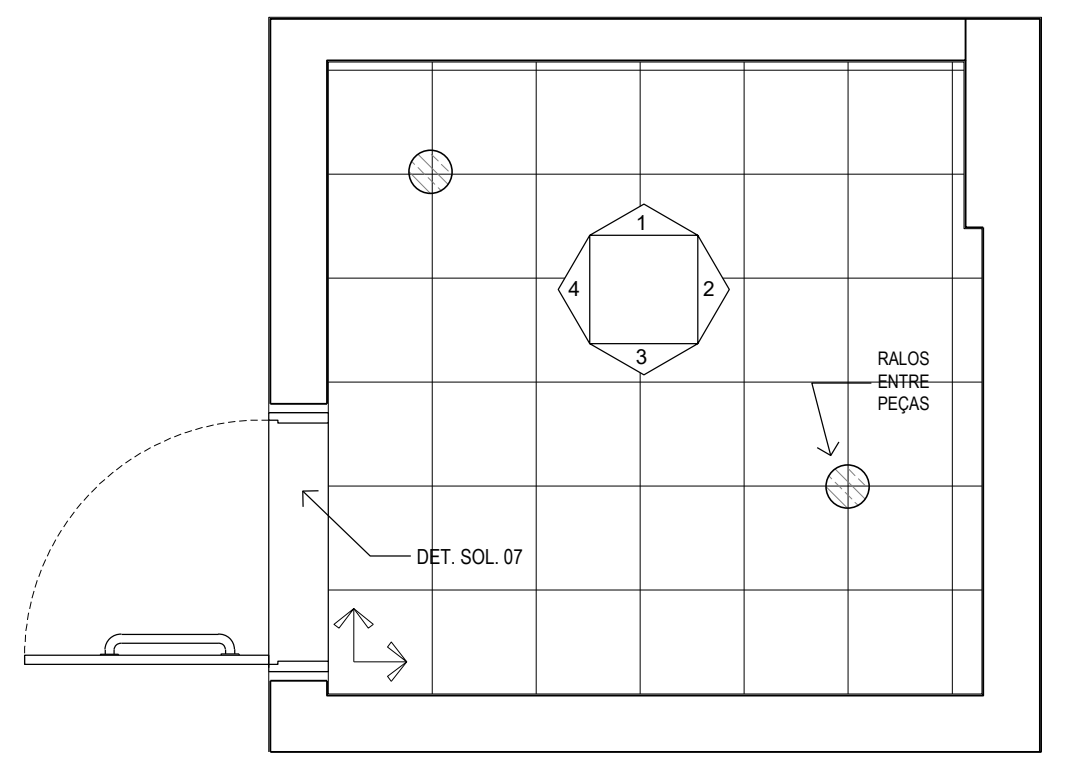

PLANTA VEST. FUNC. FEM. - PISO
3º PAVIMENTO

CONFORME NBR 9050, ALTURA DO VASO SANITÁRIO ENTRE 43cm E 45cm. COM O ASSENTO A ALTURA NO MÁXIMO 46cm.
ESSA ALTURA PODE SER OBTIDA PELA EXECUÇÃO DE UM SÓCULO SOB A BASE DA BACIA COM CAIXA ACOPLADA, ISENTO DE CANTOS VIVOS E COM SUA PROJEÇÃO AVANÇANDO NO MÁXIMO 5cm.

ITEM 7.12.2 DA NBR 9050 / 2015
O CHUVEIRO DEVE SER EQUIPADO COM DESVIADOR PARA DUCHA MANUAL, E O CONTROLE DE FLUXO (DUCHA / CHUVEIRO) DEVE SER NA DUCHA MANUAL. A FUNÇÃO CHUVEIRO PODE SER EXERCIDA POR DUCHA MANUAL, FIXADA EM BARRA DESLIZANTE, PERMITINDO REGULAGENS DE ALTURA APROPRIADAS ÀS DIVERSAS NECESSIDADES DOS USUÁRIOS.

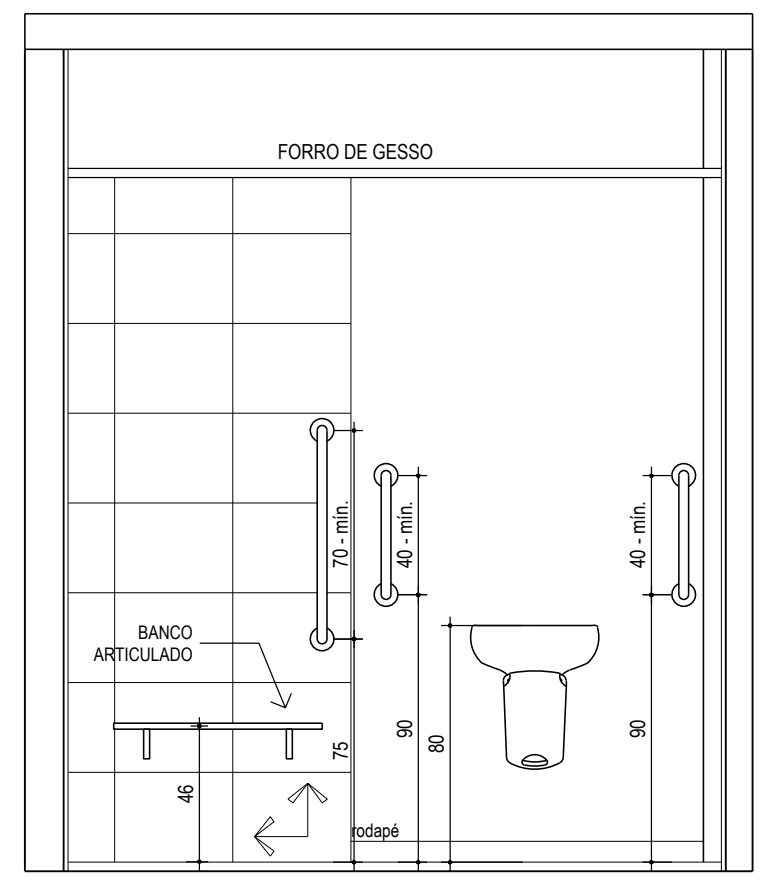

VISTA 01 - VEST. FUNC. FEM.
4º PAVIMENTO

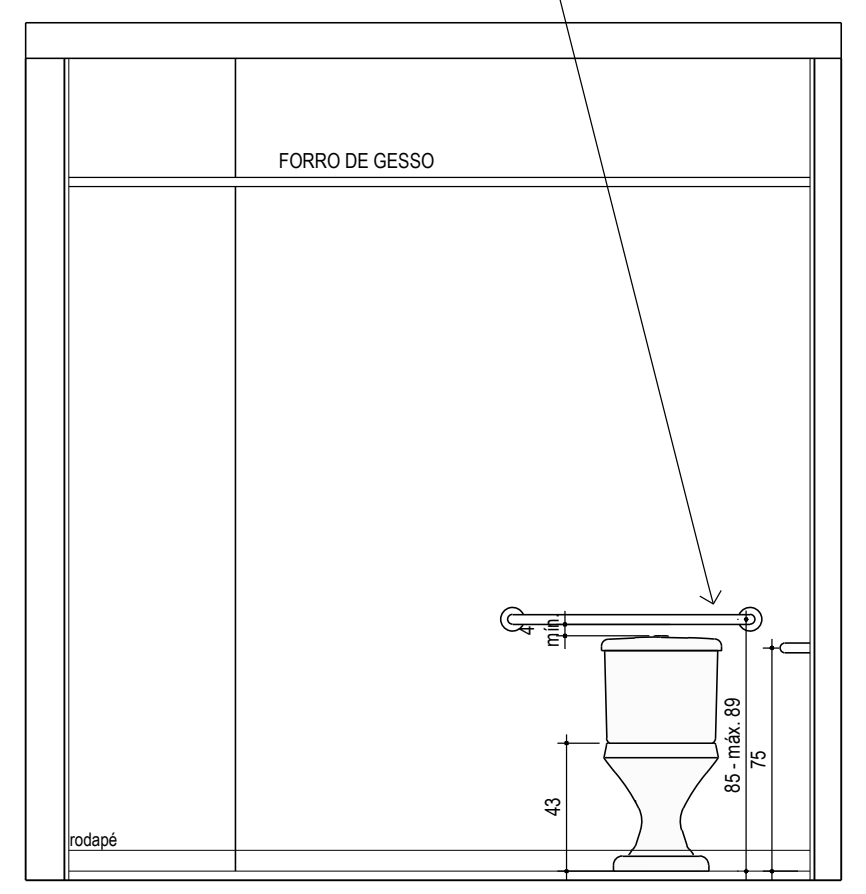

VISTA 02 - VEST. FUNC. FEM.
4º PAVIMENTO

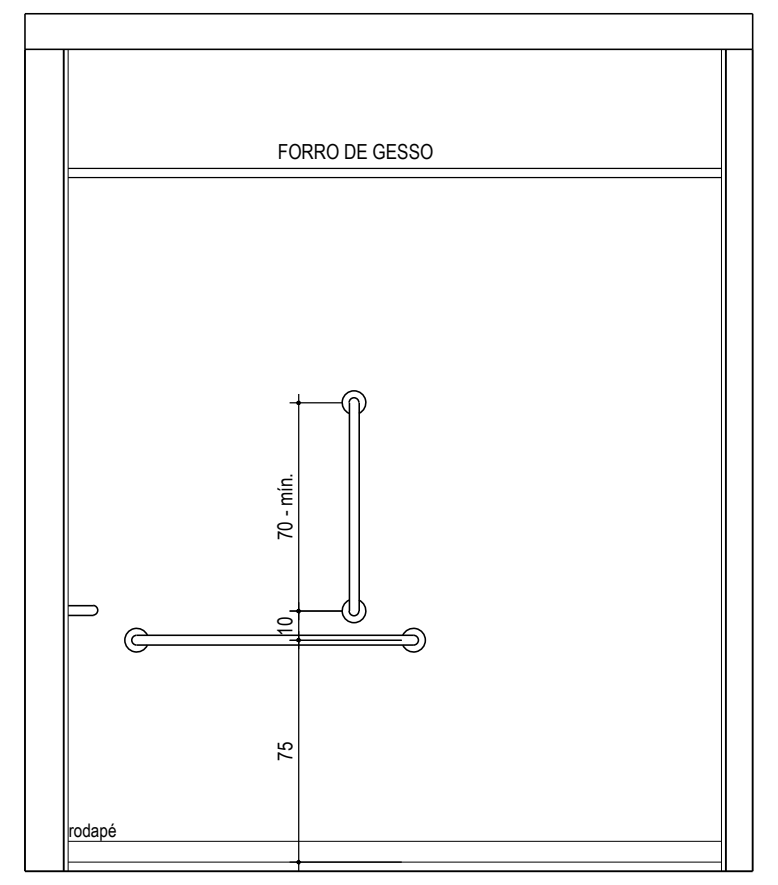

VISTA 03 - VEST. FUNC. FEM.
4º PAVIMENTO

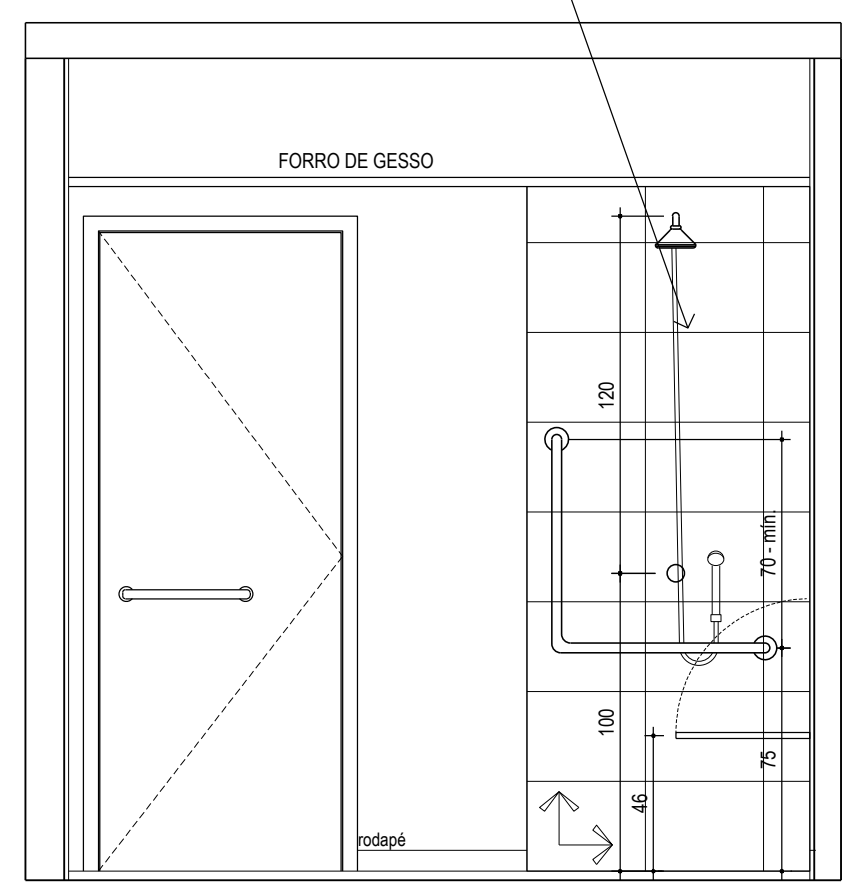

VISTA 04 - VEST. FUNC. FEM.
4º PAVIMENTO

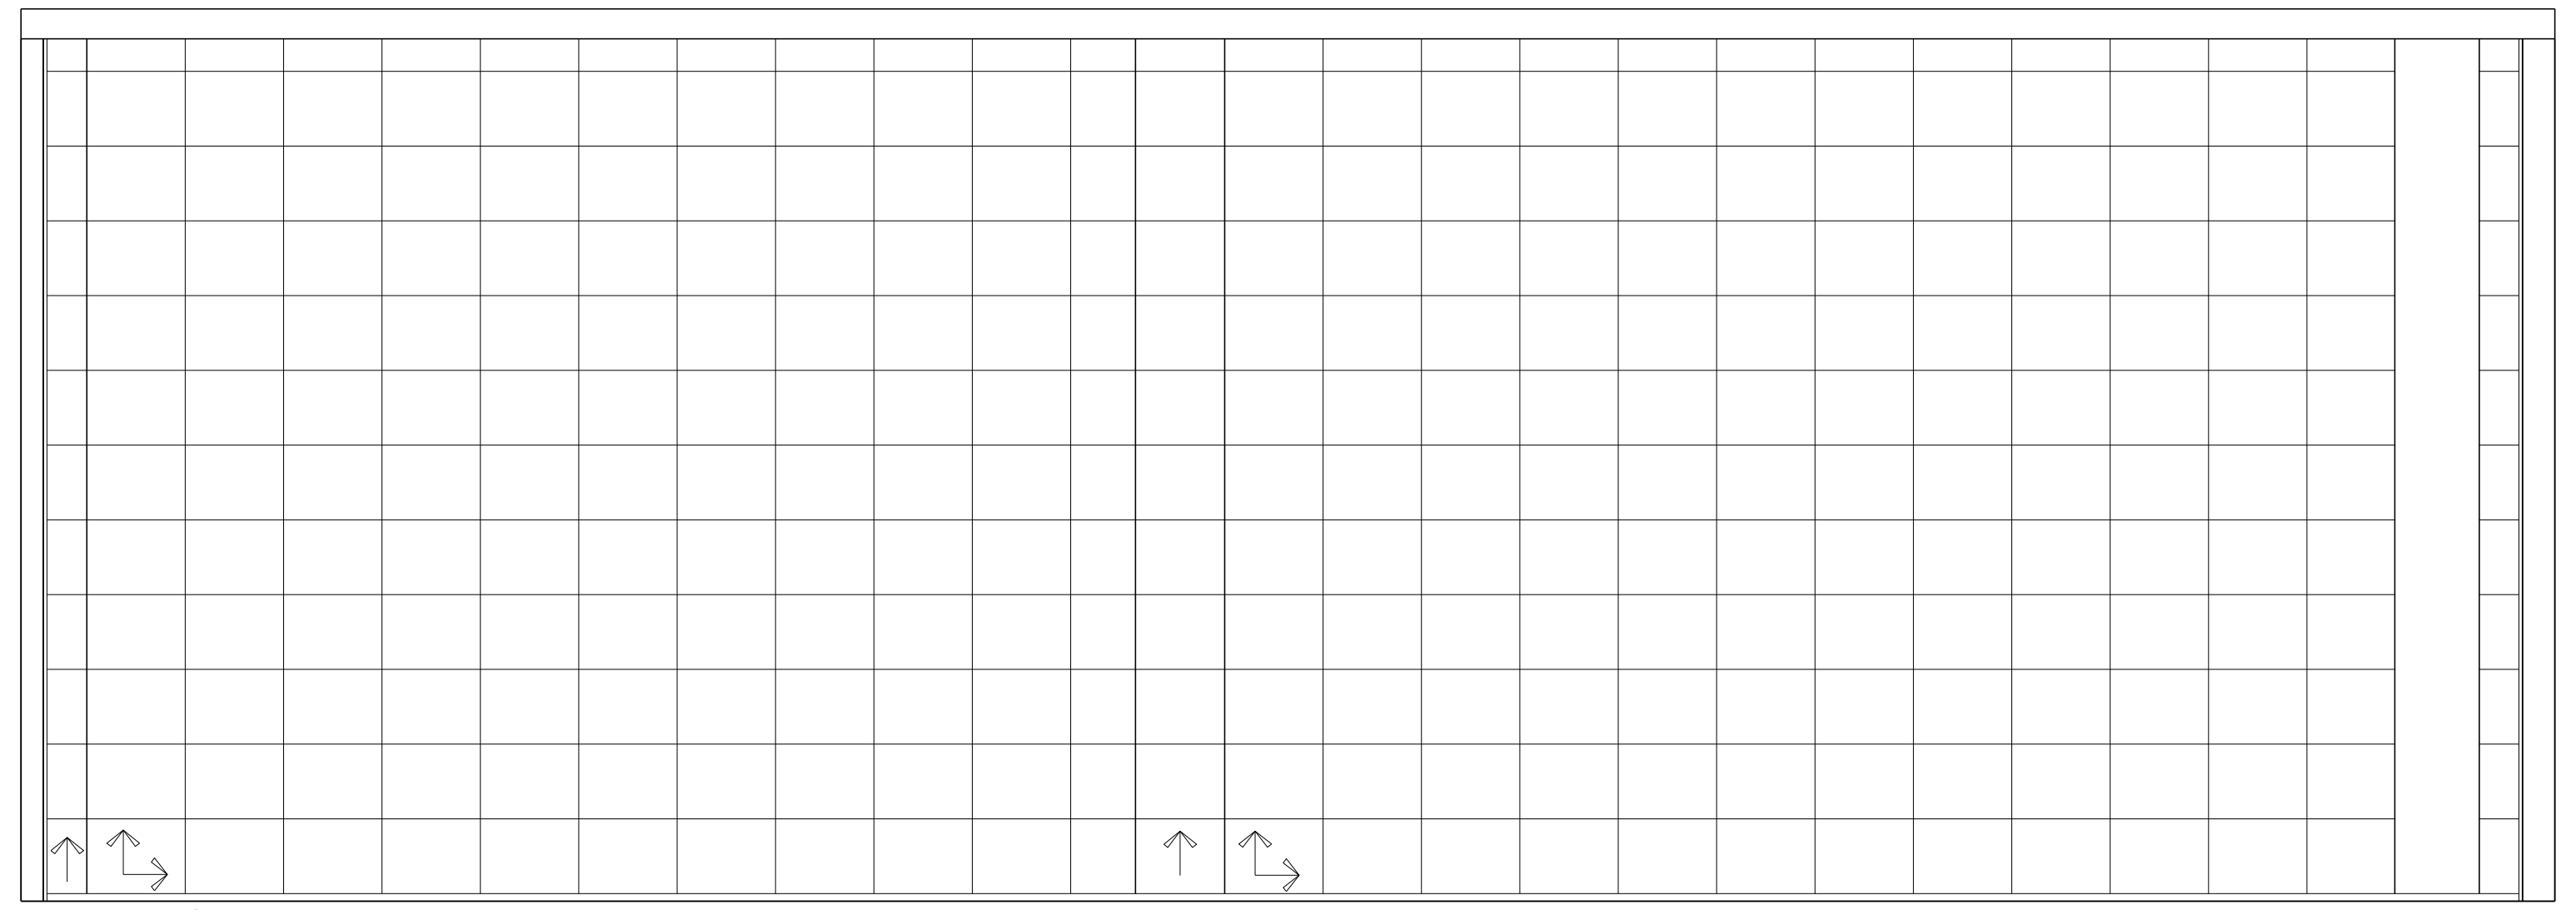

VISTA 03 - DEPÓSITO DE LIXO
1º PAVIMENTO

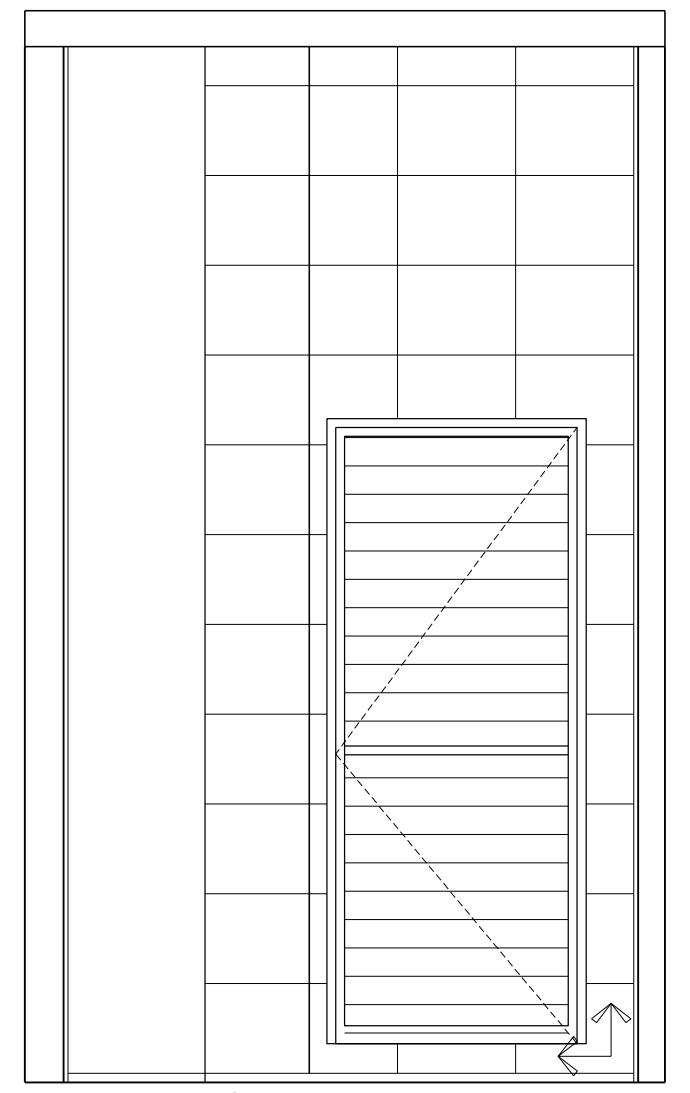

VISTA 04 - DEPÓSITO DE LIXO
1º PAVIMENTO

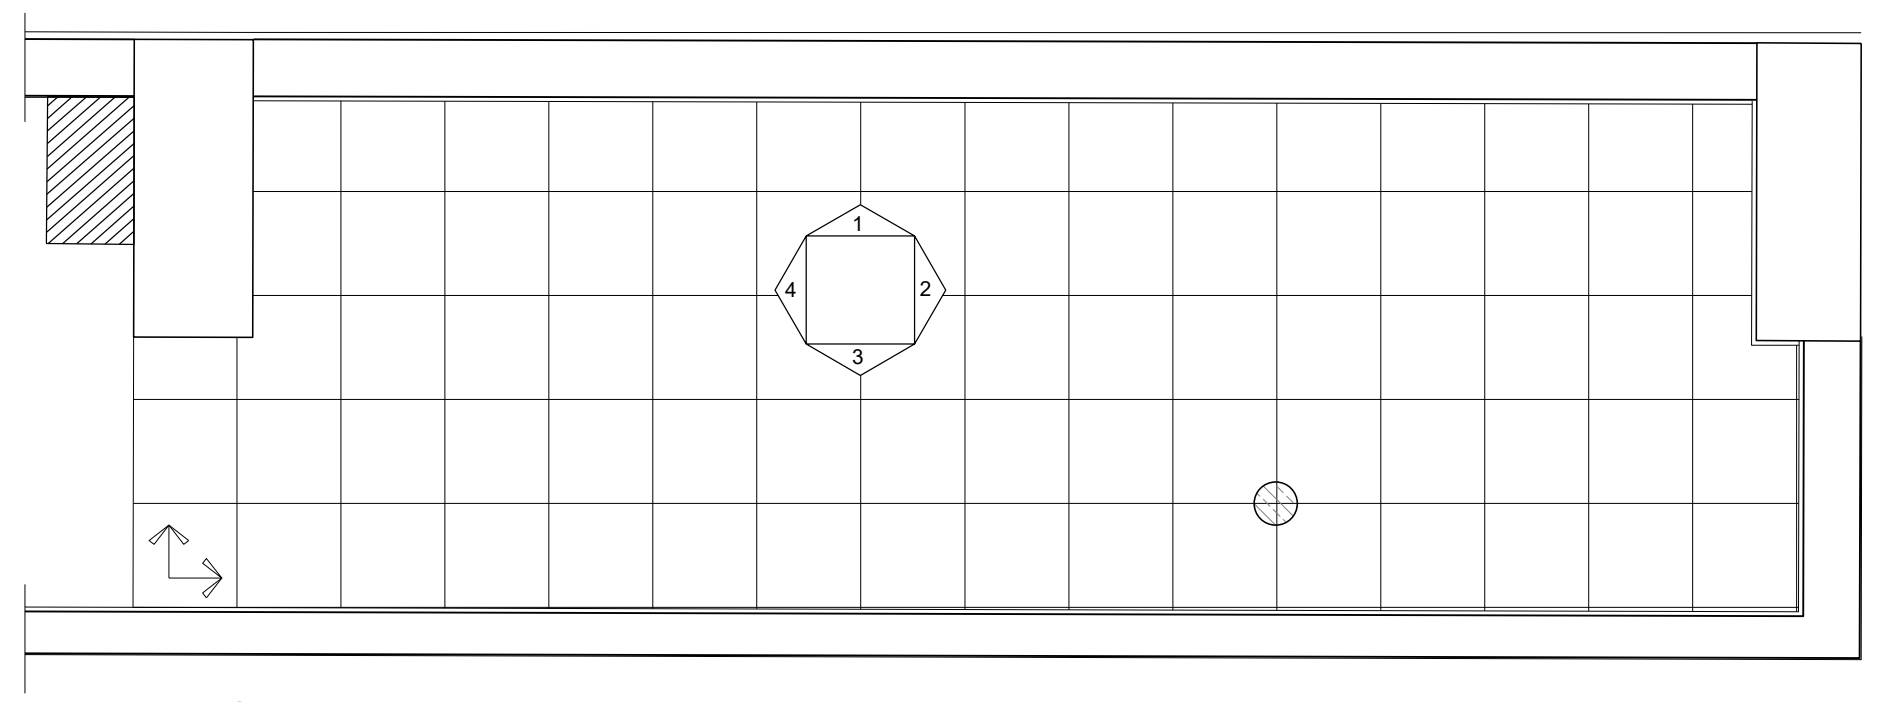

PLANTA DEPÓSITO DE LIXO
1º PAVIMENTO

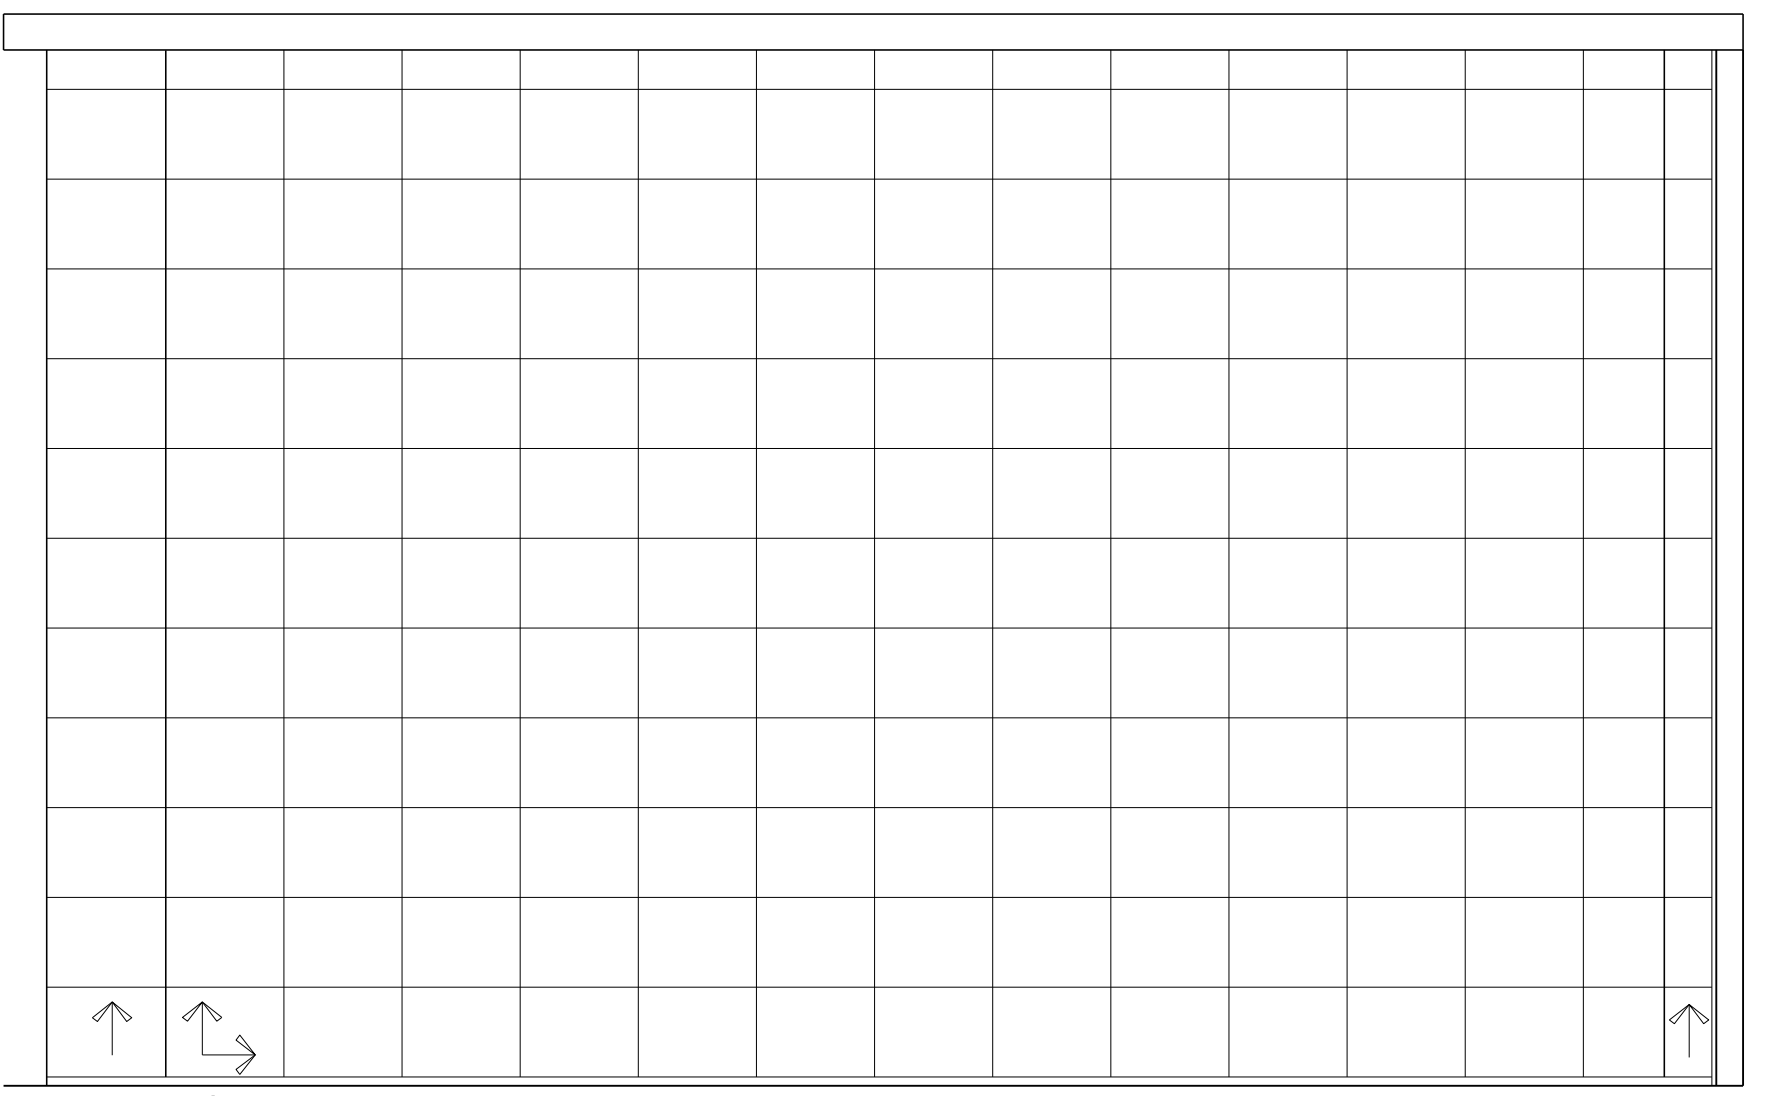

VISTA 01 - DEPÓSITO DE LIXO
1º PAVIMENTO

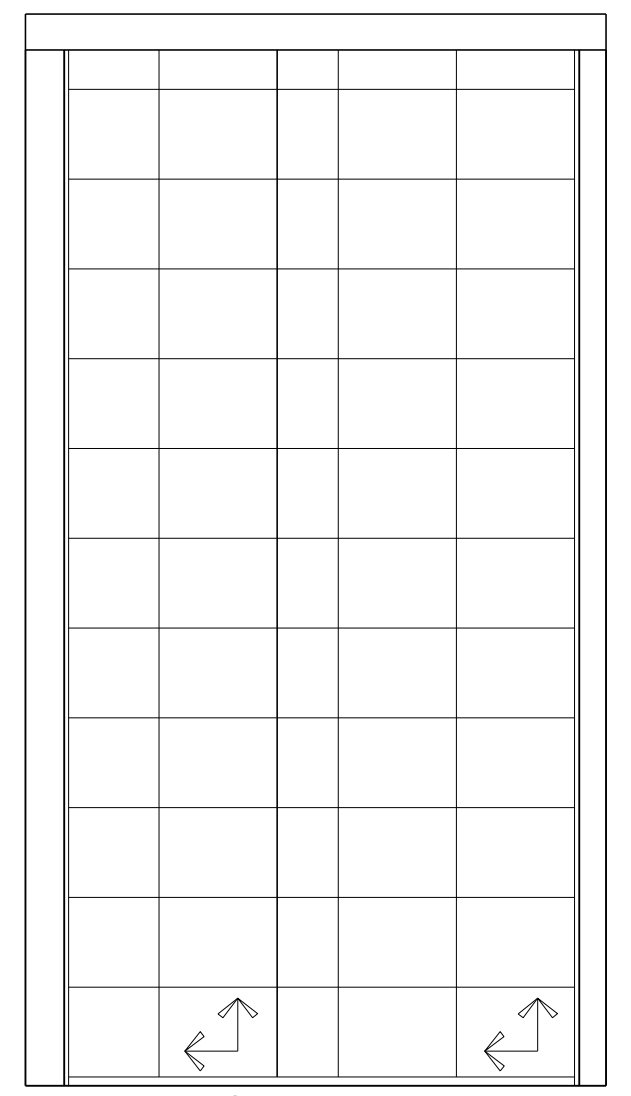

VISTA 02 - DEPÓSITO DE LIXO
1º PAVIMENTO

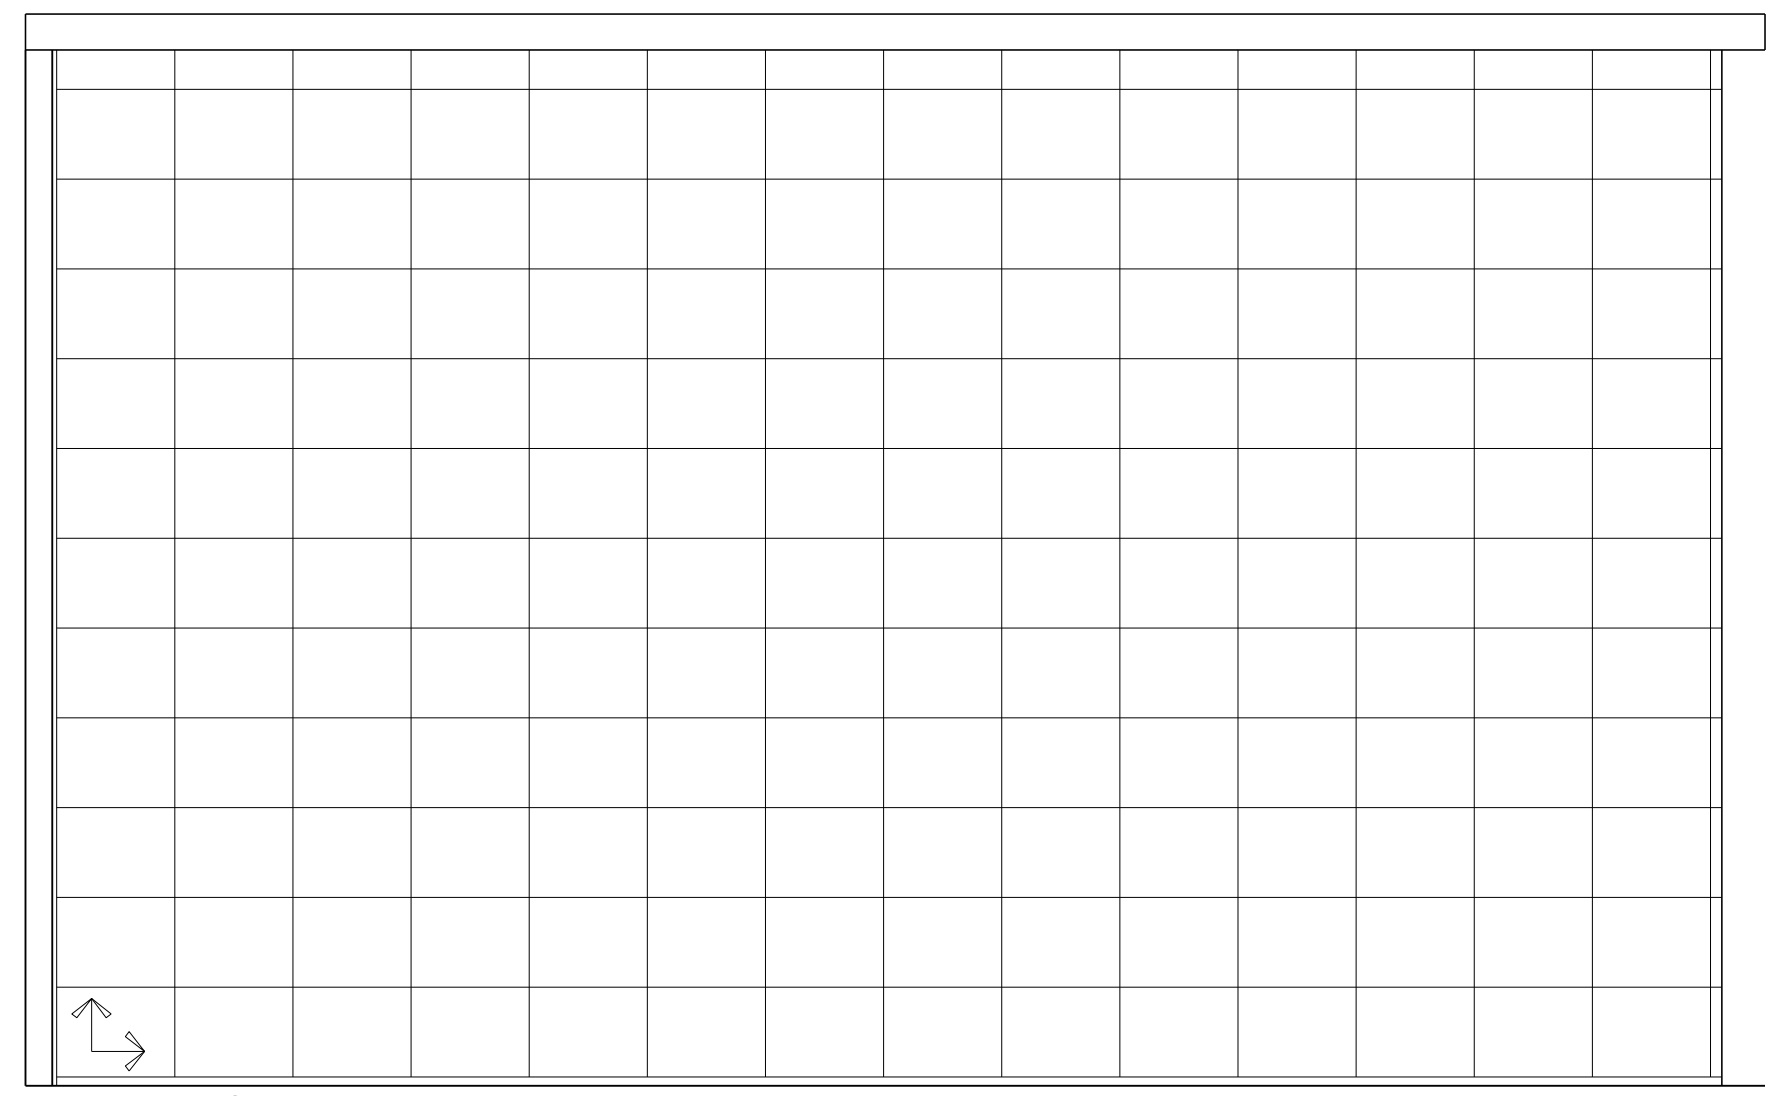

VISTA 03 - DEPÓSITO DE LIXO
1º PAVIMENTO

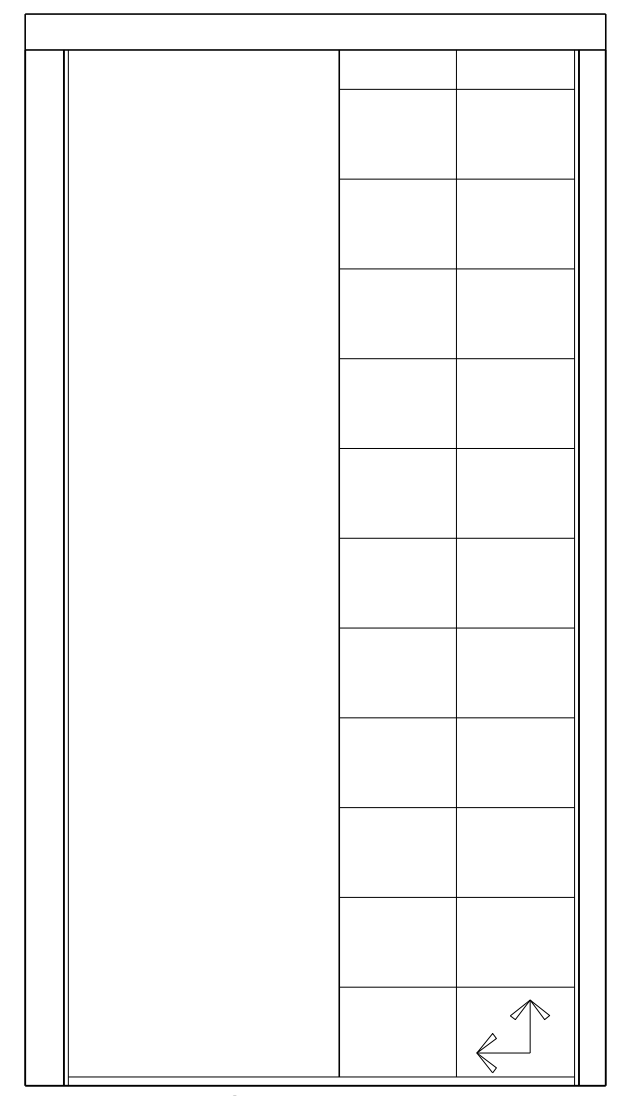

VISTA 04 - DEPÓSITO DE LIXO
1º PAVIMENTO

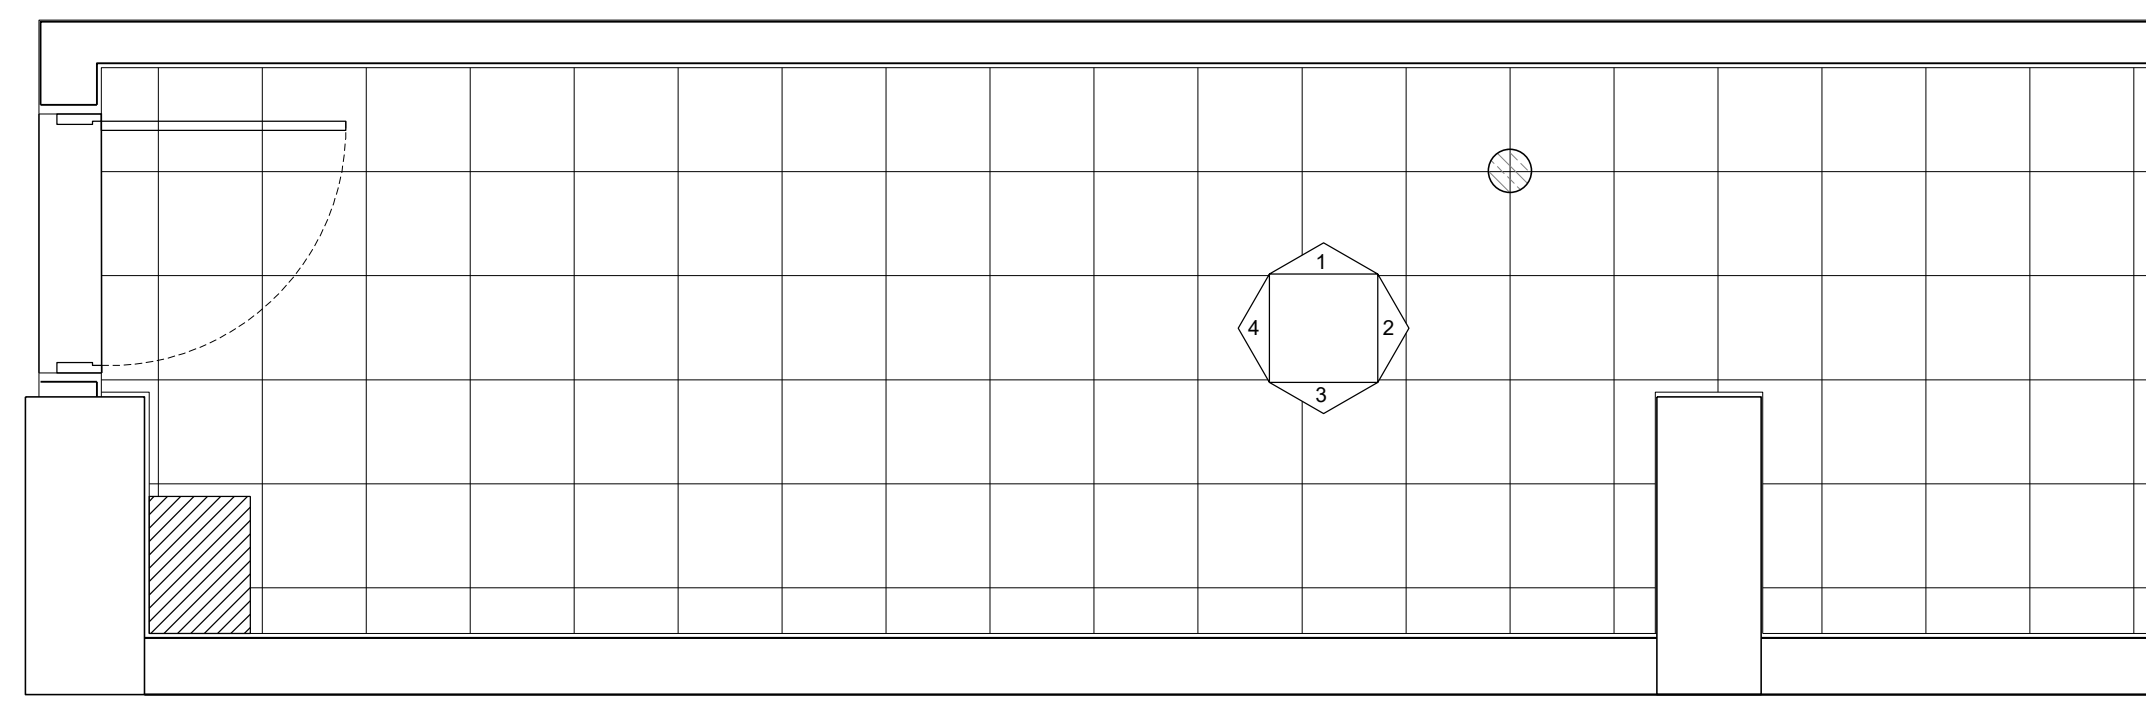

PLANTA DEPÓSITO DE LIXO
1º PAVIMENTO

PLANTAS DE REFERÊNCIA PARA BASE DE PROJETO

REVISÃO	DATA	DESCRIÇÃO	RESP.
00	01/03/2023	EMISSÃO INICIAL	

INCORPORAÇÃO
JERONIMO DA VEIGA
Empreendimentos e Participações Ltda.

CONSTRUÇÃO

PROJETISTA
ADESA ARQUITETURA
RUA PADRE GARCIA VELHO, 73 - CJ. 41
CEP: 05421- 030
FONE: 3032 4355 / 3032 4362

DISCIPLINA
ARQUITETURA

CÓDIGO/OBRA
DUO

FASE
LIBERADO OBRA

EMPREENDIMENTO
DUO
AV_LUZ

ASSUNTO
DETALHAMENTO
ÁREAS_MOLHADAS_PUC_E_INFERIORES

FOLHA N.º
ARQ
128

RESPONSÁVEL: ADELINO SANTOS
SUPERVISOR: ADELINO SANTOS
COORDENADOR: ALISSA LOPES
REVISÃO: R00
PROJETISTA
ARQUIVO: DUO-ARQ-LO-128-DET-AMO-R00.dwg
ESCALA: 1:25
DATA: 01/03/2023

DIREITOS AUTORAIS RESERVADO A REPRODUÇÃO TOTAL OU PARCIAL SEM PRÉVIA AUTORIZAÇÃO, CONFORME RESOLUÇÃO N° 67, DE 5 DE DEZEMBRO DE 2013